Согласовано

Топограф	Бахтигузин	
Топограф	Абдуллаев	
Гидролог	Бахадиров	
Геолог	Усмонов	
Геолог	Жонузоков	
Испол.	Насруллозода	

Взам. инв.№

Подп. и дата

Инв. № подл.

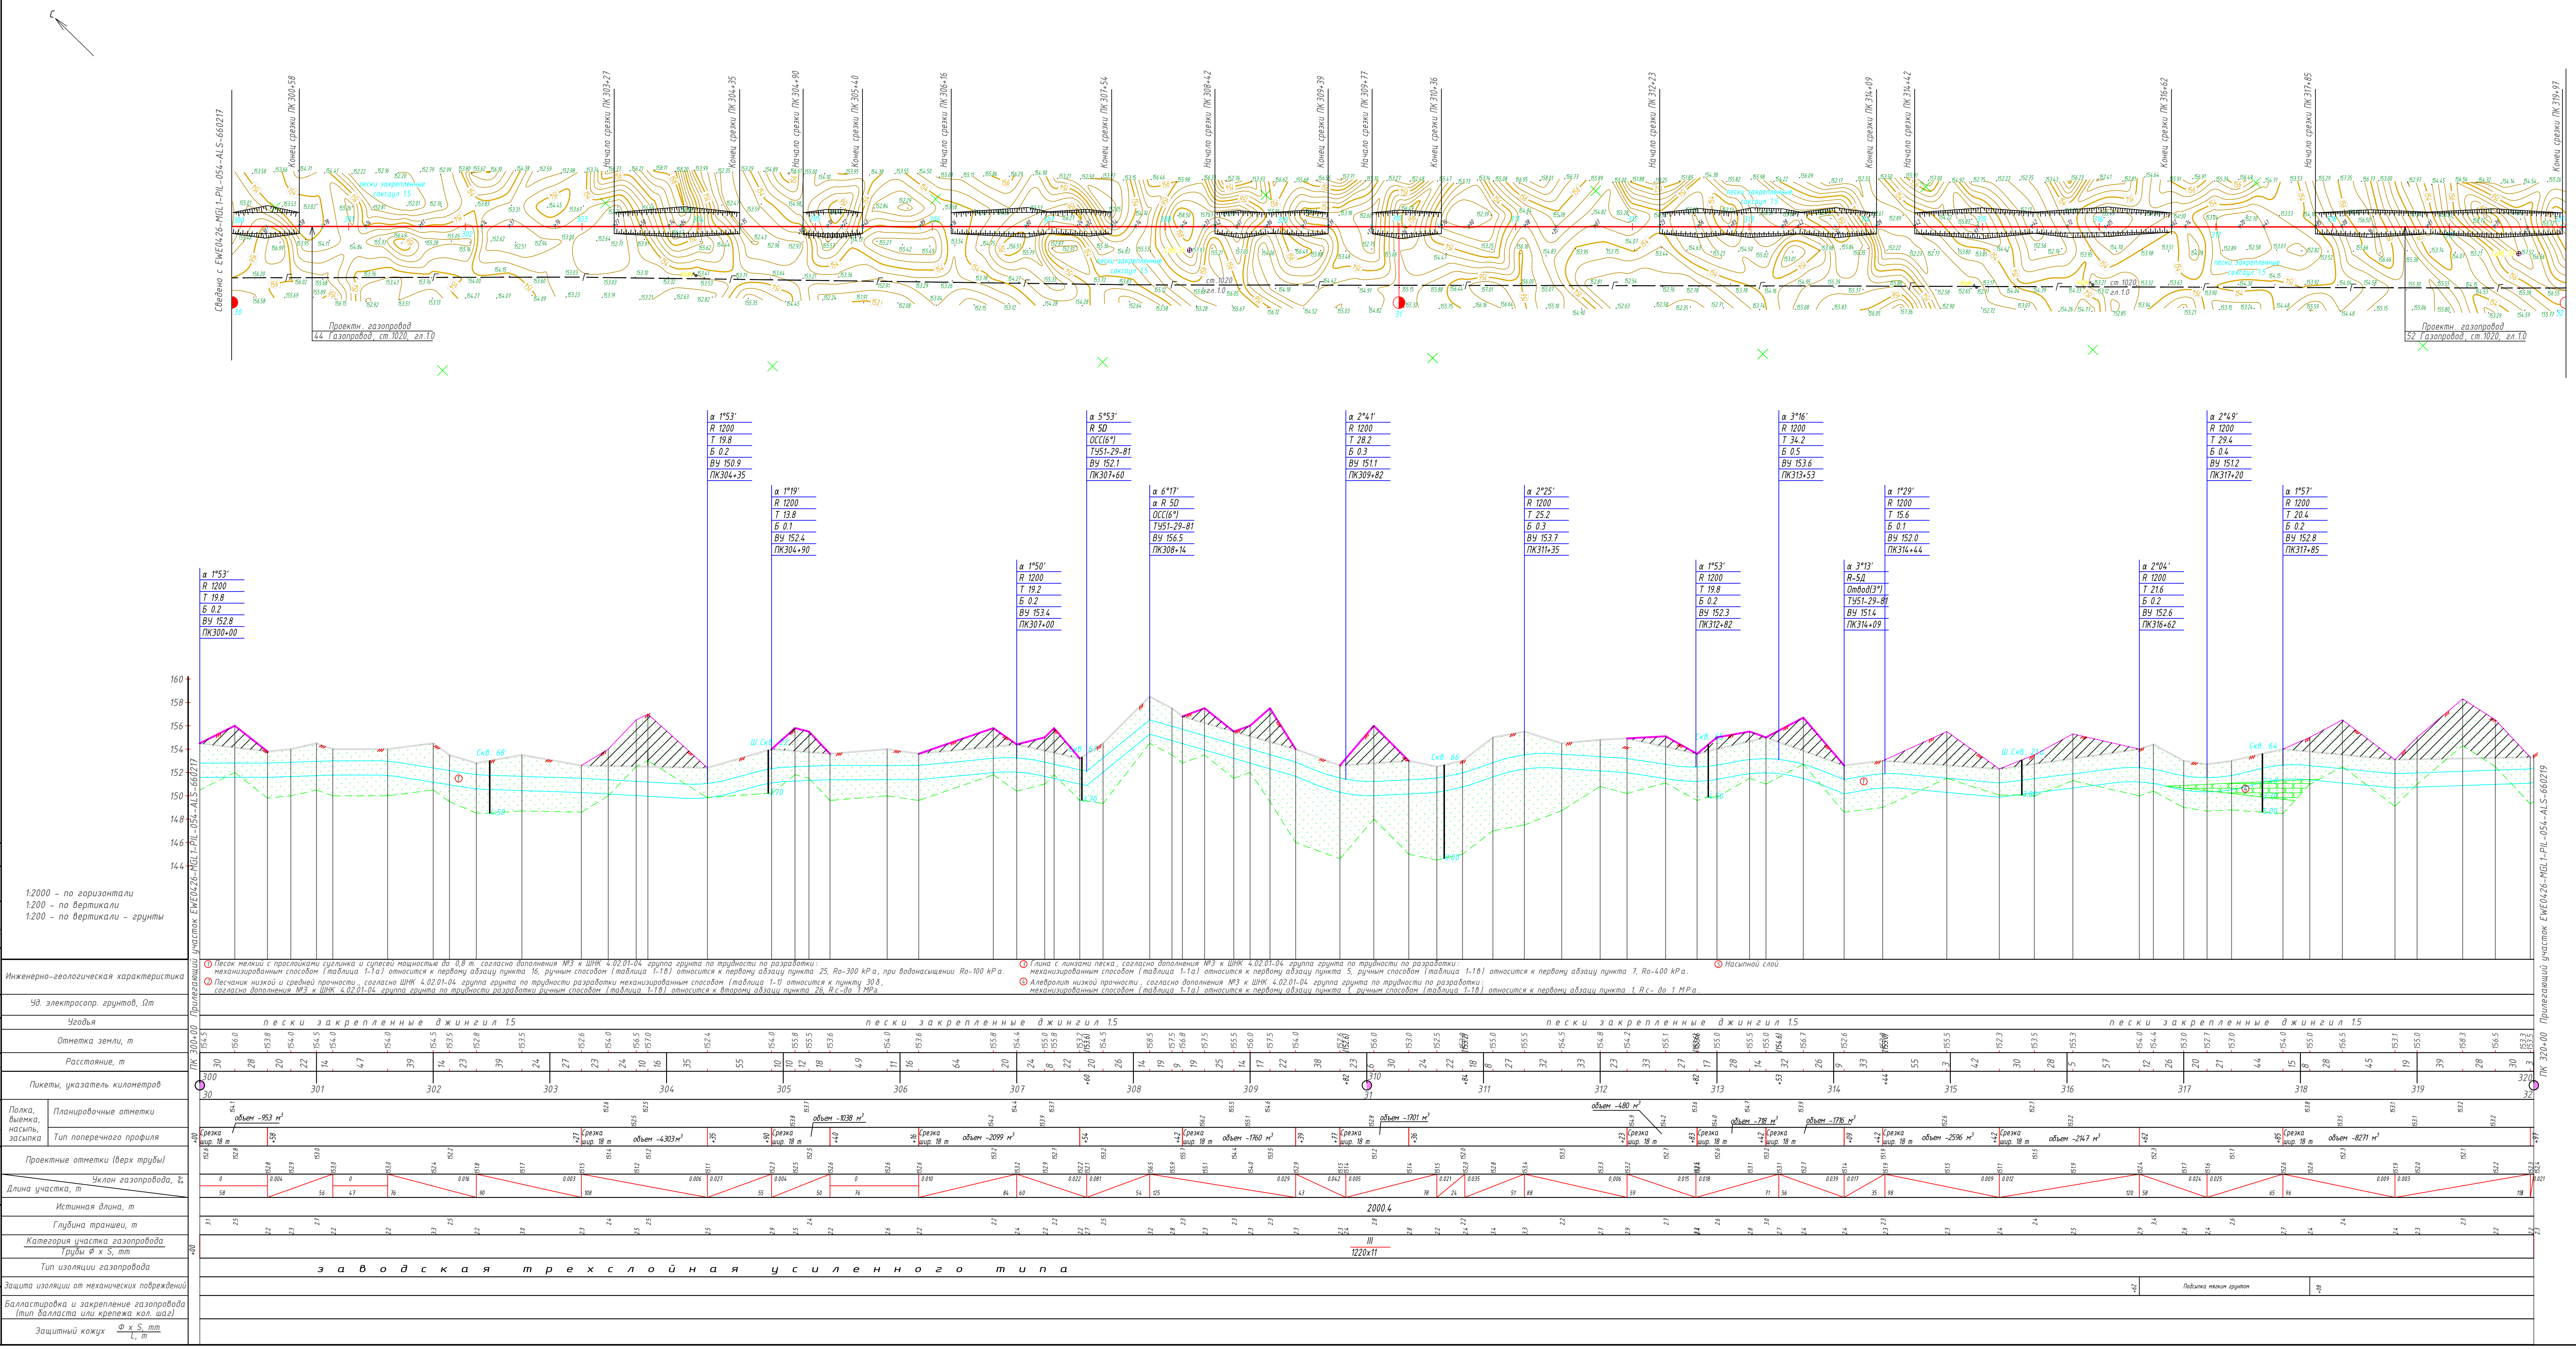

Сведено с EWE0426-MGL1-PIL-054-ALS-660217
Сведено с EWE0426-MGL1-PIL-054-ALS-660219
Конец срезки ПК 300+58
Начало срезки ПК 303+27
Конец срезки ПК 304+35
Начало срезки ПК 304+90
Конец срезки ПК 305+40
пески закрепленные саксаул 1.5
Проектн. газопровод
44 Газопровод, ст.1020, гл.1.0
Проектн. газопровод
52 Газопровод, ст.1020, гл.1.0
α 1°53' R 1200 T 19.8 Б 0.2 ВУ 152.8 ПК300+00
α 1°53' R 1200 T 19.8 Б 0.2 ВУ 150.9 ПК304+35
α 1°19' R 1200 T 13.8 Б 0.1 ВУ 152.4 ПК304+90
α 1°50' R 1200 T 19.2 Б 0.2 ВУ 153.4 ПК307+00
α 5°53' R 5D ОСС(6°) ТУ51-29-81 ВУ 152.1 ПК307+60
α 6°17' α R 5D ОСС(6°) ТУ51-29-81 ВУ 156.5 ПК308+14
1:2000 - по горизонтали
1:200 - по вертикали
1:200 - по вертикали - грунты
ПК 300+00 Прилегающий участок EWE0426-MGL1-PIL-054-ALS-660217
ПК 320+00 Прилегающий участок EWE0426-MGL1-PIL-054-ALS-660219
Инженерно-геологическая характеристика
Уд. электросопр. грунтов, Ωт
Угодья
Отметка земли, т
Расстояние, т
Пикеты, указатель километров
Полка, выемка, насыпь, засыпка
Планировочные отметки
Тип поперечного профиля
Проектные отметки (верх трубы)
Уклон газопровода, ‰
Длина участка, т
Истинная длина, т
Глубина траншеи, т
Категория участка газопровода
Трубы Φ x S, тт
Тип изоляции газопровода
Защита изоляции от механических повреждений
Балластировка и закрепление газопровода (тип балласта или крепежа кол. шаг)
Защитный кожух Φ x S, тт / L, т
① Песок мелкий с прослойками суглинка и супесей мощностью до 0,8 т. согласно дополнения №3 к ШНК 4.02.01-04 группа грунта по трудности по разработки: механизированным способом (таблица 1-1а) относится к первому абзацу пункта 16, ручным способом (таблица 1-1в) относится к первому абзацу пункта 25, Ro-300 кPа, при водонасыщении Ro-100 кPа.
② Песчаник низкой и средней прочности., согласно ШНК 4.02.01-04 группа грунта по трудности разработки механизированным способом (таблица 1-1) относится к пункту 30 б, согласно дополнения №3 к ШНК 4.02.01-04 группа грунта по трудности разработки ручным способом (таблица 1-1в) относится к второму абзацу пункта 26, Rс-до 1 MPa.
③ Глина с линзами песка, согласно дополнения №3 к ШНК 4.02.01-04 группа грунта по трудности по разработки: механизированным способом (таблица 1-1а) относится к первому абзацу пункта 5, ручным способом (таблица 1-1в) относится к первому абзацу пункта 7, Ro-400 кPа.
④ Алевролит низкой прочности. согласно дополнения №3 к ШНК 4.02.01-04 группа грунта по трудности по разработки: механизированным способом (таблица 1-1а) относится к первому абзацу пункта 1, ручным способом (таблица 1-1в) относится к первому абзацу пункта 1, Rс- до 1 MPa.
⑤ Насыпной слой
пески закрепленные джингил 1.5
Срезка шир. 18 т
объем -953 м³
объем -4303 м³
объем -1038 м³
объем -2099 м³
объем -1760 м³
объем -1701 м³
объем -718 м³
объем -1716 м³
объем -2596 м³
объем -2147 м³
объем -8271 м³
2000.4
III
1220x11
заводская трехслойная усиленного типа
Подсыпка мягким грунтом

Схема расположения листов

EWE0426-MGL1-PIL-054-ALS-660217	EWE0426-MGL1-PIL-054-ALS-660218	EWE0426-MGL1-PIL-054-ALS-660219

Экспликация деталей и отдельных изделий

№ п. п.	Наименование деталей	Ед изм.	Кол.	Примечание
1	ОСС3°-5Д-1220 (12К60)-5,5-075-У ТУ51-29-81	шт	1	
1	ОСС6°-5Д-1220 (12К60)-5,5-075-У ТУ51-29-81	шт	2	

1 Общие данные - чертеж EWE0426-MGL1-PIL-054-COM-660201
2 Ситуационный план см. EWE0426-MGL1-PIL-054-DRW-660202
3 До начала работ руководитель строительной организации должен разработать и согласовать схему и инструкцию по безопасному производству работ в охранной зоне газопровода и его сооружений.
4 Производство работ на данном участке вести в строгом соответствии с "Инструкцией по производству строительных работ в охранных зонах магистральных трубопроводов Мингазпрома" ВСН 51-1-80.
5 Ширину полосы отвода земель для строительства газопровода см. типовой чертеж EWE0426-MGL1-PIL-000-DRW-810201.
6 Охранную зону магистрального газопровода см. типовой чертеж EWE0426-MGL1-PIL-000-DRW-810202.
7 Поперечный разрез траншеи см. типовой чертеж EWE0426-MGL1-PIL-000-DRW-810203.

Рев.	Дата	Назначение ревизии	Проверил	Утвердил
A2	17.08.2026	Выпущено для строительства		
A1	16.07.2026	Выпущено для строительства		
R2	02.07.2026	Выпущено для рассмотрения		
R1	05.06.2026	Выпущено для рассмотрения		

ЗАКАЗЧИК: UZTRANSGAZ
ГЕНЕРАЛЬНЫЙ ПОДРЯДЧИК: UZBEKENERGOTAMIR
ПОДРЯДЧИК: PBG Pro Build Generation
ГЕНЕРАЛЬНЫЙ ПРОЕКТИРОВЩИК: EAST WEST ENGINEERING

EWE0426-MGL1-PIL-054-ALS-660218-A2

«СТРОИТЕЛЬСТВО НОВЫХ НИТОК (УЧАСТКОВ) ГАЗОПРОВОДОВ «ГАЗЛИ - САРИМОЙ» И «АКЧАЛОК - ГАЗЛИ - НУКУС» ОБЩЕЙ ПРОТЯЖЕННОСТЬЮ НЕ МЕНЕЕ 275 КМ».

Изм.	Кол.уч.	Лист	№док.	Подпись	Дата
ГИП		Схабицкий А.			08.2026
Провер.		Шафиева О.			08.2026
Исполн.		Мухамадеева			08.2026
Н.контр		Схабицкий А.			08.2026

ГАЗОПРОВОД «ГАЗЛИ-САРИМОЙ» (54 КМ)

Стадия	Лист	Листов
РД	1	1

План и продольный профиль газопровода ПК 300+00- ПК 320+00

ООО "EAST-WEST Engineering"
г. Ташкент 2026г.