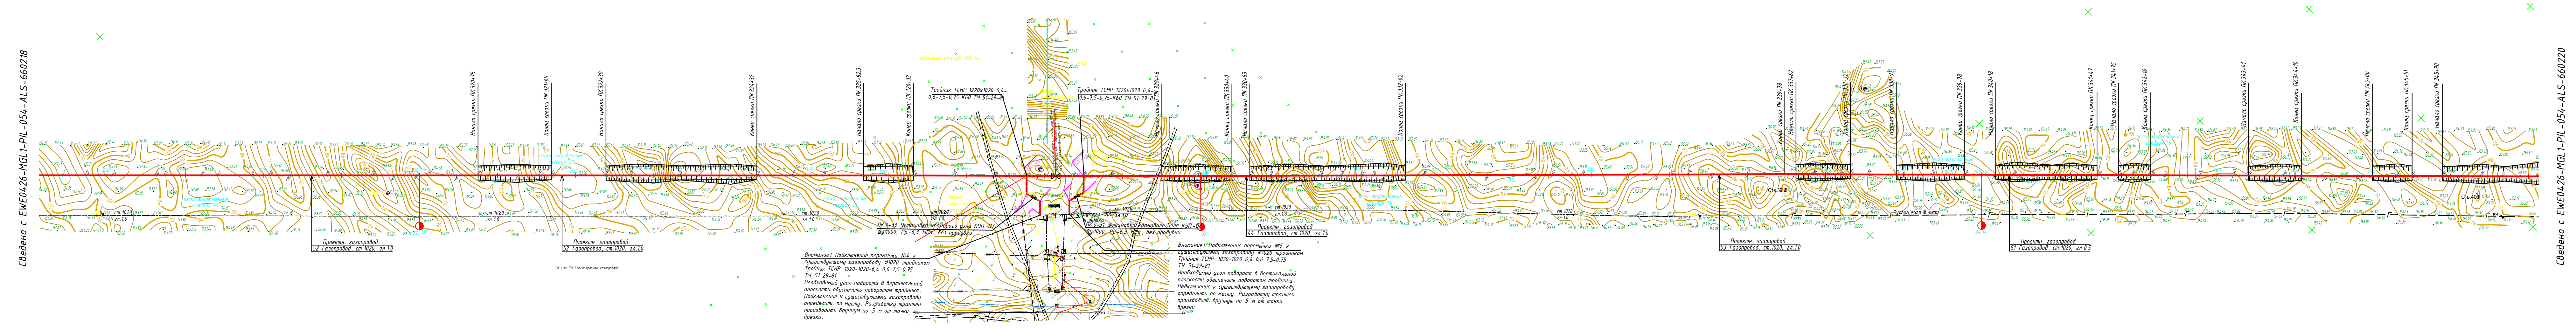

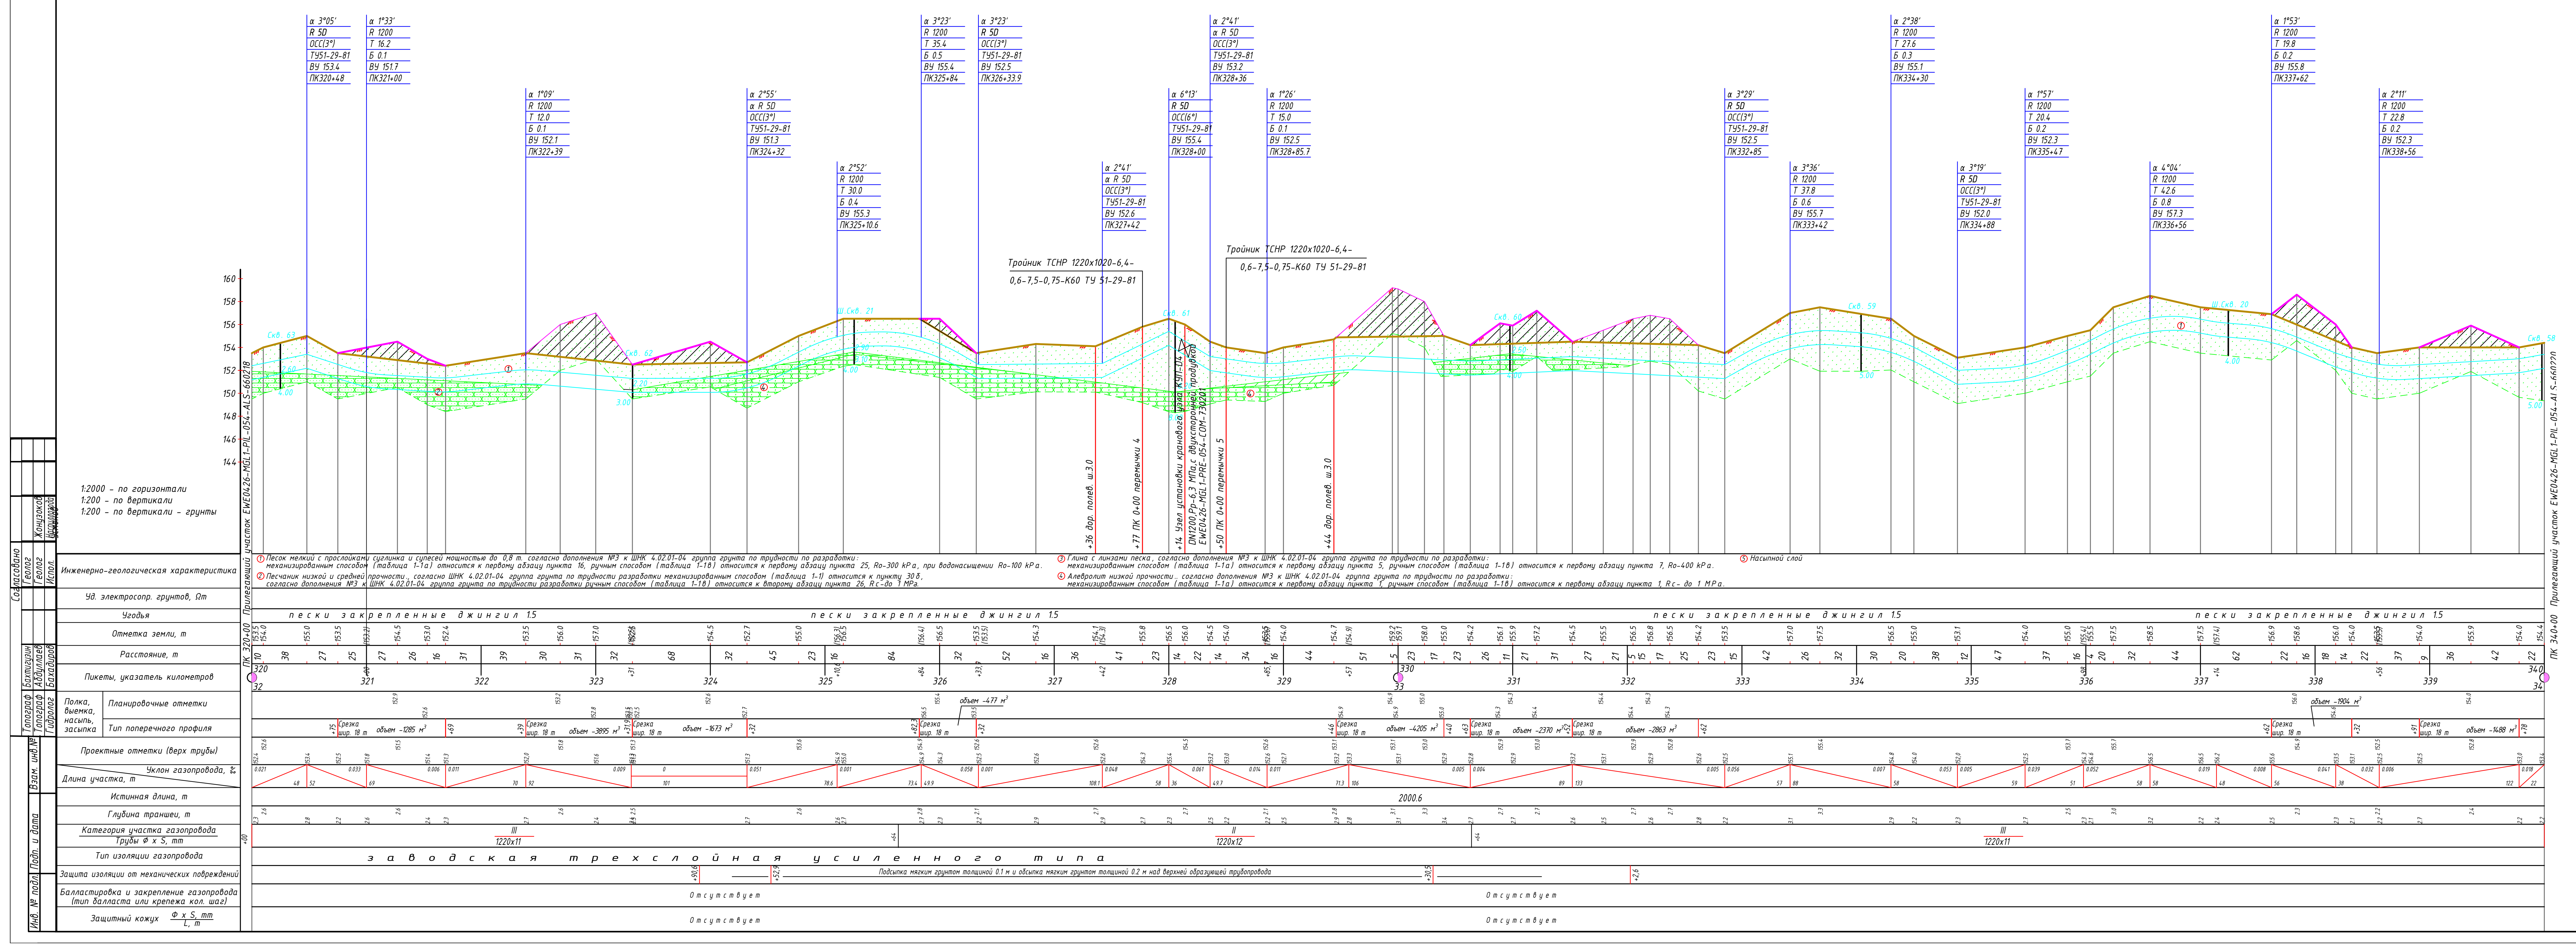
1:2000 – по горизонтали
1:200 – по вертикали
1:200 – по вертикали – грунты
Прилегающий участок EWE0426-MGL1-PIL-054-ALS
ПК 320+00
Инженерно-геологическая характеристика
Уд. электросопр. грунтов, Ωm
Угодья
Отметка земли, m
Расстояние, m
Пикеты, указатель километров
Полка, выемка, насыпь, засыпка
Планировочные отметки
Тип поперечного профиля
Проектные отметки (верх трубы)
Уклон газопровода, ‰
Длина участка, m
Истинная длина, m
Глубина траншеи, m
Категория участка газопровода
Трубы Φ x S, mm
Тип изоляции газопровода
Защита изоляции от механических повреждений
Балластировка и закрепление газопровода (тип балласта или крепежа кол. шаг)
Защитный кожух Φ x S, mm / L, m
пески закрепленные
заводская трехслойная усиленного типа
Согласовано
Геолог
Геолог
Испол.
Жонузоков
Топограф
Топограф
Гидролог
Бахтигузин
Абдуллаев
Бахадиров
Взам. инв.№
Подп. и дата
Инв. № подл.

Схема расположения листов

EWE0426-MGL1-PIL-054-ALS-660218	EWE0426-MGL1-PIL-054-ALS-660219	EWE0426-MGL1-PIL-054-ALS-660220

Ведомость углов поворотов перемычки №4 в горизонтальной плоскости

№№ углов и створов	Величина левого угла	Длина линии, m	Элементы кривых						
			Радиус R, m	Угол α°	Тангенс T₁, m	Тангенс T₂, m	Кривая K, m	Биссектриса Б, m	
0+00		23							
ВУ 1	120°00′	20	5Д	60°00′	(ОСС30°x2°)-5Д-1020 (10К60)-5,5-075-У ТУ51-29-81				
ВУ 2	239°00′	17	5Д	59°00′	(ОСС30°x2)-5Д-1020 (10К60)-5,5-075-У ТУ51-29-81				
0+99		L-60							

Ведомость углов поворотов перемычки №5 в горизонтальной плоскости

№№ углов и створов	Величина левого угла	Длина линии, m	Элементы кривых						
			Радиус R, m	Угол α°	Тангенс T₁, m	Тангенс T₂, m	Кривая K, m	Биссектриса Б, m	
0+00		21							
ВУ 1	240°00′	20	5Д	60°00′	(ОСС30°x2°)-5Д-1020 (10К60)-5,5-075-У ТУ51-29-81				
ВУ 2	120°00′	19	5Д	60°00′	(ОСС30°x2)-5Д-1020 (10К60)-5,5-075-У ТУ51-29-81				
0+99		L-60							

Продольный профиль перемычки №4

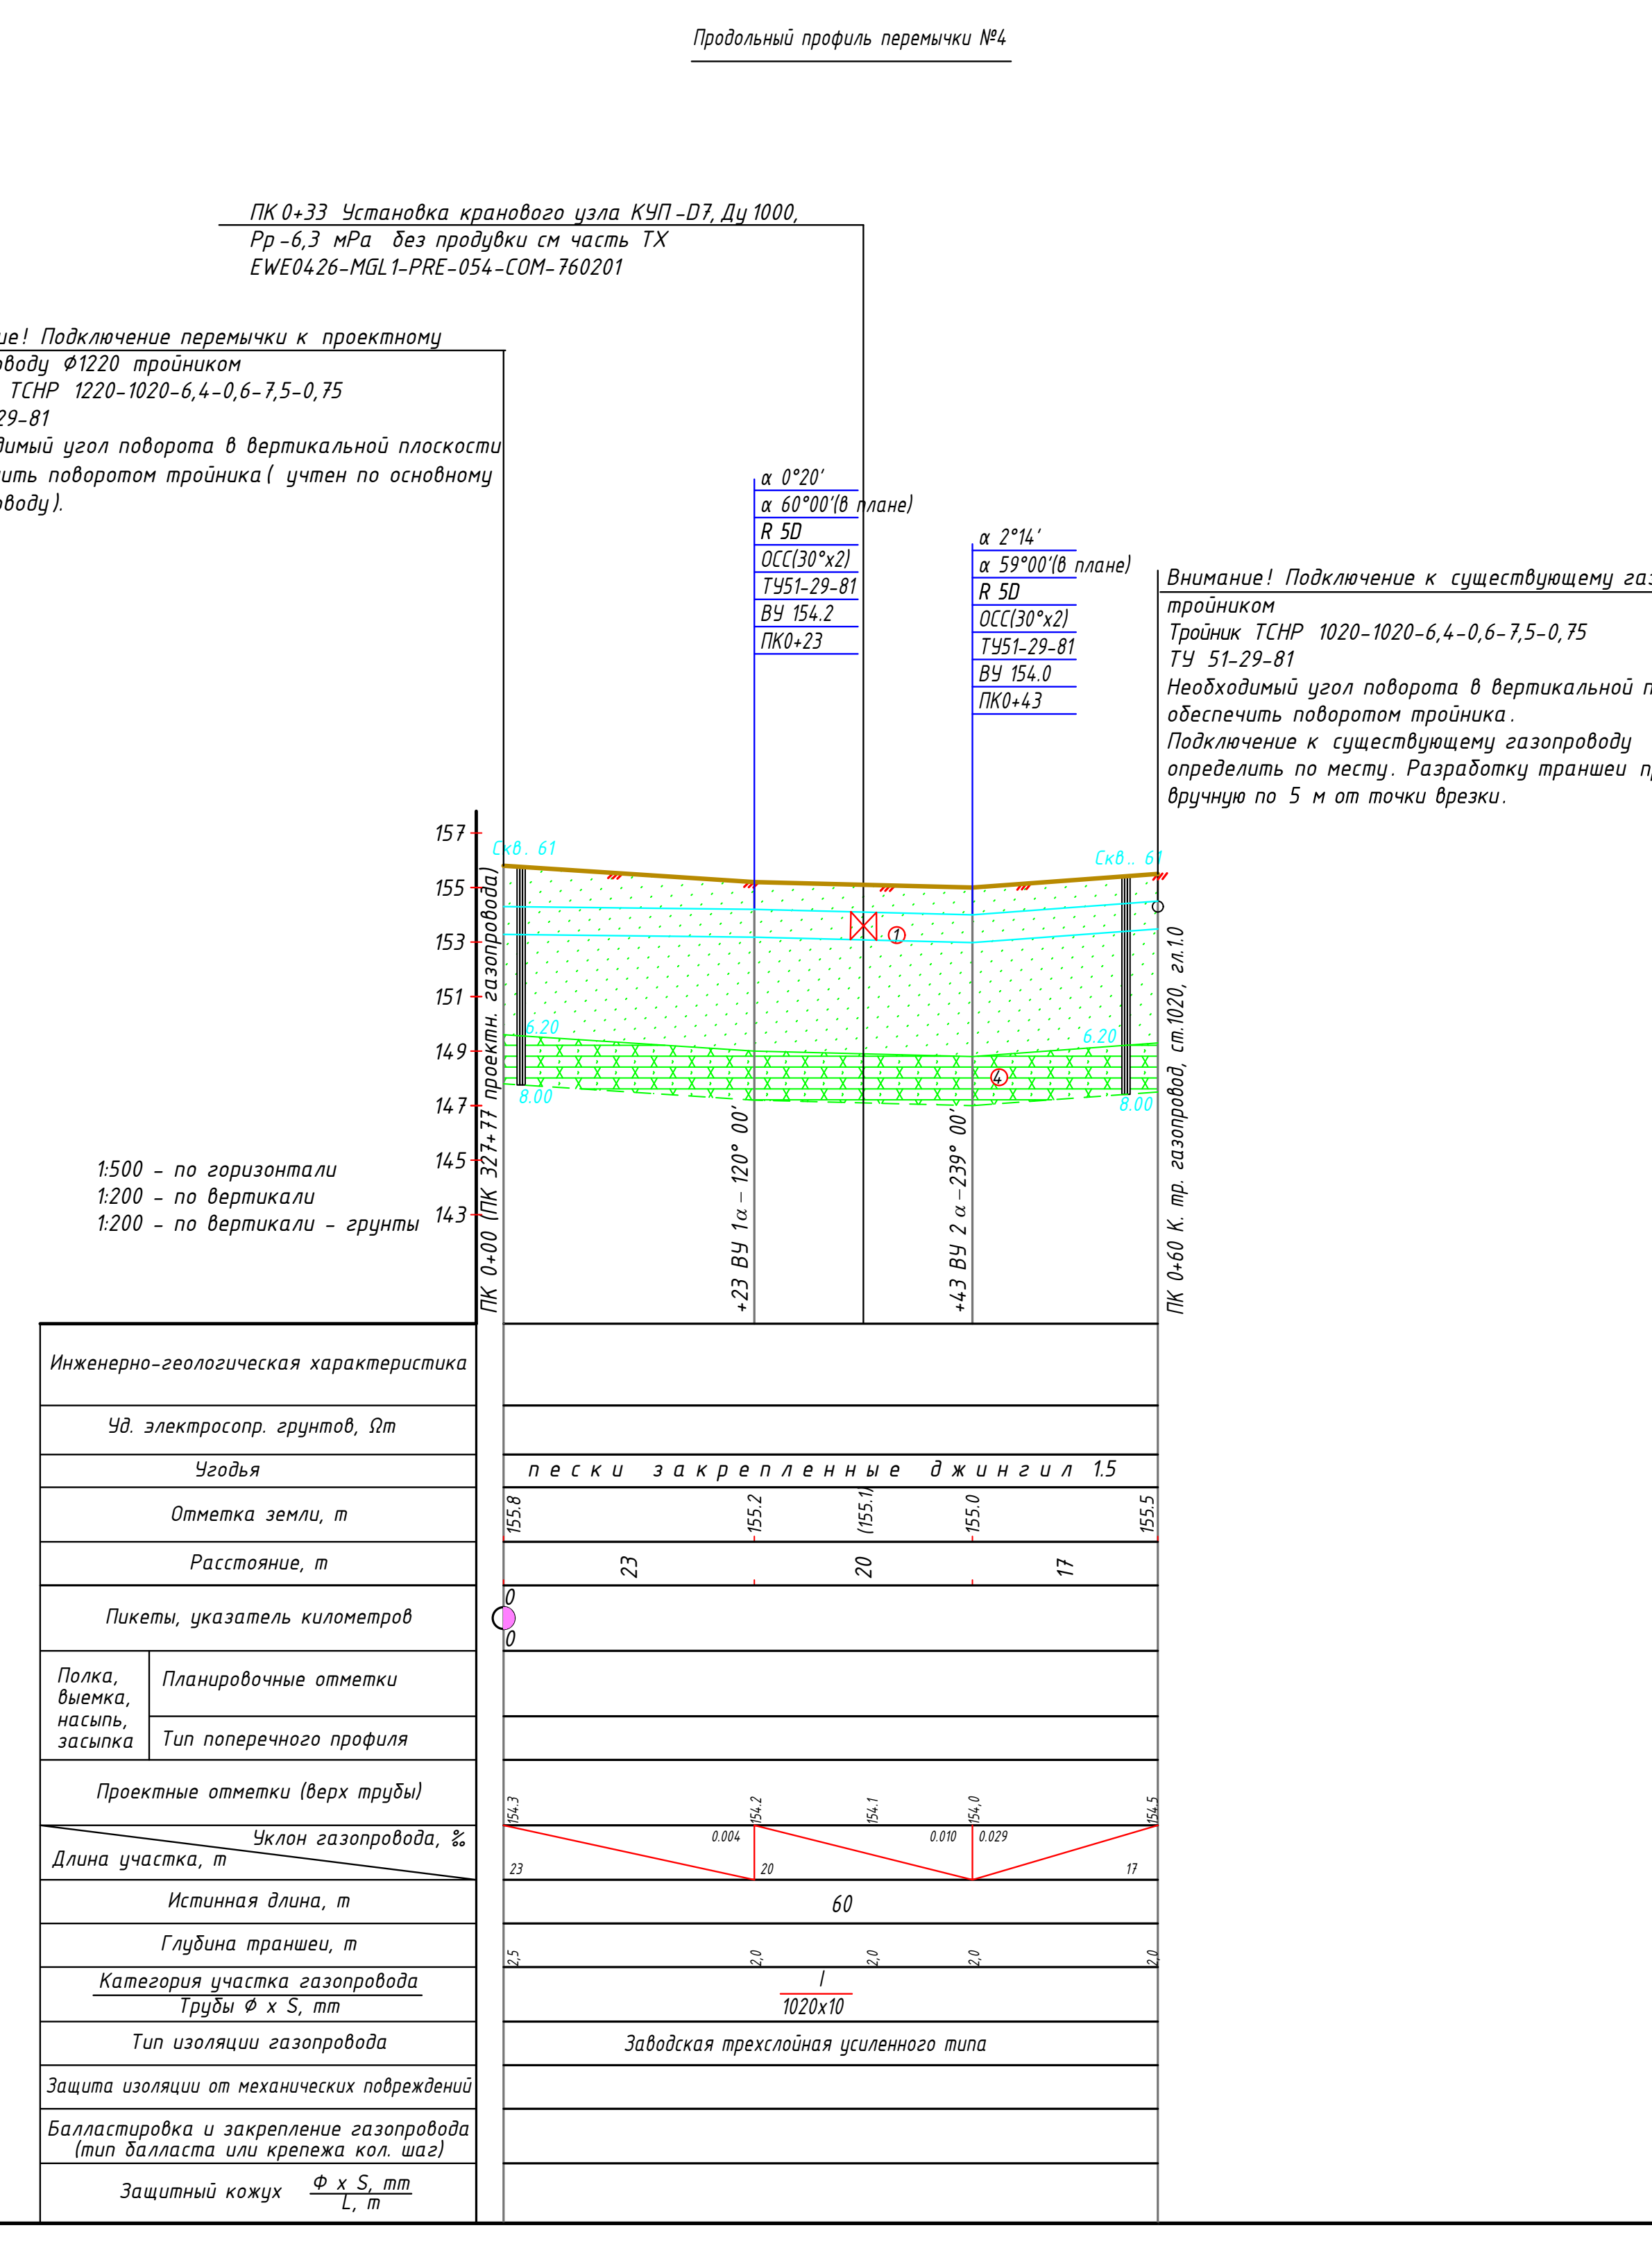
1:500 – по горизонтали
1:200 – по вертикали
1:200 – по вертикали – грунты
ПК 0+00 (ПК 327+77 проектн. газ
+23 ВУ 1α – 120° 00′
α 0°20′
α 60°00′(в плане)
R 5D
ОСС(30°x2)
ТУ51-29-81
ВУ 154.2
ПК0+23
α 2°14′
α 59°00′(в плане)
R 5D
ОСС(30°x2)
ТУ51-29-81
ВУ 154.0
ПК0+43
Скв.. 61
Заводская трехслойная усиленного типа

ПК 0+33 Установка кранового узла КУП-D7, Ду 1000,
Рр -6,3 мРа без продувки см часть ТХ
EWE0426-MGL1-PRE-054-COM-760201

Внимание! Подключение перемычки к проектному газопроводу Ø1220 тройником
Тройник ТСНР 1220-1020-6,4-0,6-7,5-0,75
ТУ 51-29-81
Необходимый угол поворота в вертикальной плоскости обеспечить поворотом тройника (учтен по основному газопроводу).

Внимание! Подключение к существующему газопроводу Ø1020 тройником
Тройник ТСНР 1020-1020-6,4-0,6-7,5-0,75
ТУ 51-29-81
Необходимый угол поворота в вертикальной плоскости обеспечить поворотом тройника.
Подключение к существующему газопроводу определить по месту. Разработку траншеи производить вручную по 5 м от точки врезки.

Продольный профиль перемычки №5

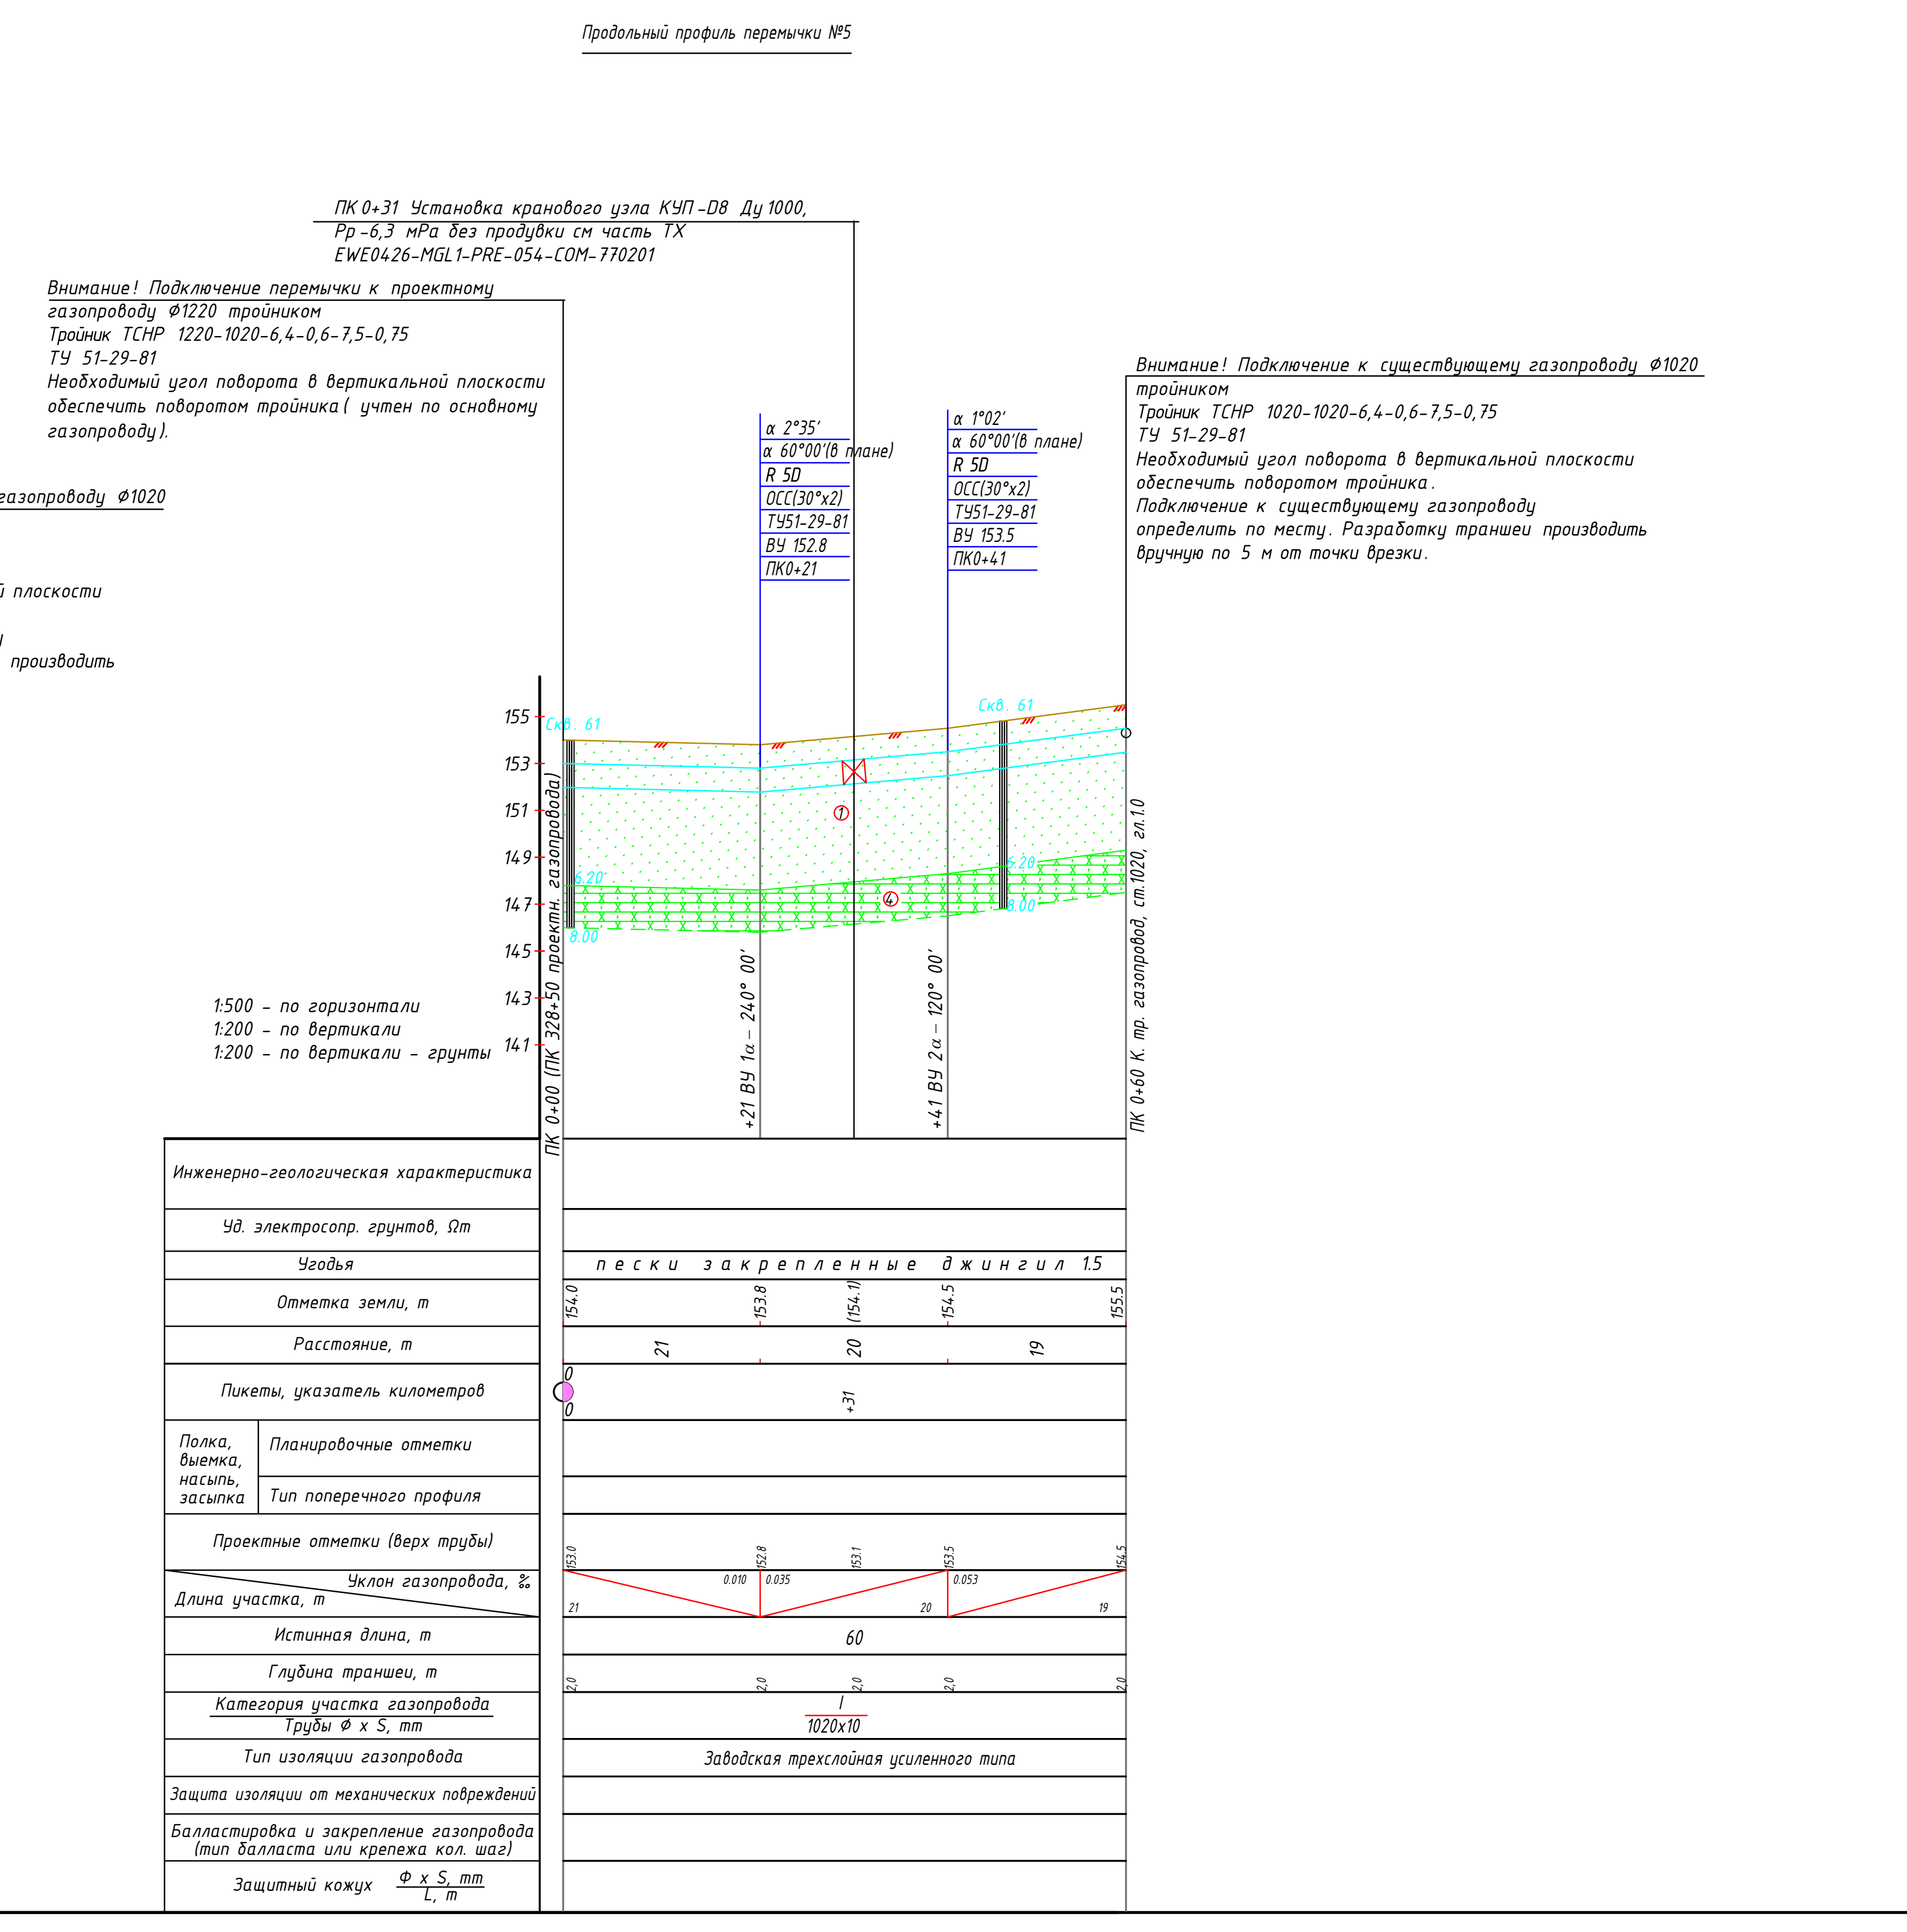
1:500 – по горизонтали
1:200 – по вертикали
1:200 – по вертикали – грунты
α 2°35′
α 60°00′(в плане)
R 5D
ОСС(30°x2)
ТУ51-29-81
ВУ 152.8
ПК0+21
α 1°02′
α 60°00′(в плане)
R 5D
ОСС(30°x2)
ТУ51-29-81
ВУ 153.5
ПК0+41
Скв. 61
Заводская трехслойная усиленного типа

ПК 0+31 Установка кранового узла КУП-D8 Ду 1000,
Рр -6,3 мРа без продувки см часть ТХ
EWE0426-MGL1-PRE-054-COM-770201

Внимание! Подключение перемычки к проектному газопроводу Ø1220 тройником
Тройник ТСНР 1220-1020-6,4-0,6-7,5-0,75
ТУ 51-29-81
Необходимый угол поворота в вертикальной плоскости обеспечить поворотом тройника (учтен по основному газопроводу).

Внимание! Подключение к существующему газопроводу Ø1020 тройником
Тройник ТСНР 1020-1020-6,4-0,6-7,5-0,75
ТУ 51-29-81
Необходимый угол поворота в вертикальной плоскости обеспечить поворотом тройника.
Подключение к существующему газопроводу определить по месту. Разработку траншеи производить вручную по 5 м от точки врезки.

1 Общие данные - чертеж EWE0426-MGL1-PIL-054-COM-660201
2. Ситуационный план см. EWE0426-MGL1-PIL-054-DRW-660202
3 До начала работ руководитель строительной организации должен разработать и согласовать схему и инструкцию по безопасному производству работ в охранной зоне газопровода и его сооружений.
4 Производство работ при пересечении с существующими газопроводами вести в строгом соответствии с "Инструкцией по производству строительных работ в охранных зонах магистральных трубопроводов Мингазпрома" ВСН 51-1-80.
5 Ширину полосы отвода земель для строительства газопровода см. типовой чертеж EWE0426-MGL1-PIL-000-DRW-810201.
6 Охранную зону магистрального газопровода см. типовой чертеж EWE0426-MGL1-PIL-000-DRW-810202.
7 Поперечный разрез траншеи см. типовой чертеж EWE0426-MGL1-PIL-000-DRW-810203.
8. Перед рытьем траншеи на данном участке должна предусматриваться предварительная планировка строительной полосы (срезку грунта в зоне выполнить по проекту).
9. Точное местоположение и глубину заложения существующих трубопроводов определить шурфованием вручную и перед началом работ обозначить предупреждающими и разъясняющими знаками, освещаемыми в ночное время.
10. Земляные работы в зоне по 2 m в обе стороны от пересечений выполнить без применения ударных инструментов вручную в присутствии представителей эксплуатирующих организаций, и известить их о начале и окончании работ на пересечениях.
11. При пересечении с подземными коммуникациями контроль монтажных сварных соединений по 20 m в обе стороны выполнить радиографическим методом.
12. Проезд техники через существующий газопровод выполнить по специально устроенным переездам (ВТУ МГ-1).
13. Производство работ, сварку, контроль монтажных сварных соединений и испытание газопровода производить в соответствии с ШНК 2.05.06-22, QR 02.01, QR 06.08, ВСН 51-3-85, ВСН 005-88, ВСН 006-89, ВСН 011-88, ВСН 012-88, "Правилами техники безопасности при строительстве магистральных стальных трубопроводов".
14 На период эксплуатации по трассе газопровода установить следующие сигнальные знаки:
- на углах поворота в плане трассы опознавательный столб (85.00-08.00-000:00.08-МР);
- сигнальный знак, совмещенный с катодными выводами через 1 km (см. раздел ЭХЗ).
15. Номера существующих ниток изменены и диаметр существующих газопроводов в месте подключения принят 1220 по уточнению Заказчика в схеме PFD л. EWE0426-MGL1-PRE-054-PFD-610101-R2 и откорректированного изыскательского материала (письмо MGL-EM-PBG-EWE-0016).
16. Толщину стенки отводов должен просчитать Завод-изготовитель с учетом своих технологических возможностей, обеспечив прочность и надежность соединительных деталей на расчетный срок службы газопровода, и с учетом того что толщина стенки отводов не менее толщины стенки основной трубы.
17. Стыки врезки в существующий газопровод-гарантийные, которые должны выполняться согласно Правил безопасности при эксплуатации магистральных газопроводов, утвержденных НХК "Узбекнефтегаз", г.Ташкент-2003г.
18. Земляные работы по 5 m в обе стороны от точки врезки в существующий газопровод производить только вручную без применения ударных инструментов.
19. Строительно-монтажные работы по врезке в существующий газопровод производить в присутствии представителя эксплатирующей организации.
20. Врезку в существующий газопровод производить в соответствии с требованиями, изложенными в "Типовой инструкции на производство огневых работ на действующих магистральных газопроводах, газосборных сетях газовых промыслов" утвержденной Мингазпромом 9.07.1971г. и ВСН 006-89.
21. Размещение механизированных колонн, баз, стоянок машин и механизмов, складов ГСМ осуществлять только за пределами минимальных расстояний от оси газопроводов (его объектов) до городов, установленных ШНК 2.05.06-22, Приложение 2.
22. Производство работ при пересечении с существующими газопроводами вести в строгом соответствии с "Инструкцией по производству строительных работ в охранных зонах магистральных трубопроводов Мингазпрома" ВСН 51-1-80.

Экспликация деталей и отдельных изделий газопровода

№ п. п.	Наименование деталей	Ед изм.	Кол.	Примечание
1	ОСС3°-5Д-1220 (12К60)-5,5-075-У ТУ51-29-81	шт	7	
2	ОСС6°-5Д-1220 (12К60)-5,5-075-У ТУ51-29-81	шт	1	
3	ТСНР 1220x1020-6,4-0,6-7,5-0,75-К60 ТУ 51-29-81	шт	2	

Экспликация деталей и отдельных изделий перемычки №4

№ п. п.	Наименование деталей	Ед изм.	Кол.	Примечание
1	ОСС30°-5Д-1020 (10К60)-5,5-075-У ТУ51-29-81	шт	4	
2	ТСНР 1020x1020-6,4-0,6-7,5-0,75-К60 ТУ 51-29-81	шт	1	

Экспликация деталей и отдельных изделий перемычки №5

№ п. п.	Наименование деталей	Ед изм.	Кол.	Примечание
1	ОСС30°-5Д-1020 (10К60)-5,5-075-У ТУ51-29-81	шт	4	
2	ТСНР 1020x1020-6,4-0,6-7,5-0,75-К60 ТУ 51-29-81	шт	1	

Рев.	Дата	Назначение ревизии	Проверил	Утвердил
A2	17.08.2026	Выпущено для строительства		
A1	16.07.2026	Выпущено для строительства		
R2	02.07.2026	Выпущено для рассмотрения		
R1	05.06.2026	Выпущено для рассмотрения		

ЗАКАЗЧИК: UZTRANSGAZ
ГЕНЕРАЛЬНЫЙ ПОДРЯДЧИК: UZBEKENERGOTAMIR
ПОДРЯДЧИК: PBG Pro Build Generation
ГЕНЕРАЛЬНЫЙ ПРОЕКТИРОВЩИК: EAST WEST ENGINEERING

EWE0426-MGL1-PIL-054-ALS-660219-A2

«СТРОИТЕЛЬСТВО НОВЫХ НИТОК (УЧАСТКОВ) ГАЗОПРОВОДОВ «ГАЗЛИ – САРИМОЙ» И «АКЧАЛОК – ГАЗЛИ – НУКУС» ОБЩЕЙ ПРОТЯЖЕННОСТЬЮ НЕ МЕНЕЕ 275 КМ».

Изм.	Кол.уч.	Лист	№док.	Подпись	Дата
ГИП		Схабицкий А.			08.2026
Провер.		Шафиева О.			08.2026
Исполн.		Мухамадеева			08.2026
Н.контр		Схабицкий А.			08.2026

ГАЗОПРОВОД «ГАЗЛИ-САРИМОЙ» (54 КМ)

Стадия	Лист	Листов
РД	1	1

План и продольный профиль газопровода
ПК 320+00 – ПК 340+00, перемычки №4
ПК 0+00 – ПК 0+60 и перемычки №5
ПК 0+00 – ПК 0+60

ООО "EAST-WEST Engineering"
г. Ташкент 2026г.

Формат A2x4