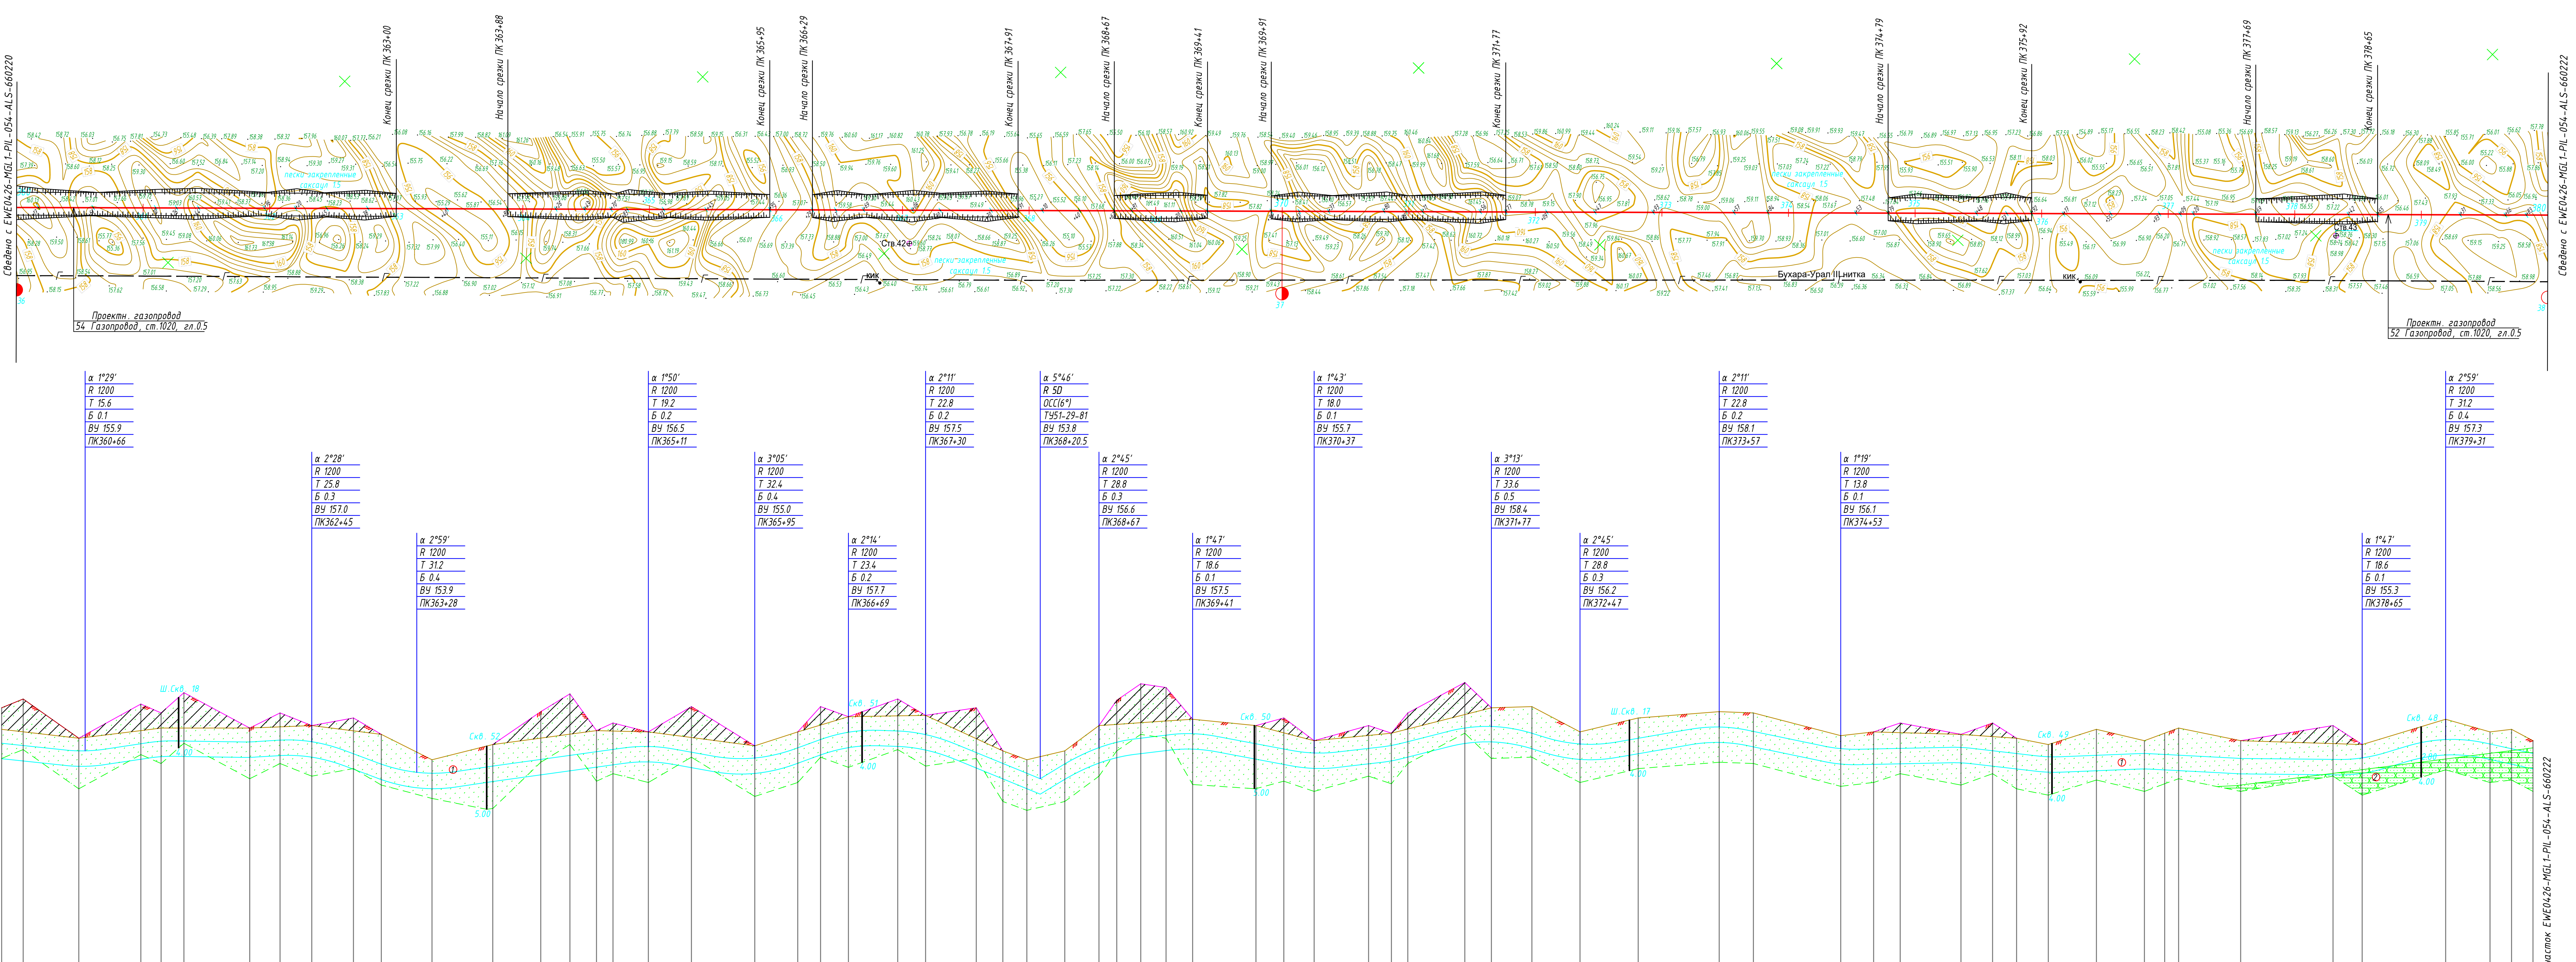

1:2000 - по горизонтали
1:200 - по вертикали
1:200 - по вертикали - грунты

Инженерно-геологическая характеристика	① Песок мелкий с прослойками суглинка и супесей мощностью до 0,8 m. согласно дополнения №3 к ШНК 4.02.01-04 группа грунта по трудности по разработки: механизированным способом (таблица 1-1а) относится к первому абзацу пункта 16, ручным способом (таблица 1-1в) относится к первому абзацу пункта 25, Ro-300 kPa, при водонасыщении Ro-100 kPa. ② Песчаник низкой и средней прочности., согласно ШНК 4.02.01-04 группа грунта по трудности разработки механизированным способом (таблица 1-1) относится к пункту 30 б, согласно дополнения №3 к ШНК 4.02.01-04 группа грунта по трудности разработки ручным способом (таблица 1-1в) относится к второму абзацу пункта 26, Rc-до 1 MPa. ③ Глина с линзами песка, согласно дополнения №3 к ШНК 4.02.01-04 группа грунта по трудности по разработки: механизированным способом (таблица 1-1а) относится к первому абзацу пункта 5, ручным способом (таблица 1-1в) относится к первому абзацу пункта 7, Ro-400 kPa. ④ Алевролит низкой прочности.. согласно дополнения №3 к ШНК 4.02.01-04 группа грунта по трудности по разработки: механизированным способом (таблица 1-1а) относится к первому абзацу пункта 1, ручным способом (таблица 1-1в) относится к первому абзацу пункта 1, Rc- до 1 MPa. ⑤ Насыпной слой
Уд. электросопр. грунтов, Ωm	
Угодья	пески закрепленные джингил 1.5
Отметка земли, m	
Расстояние, m	
Пикеты, указатель километров	360 … 380
Полка, выемка, насыпь, засыпка: Планировочные отметки	
Полка, выемка, насыпь, засыпка: Тип поперечного профиля	Срезка шир. 18 m объем -1685 m³ Срезка шир. 18 m объем -4349 m³ Срезка шир. 18 m объем -4488 m³ Срезка шир. 18 m объем -2597 m³ Срезка шир. 18 m объем -2621 m³ Срезка шир. 18 m объем -3080 m³
Проектные отметки (верх трубы)	
Уклон газопровода, ‰ / Длина участка, m	
Истинная длина, m	2000.4
Глубина траншеи, m	
Категория участка газопровода / Трубы Ф x S, mm	III / 1220x11
Тип изоляции газопровода	заводская трехслойная усиленного типа
Защита изоляции от механических повреждений	
Балластировка и закрепление газопровода (тип балласта или крепежа кол. шаг)	
Защитный кожух Ф x S, mm / L, m	

Согласовано

Геолог	Геолог	Испол.
Усмонов	Жонузоков	Насруллозода
Топограф	Топограф	Гидролог
Бахтигузин	Абдуллаев	Бахадиров

Взам. инв.№

Подп. и дата

Инв. № подл.

Схема расположения листов

EWE0426-MGL1-PIL-054-ALS-660220	EWE0426-MGL1-PIL-054-ALS-660221	EWE0426-MGL1-PIL-054-ALS-660222

Экспликация деталей и отдельных изделий

№ п. п.	Наименование деталей	Ед изм.	Кол.	Примечание
1	ОСС6°-5Д-1220 (12К60)-5,5-075-У ТУ51-29-81	шт	1	

1 Общие данные - чертеж EWE0426-MGL1-PIL-054-COM-660201
2 Ситуационный план см. EWE0426-MGL1-PIL-054-DRW-660202
3 До начала работ руководитель строительной организации должен разработать и согласовать схему и инструкцию по безопасному производству работ в охранной зоне газопровода и его сооружений.
4 Производство работ на данном участке вести в строгом соответствии с "Инструкцией по производству строительных работ в охранных зонах магистральных трубопроводов Мингазпрома" ВСН 51-1-80.
5 Ширину полосы отвода земель для строительства газопровода см. типовой чертеж EWE0426-MGL1-PIL-000-DRW-810201.
6 Охранную зону магистрального газопровода см. типовой чертеж EWE0426-MGL1-PIL-000-DRW-810202.
7 Поперечный разрез траншеи см. типовой чертеж EWE0426-MGL1-PI-000-DRW-810203.

Рев.	Дата	Назначение ревизии	Проверил	Утвердил
A2	17.08.2026	Выпущено для строительства		
A1	16.07.2026	Выпущено для строительства		
R2	02.07.2026	Выпущено для рассмотрения		
R1	05.06.2026	Выпущено для рассмотрения		

ЗАКАЗЧИК: UZTRANSGAZ
ГЕНЕРАЛЬНЫЙ ПОДРЯДЧИК: UZBEKENERGOTAMIR
ПОДРЯДЧИК: PBG Pro Build Generation
ГЕНЕРАЛЬНЫЙ ПРОЕКТИРОВЩИК: EAST WEST ENGINEERING

EWE0426-MGL1-PIL-054-ALS-660221-A2

«СТРОИТЕЛЬСТВО НОВЫХ НИТОК (УЧАСТКОВ) ГАЗОПРОВОДОВ «ГАЗЛИ - САРИМОЙ» И «АКЧАЛОК - ГАЗЛИ - НУКУС» ОБЩЕЙ ПРОТЯЖЕННОСТЬЮ НЕ МЕНЕЕ 275 КМ».

ГАЗОПРОВОД «ГАЗЛИ-САРИМОЙ» (54 КМ)

Изм.	Кол.уч.	Лист	№док.	Подпись	Дата
ГИП		Схабицкий А.			08.2026
Провер.		Шафиева О.			08.2026
Исполн.		Мухамадеева			08.2026
Н.контр		Схабицкий А.			08.2026

Стадия	Лист	Листов
РД	1	1

План и продольный профиль газопровода
ПК 360+00- ПК 380+00

ООО "EAST-WEST Engineering"
г. Ташкент 2026г.