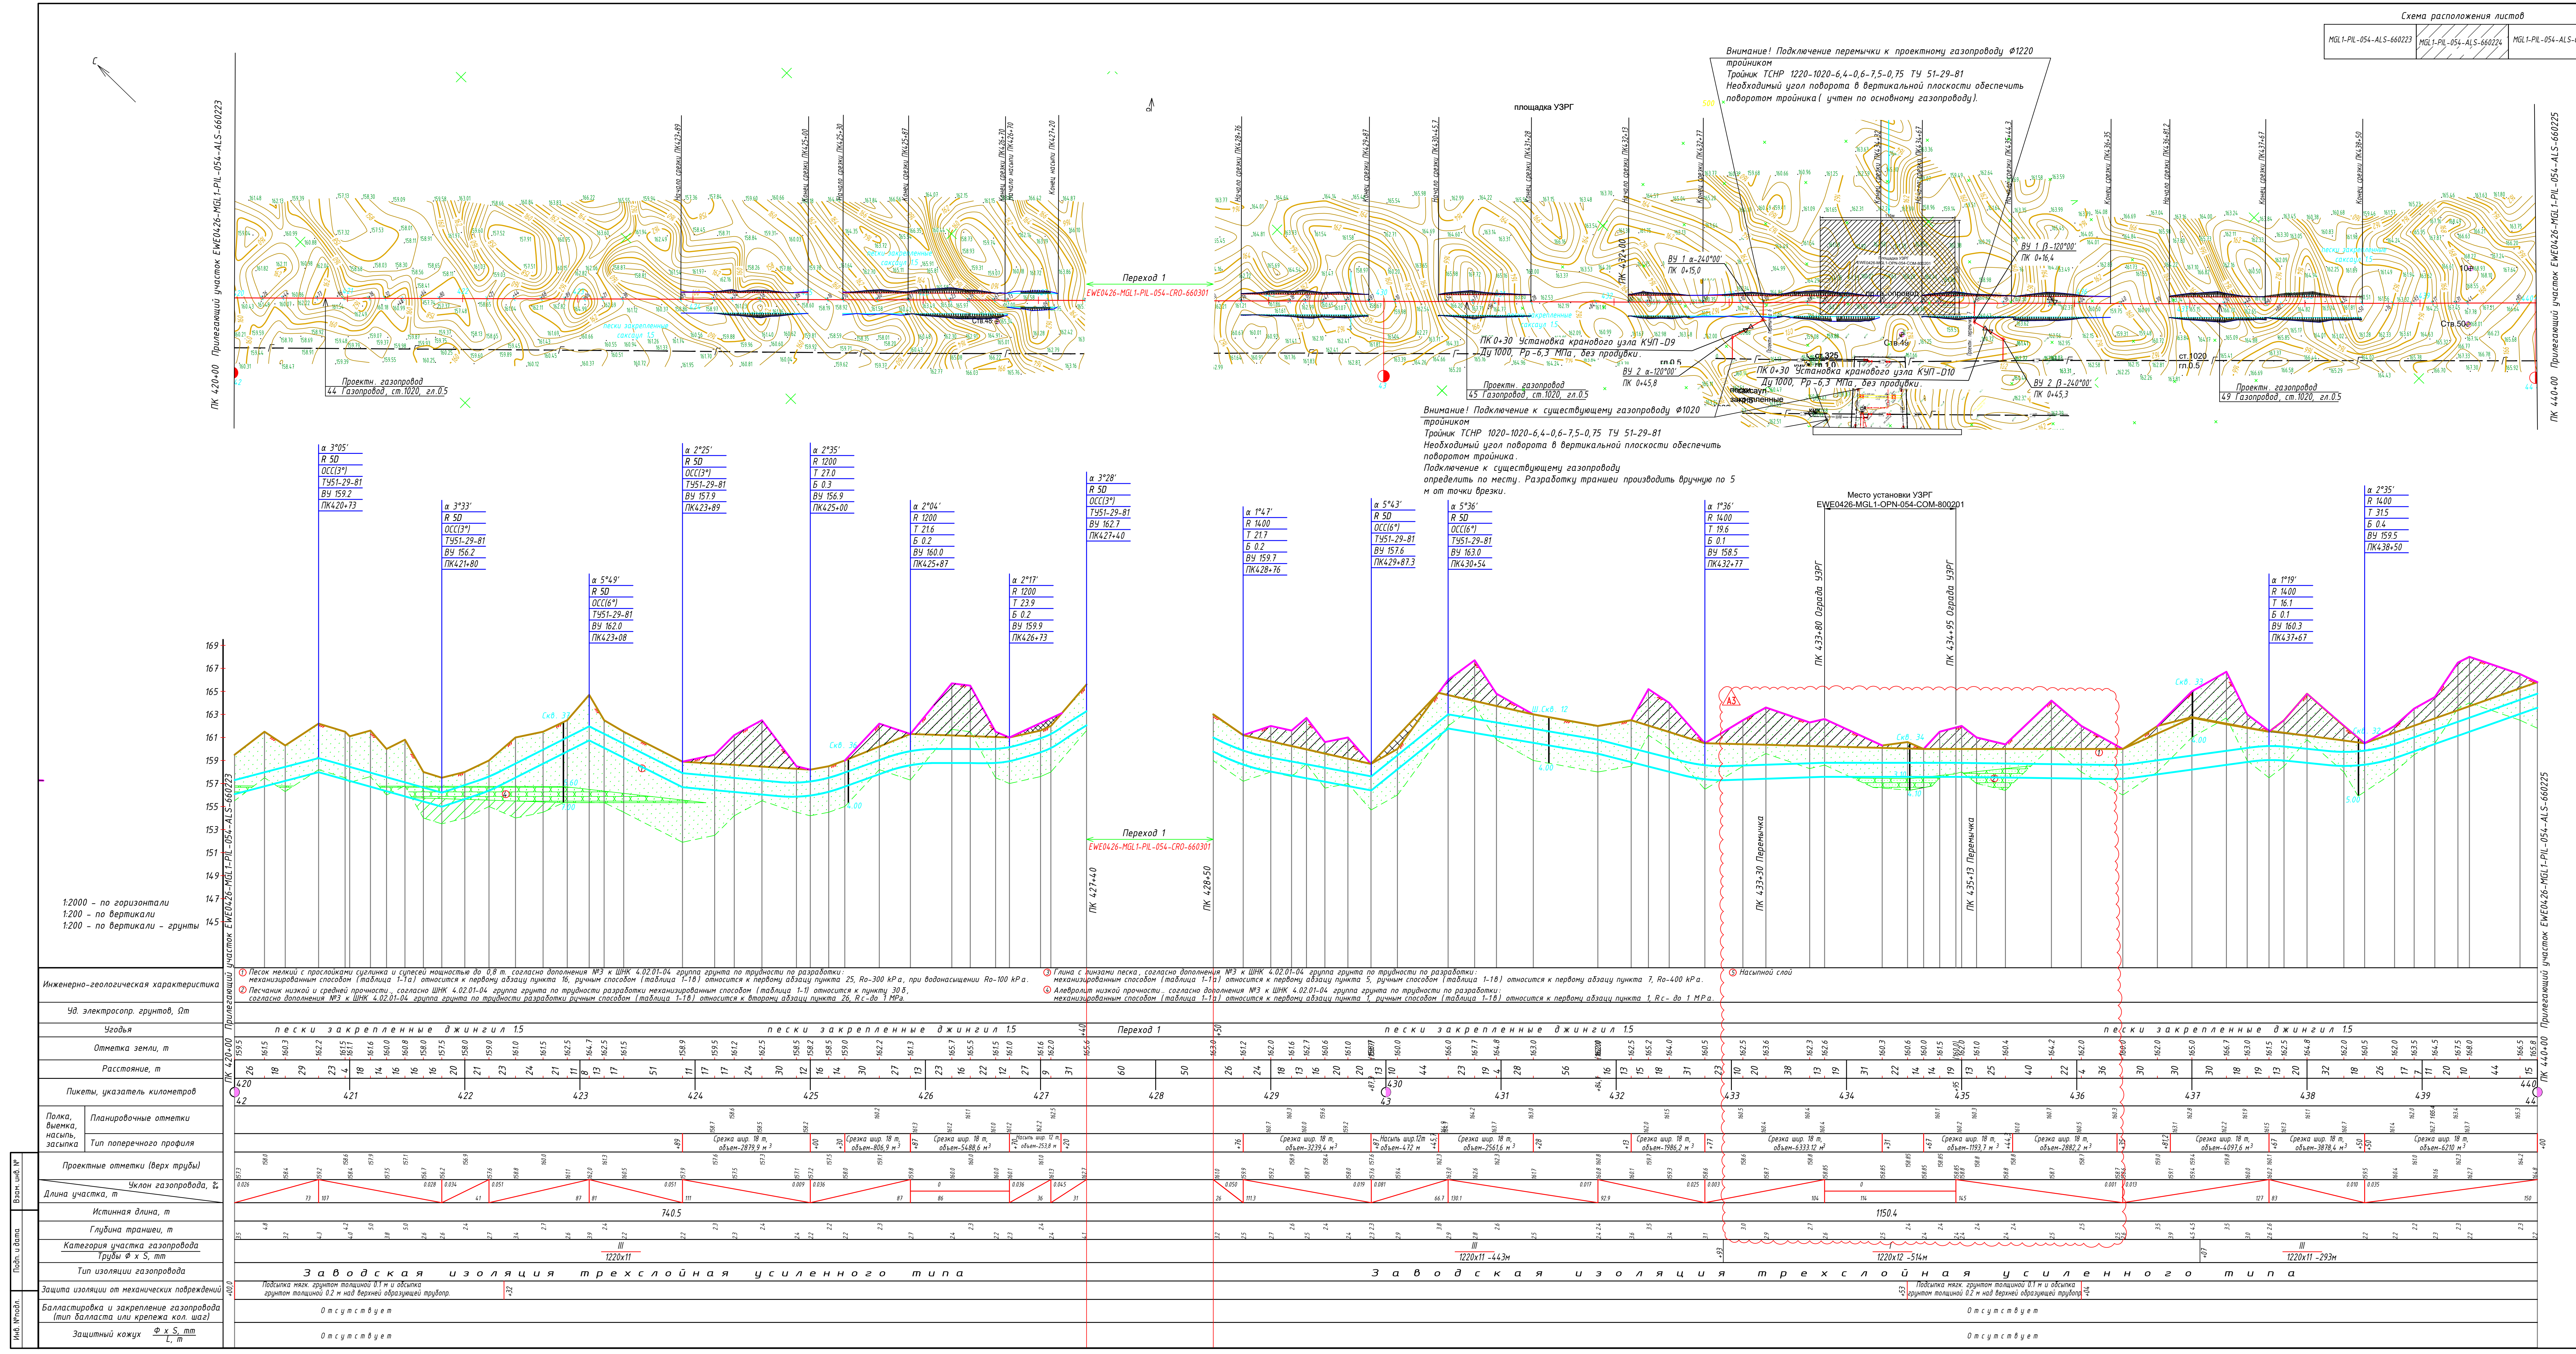
Схема расположения листов
MGL1-PIL-054-ALS-660223
MGL1-PIL-054-ALS-660224
MGL1-PIL-054-ALS-660225
Внимание! Подключение перемычки к проектному газопроводу Ф1220 тройником
Тройник ТСНР 1220-1020-6,4-0,6-7,5-0,75 ТУ 51-29-81
Необходимый угол поворота в вертикальной плоскости обеспечить поворотом тройника (учтен по основному газопроводу).
площадка УЗРГ
ВУ 1 α-240°00'
ПК 0+15,0
ВУ 2 α-120°00'
ПК 0+45,8
ВУ 1 β-120°00'
ПК 0+16,4
ВУ 2 β-240°00'
ПК 0+45,3
ПК 0+30 Установка кранового узла КУП-D9 Ду 1000, Рр -6,3 МПа, без продувки.
ПК 0+30 Установка кранового узла КУП-D10 Ду 1000, Рр -6,3 МПа, без продувки.
Проектн. газопровод
45 Газопровод, ст.1020, гл.0.5
Внимание! Подключение к существующему газопроводу Ф1020 тройником
Тройник ТСНР 1020-1020-6,4-0,6-7,5-0,75 ТУ 51-29-81
Необходимый угол поворота в вертикальной плоскости обеспечить поворотом тройника.
Подключение к существующему газопроводу определить по месту. Разработку траншеи производить вручную по 5 м от точки врезки.
Место установки УЗРГ
EWE0426-MGL1-OPN-054-COM-800201
α 5°43'
R 5D
ОСС(6°)
ТУ51-29-81
ВУ 157.6
ПК429+87.3
α 5°36'
R 5D
ОСС(6°)
ТУ51-29-81
ВУ 163.0
ПК430+54
α 1°36'
R 1400
Т 19.6
Б 0.1
ВУ 158.5
ПК432+77
Переход 1
1:2000 - по горизонтали
1:200 - по вертикали
1:200 - по вертикали - грунты
Инженерно-геологическая характеристика
Ур. земли
Отметка земли, м
Расстояния, м
Пикеты, указатель километров
Тип поперечного профиля
Проектные отметки (верх трубы)
Уклон газопровода, ‰
Длина участка, м
Глубина траншеи, м
Категория участка газопровода
Трубы Ф х S, мм
Тип изоляции газопровода
Защита изоляции от механических повреждений
Балластировка и закрепление газопровода
Защитный кожух
пески закрепленные джинкиль 15
Заводская изоляция трехслойная усиленного типа

Ведомость углов поворотов перемычки №6 в горизонтальной плоскости

№№ углов и створов	Величина левого угла	Длина линии, т	Радиус R, т	Угол α°	Тангенс T₁, т	Тангенс T₂, т	Кривая К, т	Биссектриса Б, т	
0+00									
		15							
ВУ 1	240°00'		5Д	60°00'	(ОСС30°х2°)-5Д-1020 (10К60)-5,5-075-У ТУ51-29-81				
		30,8							
ВУ 2	120°00'		5Д	60°00'	(ОСС30°х2)-5Д-1020 (10К60)-5,5-075-У ТУ51-29-81				
		18,6							
0+64,4									
		L-64,4							

Экспликация деталей и отдельных изделий перемычки №6

№ п. п.	Наименование деталей	Ед изм.	Кол.	Примечание
1	ОСС30°-5Д-1020 (10К60)-5,5-075-У ТУ51-29-81	шт	4	
2	Тройник ТСНР 1020х1020-5,5-0,75-К60 ТУ 51-29-81	шт	1	

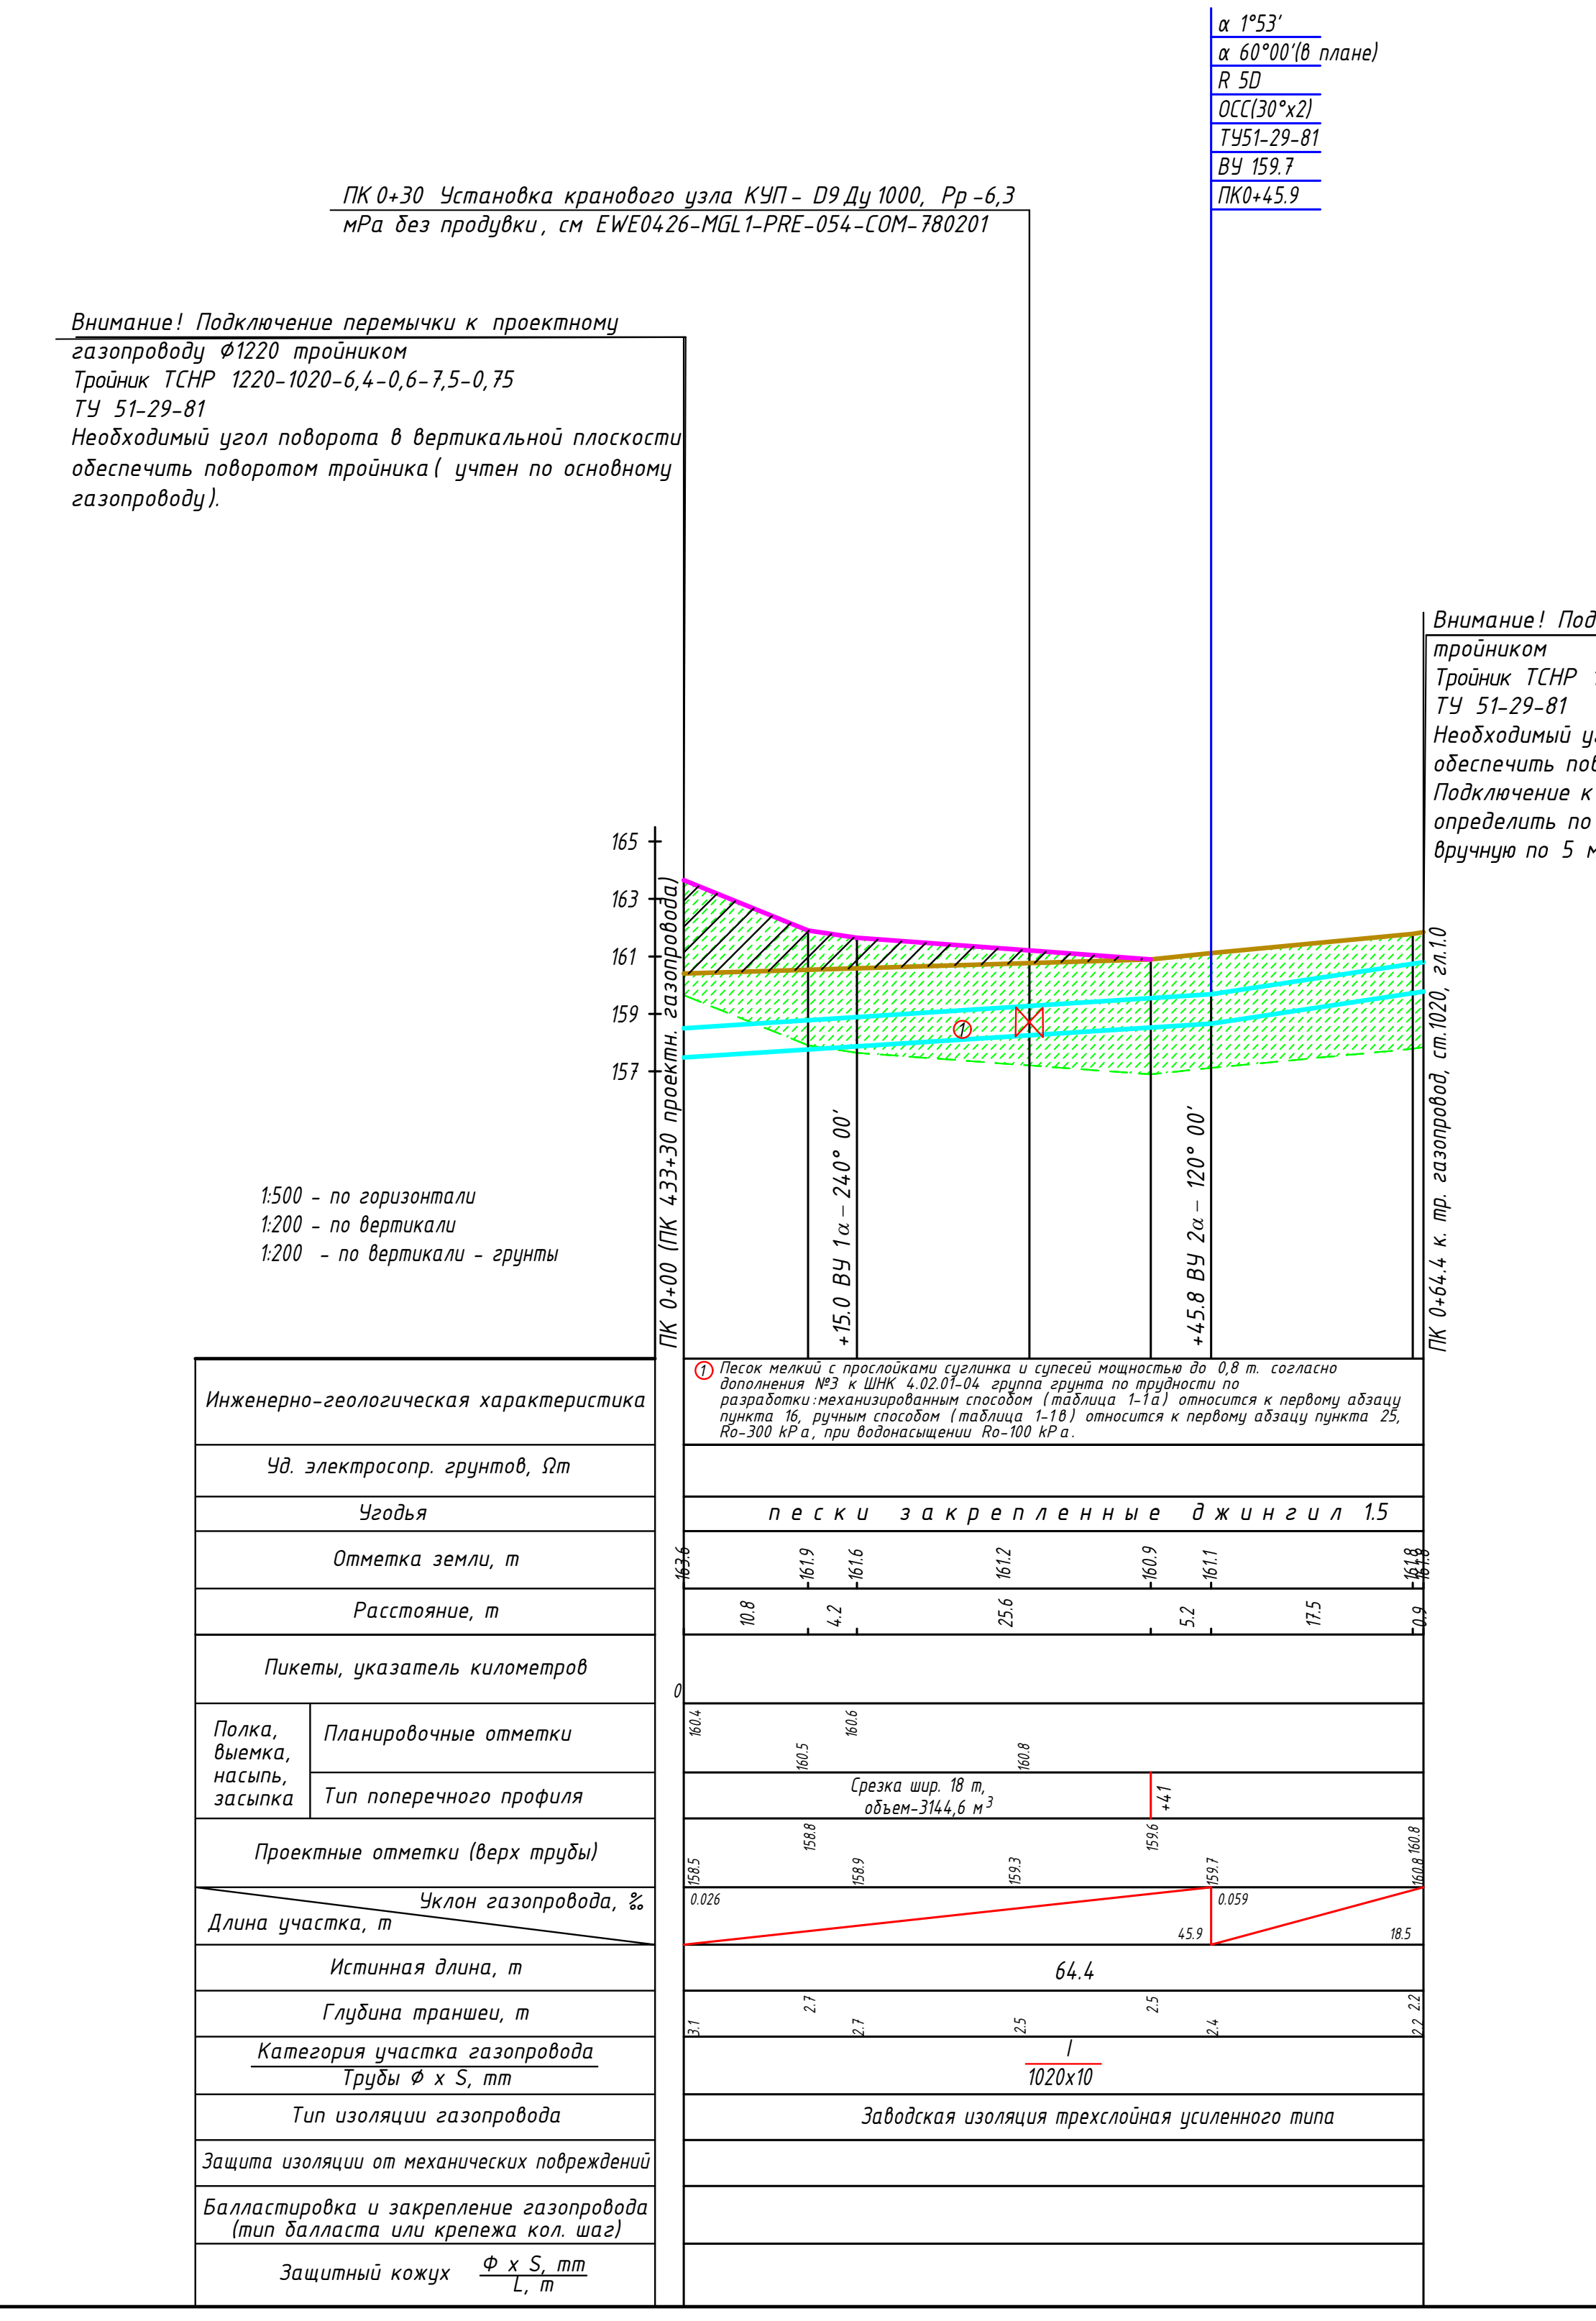
ПК 0+30 Установка кранового узла КУП- D9 Ду 1000, Рр -6,3 мРа без продувки, см EWE0426-MGL1-PRE-054-COM-780201
Внимание! Подключение перемычки к проектному газопроводу Ф1220 тройником
Тройник ТСНР 1220-1020-6,4-0,6-7,5-0,75
ТУ 51-29-81
Необходимый угол поворота в вертикальной плоскости обеспечить поворотом тройника (учтен по основному газопроводу).
α 1°53'
α 60°00'(в плане)
R 5D
ОСС(30°х2)
ТУ51-29-81
ВУ 159.7
ПК0+45.9
Внимание! Подключение к существующему газопроводу Ф1020 тройником
Тройник ТСНР 1020-1020-6,4-0,6-7,5-0,75
ТУ 51-29-81
Необходимый угол поворота в вертикальной плоскости обеспечить поворотом тройника.
Подключение к существующему газопроводу определить по месту. Разработку траншеи производить вручную по 5 м от точки врезки.
165
163
161
159
1:500 - по горизонтали
1:200 - по вертикали
1:200 - по вертикали - грунты
Заводская изоляция трехслойная усиленного типа

Ведомость углов поворотов перемычки №7 в горизонтальной плоскости

№№ углов и створов	Величина левого угла	Длина линии, т	Радиус R, т	Угол α°	Тангенс T₁, т	Тангенс T₂, т	Кривая К, т	Биссектриса Б, т	
0+00									
		16,4							
ВУ 1	120°00'		5Д	60°00'	(ОСС30°х2°)-5Д-1020 (10К60)-5,5-075-У ТУ51-29-81				
		28,9							
ВУ 2	240°00'		5Д	60°00'	(ОСС30°х2)-5Д-1020 (10К60)-5,5-075-У ТУ51-29-81				
		19,1							
0+64,4									
		L-64,4							

Экспликация деталей и отдельных изделий перемычки №7

№ п. п.	Наименование деталей	Ед изм.	Кол.	Примечание
1	ОСС30°-5Д-1020 (10К60)-5,5-075-У ТУ51-29-81	шт	4	
2	Тройник ТСНР 1020х1020-5,5-0,75-К60 ТУ 51-29-81	шт	1	

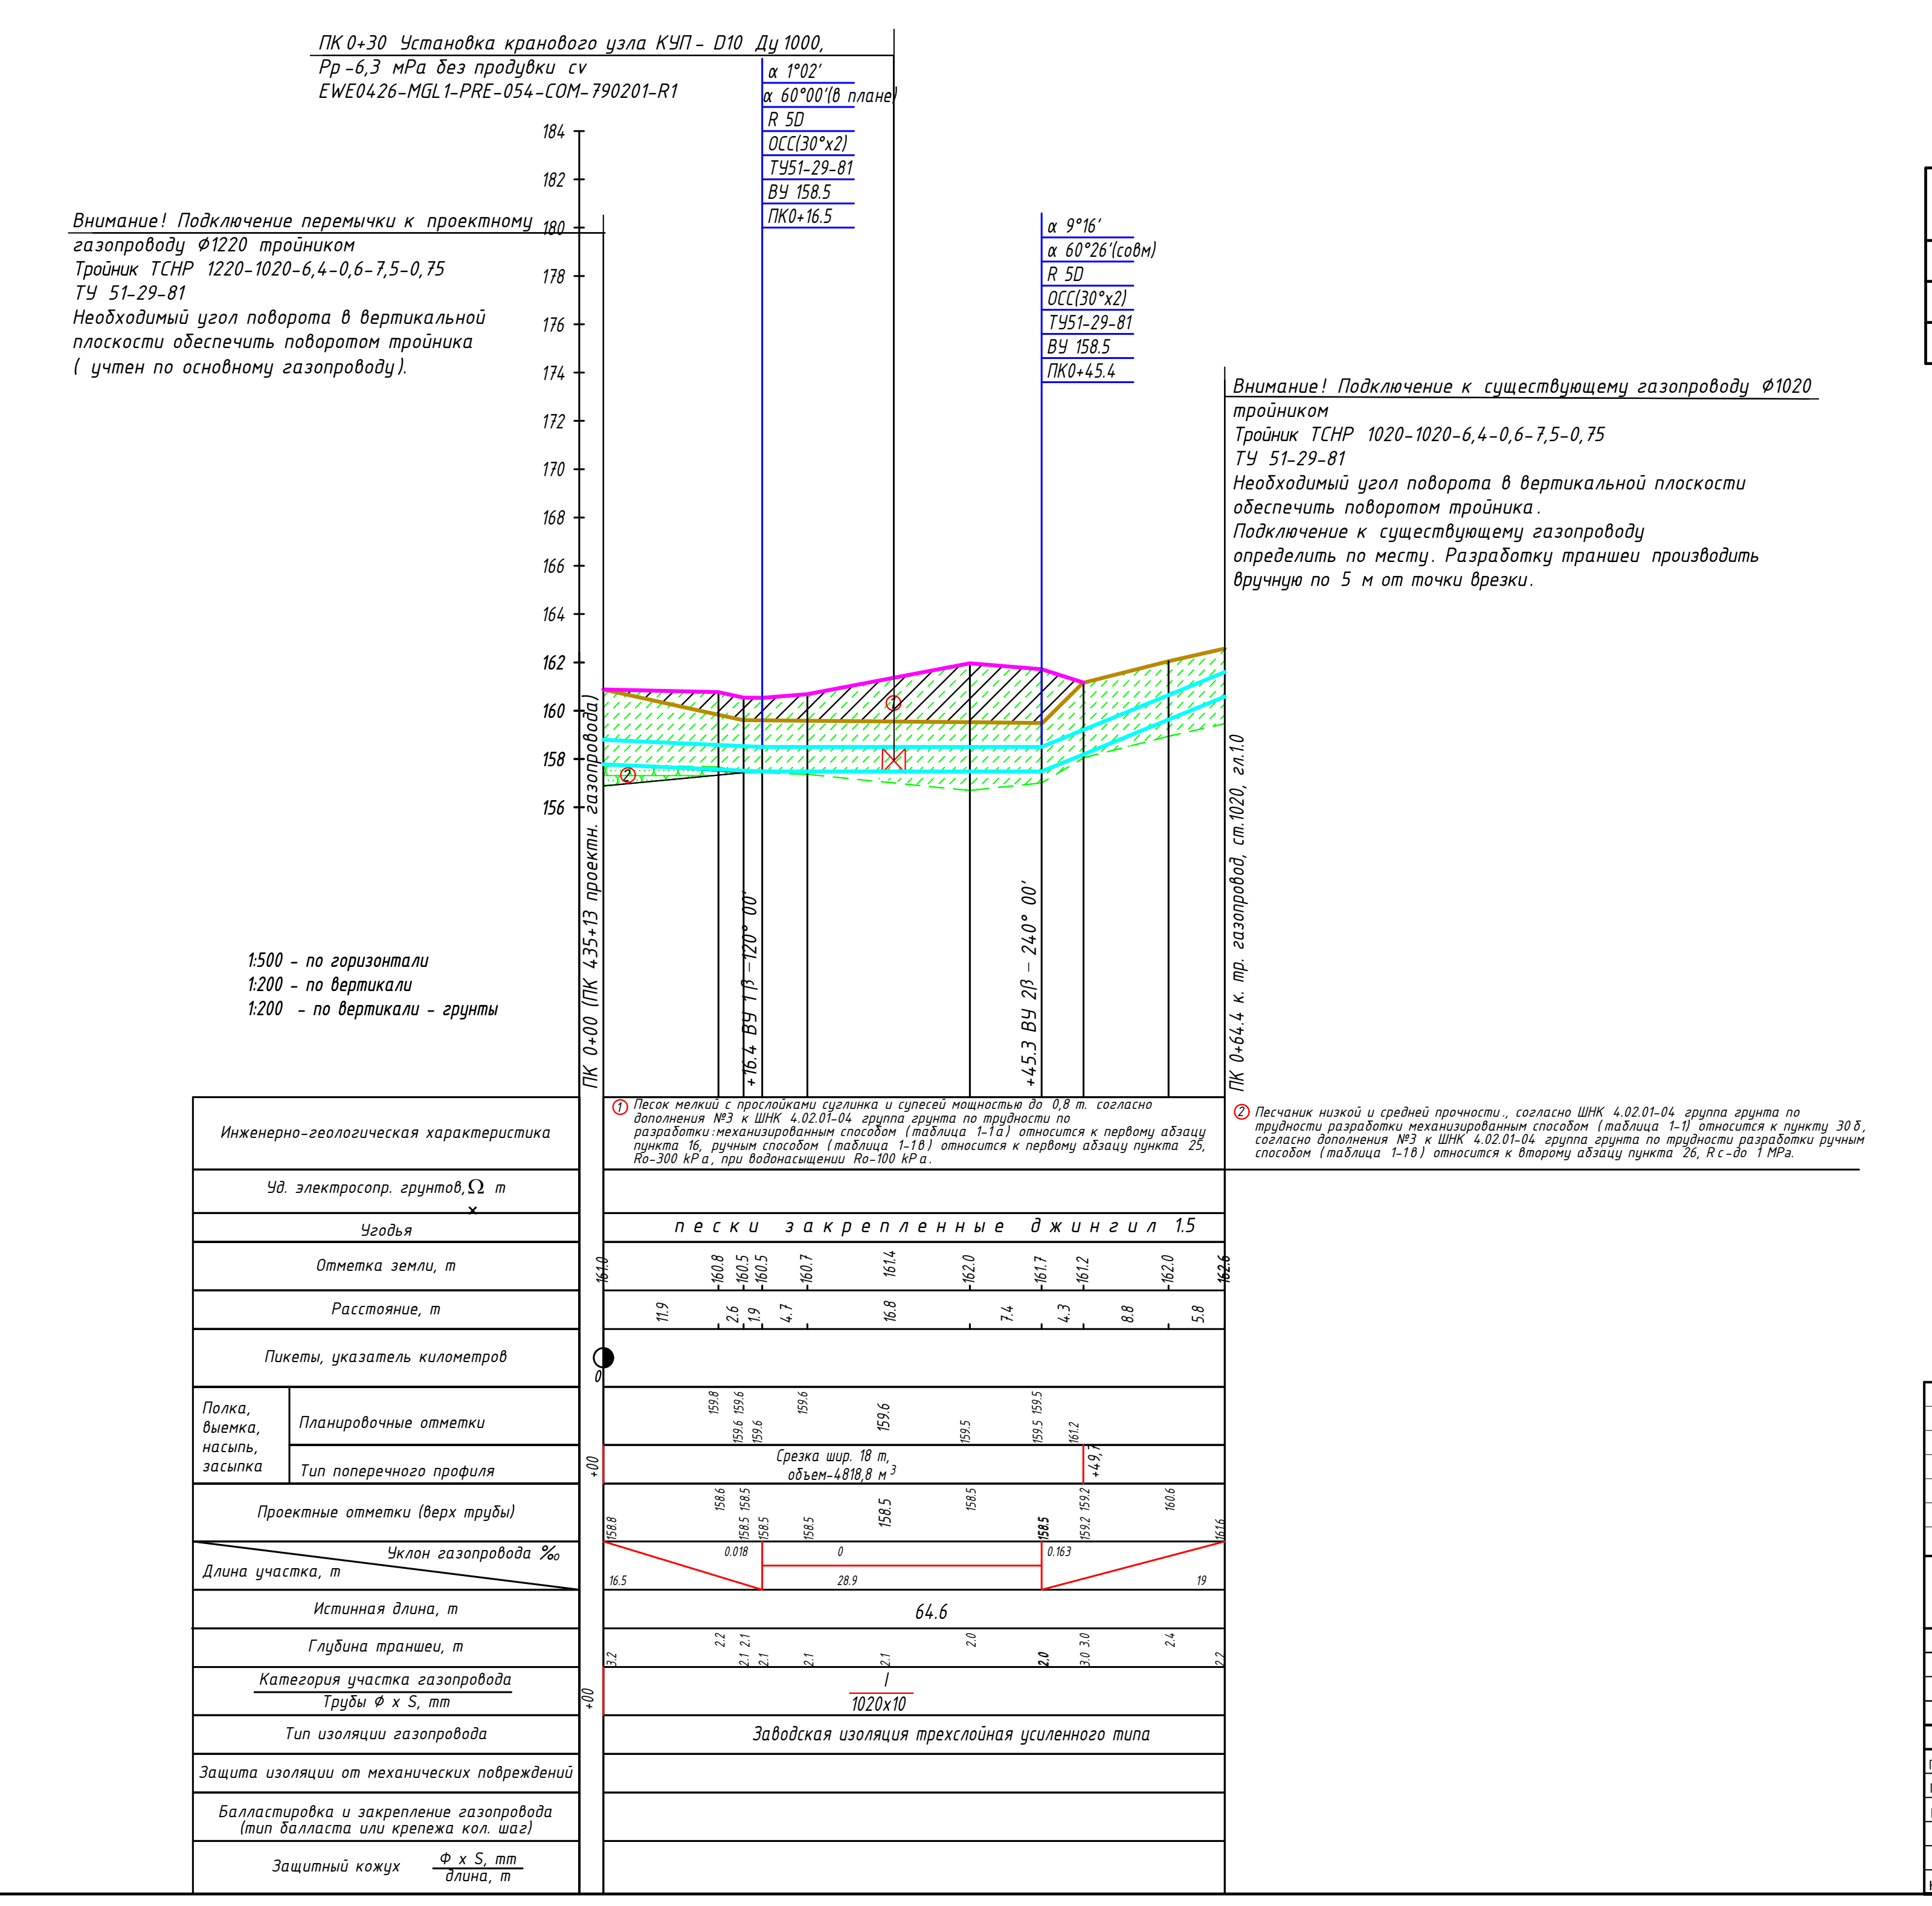
ПК 0+30 Установка кранового узла КУП- D10 Ду 1000, Рр -6,3 мРа без продувки cv EWE0426-MGL1-PRE-054-COM-790201-R1
α 1°02'
α 60°00'(в плане)
R 5D
ОСС(30°х2)
ТУ51-29-81
ВУ 158.5
ПК0+16.5
Внимание! Подключение перемычки к проектному газопроводу Ф1220 тройником
Тройник ТСНР 1220-1020-6,4-0,6-7,5-0,75
ТУ 51-29-81
Необходимый угол поворота в вертикальной плоскости обеспечить поворотом тройника (учтен по основному газопроводу).
α 9°16'
α 60°26'(совм)
R 5D
ОСС(30°х2)
ТУ51-29-81
ВУ 158.5
ПК0+45.4
Внимание! Подключение к существующему газопроводу Ф1020 тройником
Тройник ТСНР 1020-1020-6,4-0,6-7,5-0,75
ТУ 51-29-81
Необходимый угол поворота в вертикальной плоскости обеспечить поворотом тройника.
Подключение к существующему газопроводу определить по месту. Разработку траншеи производить вручную по 5 м от точки врезки.
184
182
180
178
176
174
172
170
168
166
164
162
160
158
1:500 - по горизонтали
1:200 - по вертикали
1:200 - по вертикали - грунты
Заводская изоляция трехслойная усиленного типа

1 Общие данные - чертеж EWE0426-MGL1-PIL-054-COM-660201
2 Ситуационный план см. EWE0426-MGL1-PIL-054-DRW-660202
3 До начала работ руководитель строительной организации должен разработать и согласовать схему и инструкцию по безопасному производству работ в охранной зоне газопровода и его сооружений.
4 Производство работ на данном участке вести в строгом соответствии с "Инструкцией по производству строительных работ в охранных зонах магистральных трубопроводов Мингазпрома" ВСН 51-1-80.
5 Ширину полосы отвода земель для строительства газопровода см. типовой чертеж EWE0426-MGL1-PIL-000-DRW-810201.
6 Охранную зону магистрального газопровода см. типовой чертеж EWE0426-MGL1-PIL-000-DRW-810202.
7 Поперечный разрез траншеи см. типовой чертеж EWE0426-MGL1-PIL-000-DRW-810203.
8 Стыки врезки в существующий газопровод-гарантийные, которые должны быть в строгом соответствии с "Правилами безопасности при эксплуатации магистральных газопроводов" 2003 г.
9 Врезку в существующие газопроводы производить в соответствии с требованиями, изложенными в "Типовой инструкции на производство огневых работ на действующих магистральных газопроводах, газосборных сетях, газовых промыслов", утвержденных Мингазпромом 9 июня 1971 г., ВСН 006-89.
10 Размещение механизированных колонн, баз, стоянок машин и механизмов, складов ГСМ и другого оборудования осуществлять только за пределами опасной зоны газопровода.
11 Земляные работы в зоне по 5 м в обе стороны от врезки в существующий газопровод выполнить без применения ударных инструментов вручную в присутствии представителя организации, эксплуатирующей этот газопровод.
12 Производство работ при пересечении с существующим газопроводами вести в строгом соответствии с "Инструкцией по производству строительных работ в охранных зонах магистральных трубопроводов Мингазпрома" ВСН 51-1-80.
A3
13 При выявлении в процессе производства строительно-монтажных работ по трассе газопровода фактических отметок поверхности земли в барханных песках, отличающихся от проектных отметок, предусмотреть укладку газопровода с обеспечением проектной глубины заложения и засыпки не менее 1,0 м над верхней образующей трубы.
При этом фактическое положение газопровода по высоте должно быть отражено в исполнительной документации.
Выявленные изменения фактических отметок и положения газопровода внести в исполнительную геодезическую документацию (исполнительную схему) и отразить соответствующей записью в журнале авторского надзора.

Экспликация деталей и отдельных изделий

№ п. п.	Наименование деталей	Ед изм.	Кол.	Примечание
1	ОСС6°-5Д-1220 (12К60)-5,5-075-У ТУ51-29-81	шт	3	A3
2	ОСС3°-5Д-1220 (12К60)-5,5-075-У ТУ51-29-81	шт	4	
3	Тройник ТСНР 1220х1020-5,5-0,75-К60 ТУ 51-29-81	шт	2	

Рев.	Дата	Назначение ревизии	Проверил	Утвердил
A3	16.09.2026	Выпущено для строительства		
A2	18.08.2026	Выпущено для строительства		
A1	16.07.2026	Выпущено для строительства		
R2	30.06.2026	Выпущено для рассмотрения		
R1	05.06.2026	Выпущено для рассмотрения		

ЗАКАЗЧИК: UZTRANSGAZ
ГЕНЕРАЛЬНЫЙ ПОДРЯДЧИК: UET UZBEKENERGOTAMIR
ПОДРЯДЧИК: PBG Pro Build Generation
ГЕНЕРАЛЬНЫЙ ПРОЕКТИРОВЩИК: EAST WEST ENGINEERING

EWE0426-MGL1-PIL-054-ALS-660224-A3

«СТРОИТЕЛЬСТВО НОВЫХ НИТОК (УЧАСТКОВ) ГАЗОПРОВОДОВ «ГАЗЛИ - САРИМОЙ» И «АКЧАЛОК - ГАЗЛИ - НУКУС» ОБЩЕЙ ПРОТЯЖЕННОСТЬЮ НЕ МЕНЕЕ 275 КМ».

Изм.	Кол.уч.	Лист	№док.	Подпись	Дата
ГИП		Кирпичников С.			09.2026
Провер.		Шафиева О.			09.2026
Исполн.		Асхатов А.			09.2026
Н.контр		Кирпичников С.			09.2026

ГАЗОПРОВОД «ГАЗЛИ-САРИМОЙ» (54 КМ)

Стадия	Лист	Листов
РД	1	1

План и продольный профиль газопровода
ПК 420+00- ПК 440+00, перемычки №6
ПК 0+00- ПК 0+64,4 и перемычки №7
ПК 0+00- ПК 0+64,4

ООО "EAST-WEST Engineering"
г. Ташкент 2026г.

Формат А2х5