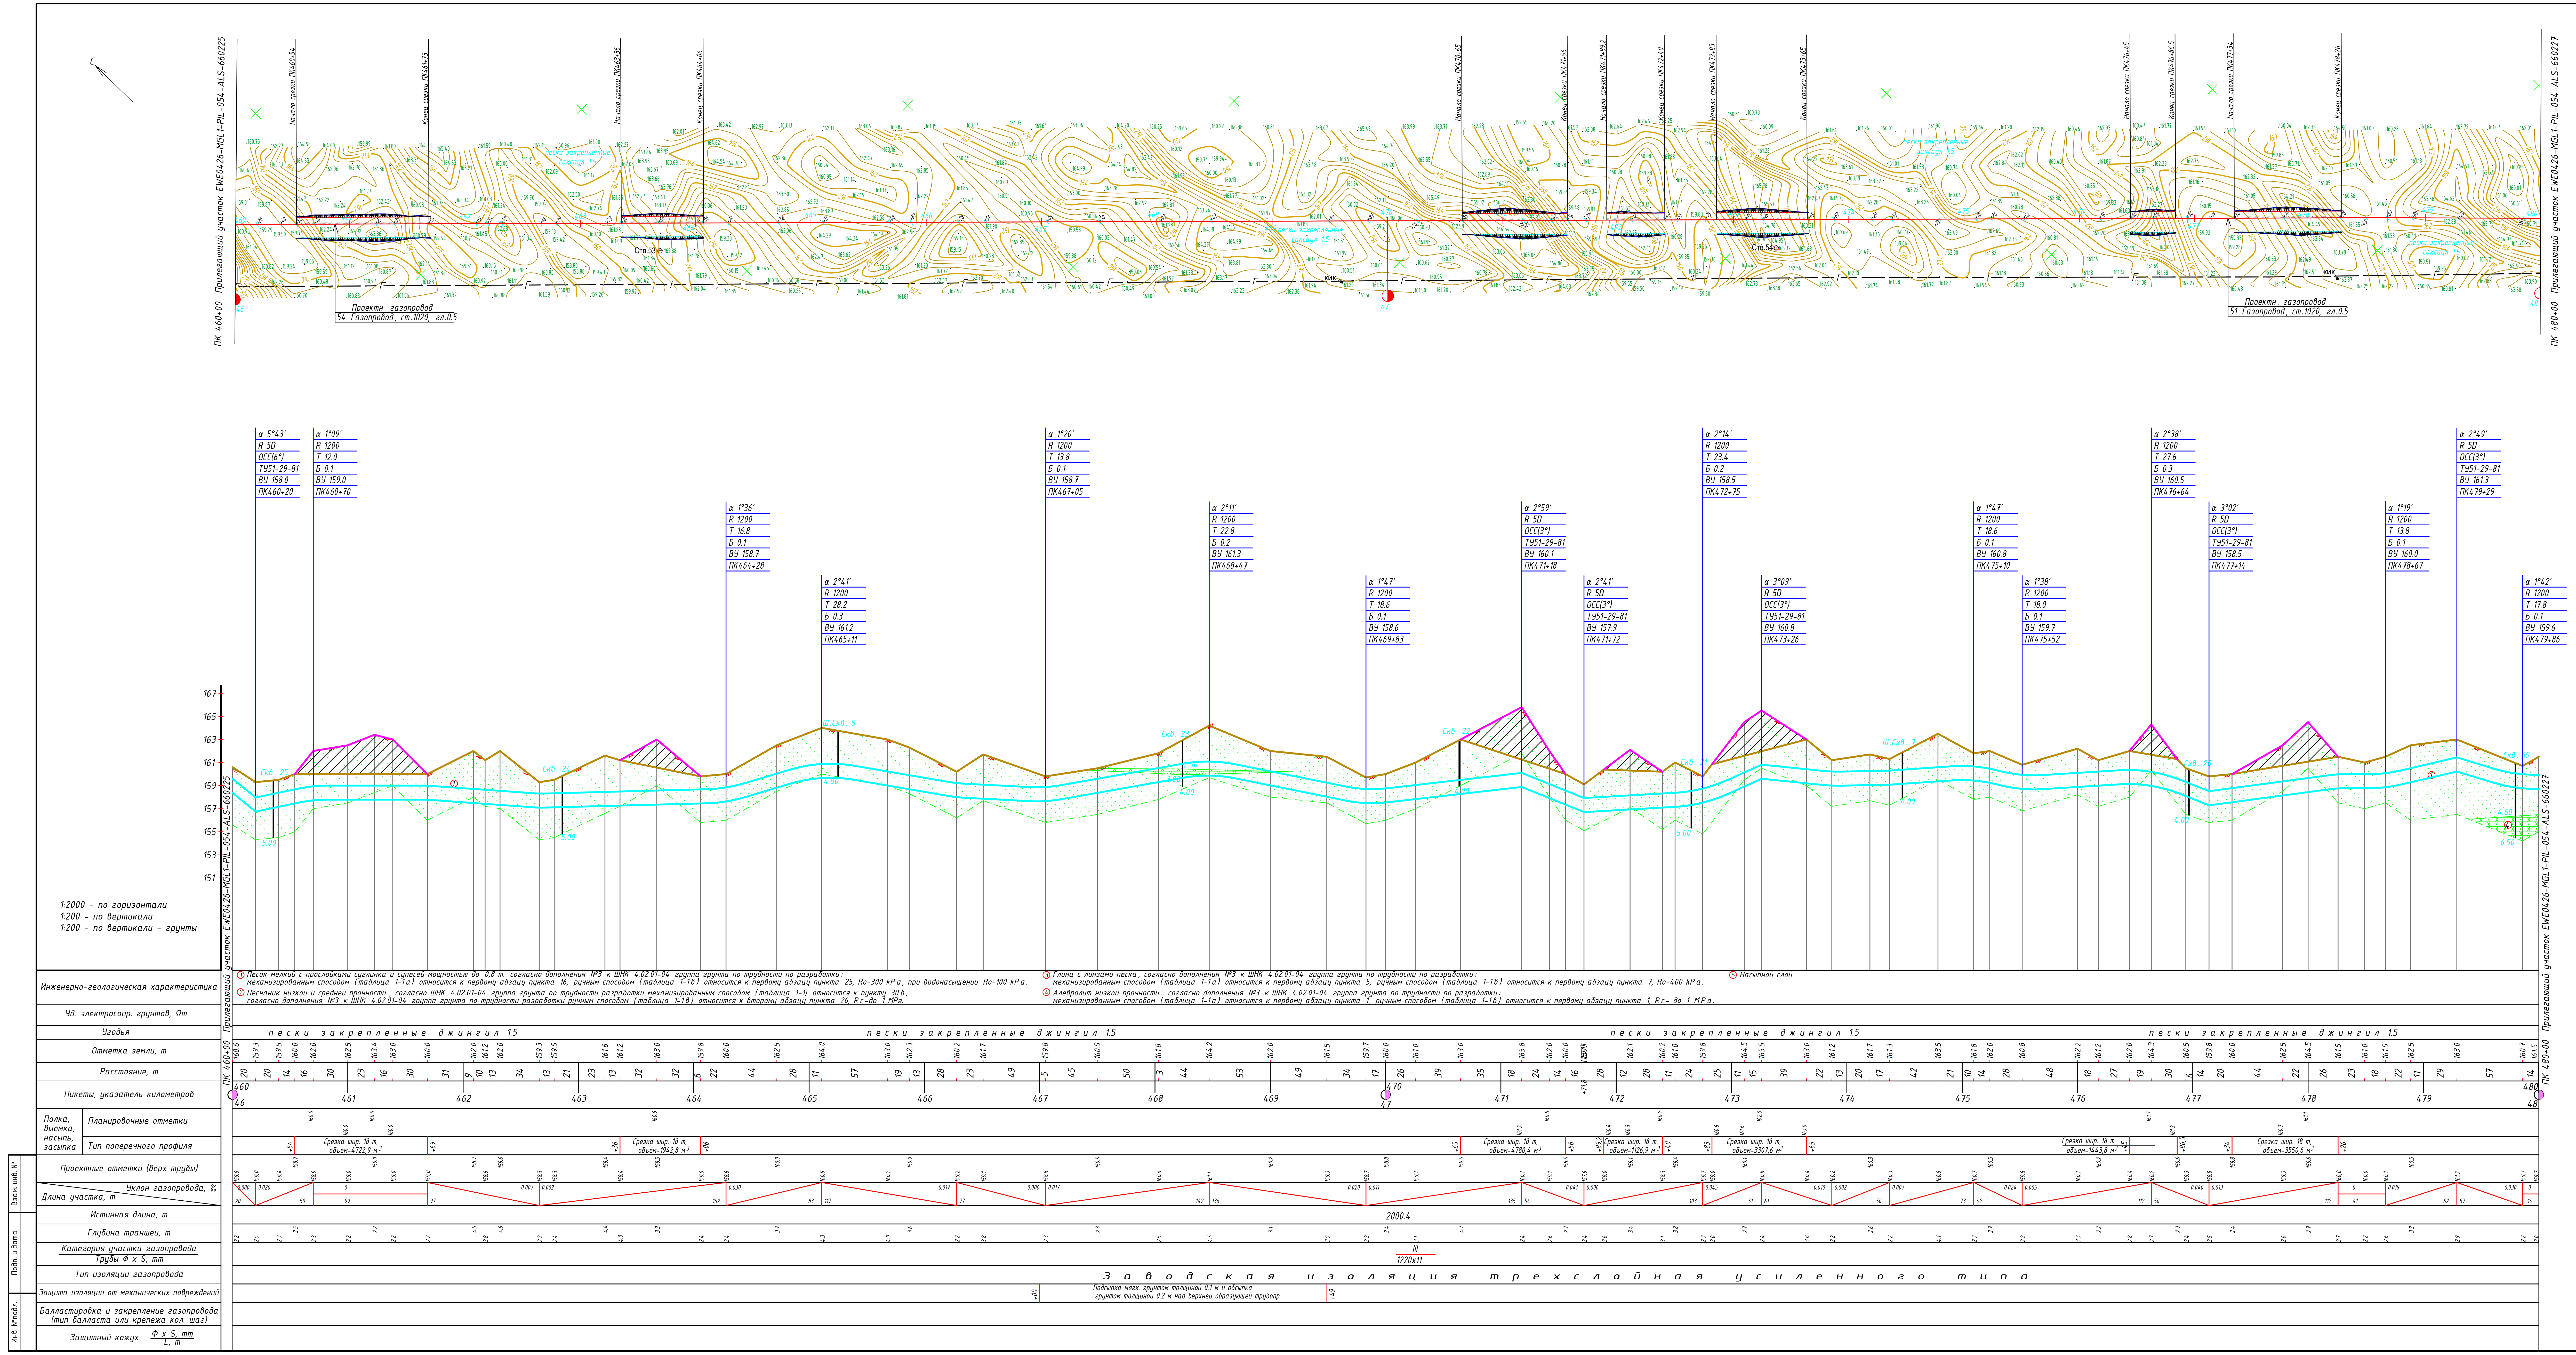
Прилегающий участок EWE0426-MGL1-PIL-054-ALS-660225
ПК 460+00
Прилегающий участок EWE0426-MGL1-PIL-054-ALS-660227
ПК 480+00
Проектн. газопровод
54 Газопровод, ст.1020, гл.0.5
Проектн. газопровод
51 Газопровод, ст.1020, гл.0.5
КИК
пески закрепленные саксаул 1.5
1:2000 - по горизонтали
1:200 - по вертикали
1:200 - по вертикали - грунты
Инженерно-геологическая характеристика
① Песок мелкий с прослойками суглинка и супесей мощностью до 0,8 т. согласно дополнения №3 к ШНК 4.02.01-04 группа грунта по трудности по разработки: механизированным способом (таблица 1-1а) относится к первому абзацу пункта 16, ручным способом (таблица 1-1в) относится к первому абзацу пункта 25, Ro-300 kPa, при водонасыщении Ro-100 kPa.
② Песчаник низкой и средней прочности., согласно ШНК 4.02.01-04 группа грунта по трудности разработки механизированным способом (таблица 1-1) относится к пункту 30 б, согласно дополнения №3 к ШНК 4.02.01-04 группа грунта по трудности разработки ручным способом (таблица 1-1в) относится к второму абзацу пункта 26, Rc-до 1 MPa.
③ Глина с линзами песка, согласно дополнения №3 к ШНК 4.02.01-04 группа грунта по трудности по разработки: механизированным способом (таблица 1-1а) относится к первому абзацу пункта 5, ручным способом (таблица 1-1в) относится к первому абзацу пункта 7, Ro-400 kPa.
④ Алевролит низкой прочности.. согласно дополнения №3 к ШНК 4.02.01-04 группа грунта по трудности по разработки: механизированным способом (таблица 1-1а) относится к первому абзацу пункта 1, ручным способом (таблица 1-1в) относится к первому абзацу пункта 1, Rc- до 1 MPa.
⑤ Насыпной слой
Уд. электросопр. грунтов, Ωm
Угодья
пески закрепленные джингил 1.5
Отметка земли, m
Расстояние, m
Пикеты, указатель километров
Полка, выемка, насыпь, засыпка
Планировочные отметки
Тип поперечного профиля
Срезка шир. 18 m, объем-4722,9 м³
Срезка шир. 18 m, объем-4780,4 м³
Срезка шир. 18 m, объем-1126,9 м³
Срезка шир. 18 m, объем-3307,6 м³
Срезка шир. 18 m, объем-1443,8 м³
Проектные отметки (верх трубы)
Уклон газопровода, ‰
Длина участка, m
Истинная длина, m
2000.4
Глубина траншеи, m
Категория участка газопровода / Трубы Ø x S, mm
III / 1220x11
Тип изоляции газопровода
Заводская изоляция трехслойная усиленного типа
Защита изоляции от механических повреждений
Подсыпка мягк. грунтом толщиной 0.1 м и обсыпка грунтом толщиной 0.2 м над верхней образующей трубопр.
Балластировка и закрепление газопровода (тип балласта или крепежа кол. шаг)
Защитный кожух Ø x S, mm / L, m
Взам. инв. №
Подп. и дата
Инв. №подл.

Экспликация деталей и отдельных изделий

№ п. п.	Наименование деталей	Ед изм.	Кол.	Примечание
1	ОСС6°-5Д-1220 (12К60)-5,5-075-У ТУ51-29-81	шт	1	
2	ОСС3°-5Д-1220 (12К60)-5,5-075-У ТУ51-29-81	шт	5	

Схема расположения листов

MGL1-PIL-054-ALS-660225	MGL1-PIL-054-ALS-660226	MGL1-PIL-054-ALS-660227

1 Общие данные - чертеж EWE0426-MGL1-PIL-054-COM-660201
2 Ситуационный план см. EWE0426-MGL1-PIL-054-DRW-660202
3 До начала работ руководитель строительной организации должен разработать и согласовать схему и инструкцию по безопасному производству работ в охранной зоне газопровода и его сооружений.
4 Производство работ на данном участке вести в строгом соответствии с "Инструкцией по производству строительных работ в охранных зонах магистральных трубопроводов Мингазпрома" ВСН 51-1-80.
5 Ширину полосы отвода земель для строительства газопровода см. типовой чертеж EWE0426-MGL1-PIL-000-DRW-810201.
6 Охранную зону магистрального газопровода см. типовой чертеж EWE0426-MGL1-PIL-000-DRW-810202.
7 Поперечный разрез траншеи см. типовой чертеж EWE0426-MGL1-PIL-000-DRW-810203.

Рев.	Дата	Назначение ревизии	Проверил	Утвердил
A2	18.08.2026	Выпущено для строительства		
A1	16.07.2026	Выпущено для строительства		
R2	30.06.2026	Выпущено для рассмотрения		
R1	05.06.2026	Выпущено для рассмотрения		

ЗАКАЗЧИК: UTG UZTRANSGAZ
ГЕНЕРАЛЬНЫЙ ПОДРЯДЧИК: UET UZBEKENERGOTAMIR
ПОДРЯДЧИК: PBG Pro Build Generation
ГЕНЕРАЛЬНЫЙ ПРОЕКТИРОВЩИК: EAST WEST ENGINEERING

EWE0426-MGL1-PIL-054-ALS-660226-A2

«СТРОИТЕЛЬСТВО НОВЫХ НИТОК (УЧАСТКОВ) ГАЗОПРОВОДОВ «ГАЗЛИ - САРИМОЙ» И «АКЧАЛОК - ГАЗЛИ - НУКУС» ОБЩЕЙ ПРОТЯЖЕННОСТЬЮ НЕ МЕНЕЕ 275 КМ».

Изм.	Кол.уч.	Лист	№док.	Подпись	Дата
ГИП		Схабицкий А.			08.2026
Провер.		Шафиева О.			08.2026
Исполн.		Асхатов А.			08.2026
Н.контр		Схабицкий А.			08.2026

ГАЗОПРОВОД «ГАЗЛИ-САРИМОЙ» (54 КМ)

Стадия	Лист	Листов
РД	1	1

План и продольный профиль газопровода
ПК 460+00- ПК 480+00

ООО "EAST-WEST Engineering"
г. Ташкент 2026г.

Формат A2x4