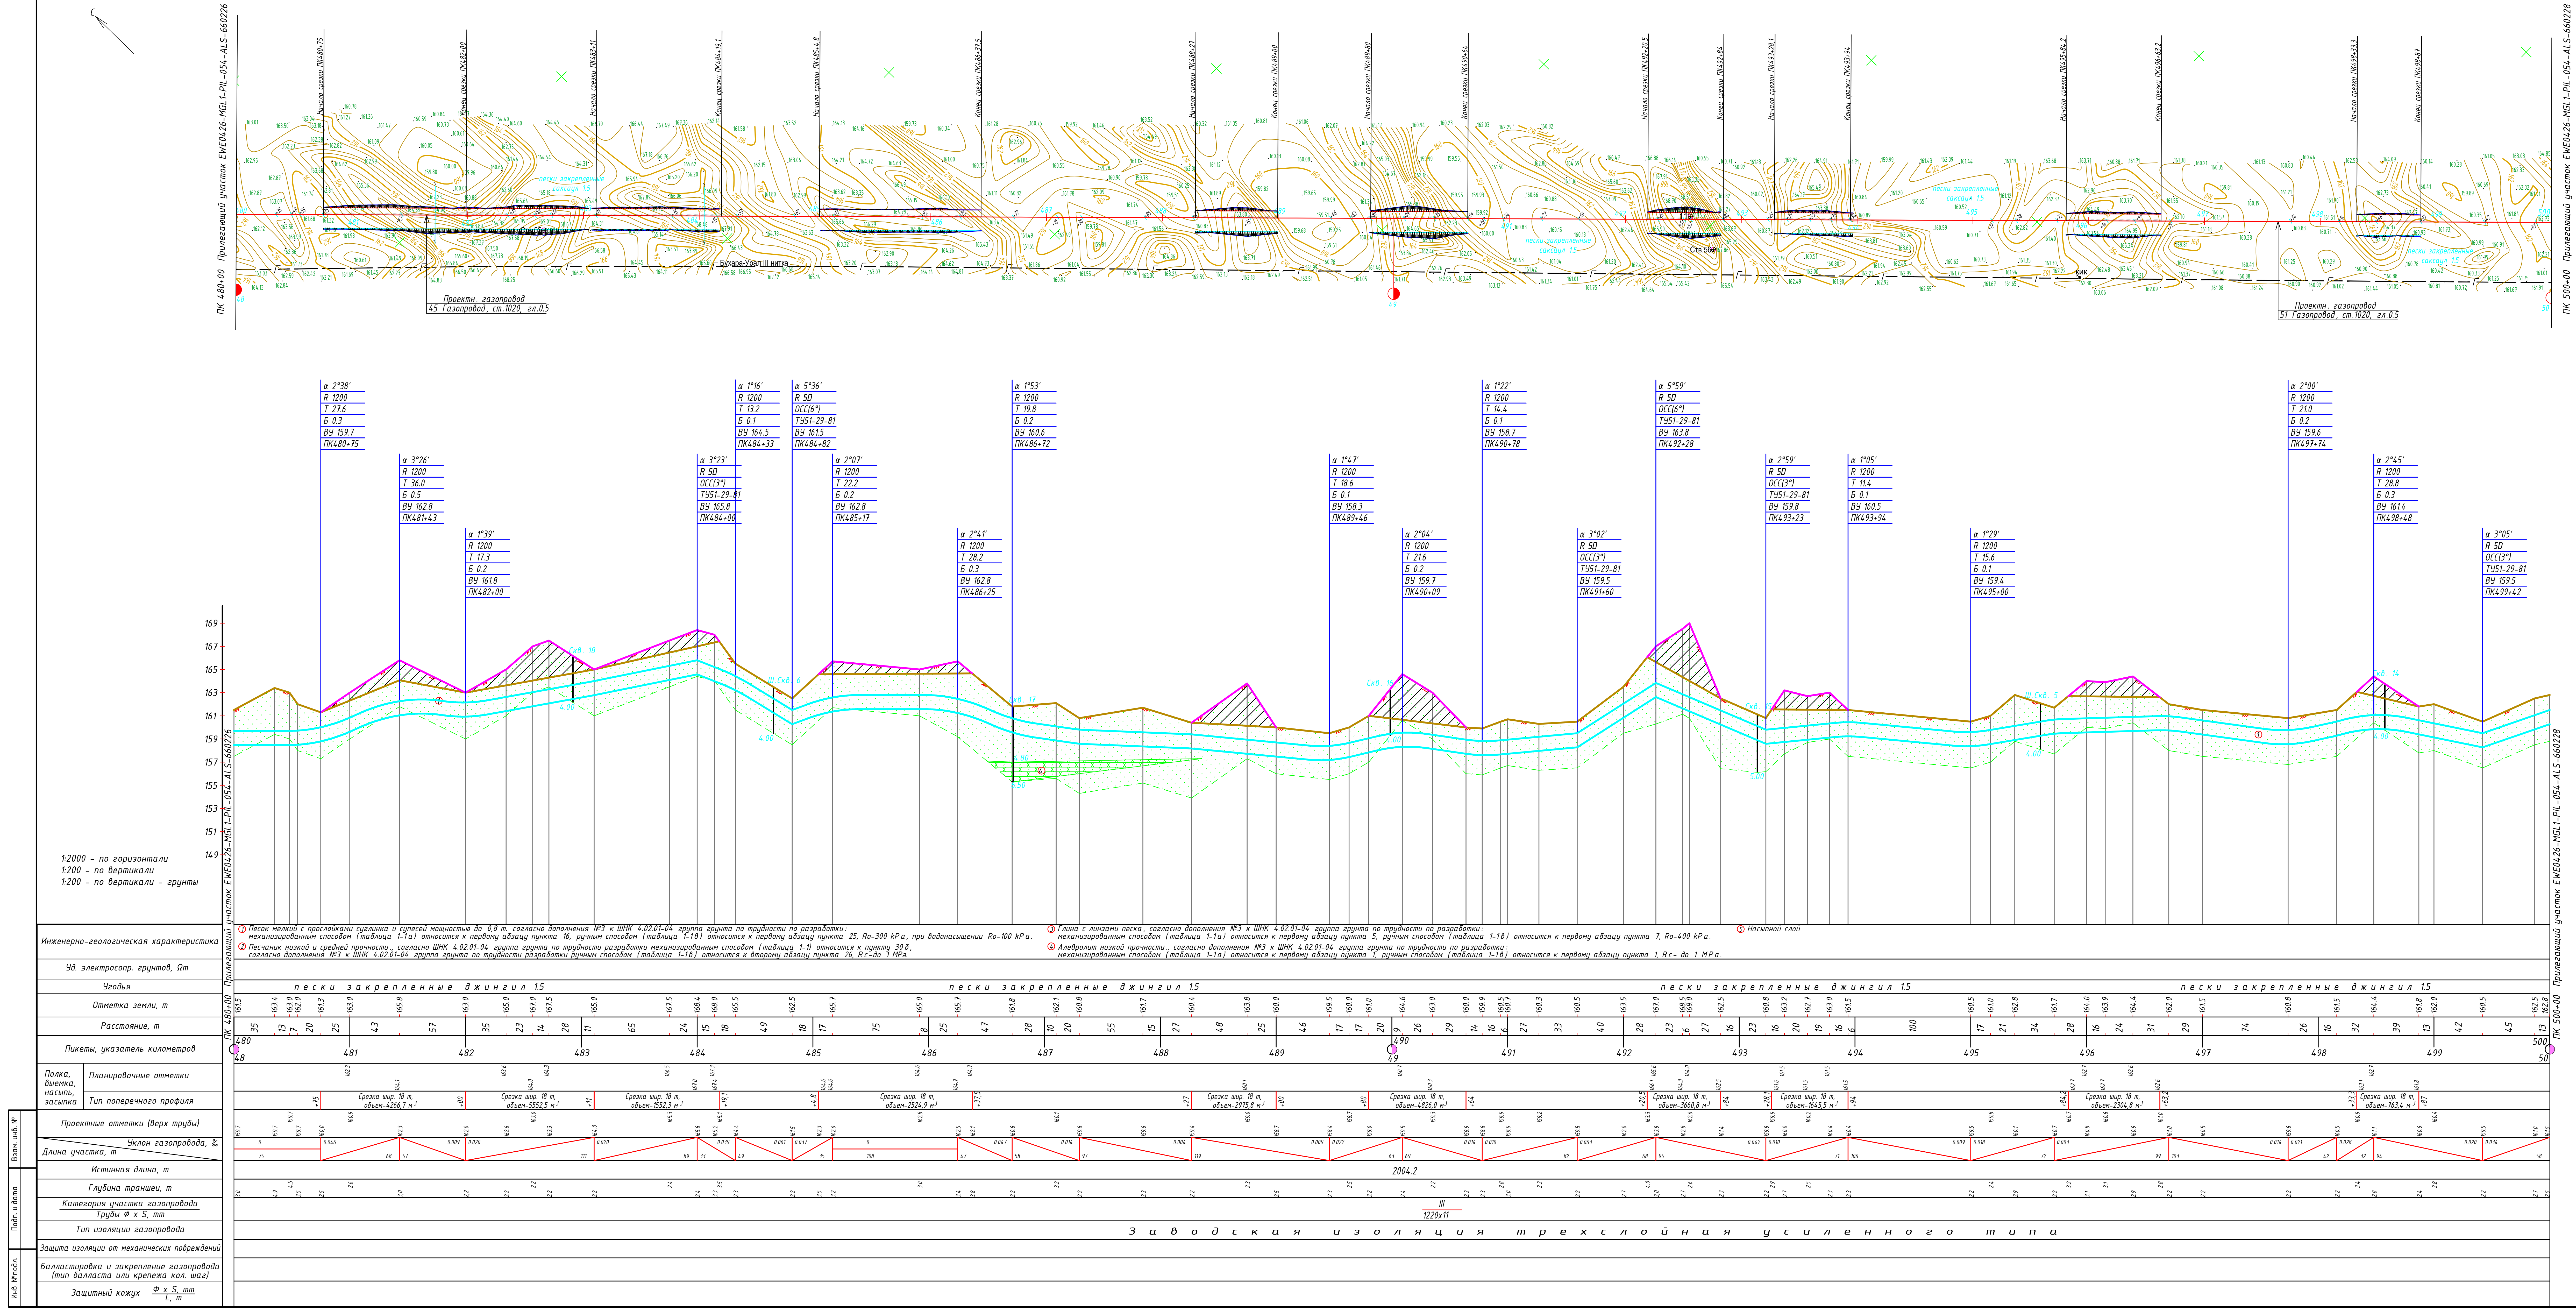
ПК 480+00 Прилегающий участок EWE0426-MGL1-PIL-054-ALS-660226
ПК 500+00 Прилегающий участок EWE0426-MGL1-PIL-054-ALS-660228
480
481
482
483
484
485
486
487
488
489
490
491
492
493
494
495
496
497
498
499
500
п е с к и з а к р е п л е н н ы е д ж и н г и л 1.5
Срезка шир. 18 m, объем-4266,7 м³
Срезка шир. 18 m, объем-5552,5 м³
Срезка шир. 18 m, объем-1552,3 м³
Срезка шир. 18 m, объем-2975,8 м³
Срезка шир. 18 m, объем-4826,0 м³
Срезка шир. 18 m, объем-3660,8 м³
Срезка шир. 18 m, объем-1645,5 м³
2004.2
III
1220x11
З а в о д с к а я и з о л я ц и я т р е х с л о й н а я у с и л е н н о г о т и п а

1:2000 – по горизонтали
1:200 – по вертикали
1:200 – по вертикали – грунты

Инженерно-геологическая характеристика

① Песок мелкий с прослойками суглинка и супесей мощностью до 0,8 m. согласно дополнения №3 к ШНК 4.02.01-04 группа грунта по трудности по разработки: механизированным способом (таблица 1-1а) относится к первому абзацу пункта 16, ручным способом (таблица 1-1в) относится к первому абзацу пункта 25, Ro-300 kPa, при водонасыщении Ro-100 kPa.

② Песчаник низкой и средней прочности., согласно ШНК 4.02.01-04 группа грунта по трудности разработки механизированным способом (таблица 1-1) относится к пункту 30 б, согласно дополнения №3 к ШНК 4.02.01-04 группа грунта по трудности разработки ручным способом (таблица 1-1в) относится к второму абзацу пункта 26, Rc-до 1 MPa.

③ Глина с линзами песка, согласно дополнения №3 к ШНК 4.02.01-04 группа грунта по трудности по разработки: механизированным способом (таблица 1-1а) относится к первому абзацу пункта 5, ручным способом (таблица 1-1в) относится к первому абзацу пункта 7, Ro-400 kPa.

④ Алевролит низкой прочности.. согласно дополнения №3 к ШНК 4.02.01-04 группа грунта по трудности по разработки: механизированным способом (таблица 1-1а) относится к первому абзацу пункта 1, ручным способом (таблица 1-1в) относится к первому абзацу пункта 1, Rc- до 1 MPa.

⑤ Насыпной слой

Уд. электросопр. грунтов, Ωm
Угодья
Отметка земли, m
Расстояние, m
Пикеты, указатель километров
Полка, выемка, насыпь, засыпка: Планировочные отметки; Тип поперечного профиля
Проектные отметки (верх трубы)
Уклон газопровода, ‰ / Длина участка, m
Истинная длина, m
Глубина траншеи, m
Категория участка газопровода / Трубы Ø x S, mm
Тип изоляции газопровода
Защита изоляции от механических повреждений
Балластировка и закрепление газопровода (тип балласта или крепежа кол. шаг)
Защитный кожух $\frac{Ф \times S,\ mm}{L,\ m}$

Взам. инв. №
Подп. и дата
Инв. №подл.

Схема расположения листов

MGL1-PIL-054-ALS-660226	MGL1-PIL-054-ALS-660227	MGL1-PIL-054-ALS-660228

Экспликация деталей и отдельных изделий

№ п. п.	Наименование деталей	Ед изм.	Кол.	Примечание
1	ОСС6°-5Д-1220 (12К60)-5,5-075-У ТУ51-29-81	шт	2	
2	ОСС3°-5Д-1220 (12К60)-5,5-075-У ТУ51-29-81	шт	4	

1 Общие данные – чертеж EWE0426-MGL1-PIL-054-COM-660201
2 Ситуационный план см. EWE0426-MGL1-PIL-054-DRW-660202
3 До начала работ руководитель строительной организации должен разработать и согласовать схему и инструкцию по безопасному производству работ в охранной зоне газопровода и его сооружений.
4 Производство работ на данном участке вести в строгом соответствии с "Инструкцией по производству строительных работ в охранных зонах магистральных трубопроводов Мингазпрома" ВСН 51-1-80.
5 Ширину полосы отвода земель для строительства газопровода см. типовой чертеж EWE0426-MGL1-PIL-000-DRW-810201.
6 Охранную зону магистрального газопровода см. типовой чертеж EWE0426-MGL1-PIL-000-DRW-810202.
7 Поперечный разрез траншеи см. типовой чертеж EWE0426-MGL1-PIL-000-DRW-810203.

Рев.	Дата	Назначение ревизии	Проверил	Утвердил
A2	18.08.2026	Выпущено для строительства		
A1	16.07.2026	Выпущено для строительства		
R2	30.06.2026	Выпущено для рассмотрения		
R1	05.06.2026	Выпущено для рассмотрения		

ЗАКАЗЧИК: UTG UZTRANSGAZ
ГЕНЕРАЛЬНЫЙ ПОДРЯДЧИК: UET UZBEKENERGOTAMIR
ПОДРЯДЧИК: PBG Pro Build Generation
ГЕНЕРАЛЬНЫЙ ПРОЕКТИРОВЩИК: EAST WEST ENGINEERING

EWE0426-MGL1-PIL-054-ALS-660227-A2

«СТРОИТЕЛЬСТВО НОВЫХ НИТОК (УЧАСТКОВ) ГАЗОПРОВОДОВ «ГАЗЛИ – САРИМОЙ» И «АКЧАЛОК – ГАЗЛИ – НУКУС» ОБЩЕЙ ПРОТЯЖЕННОСТЬЮ НЕ МЕНЕЕ 275 КМ».

ГАЗОПРОВОД «ГАЗЛИ-САРИМОЙ» (54 КМ)

План и продольный профиль газопровода ПК 480+00– ПК 500+00

Изм.	Кол.уч.	Лист	№док.	Подпись	Дата
ГИП		Схабицкий А.			08.2026
Провер.		Шафиева О.			08.2026
Исполн.		Асхатов А.			08.2026
Н.контр		Схабицкий А.			08.2026

Стадия	Лист	Листов
РД	1	1

ООО "EAST-WEST Engineering"
г. Ташкент 2026г.

Формат A2x4