1 Сроки работ по строительству газопровода под автодорой согласовать с организацией, эксплуатирующей эту автодорогу и известить ее о начале и окончании работ на переходе.

2 На период эксплуатации в месте пересечения газопровода с дорогой установить предупреждающие и запрещающие знаки по ВТ. МГ-86.

3 Место производства работ при строительстве перехода под автодорогой оградить и установить предупреждающие и запрещающие знаки, освещаемые в ночное время.

4 Строительство газопровода под автодорогой вести открытым способом с устройством объездной дороги, которую после окончания строительства ликвидировать, гравийное покрытие восстановить.

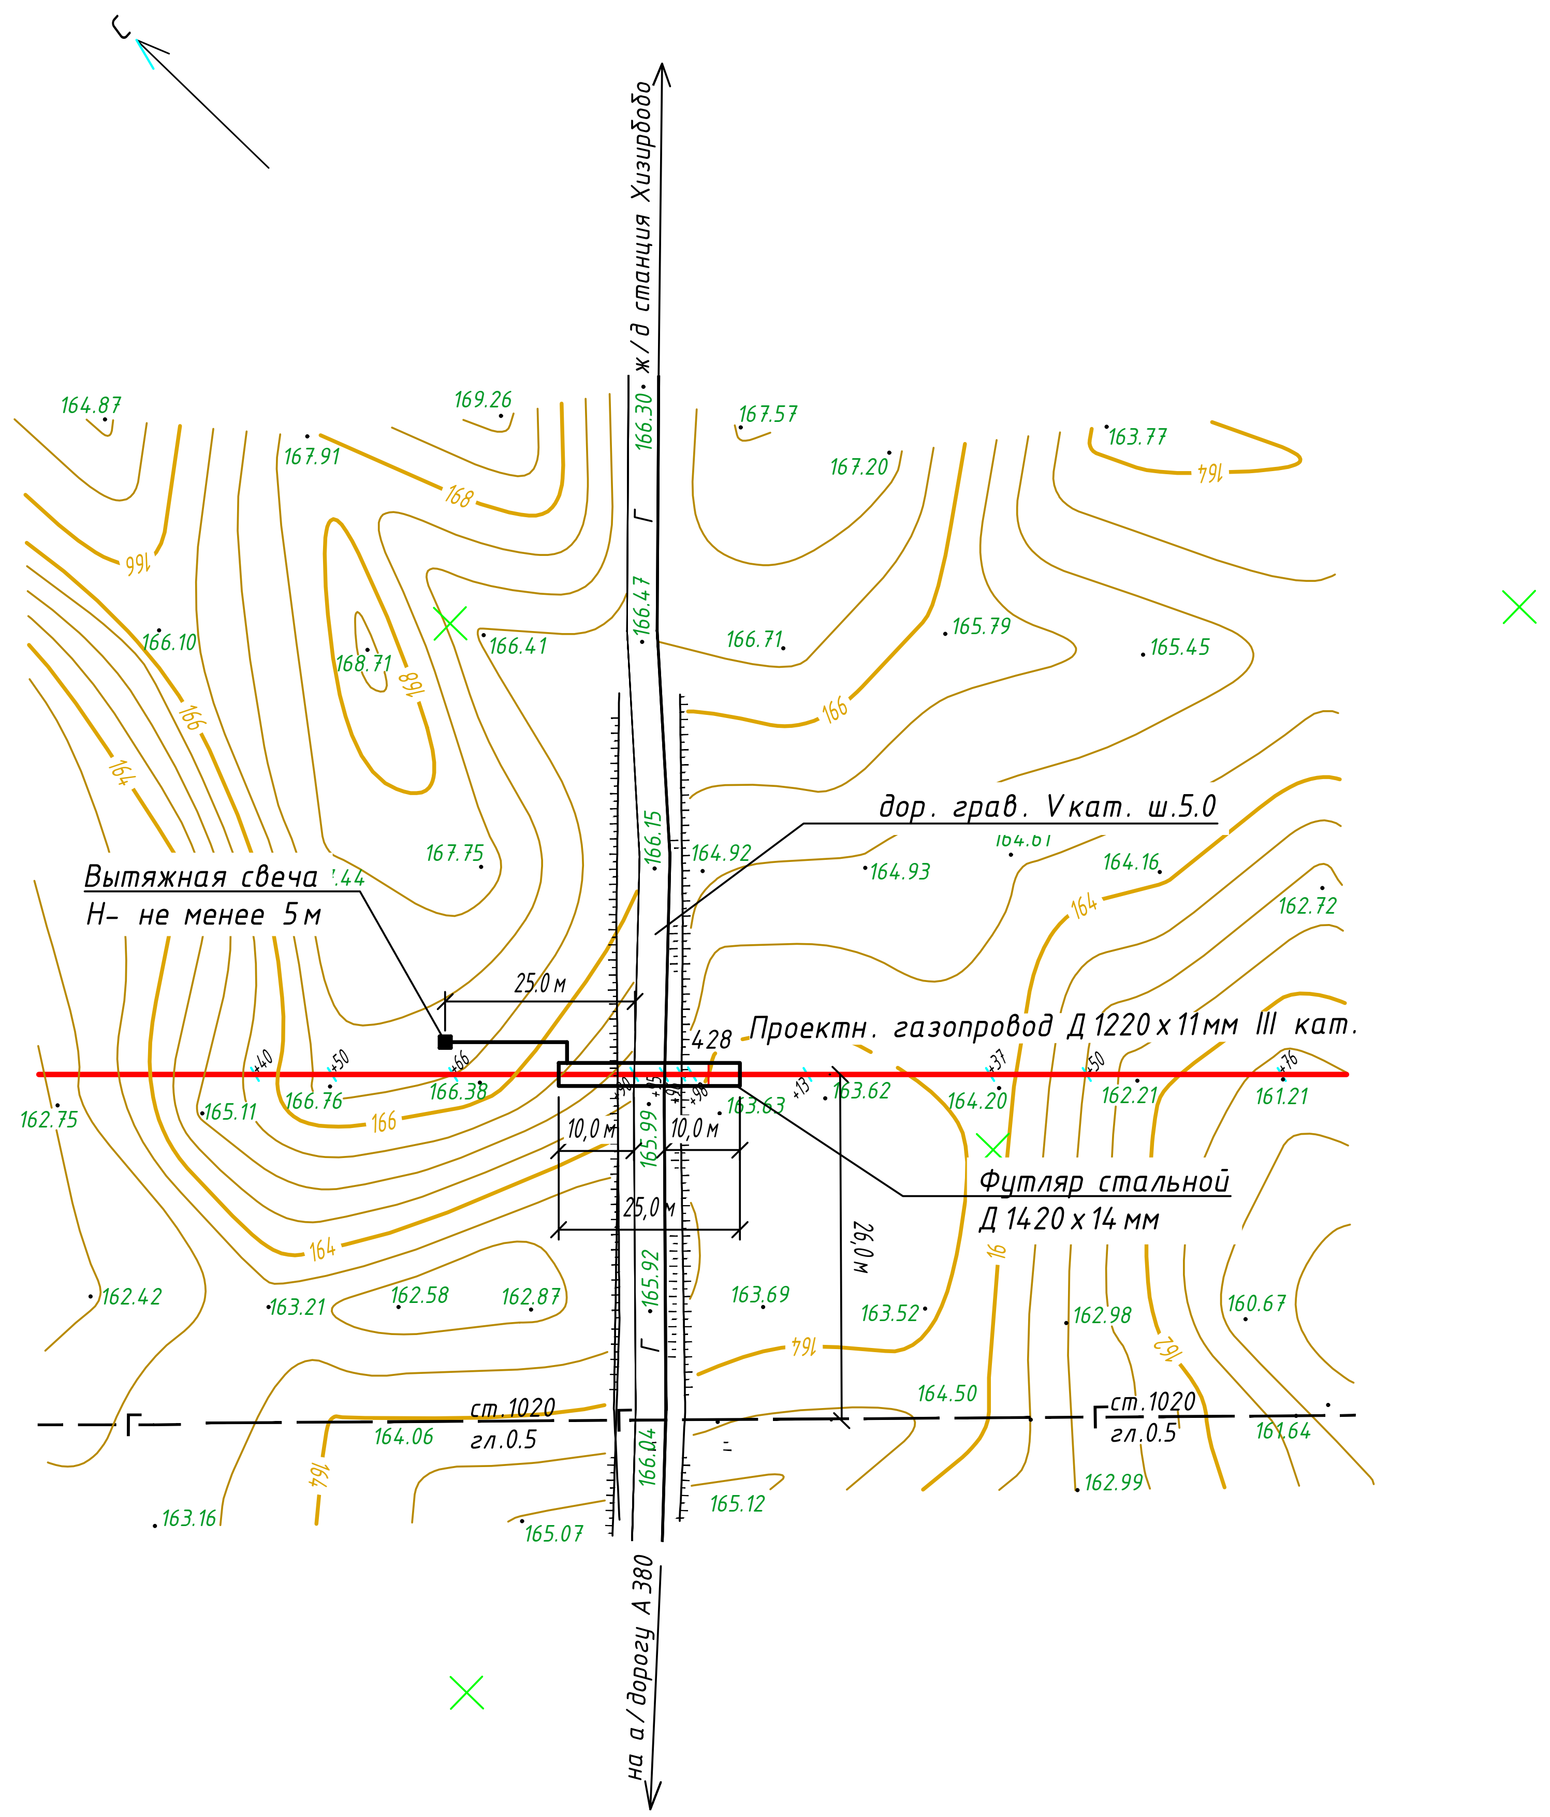

1:1000 – по горизонтали
1:200 – по вертикали
1:200 – по вертикали – грунты

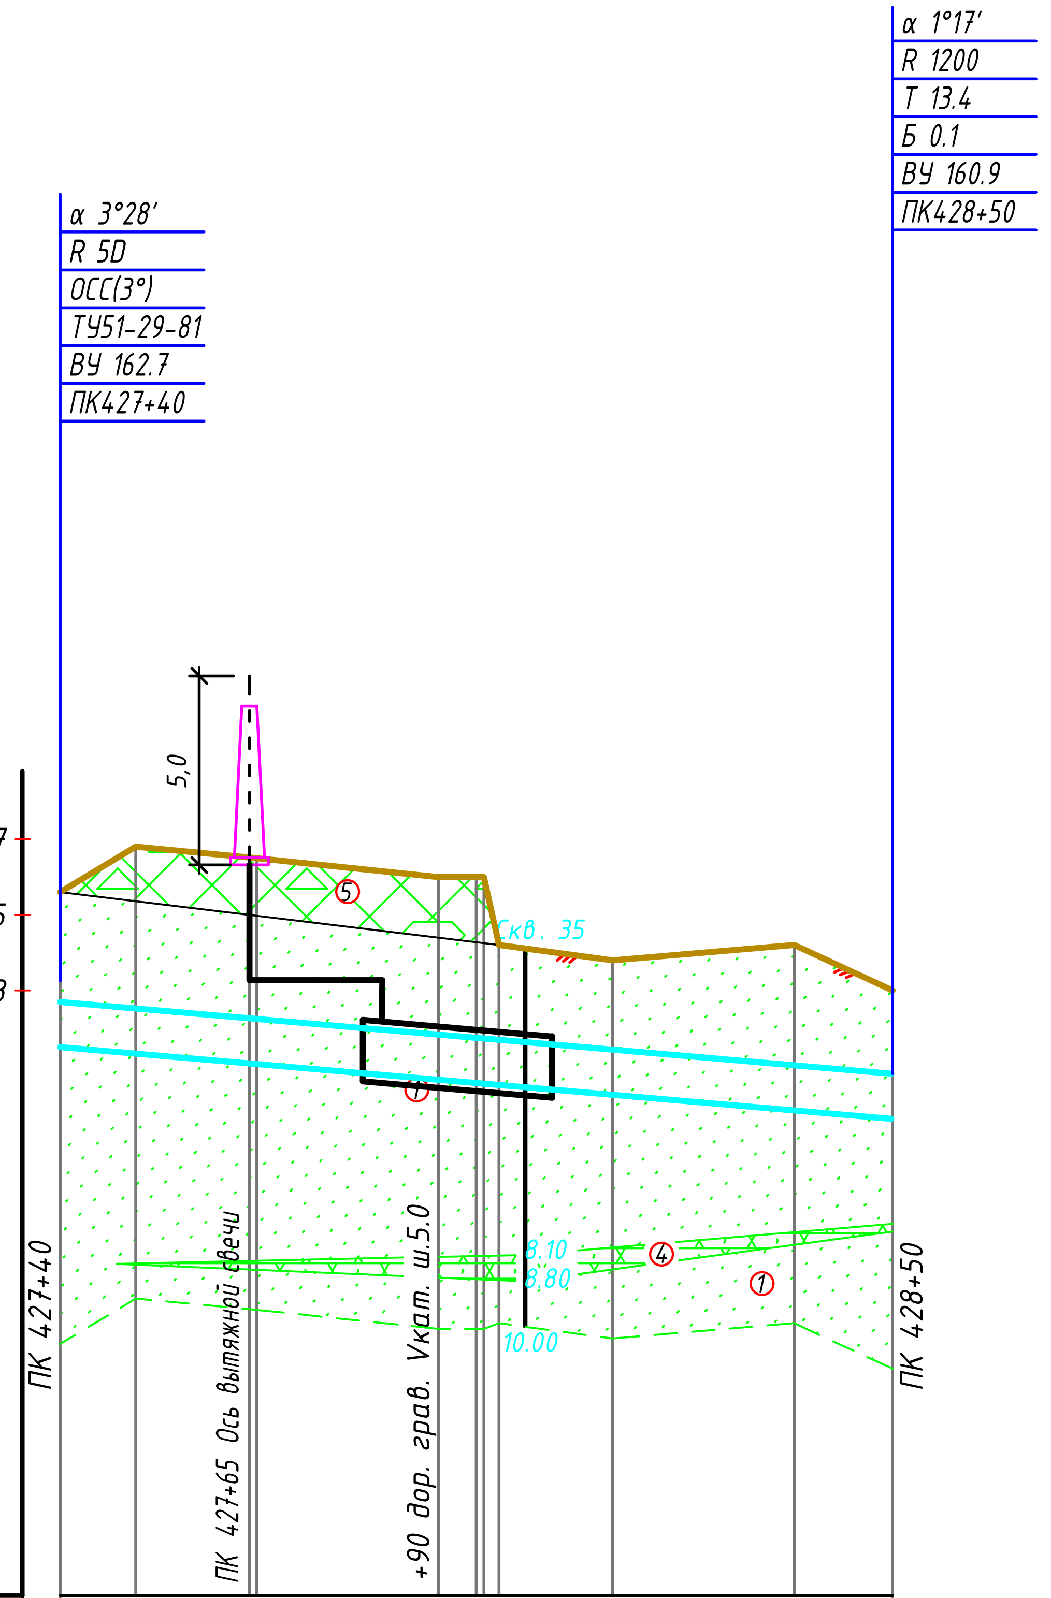

Инженерно-геологическая характеристика	
Уд. электросопр. грунтов, Ωm	
Угодья	пески закрепленные; +90; Н. з.; +98; пески закрепленные
Отметка земли, m	165.6; 166.8; 166.5; (166.2); 166.0; 166.0; 166.0; 164.2; (164.0); 163.8; 164.2; 163.0
Расстояние, m	10; 16; 24; 5; 1; 2; 2; 13; 24; 13
Пикеты, указатель километров	+80; 428; +05
Полка, выемка, насыпь, засыпка — Планировочные отметки	
Полка, выемка, насыпь, засыпка — Тип поперечного профиля	
Проектные отметки (верх трубы)	162.7; 162.6; 162.3; 162.0; 162.1; 161.9; 161.9; 161.8; 161.8; 161.7; 161.6; 161.4; 161.0; 160.8
Уклон газопровода, ‰ / Длина участка, m	0.017 / 110
Истинная длина, m	110
Глубина траншеи, m	4.1; 5.4; 5.4; 5.4; 5.5; 5.5; 5.5; 5.6; 3.8; 3.7; 3.6; 3.6; 4.4; 3.4
Категория участка газопровода / Трубы Ф х S, mm	III / 1220х11
Тип изоляции газопровода	Заводская изоляция трехслойная усиленного типа
Защита изоляции от механических повреждений	
Балластировка и закрепление газопровода (тип балласта или крепежа кол. шаг)	+80; Опорно-направляющие кольца, шаг 6м; +05
Защитный кожух Ф х S, mm / L, m	+80; 1420х14 / 25; +05

① Песок мелкий с прослойками суглинка и супесей мощностью до 0,8 m.
согласно дополнения №3 к ШНК 4.02.01-04
группа грунта по трудности по разработки:
механизированным способом (таблица 1-1а)
относится к первому абзацу пункта 16,
ручным способом (таблица 1-1в)
относится к первому абзацу пункта 25, Ro-300 kPa,
при водонасыщении Ro-100 kPa.

④ Алевролит низкой прочности.
согласно дополнения №3 к ШНК 4.02.01-04
группа грунта по трудности по разработки:
механизированнёым способом (таблица 1-1а) относится к первому абзацу пункта 1,
ручным способом (таблица 1-1в) относится к первому абзацу пункта 1, Rc- до 1 MPa.

⑤ Насыпной слой

Экспликация деталей и отдельных изделий

№ п. п.	Наименование деталей	Ед изм.	Кол.	Примечание
1	ОСС3°-5Д-1220 (12К60)-5,5-075-У ТУ51-29-81	шт	1	учтено в ALS-660224

Рев.	Дата	Назначение ревизии	Проверил	Утвердил
A2	18.08.2026	Выпущено для строительства		
A1	18.07.2026	Выпущено для строительства		
R1	07.07.2026	Выпущено для рассмотрения		

ЗАКАЗЧИК: UTG UZTRANSGAZ
ГЕНЕРАЛЬНЫЙ ПОДРЯДЧИК: UET UZBEKENERGOTAMIR
ПОДРЯДЧИК: PBG Pro Build Generation
ГЕНЕРАЛЬНЫЙ ПРОЕКТИРОВЩИК: EAST WEST ENGINEERING

EWE0426-MGL1-PIL-054-CRO-660301-A2

«СТРОИТЕЛЬСТВО НОВЫХ НИТОК (УЧАСТКОВ) ГАЗОПРОВОДОВ «ГАЗЛИ – САРИМОЙ» И «АКЧАЛОК – ГАЗЛИ – НУКУС» ОБЩЕЙ ПРОТЯЖЕННОСТЬЮ НЕ МЕНЕЕ 275 КМ».

Изм.	Кол.уч.	Лист	№док.	Подпись	Дата
ГИП		Схабицкий А.			08.2026
Провер.		Шафиева О.			08.2026
Исполн.		Асхатов А.			08.2026
Н.контр		Схабицкий А.			08.2026

ГАЗОПРОВОД «ГАЗЛИ-САРИМОЙ» (54 КМ)

Стадия	Лист	Листов
РД	1	1

План-профиль перехода через автодорогу V категории ПК 427+40- ПК 428+50

EAST WEST ENGINEERING
ООО "EAST-WEST Engineering"
г. Ташкент 2026г.

Формат А3х3

Взам. инв. №
Подп. и дата
Инв. № подл.