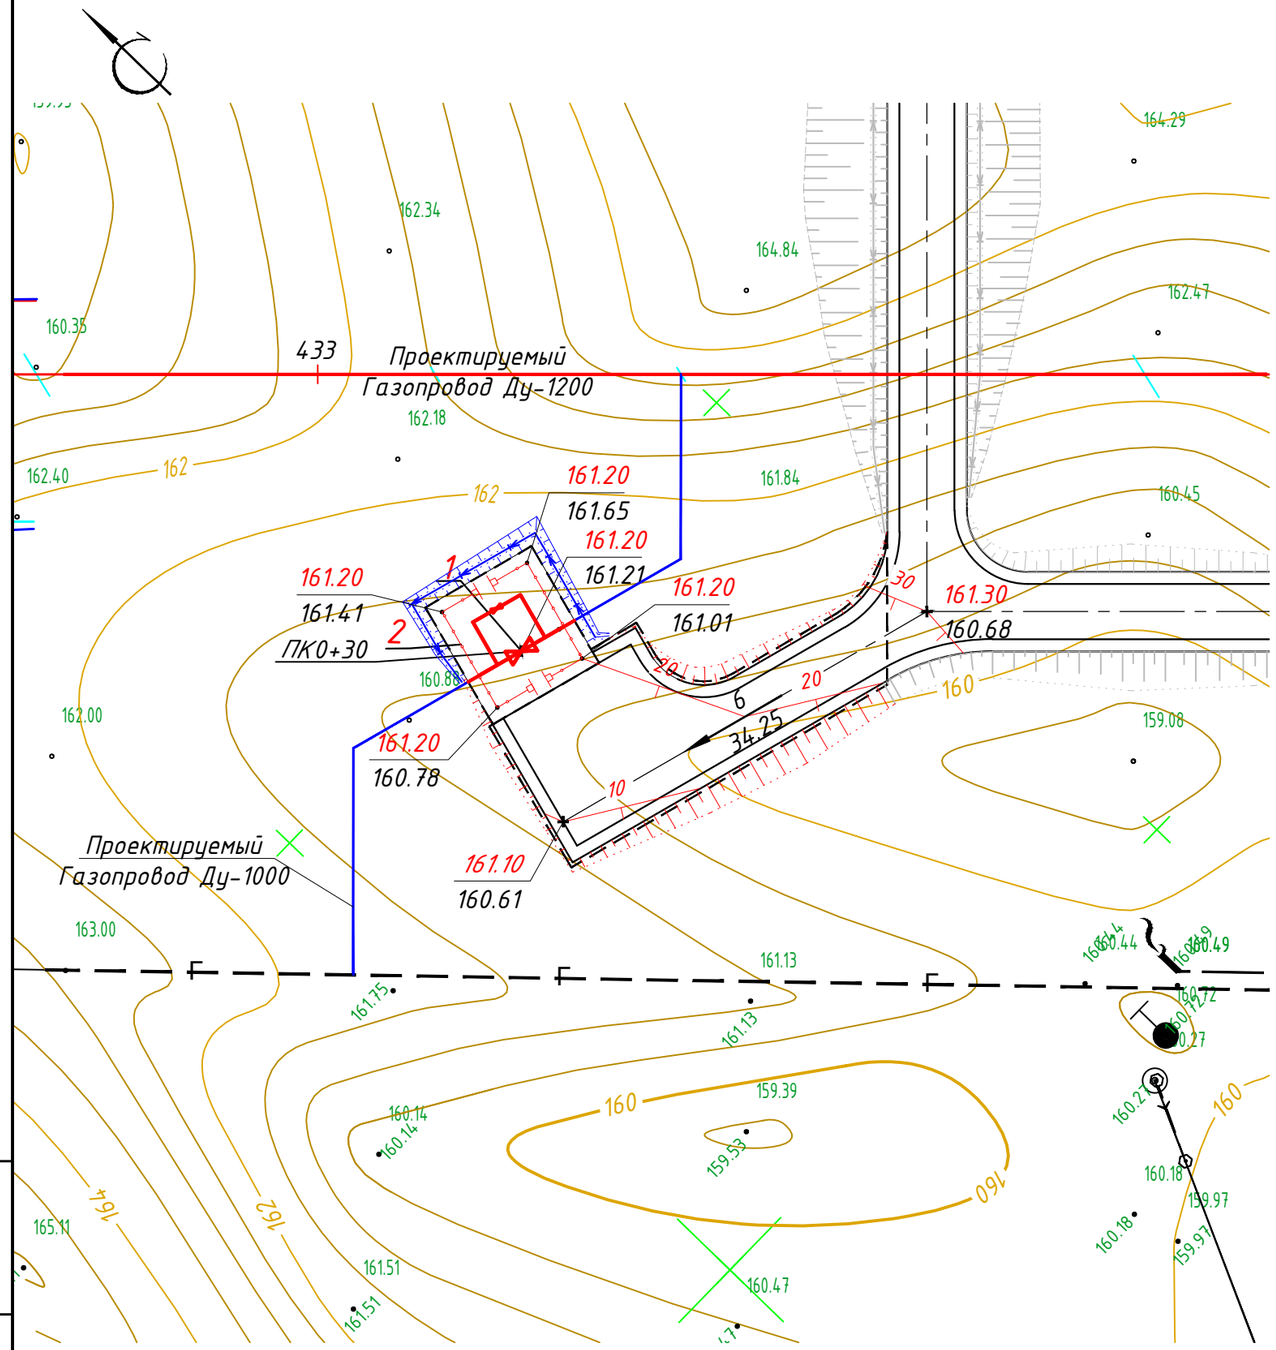


Экспликация зданий и сооружений

Номер на плане	Наименование	Примечание
1	Крановый узел Ду 1000	
2	Ограждение сетчатое	

Условные обозначения

- Ограждение
- Калитка
- Граница планировки
- Существующий газопровод
- Проектируемый газопровод ДУ-1200
- Проектируемый газопровод ДУ-1000
- 161.20 / 161.21 — Проектная отметка / Существующая отметка
- 10 — Проектные красные горизонтали
- Откосы насыпи
- Откосы выемки
- Водоотводная канава

Рев.	Дата	Назначение ревизии	Проверил	Утвердил
A2	06.10.2026	Выпущено для строительства		
A1	28.08.2026	Выпущено для строительства		
R1	24.07.2026	Выпущено для рассмотрения		

ЗАКАЗЧИК: UTG UZBEKNEFTEGAZ HOLDING COMPANY

ГЕНЕРАЛЬНЫЙ ПОДРЯДЧИК: UET UZBEKENERGOTAMIR

ПОДРЯДЧИК: PBG Pro Build Generation

ГЕНЕРАЛЬНЫЙ ПРОЕКТИРОВЩИК: EAST WEST ENGINEERING

Примечания:

При составлении настоящего чертежа были использованы :

1. Материалы топографо-геодезической съемки, предоставлены АО "O'ZLITINEFTGAZ".
2. Система координат местная. Высотные отметки даны в Балтийской системе.
3. Размеры даны в метрах.
4. Площадка кранового узла КУП-D9 привязана линейно к пикету ПК 0+30.
5. Данный лист смотри совместно с листами разделов PIL, PRE, ELE, STR, SYS.
6. Детальный план кранового узла см. EWE0426-MGL1-PRE-054-DRW-780203.

Изм.	Кол.уч.	Лист	№док.	Подпись	Дата
ГИП		Кирпичников С.			10.2026
Нач.отд.		Нигманова Н.			10.2026
Исполн.		Горлова О.			10.2026
Н.контр		Кирпичников С.			10.2026

EWE0426-MGL1-GLT-054-DRW-780103-A2

«СТРОИТЕЛЬСТВО НОВЫХ НИТОК (УЧАСТКОВ) ГАЗОПРОВОДОВ «ГАЗЛИ - САРИМОЙ» И «АКЧАЛОК - ГАЗЛИ - НУКУС» ОБЩЕЙ ПРОТЯЖЕННОСТЬЮ НЕ МЕНЕЕ 275 км».

ГАЗОПРОВОД «ГАЗЛИ-САРИМОЙ» (54 км)

Генеральный план и транспорт.

Стадия	Лист	Листов
РД	1	1

КУП-D9.
План организации рельефа
М 1:500

ООО "EAST-WEST Engineering"
г. Ташкент 2026г.

Взам. инв.№ | Подпись и дата | Инв. № подл

Формат / Format A3