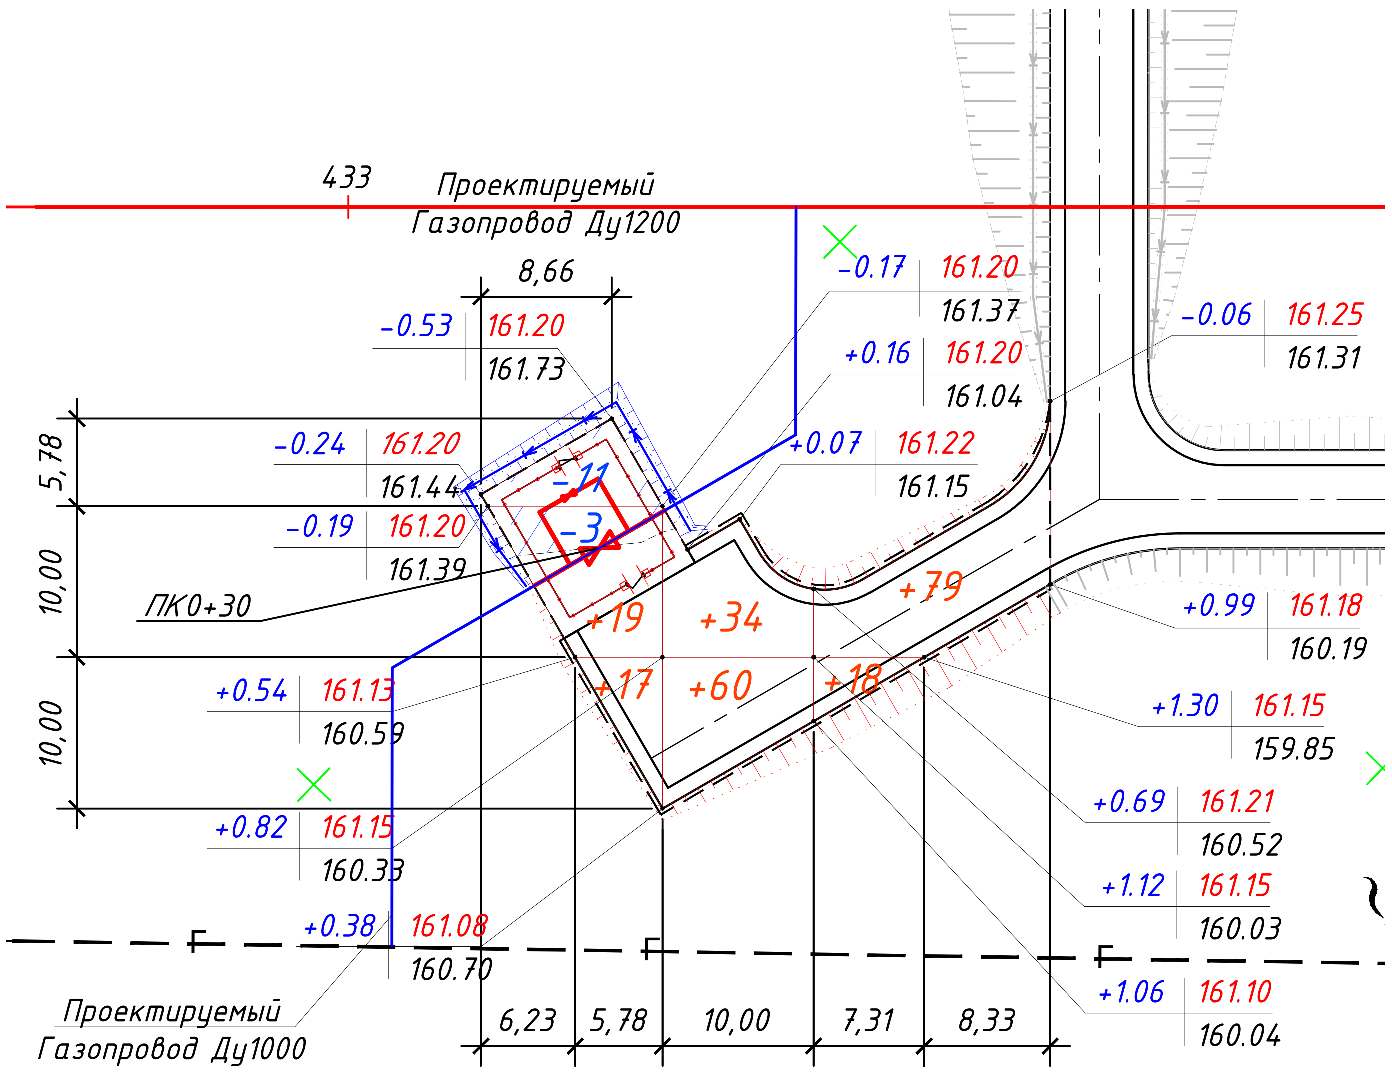

Итого,м3						Всего,м3	
	Насыпь (+)	+36	+94	+68	+29		+227
	Выемка (-)	-14	--	--	--		-14

Условные обозначения

+60 объем насыпи в $м^3$

+0.38 | 161.08 / 160.70 — рабочая отм. | проектная отм. / отм.сущ.рельефа

Примечания:

При составлении настоящего чертежа были использованы :

1. Сетка картограммы привязана линейно к пикету ПК0+30.
2. Сетка квадратов объёмы земляных масс разбита на ячейки размерами 10х10м.
3. Производство земляных работ вести в соответствии с требованиями ҚР 02.01.

Ведомость объемов земляных масс

Наименование грунта	Количество, $м^3$		Примечание
	Насыпь (+)	Выемка (-)	
1. Грунт планировки территории	227	14	
2. Вытесненный грунт, в т.ч. при устройстве:			
а) автодорожных покрытий		93	
б) покрытий площадок		9.5	
в) водоотводной канавы		12	
г) плодородной почвы на участках насыпи			
д) плодородной почвы на участках выемки			
3. Замена растительного грунта на участках насыпи			
4. Грунт для устройства откосов насыпи	18		
5. Грунт для устройства откосов выемки			
6. Поправка на уплотнение	24.5		
Всего пригодного грунта	269.5	128.5	
5. Недостаток пригодного грунта		141**	
8. Плодородный грунт, всего в т.ч.:		126	
а) Используемый для озеленения территории			
б) Избыток плодородного грунта	126		
(рекультивация земель)			
9. Итого перерабатываемого грунта	395.5	395.5	

* С учетом плодородного грунта.

** В карьере.

Общая площадь картограммы = 420 м2

Рев.	Дата	Назначение ревизии	Проверил	Утвердил
A1	28.08.2026	Выпущено для строительства		
R1	24.07.2026	Выпущено для рассмотрения		

ЗАКАЗЧИК: UTG UZTRANSGAZ
ГЕНЕРАЛЬНЫЙ ПОДРЯДЧИК: UET UZBEKENERGOTAMIR
ПОДРЯДЧИК: PBG Pro Build Generation
ГЕНЕРАЛЬНЫЙ ПРОЕКТИРОВЩИК: EAST WEST ENGINEERING

EWE0426-MGL1-GLT-054-DRW-780104-A1

«СТРОИТЕЛЬСТВО НОВЫХ НИТОК (УЧАСТКОВ) ГАЗОПРОВОДОВ «ГАЗЛИ - САРИМОЙ» И «АКЧАЛОК - ГАЗЛИ - НУКУС» ОБЩЕЙ ПРОТЯЖЕННОСТЬЮ НЕ МЕНЕЕ 275 км».

Изм.	Кол.уч.	Лист	№ док.	Подпись	Дата
ГИП		Схабицкий А.			08.2026
Нач.отд.		Нигманова Н.			08.2026
Исполн.		Горлова О.			08.2026
Н.контр		Схабицкий А.			08.2026

ГАЗОПРОВОД «ГАЗЛИ-САРИМОЙ» (54 км)
Генеральный план и транспорт.

Стадия	Лист	Листов
РД	1	1

КУП-D9.
План земляных масс М 1:500

EAST WEST ENGINEERING
ООО "EAST-WEST Engineering"
г. Ташкент 2026г.

Инв. № подл
Подпись и дата
Взам. инв.№

Формат / Format A3