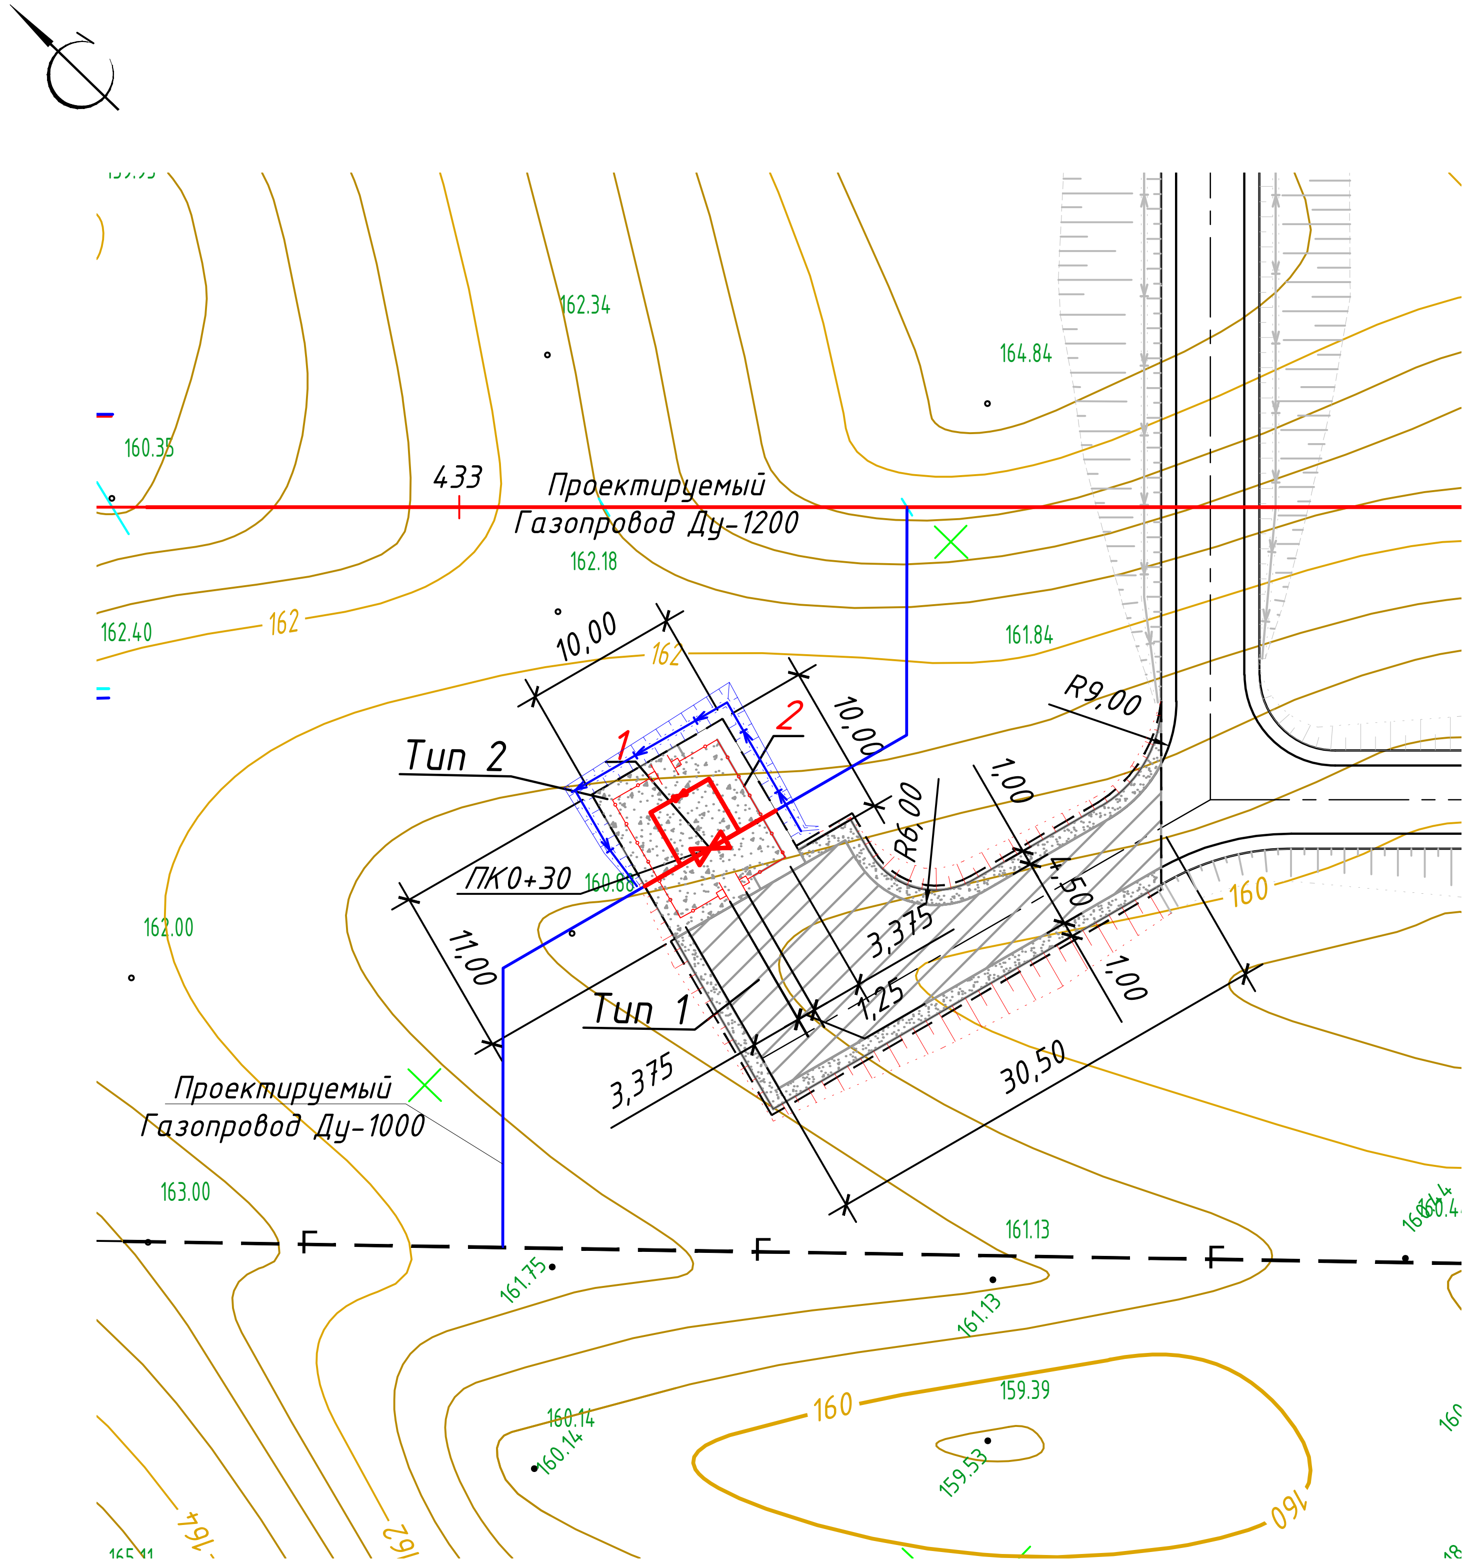
433
Проектируемый
Газопровод Ду-1200
162.34
164.84
160.35
162.18
162.40
162
162
161.84
10,00
10,00
R9,00
1
2
Тип 2
ПК0+30
160.68
R6,00
1,00
4,50
160
162.00
11,00
3,375
1,25
1,00
Тип 1
3,375
30,50
Проектируемый
Газопровод Ду-1000
163.00
161.13
161.13
161.75
160.14
160.14
160
159.39
159.53
160
164
162

Тип 1

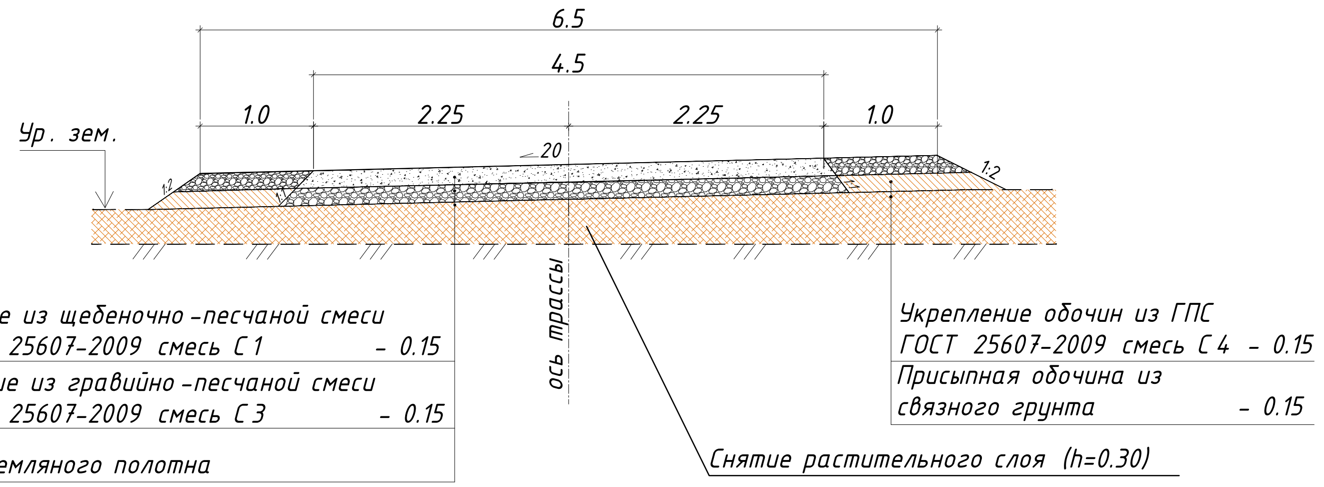
6.5
4.5
1.0
2.25
2.25
1.0
Ур. зем.
20
1:2
1:2
ось трассы
Покрытие из щебеночно-песчаной смеси
по ГОСТ 25607-2009 смесь С1 - 0.15
Основание из гравийно-песчаной смеси
по ГОСТ 25607-2009 смесь С3 - 0.15
Грунт земляного полотна
Укрепление обочин из ГПС
ГОСТ 25607-2009 смесь С4 - 0.15
Присыпная обочина из
связного грунта - 0.15
Снятие растительного слоя (h=0.30)

Тип 2

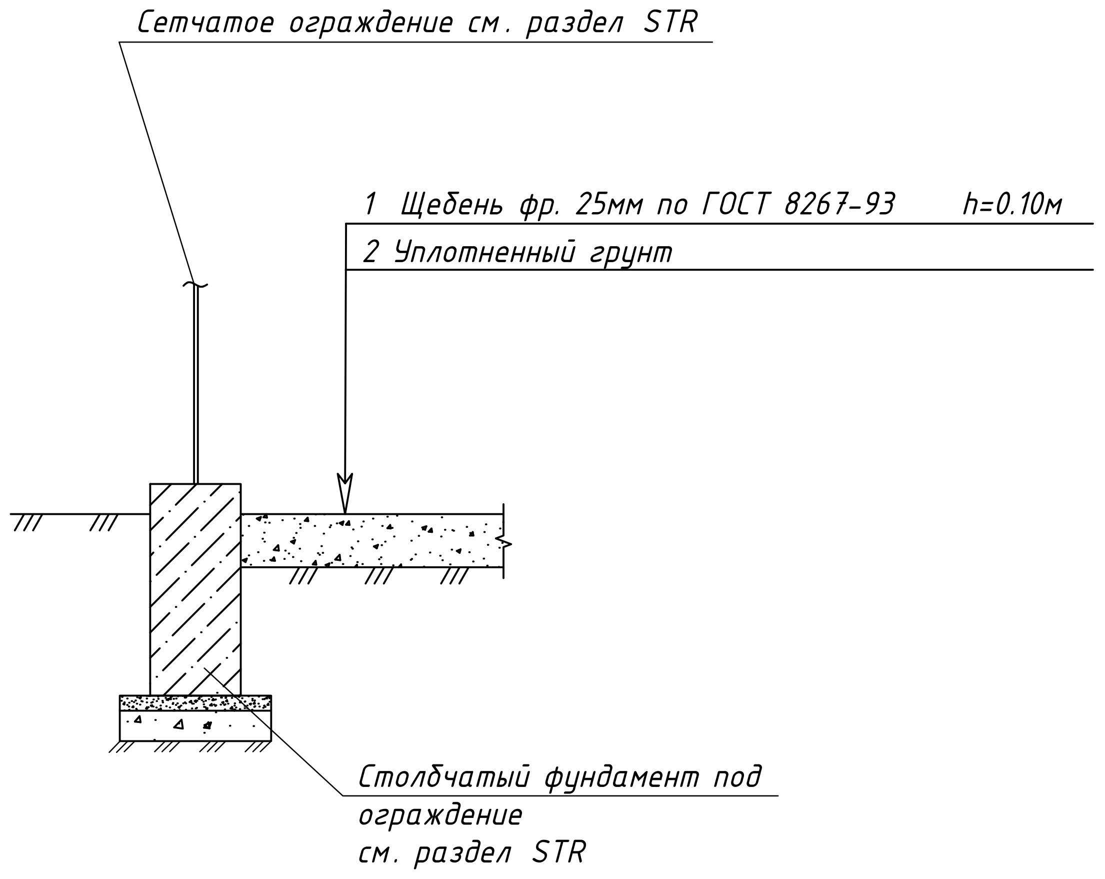
Сетчатое ограждение см. раздел STR
1 Щебень фр. 25мм по ГОСТ 8267-93 h=0.10м
2 Уплотненный грунт
Столбчатый фундамент под
ограждение
см. раздел STR

Примечания:

При составлении настоящего чертежа были использованы :

1. Материалы топографо-геодезической съемки, предоставлены АО "O'ZLITINEFTGAZ".
2. Система координат местная. Высотные отметки даны в Балтийской системе.
3. Размеры даны в метрах.
4. Площадка кранового узла КУП-D9 привязана линейно к пикету ПК 0+30.
5. Данный лист смотри совместно с листами разделов PIL, PRE, ELE, STR, SYS.
6. Детальный план кранового узла см.EWE0426-MGL1-PRE-054-DRW-780203.

Экспликация зданий и сооружений

Номер на плане	Наименование	Примечание
1	Крановый узел Ду 1000	
2	Ограждение сетчатое	

Ведомость тротуаров, дорожек и площадок

Тип	Обозначение	Наименование	Ед. изм.	Примечание
		Покрытие площадки		
1	▒	Покрытие из щебня по ГОСТ 8267-93, h=0.10	$м^2$	95
		Покрытие проездов		
2	▨	Покрытие из щебеночно-песчаной смеси по ГОСТ 25607-2009 смесь С1 h=0,15 м Основание из гравийно-песчаной смеси по ГОСТ 25607-2009 смесь С3 h=0,15 м	$м^2$	237.0
		Укрепление обочин из ГПС ГОСТ 25607-2009 смесь С4 h=0,15 м	$м^2$	72.0

Рев.	Дата	Назначение ревизии	Проверил	Утвердил
A2	06.10.2026	Выпущено для строительства		
A1	28.08.2026	Выпущено для строительства		
R1	24.07.2026	Выпущено для рассмотрения		

ЗАКАЗЧИК: UTG UZTRANSGAZ
ГЕНЕРАЛЬНЫЙ ПОДРЯДЧИК: UET UZBEKENERGOTAMIR
ПОДРЯДЧИК: PBG Pro Build Generation
ГЕНЕРАЛЬНЫЙ ПРОЕКТИРОВЩИК: EAST WEST ENGINEERING

EWE0426-MGL1-GLT-054-DRW-780106-A2

«СТРОИТЕЛЬСТВО НОВЫХ НИТОК (УЧАСТКОВ) ГАЗОПРОВОДОВ «ГАЗЛИ - САРИМОЙ» И «АКЧАЛОК - ГАЗЛИ - НУКУС» ОБЩЕЙ ПРОТЯЖЕННОСТЬЮ НЕ МЕНЕЕ 275 км».

Изм.	Кол.уч.	Лист	№ док.	Подпись	Дата
ГИП		Кирпичников С.			10.2026
Нач.отд.		Нигманова Н.			10.2026
Исполн.		Горлова О.			10.2026
Н.контр		Кирпичников С.			10.2026

ГАЗОПРОВОД «ГАЗЛИ-САРИМОЙ» (54 км)
Генеральный план и транспорт.

Стадия	Лист	Листов
РД	1	1

КУП-D9.
План благоустройства территории
М 1:500

ООО "EAST-WEST Engineering"
г. Ташкент 2026 г.

Взам. инв. №
Подпись и дата
Инв.№ подл.

Формат / Format A4x3