
N СЕВЕР

| ПЕРЕЧЕНЬ СВАРНЫХ ШВОВ | | |
|---|---|---|
| № | DN | ТИП |
| 1 | 1000 | BUTTWELD |
| 2 | 1000 | BUTTWELD |
| 3 | 1000 | BUTTWELD |
| 4 | 1000 | BUTTWELD |
| 5 | 1000 | BUTTWELD |
| 6 | 1000 | BUTTWELD |
| 7 | 1000 | INSTRUMENT |
| 8 | 300 | BUTTWELD |
| 9 | 300 | BUTTWELD |

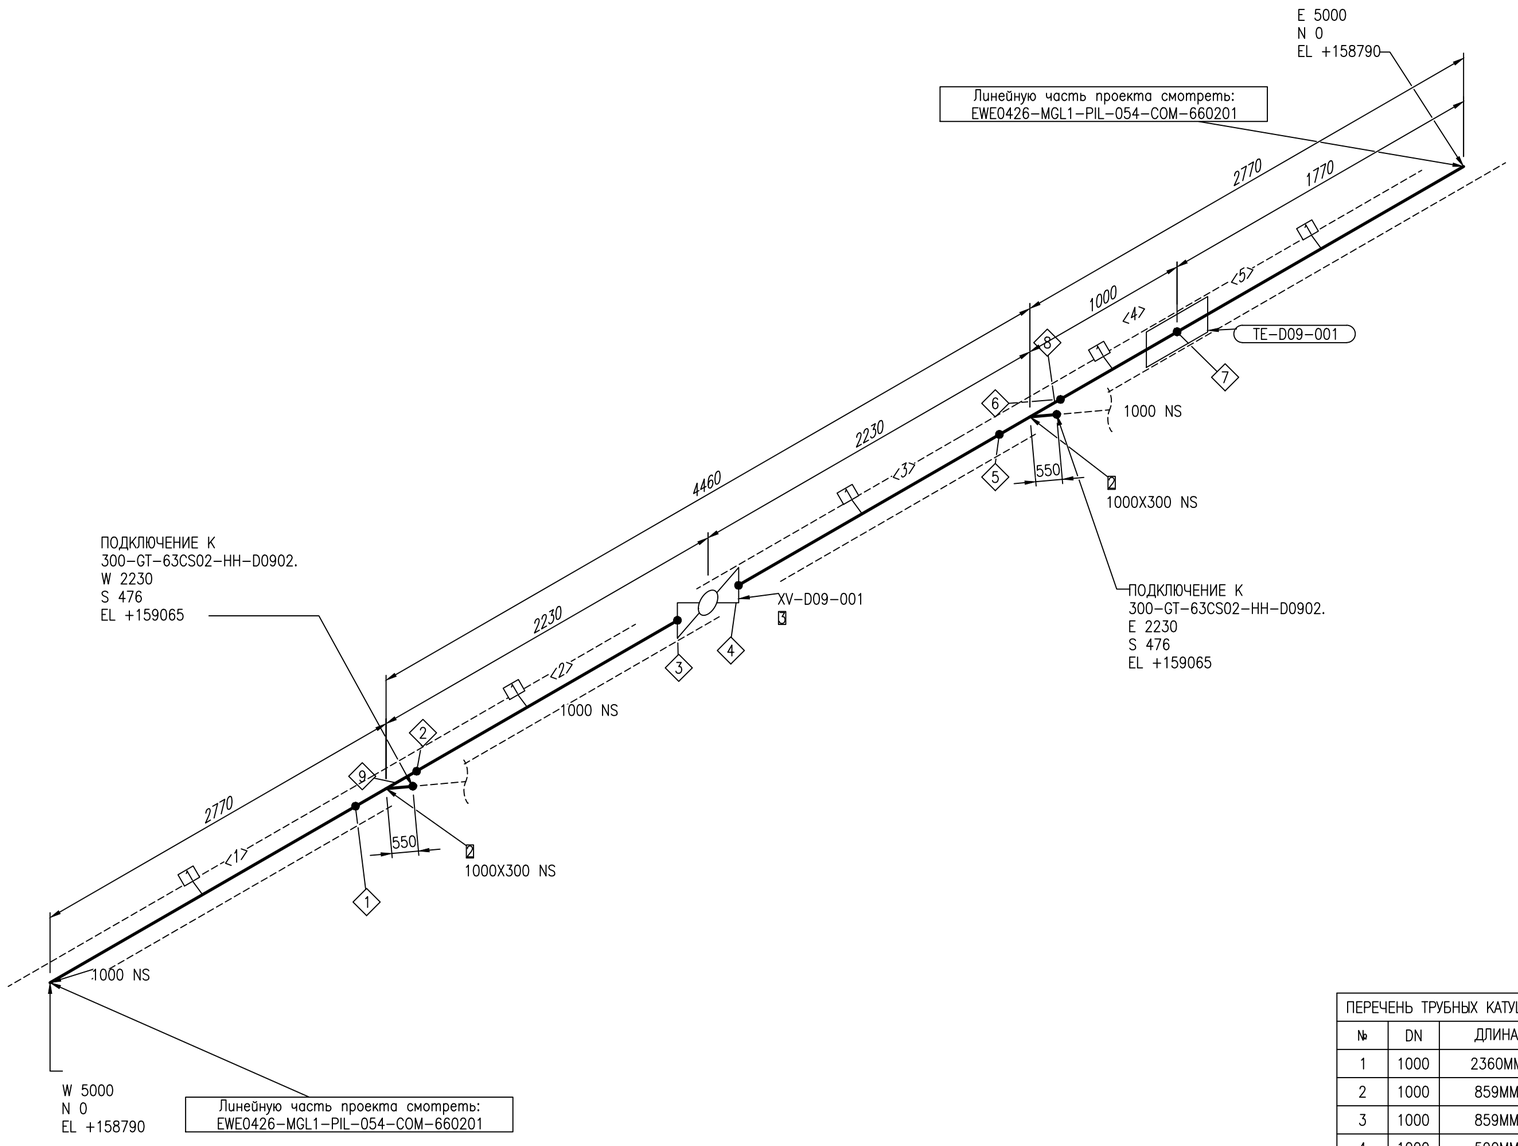


| ПЕРЕЧЕНЬ ТРУБНЫХ КАТУШЕК | | |
|---|---|---|
| № | DN | ДЛИНА |
| 1 | 1000 | 2360ММ |
| 2 | 1000 | 859ММ |
| 3 | 1000 | 859ММ |
| 4 | 1000 | 590ММ |
| 5 | 1000 | 1770ММ |

СПЕЦИФИКАЦИЯ ИЗДЕЛИЙ И МАТЕРИАЛОВ

| ПОЗ. | НАИМЕНОВАНИЕ | СТАНДАРТ | КОЛ. | ПРИМЕЧАНИЕ |
|---|---|---|---|---|
| 1 | Трубы стальные сварные прямошовные, типа 3, К60, 1020Х10 | ГОСТ 31447-2012 | 6.5М | ТРУБА УЧТЕНА В ЛИНЕЙНОЙ ЧАСТИ ПРОЕКТА |
| 2 | Тройник Т I 1020(11К60)-325(10К48)-5,5(6,9)-0,75-30, сталь К60 | ТУ 1469-017-38948552-2015 | 2 | |
| 3 | Кран шаровой DN1000 PN-6,3 МПа с пневмогидроприводом, приварной, подземный | EWE0426-MGL1-PRE-054-DSH-610124 | 1 | |

| Трубопровод | ДАННЫЕ ПО ТРУБОПРОВОДУ | | |
|---|---|---|---|
| 1000-GT-63CS00-HH-D0901 | Расчетные параметры | Температура | -26,9...+85 °C |
| | | Давление | 6,3 MPa |
| | Рабочие параметры | Температура | -20...+40 °C |
| | | Давление | 5,5 MPa |
| Ссылочные чертежи No | Параметры испытания | Тип | Гидравлическое |
| | | Давление | 6,9 MPa |
| EWE0426-MGL1-PRE-054-SCM-610111 | Изоляция | Тип | HH |
| | | Толщина | mm |
| | Катодная защита | Да или Нет | Да |

| Рев. | Дата | Назначение ревизии | Проверил | Утвердил |
|---|---|---|---|---|
| A1 | 07.09.2026 | Выпущено для рассмотрения | | |
| R1 | 22.06.2026 | Выпущено для рассмотрения | | |

ЗАКАЗЧИК: UTG UZTRANSGAZ | ГЕНЕРАЛЬНЫЙ ПОДРЯДЧИК: UET UZBEKENERGOTAMIR | ПОДРЯДЧИК: PBG Pre Build Generation | ГЕНЕРАЛЬНЫЙ ПРОЕКТИРОВЩИК: EAST WEST ENGINEERING

| Изм. | Кол.уч. | Лист | №док. | Подпись | Дата |
|---|---|---|---|---|---|
| ГИП | | Кирпичников С. | | | 09.2026 |
| Нач.отд. | | Рябинин А. | | | 09.2026 |
| Исполн. | | Таштимуров Р. | | | 09.2026 |
| Н.контр | | Кирпичников С. | | | 09.2026 |

EWE0426-MGL1-PRE-054-ISO-780602-A1

«СТРОИТЕЛЬСТВО НОВЫХ НИТОК (УЧАСТКОВ) ГАЗОПРОВОДОВ «ГАЗЛИ - САРИМОЙ» И «АКЧАЛОК - ГАЗЛИ - НУКУС» ОБЩЕЙ ПРОТЯЖЕННОСТЬЮ НЕ МЕНЕЕ 275 КМ».

ГАЗОПРОВОД «ГАЗЛИ-САРИМОЙ» (54 КМ)
Линейный крановый узел DN1000 КУП-D9

| Стадия | Лист | Листов |
|---|---|---|
| РД | 1 | 1 |

Изометрический чертеж трубопровода
1000-GT-63CS00-HH-D0901

ООО "EAST-WEST Engineering"
г. Ташкент 2026г.

Взам. инв. №

Подпись и дата

Инв.№ подл.

Формат А2 594х420