
N СЕВЕР

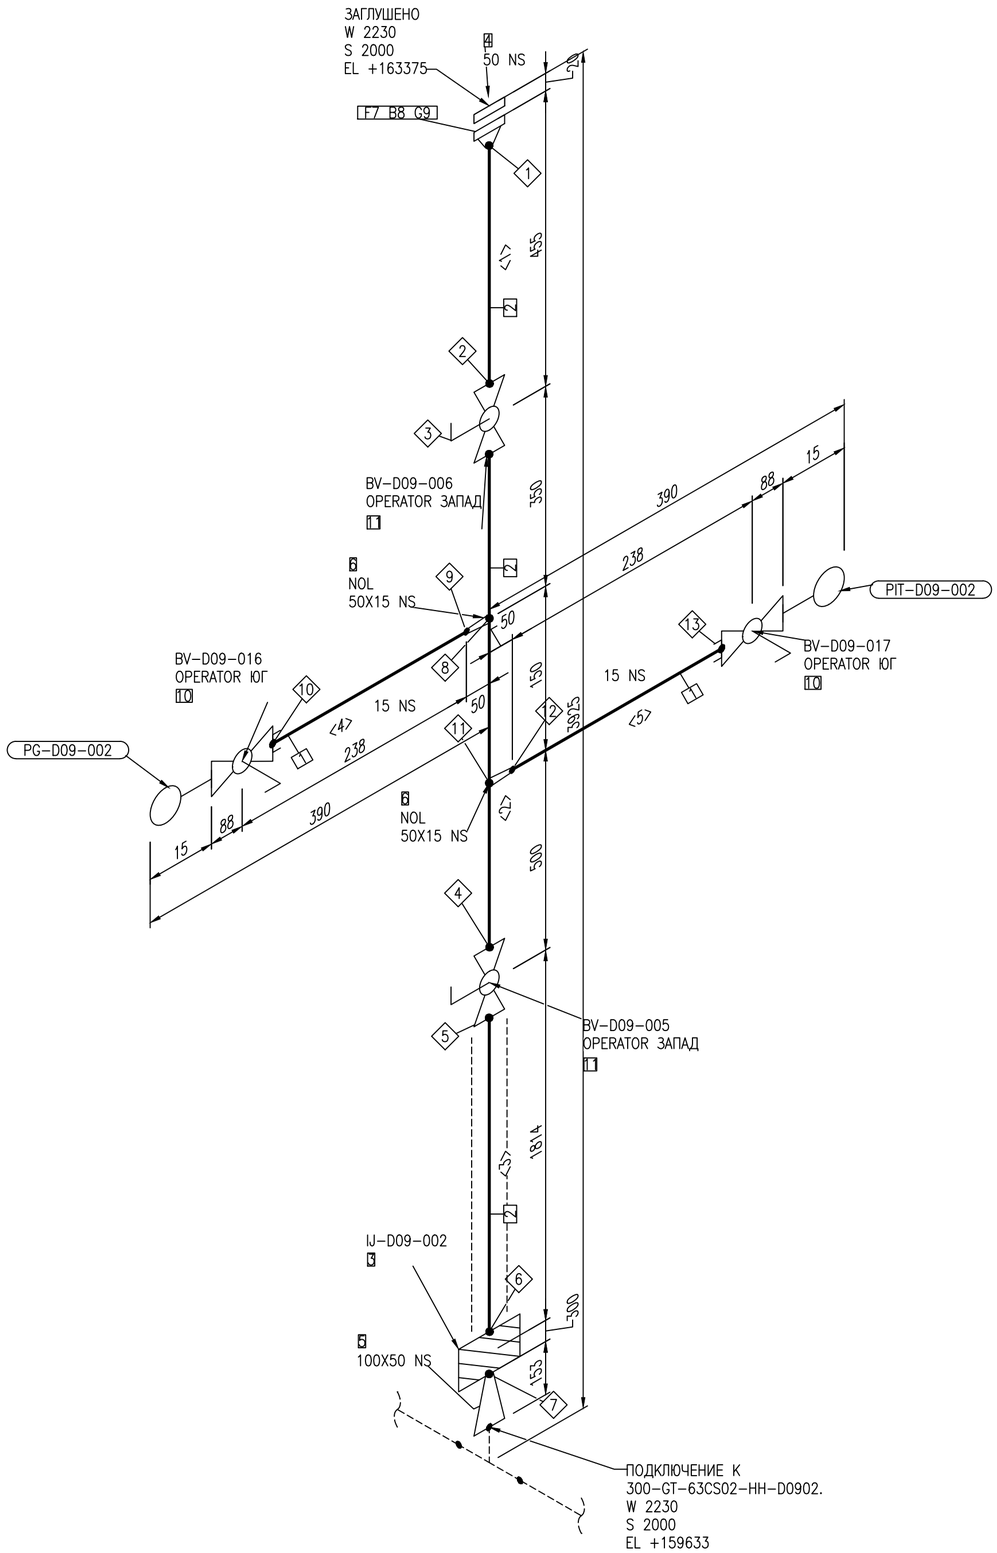

ПЕРЕЧЕНЬ СВАРНЫХ ШВОВ		
№	DN	ТИП
1	50	BUTTWELD
2	50	BUTTWELD
3	50	BUTTWELD
4	50	BUTTWELD
5	50	BUTTWELD
6	50	BUTTWELD
7	50	BUTTWELD
8	50	TAPWELD
9	15	WELD
10	15	SOCKETWELD
11	50	TAPWELD
12	15	WELD
13	15	SOCKETWELD

ПЕРЕЧЕНЬ ТРУБНЫХ КАТУШЕК		
№	DN	ДЛИНА
1	50	273ММ
2	50	770ММ
3	50	1399ММ
4	15	150ММ
5	15	150ММ

СПЕЦИФИКАЦИЯ ИЗДЕЛИЙ И МАТЕРИАЛОВ

ПОЗ.	НАИМЕНОВАНИЕ	СТАНДАРТ	КОЛ.	ПРИМЕЧАНИЕ
1	Трубы стальные бесшовные холоднодеформированные Cm20, 22X3	ГОСТ 8734-75/ ГОСТ 8733-74	0.3М	
2	Трубы стальные бесшовные горячедеформированные Cm20, 57X4	ГОСТ 8732-78/ ГОСТ 8731-74	2.5М	
3	Изолирующее соединение приварное, 6.3 МПа, 57X4	EWE0426-MGL1-PRE-054-DSH-610135	1	
4	Заглушка фланцевая стальная АТК 24.200.02-90, исполнение 4, 6.3 МПа, Cm20, DN50	АТК 24.200.02-90	1	
5	Переход ПШК I 114(5К48)X57(4К42)-5,5(6,9)-0.75-30, сталь 09Г2С	ТУ 1469-017-38948552-2015	1	
6	Штуцер приварной ШУсТ-1-50-22X3.0-6,3-20-2	ТУ 3600-010-88626180-2012	2	
7	Фланец стальной приварной встык, тип 11, исполнение J, ряд 1, 6.3 МПа, Cm20, 57X4	ГОСТ 33259-2015	1	
8	Крепежный комплект 2-1-M20x110, шпильки Cm35, шайбы Cm20, гайки Cm25, для DN50	ОСТ 26-2040-96	4	
9	Прокладка овального сечения, линзовая стальная, тип 1, Сталь 08КП, 6.3 МПа, DN50	ГОСТ 34655-2020	1	
10	Кран шаровой DN15 PN-6,3 МПа с ручным приводом, приварной x резьбовой, 1/2" NPT F, надземный	EWE0426-MGL1-PRE-054-DSH-610125	2	
11	Кран шаровой DN50 PN-6,3 МПа с ручным приводом,приварной, надземный	EWE0426-MGL1-PRE-054-DSH-610125	2	

Трубопровод	ДАННЫЕ ПО ТРУБОПРОВОДУ		
50-GT-63CS02-HH-D0904	Расчетные параметры	Температура	-26,9...+85 °C
		Давление	6,3 MPa
	Рабочие параметры	Температура	-20...+40 °C
		Давление	5,5 MPa
	Параметры испытания	Тип	Гидравлическое
Ссылочные чертежи No		Давление	6,9 MPa
EWE0426-MGL1-PRE-054-SCM-610111	Изоляция	Тип	HH
		Толщина	mm
	Катодная защита	Да или Нет	Да

Рев.	Дата	Назначение ревизии	Проверил	Утвердил
A1	07.09.2026	Утверждено для строительства		
R1	22.06.2026	Выпущено для рассмотрения		

ЗАКАЗЧИК: UTG UZBEKTRANSGAZ | ГЕНЕРАЛЬНЫЙ ПОДРЯДЧИК: UET | ПОДРЯДЧИК: PBG | ГЕНЕРАЛЬНЫЙ ПРОЕКТИРОВЩИК: EAST WEST ENGINEERING

Изм.	Кол.уч.	Лист	№док.	Подпись	Дата
ГИП		Кирпичников С.			09.2026
Нач.отд.		Рябинин А.			09.2026
Исполн.		Таштимуров Р.			09.2026
Н.контр		Кирпичников С.			09.2026

EWE0426-MGL1-PRE-054-ISO-780605-A1

«СТРОИТЕЛЬСТВО НОВЫХ НИТОК (УЧАСТКОВ) ГАЗОПРОВОДОВ «ГАЗЛИ - САРИМОЙ» И «АКЧАЛОК - ГАЗЛИ - НУКУС» ОБЩЕЙ ПРОТЯЖЕННОСТЬЮ НЕ МЕНЕЕ 275 КМ».

ГАЗОПРОВОД «ГАЗЛИ-САРИМОЙ» (54 КМ)
Линейный крановый узел DN1000 КУП-D9

Стадия	Лист	Листов
РД	1	1

Изометрический чертеж трубопровода
50-GT-63CS02-HH-D0904

EAST WEST ENGINEERING
ООО "EAST-WEST Engineering"
г. Ташкент 2026г.

Взам. инв. №
Подпись и дата
Инв.№ подл.

Формат А2 594x420