

План / Plan
М (1:50)

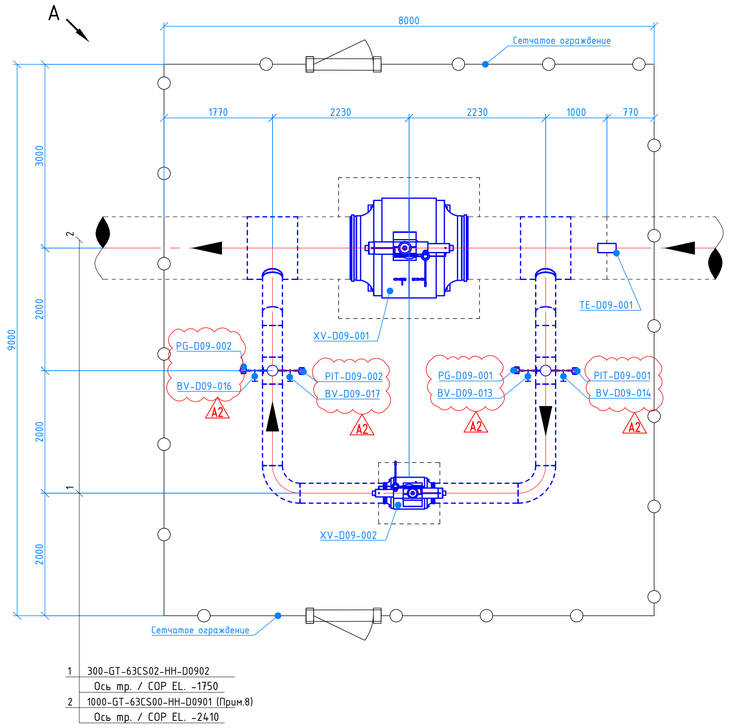


1 300-GT-63CS02-HH-D0902
Ось тр. / COP EL. -1750
2 1000-GT-63CS00-HH-D0901 (Прим.8)
Ось тр. / COP EL. -2410


Изометрический вид "А"
М (1:50)

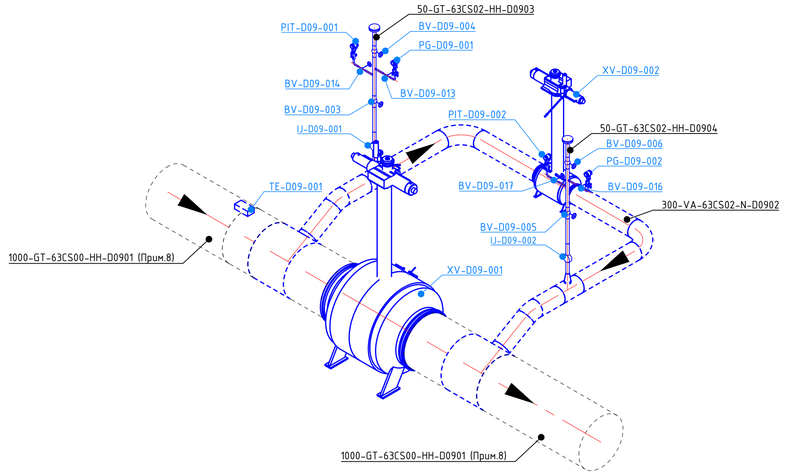

Разрез / Section 1-1
М (1:50)

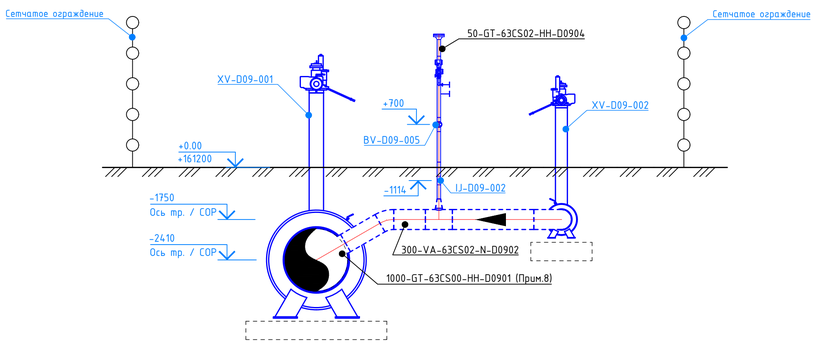

Разрез / Section 2-2
М (1:50)

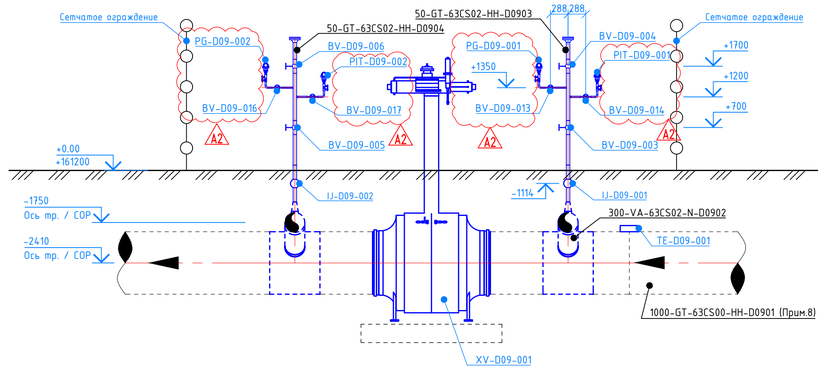

Условные обозначения:

N - нет изоляции
НН - гидроизоляция от почвенной коррозии

ПРИМЕЧАНИЯ

1. Общие данные см. EWE0426-MGL1-PRE-054-COM-780201;
2. * - Размеры для справок;
3. ** - Размеры уточнить по месту;
4. Кран XV-D09-001 расположен на пикете ПК 0+30 перемычки №6 Ду1000;
5. Размеры фитингов - по ГОСТ. Все размеры указаны в миллиметрах;
6. Высотные отметки уточнить по месту;
7. Данный чертеж составлен на основе EWE0426-MGL1-PIL-054-COM-660201;
8. Труба учтена в линейной части проекта;
9. Привязка к пикетажу указана в EWE0426-MGL1-PRE-054-PLA-780202;
10. Фундаменты под опоры, шаровой кран XV-D09-001, продувочную свечу см. EWE0426-MGL1-STR-054-COM-780501;
11. Детальную информацию по трубопроводам см. изометрические чертежи;
12. На схеме указано основное направление потока газа, согласно схеме PFD, см. EWE0426-MGL1-PRE-054-PFD-610101. В процессе эксплуатации поток может быть направлен в обратном направлении.

Рев	Дата	Назначение ревизии	Проверил	Утвердил
A2	28.08.2026	Утверждено для строительства		
A1	24.07.2026	Утверждено для строительства		
R1	19.06.2026	Выпущено для рассмотрения		

ЗАКАЗЧИК: UTG ГЕНЕРАЛЬНЫЙ ПОДРЯДЧИК: UET ПОДРЯДЧИК: PBG ГЕНЕРАЛЬНЫЙ ПРОЕКТИРОВЩИК: EAST WEST ENGINEERING

EWE0426-MGL1-PRE-054-DRW-780203-A2

«СТРОИТЕЛЬСТВО НОВЫХ НИТОК (УЧАСТКОВ) ГАЗОПРОВОДОВ «ГАЗЛИ - САРИМОЙ» И «АКЧАЛОК - ГАЗЛИ - НУКУС» ОБЩЕЙ ПРОТЯЖЕННОСТЬЮ НЕ МЕНЕЕ 275 КМ».

Изм.	Кол.уч.	Лист	№док.	Подпись	Дата			
ГИП		Скабицкий А.			08.2026	ГАЗОПРОВОД «ГАЗЛИ-САРИМОЙ» (54 КМ). Линейный крановый узел DN1000 КУП-D9.	Стадия	Лист	Листов
Нач.отд.		Рябинин А.			08.2026		РП	1	1
Исполн.		Таштимуров Р.			08.2026				
Н.контр		Скабицкий А.			08.2026	КУП-D9. План. Разрезы. Виды. М 1:50	ООО "EAST-WEST Engineering" г. Ташкент 2026г.		

Взам. инв. №
Подпись и дата
Инв.№ подл.

Формат / Format A1