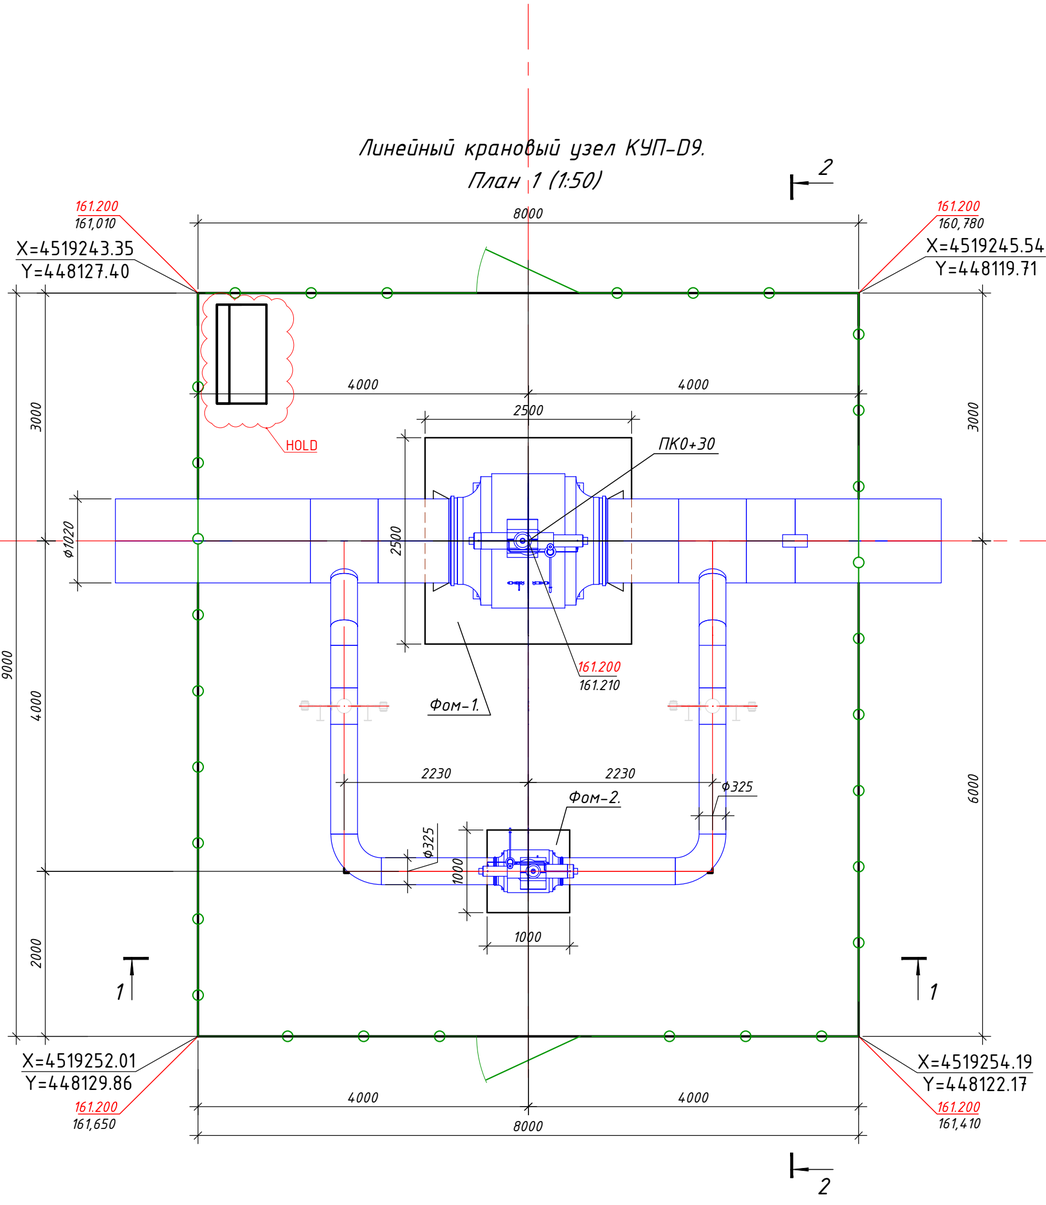


Спецификация элементов

Марка Поз.	Обозначение	Наименование	Кол. шт.	Масса ед.кг	Примеч.
		Линейный крановый узел КУП-D9.			
Фом-1	EWE0426-MGL1-STR-054-DRW-780504	Фундамент оборудования, монолитный Фом-1	1		
Фом-2	EWE0426-MGL1-STR-054-DRW-780505	Фундамент оборудования, монолитный Фом-2	1		

Внимание!
От отметки 160,80 предусмотреть насыпь до спланированных, планировочных отметок земли на территории кранового узла КУП-D9 – 161,200, данная насыпь учтена в части проекта Генерального плана (ГП).

Примечание:

1. *Установка кранового узла КУП-D9 (Ду1000) расположена на ПК0+30 трассы проектной перемычки № 6 газопровода, продольный профиль перемычки ПК0 – ПК0+64,4.*

Условные обозначения:

161.200 – *Отметка спланированной поверхности земли*

161.410 – *Отметка существующей поверхности земли*

A1	09.09.2026	Выпущено для строительства		
R1	31.07.2026	Выпущено для рассмотрения		
Рев	Дата	Назначение ревизии	Проверил	Утвердил

ЗАКАЗЧИК: UTG ГЕНЕРАЛЬНЫЙ ПОДРЯДЧИК: UET ПОДРЯДЧИК: PBG ГЕНЕРАЛЬНЫЙ ПРОЕКТИРОВЩИК: EAST WEST ENGINEERING

Изм.	Кол.уч.	Лист	№ док.	Подпись	Дата	
ГИП		Кирпичников С.			09.09.26	
Нач.отд.		Каршиев А.			09.09.26	
Исполн.		Хабиров Х.			09.09.26	
Н.контр		Кирпичников С.			09.09.26	

EWE0426-MGL1-STR-054-DRW-780502-A1

«СТРОИТЕЛЬСТВО НОВЫХ НИТОК (УЧАСТКОВ) ГАЗОПРОВОДОВ «ГАЗЛИ – САРИМОЙ» И «АКЧАЛОК – ГАЗЛИ – НУКУС» ОБЩЕЙ ПРОТЯЖЕННОСТЬЮ НЕ МЕНЕЕ 275 КМ».

ГАЗОПРОВОД "ГАЗЛИ-САРИМОЙ" (54 КМ)
Линейный крановый узел DN1000 КУП-D9

Стадия	Лист	Листов
РП	1	1

Схема расположения кранового узла КУП-D9.

EAST WEST ENGINEERING ООО "EAST-WEST Engineering" г. Ташкент 2026г.

Взам. инв. №

Подпись и дата

Инв.№ подл.

Формат / Format A2