Разрез 1 - 1 м 1:20.

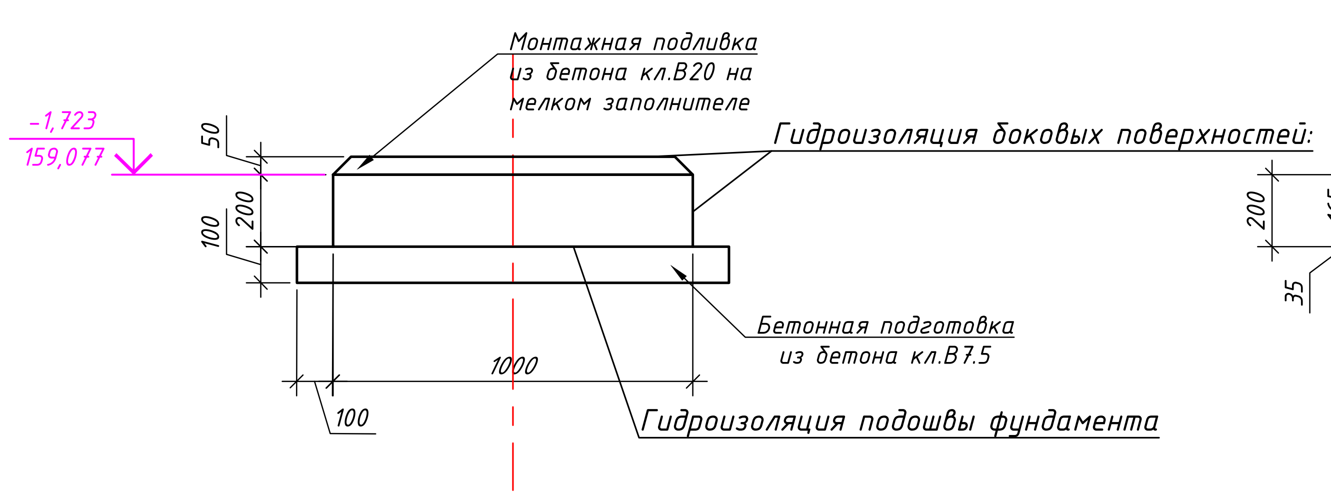
-1,723
159,077
50
100
200
Монтажная подливка из бетона кл.В20 на мелком заполнителе
Гидроизоляция боковых поверхностей:
Бетонная подготовка из бетона кл.В7.5
1000
100
Гидроизоляция подошвы фундамента

Разрез 1-1 м 1:20.
(армирование)

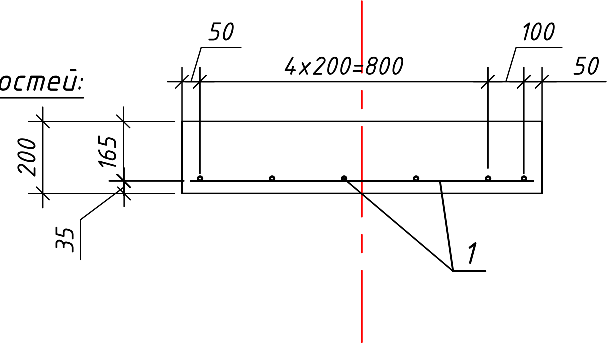

План фундамента
Фом-2 м 1:20.

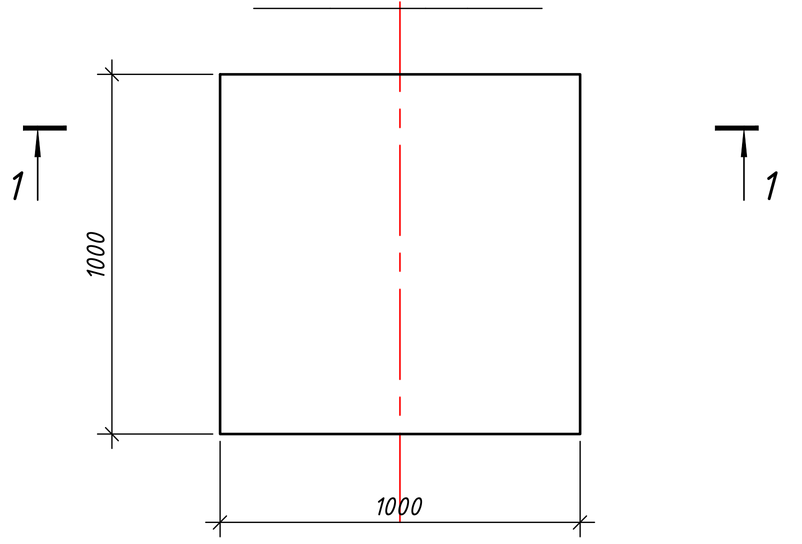

Сетка С1 м 1:20.

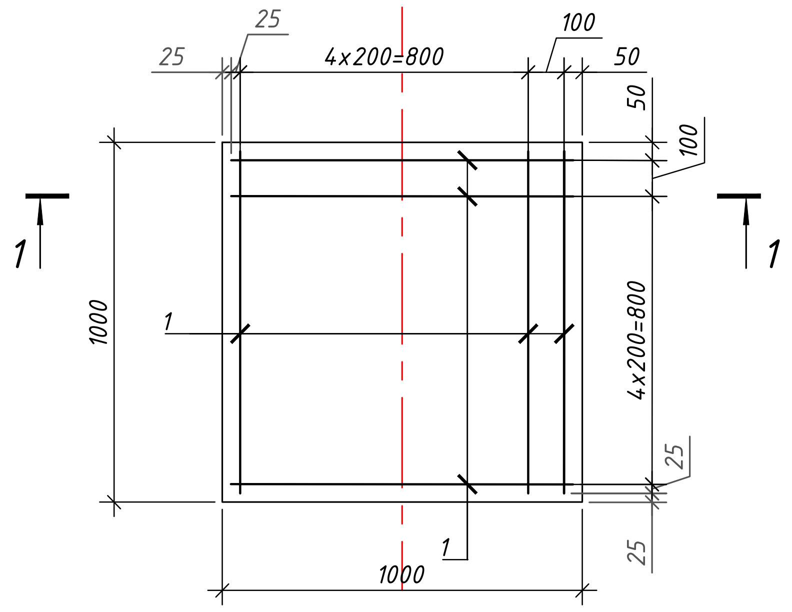

Спецификация элементов

Марка Поз.	Обозначение	Наименование	Кол.шт	Масса ед., кг	Прим.
		Фундамент Фом-2			
		Сборные единицы			
С1	См. данный лист	Сетка С1	1		10.12
		Детали			
1	ГОСТ 34028-2016	Ф12 А500 L=950 мм	12	0.84	10.12
		Материалы			
	на подливку	Бетон на мелком заполнителе кл. В20, W6, F50			0.05 м³
		Бетон кл. В15, W6, F50			0.20 м³
	на подготовку	Бетон кл. В7.5			0.14 м³
		Гидроизоляция фундамента на площади:			3,05 м²

Примечания:

1. Объединение арматурных стержней в плоские сетки или пространственные каркасы выполнять вязальной стальной отожженной проволокой d=0.8-1.0мм. Применение ручной электродуговой сварки не допускается.
2. Подливку выполнить из бетона кл. В20 на мелком заполнителе.
3. Расположение фундамента смотри чертёж: Схема расположения кранового узла КУП-D9.
4. Фундаментов Фом-2 изготовить в количестве - 1шт.
5. Бетон для фундамента применять на сульфатостойком портландцементе.
6. HOLD в ожидании КД от Поставщика на приводные краны.

Гидроизоляция фундамента из двух слоев полимерного покрытия на основе лака ХП-734 по ГОСТ 52165-2003 толщиной 25 мкм.

Рев	Дата	Назначение ревизии	Проверил	Утвердил
A1	09.09.2026	Выпущено для строительство		
R1	31.07.2026	Выпущено для рассмотрения		

ЗАКАЗЧИК: UZTRANSGAZ
ГЕНЕРАЛЬНЫЙ ПОДРЯДЧИК: UZBEKENERGOTAMIR
ПОДРЯДЧИК: PBG Pro Build Generation
ГЕНЕРАЛЬНЫЙ ПРОЕКТИРОВЩИК: EAST WEST ENGINEERING

EWE0426-MGL1-STR-054-DRW-780506-A1

«СТРОИТЕЛЬСТВО НОВЫХ НИТОК (УЧАСТКОВ) ГАЗОПРОВОДОВ «ГАЗЛИ - САРИМОЙ» И «АКЧАЛОК - ГАЗЛИ - НУКУС» ОБЩЕЙ ПРОТЯЖЕННОСТЬЮ НЕ МЕНЕЕ 275 КМ».

Изм.	Кол.уч.	Лист	№ док.	Подпись	Дата
ГИП		Кирпичников С.			09.09.26
Нач.отд.		Каршиев А.			09.09.26
Исполн.		Хабиров Х.			09.09.26
Н.контр		Кирпичников С.			09.09.26

ГАЗОПРОВОД "ГАЗЛИ-САРИМОЙ" (54 КМ)
Линейный крановый узел DN1000 КУП-D9

Стадия	Лист	Листов
РП	1	1

Фундамент Фом-2.

EAST WEST ENGINEERING
ООО "EAST-WEST Engineering"
г. Ташкент 2026г.

Формат / Format A2

Взам. инв. №
Подпись и дата
Инв.№ подл.