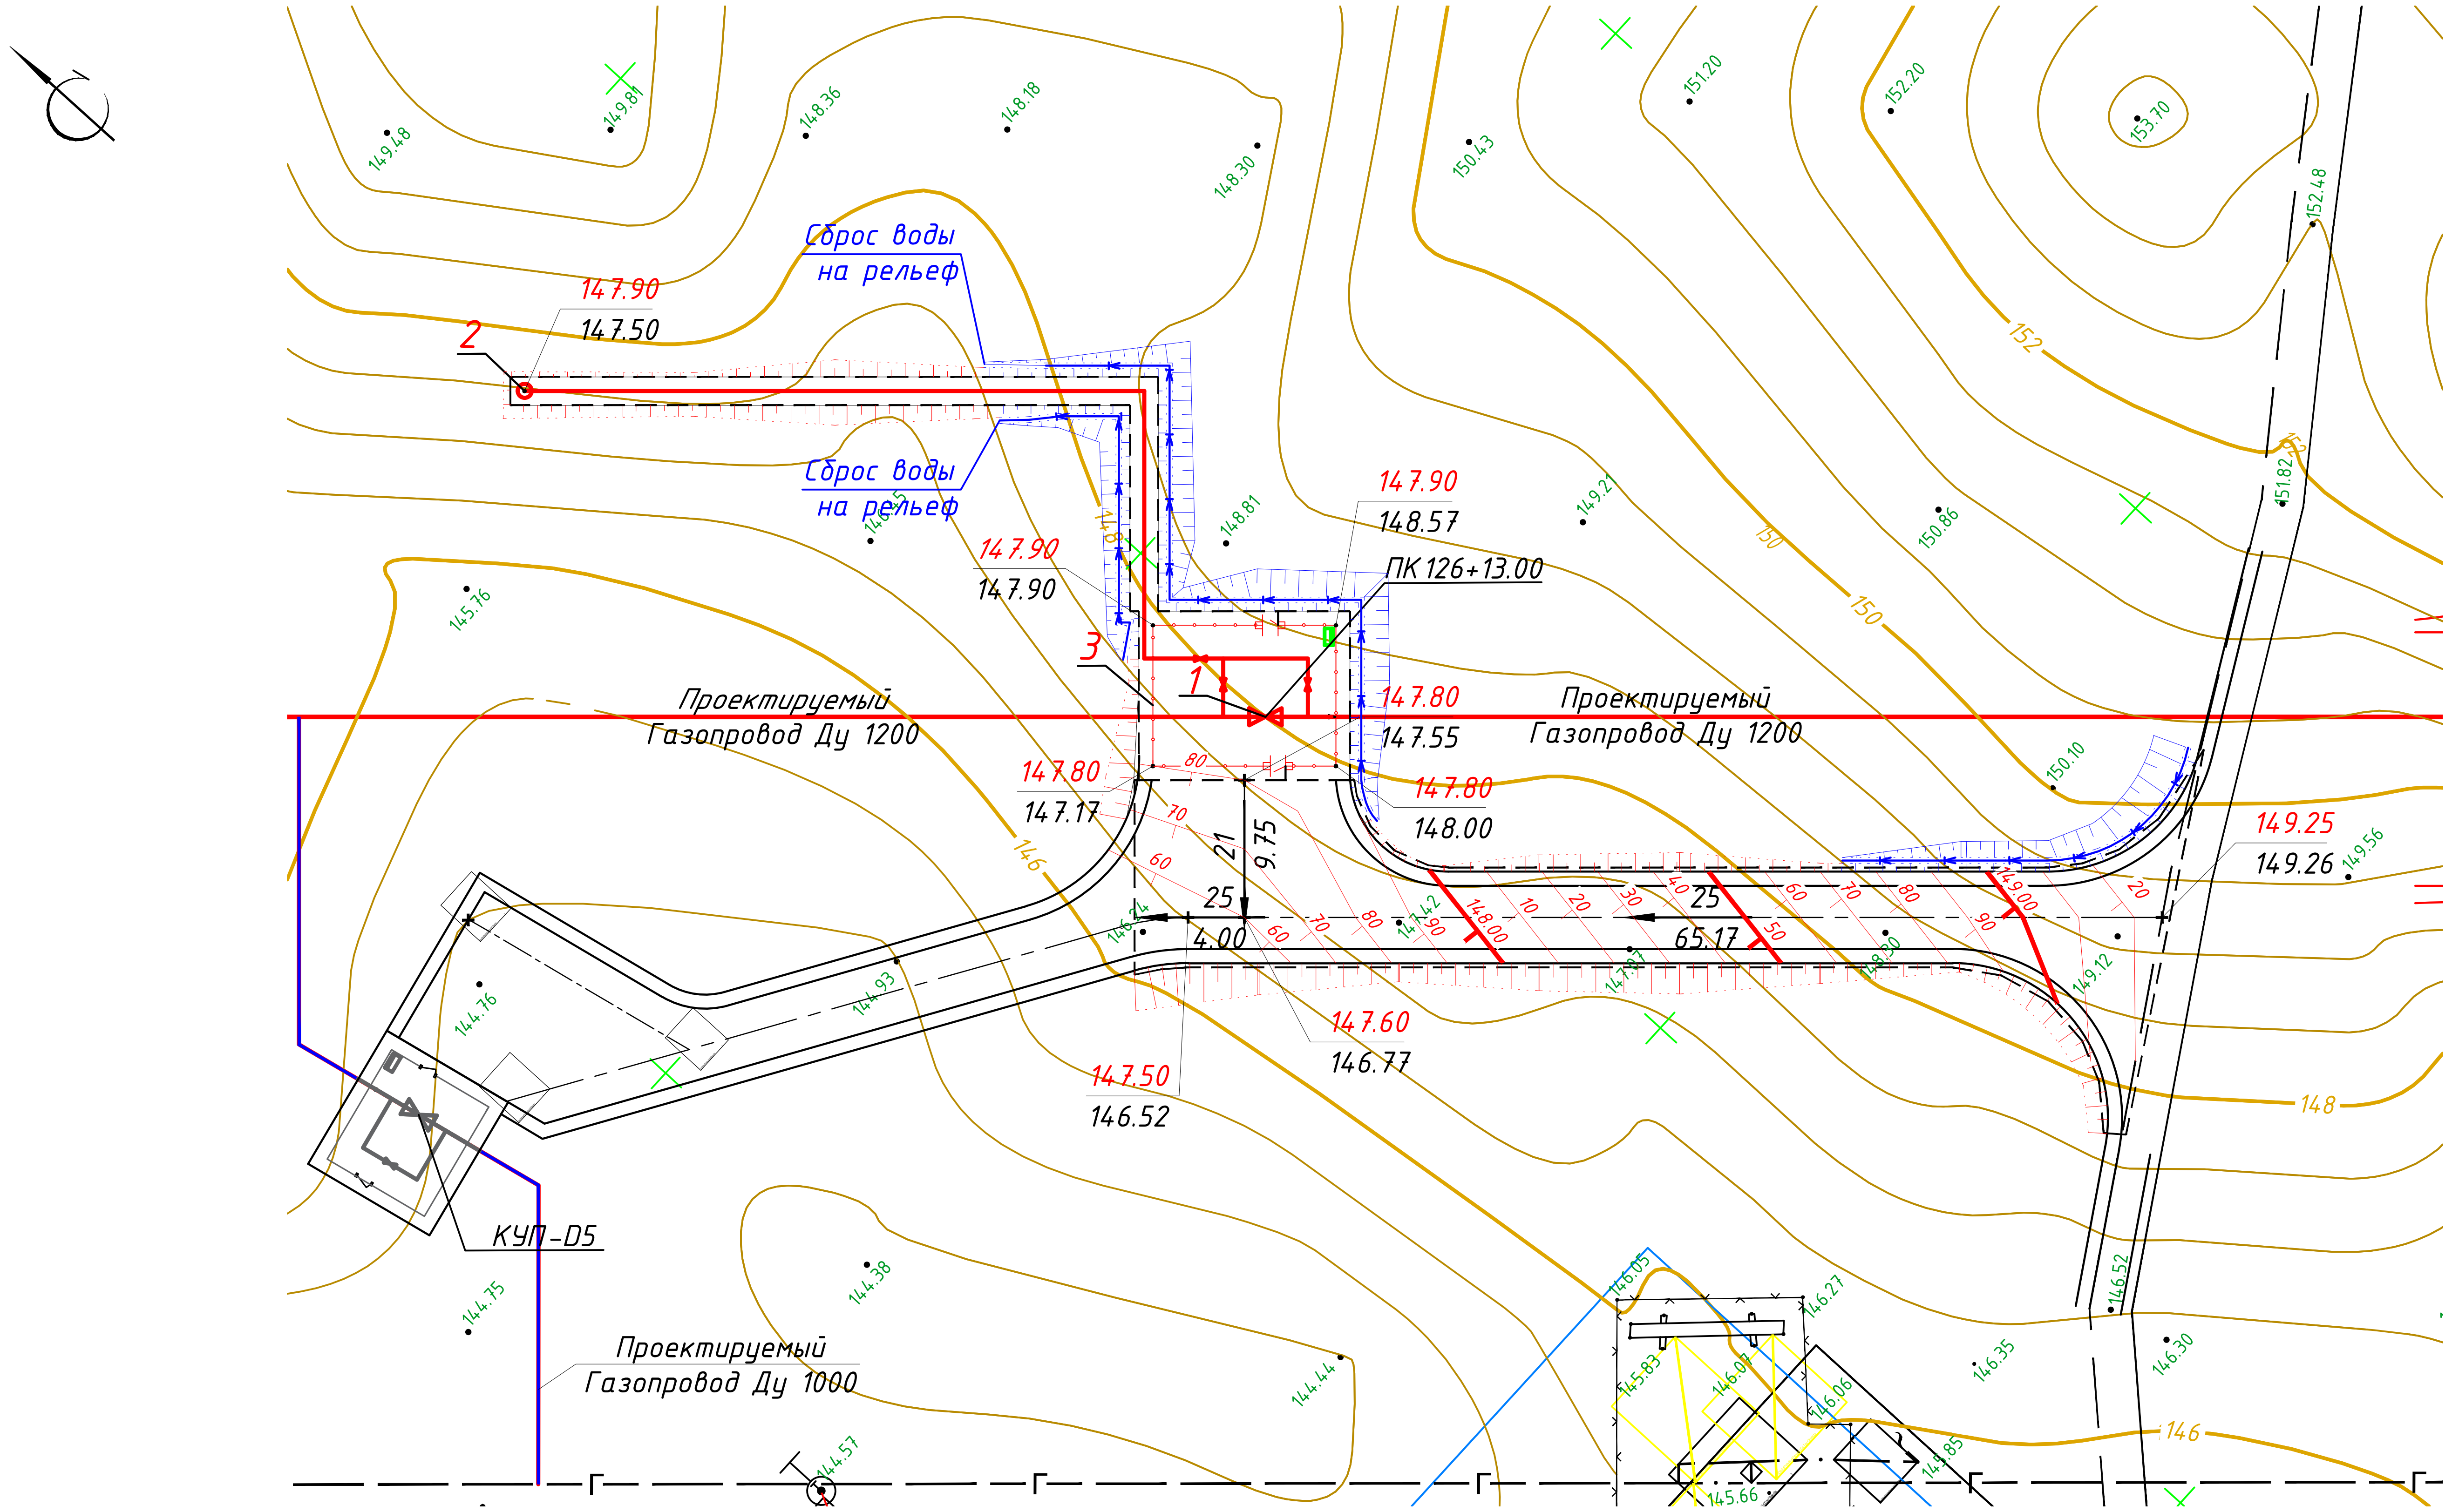
Сброс воды на рельеф
147.90
147.50
2
Сброс воды на рельеф
147.90
147.90
147.90
148.57
ПК 126+13.00
3
1
147.80
147.55
Проектируемый Газопровод Ду 1200
Проектируемый Газопровод Ду 1200
147.80
147.17
147.80
148.00
149.25
149.26
21
9.75
25
4.00
25
65.17
147.60
146.77
147.50
146.52
КУП-D5
Проектируемый Газопровод Ду 1000
152
150
148
146
149.48
149.81
148.36
148.18
148.30
150.43
151.20
152.20
153.70
152.48
151.82
150.86
149.21
148.81
145.76
150.10
149.56
149.12
144.76
144.93
144.75
144.38
144.44
144.57
146.05
146.27
145.83
146.06
145.66
146.35
146.30
146.52
144.85

Примечания:

При составлении настоящего чертежа были использованы :

1. Материалы топографо-геодезической съемки, предоставлены АО "O'ZLITINEFTGAZ".
2. Система координат местная. Высотные отметки даны в Балтийской системе.
3. Размеры даны в метрах.
4. Площадка кранового узла КУП-D3 привязана линейно к пикету ПК 126+13.00.
5. Данный лист смотри совместно с листами разделов PIL, PRE, ELE, STR, SYS.
6. Детальный план кранового узла см. EWE0426-MGL1-PRE-054-DRW-720203.
7. План организации рельефа кранового узла КУП-D5 см. EWE0426-MGL1-GLT-054-DRW-740103.

Экспликация зданий и сооружений

Номер на плане	Наименование	Примечание
1	Крановый узел Ду 1200	
2	Продувочная свеча	
3	Ограждение сетчатое	

Условные обозначения

—•—•—	Ограждение
	Калитка
— — —	Граница планировки
——г——	Существующий газопровод
——	Проектируемый газопровод ДУ-1200
——	Проектируемый газопровод ДУ-1000
147.80 148.00	Проектная отметка Существующая отметка
20	Проектные красные горизонтали
	Откосы насыпи
	Откосы выемки
	Водоотводная канава

Рев.	Дата	Назначение ревизии	Проверил	Утвердил
A2	06.10.2026	Выпущено для строительства		
A1	26.08.2026	Выпущено для строительства		
R1	20.07.2026	Выпущено для рассмотрения		

ЗАКАЗЧИК:
ГЕНЕРАЛЬНЫЙ ПОДРЯДЧИК:
ПОДРЯДЧИК:
ГЕНЕРАЛЬНЫЙ ПРОЕКТИРОВЩИК:

EWE0426-MGL1-GLT-054-DRW-720103-A2

«СТРОИТЕЛЬСТВО НОВЫХ НИТОК (УЧАСТКОВ) ГАЗОПРОВОДОВ «ГАЗЛИ – САРИМОЙ» И «АКЧАЛОК – ГАЗЛИ – НУКУС» ОБЩЕЙ ПРОТЯЖЕННОСТЬЮ НЕ МЕНЕЕ 275 км».

Изм.	Кол.уч.	Лист	№ док.	Подпись	Дата
ГИП		Кирпичников С.			10.2026
Нач.отд.		Нигманова Н.			10.2026
Исполн.		Нигманова Н.			10.2026
Н.контр		Кирпичников С.			10.2026

ГАЗОПРОВОД «ГАЗЛИ-САРИМОЙ» (54 км)
Генеральный план и транспорт.

Стадия	Лист	Листов
РД	1	1

КУП-D3.
План организации рельефа М 1:500

ООО "EAST-WEST Engineering"
г. Ташкент 2026 г.

Формат / Format A4x3

Взам. инв. №
Подпись и дата
Инв.№ подл.