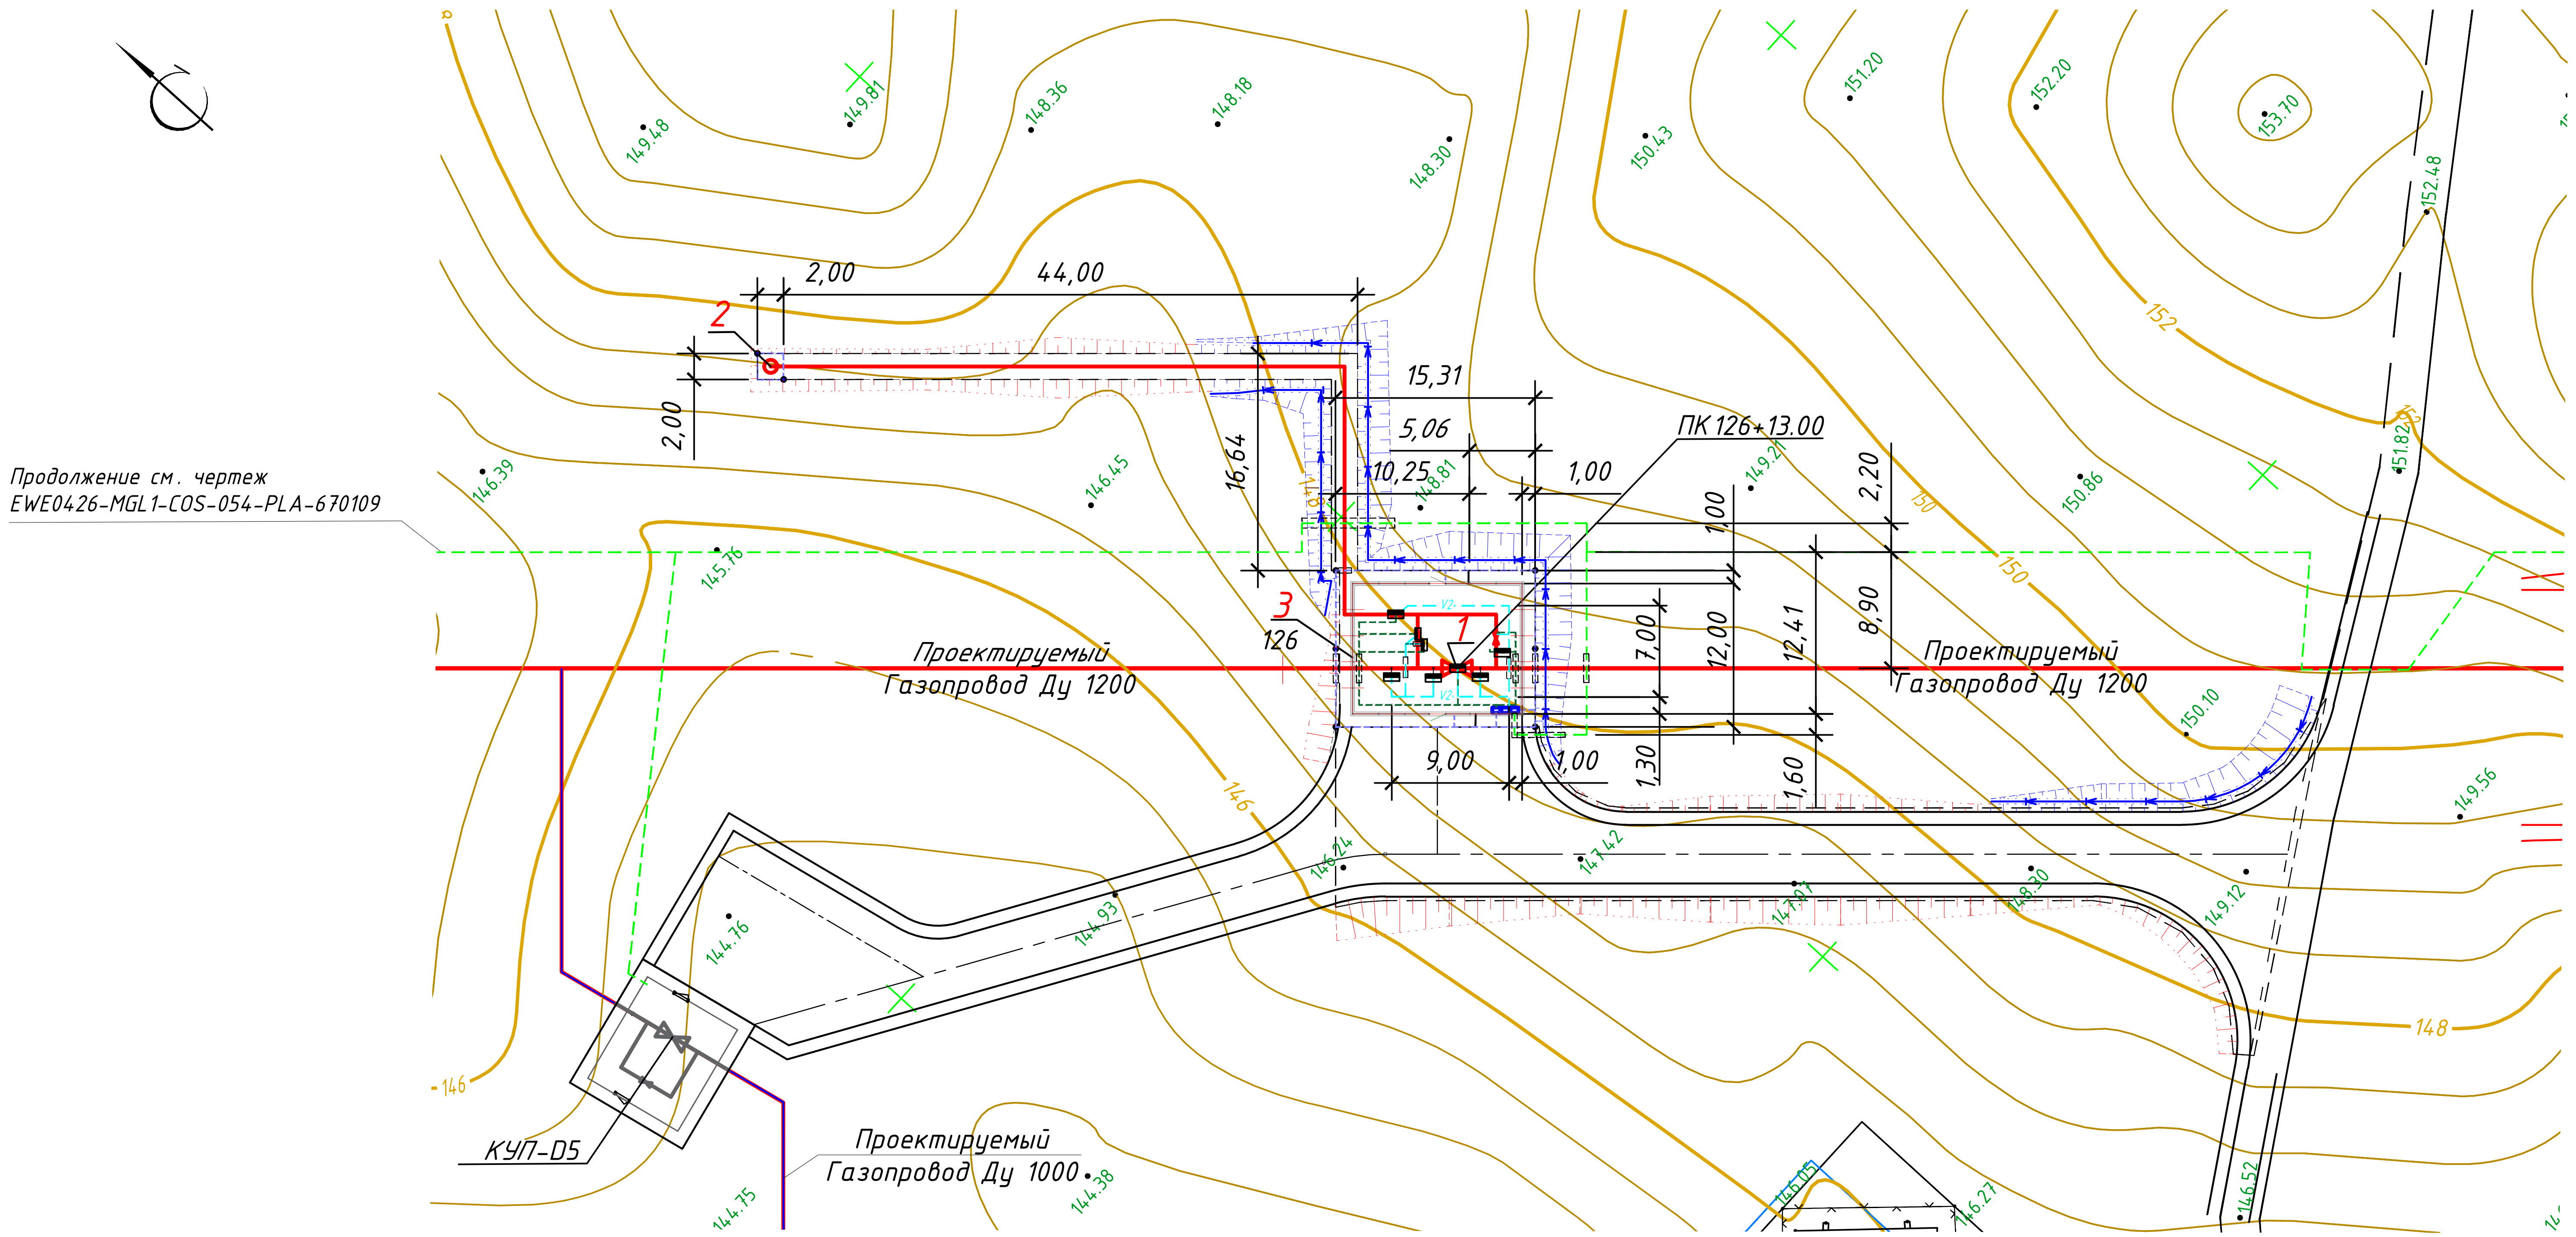
Продолжение см. чертеж
EWE0426-MGL1-COS-054-PLA-670109
2,00
44,00
2,00
15,31
5,06
16,64
10,25
1,00
ПК 126+13.00
1,00
2,20
7,00
12,00
12,41
8,90
3
126
1
2
Проектируемый
Газопровод Ду 1200
Проектируемый
Газопровод Ду 1200
9,00
1,00
1,30
1,60
КУП-Д5
Проектируемый
Газопровод Ду 1000
149.48
149.81
148.36
148.18
148.30
150.43
151.20
152.20
153.70
152.48
152
151.82
146.39
146.45
148.81
149.21
150
150.86
145.76
150.10
149.56
146
147.42
144.24
144.76
144.93
147.77
148.30
149.12
148
146
144.75
144.38
146.52
146.27

Экспликация зданий и сооружений

Номер на плане	Наименование	Примечание
1	Крановый узел Ду 1200	
2	Продувочная свеча	
3	Ограждение сетчатое	

Условные обозначения

—г—г—	Существующий газопровод
—	Проектируемый газопровод ДУ-1200
—	Проектируемый газопровод ДУ-1000
●	Вертикальный заземлитель Ф 16
- - -	Полоса заземления 4х40
- - -	Гибкий провод
⌐ ¬	Стальная труба
▭	Шкаф телемеханики (ШТМ)
▬	Датчики давления
—V2—	Проектный кабель КИПиА в траншее
—[V2]—	Проектный кабель КИПиА в ПНД трубе
—V0—	Проектируемый волоконно-оптический кабель в траншее
—[V0]—	Проектируемый волоконно-оптический кабель в трубе

Примечания:

При составлении настоящего чертежа были использованы :

1. Материалы топографо-геодезической съемки, предоставлены АО "O'ZLITINEFTGAZ".
2. Площадка кранового узла КУП-Д3 привязана линейно к пикету ПК 126+13.00
3. Расстояние по горизонтали (в свету) от подземных инженерных сетей до зданий и сооружений следует принимать не менее указанных в табл.9 см. ШНК 2.09.17-21"Проектирование генеральных планов промышленных предприятий".
4. Расположение оборудования и прокладку кабелей уточнить по месту при монтаже.
5. Данный лист смотри совместно с листами разделов PIL, PRE, ELE, STR, SYS.
6. Детальный план кранового узла см. EWE0426-MGL1-PRE-054-DRW-720203.
7. Детальный план сетей КИПиА см. EWE0426-MGL1-SYS-054-PLA-720306.
8. Детальный план сетей заземления см. см. EWE0426-MGL1-ELE-054-DRW-720402.
9. Детальный план ограждения см. EWE0426-MGL1-STR-054-DRW-720507.
10. Разбивочный план кранового узла КУП-Д5 см. EWE0426-MGL1-GLT-054-DRW-740102.

Взам. инв. №
Подпись и дата
Инв.№ подл.

Рев.	Дата	Назначение ревизии	Проверил	Утвердил
A1	25.09.2026	Выпущено для строительства		
R1	17.08.2026	Выпущено для рассмотрения		

ЗАКАЗЧИК: UTG UZTRANSGAZ
ГЕНЕРАЛЬНЫЙ ПОДРЯДЧИК: UET UZBEKENERGOTAMIR
ПОДРЯДЧИК: PBG Pro Build Generation
ГЕНЕРАЛЬНЫЙ ПРОЕКТИРОВЩИК: EAST WEST ENGINEERING

EWE0426-MGL1-GLT-054-DRW-720105-A1

«СТРОИТЕЛЬСТВО НОВЫХ НИТОК (УЧАСТКОВ) ГАЗОПРОВОДОВ «ГАЗЛИ - САРИМОЙ» И «АКЧАЛОК - ГАЗЛИ - НУКУС» ОБЩЕЙ ПРОТЯЖЕННОСТЬЮ НЕ МЕНЕЕ 275 км».

Изм.	Кол.уч.	Лист	№ док.	Подпись	Дата
ГИП		Схабицкий А.			09.2026
Нач.отд.		Нигманова Н.			09.2026
Исполн.		Горлова О.			09.2026
Н.контр		Схабицкий А.			09.2026

ГАЗОПРОВОД «ГАЗЛИ-САРИМОЙ» (54 км)
Генеральный план и транспорт.

Стадия	Лист	Листов
РД	1	1

КУП-Д3.
Сводный план инженерных сетей.
М 1:500

ООО "EAST-WEST Engineering"
г. Ташкент 2026г.

Формат / Format A4x3