
СЕВЕР

ПЕРЕЧЕНЬ СВАРНЫХ ШВОВ		
№	DN	ТИП
1	100	BUTTWELD
2	300	BUTTWELD
3	300	BUTTWELD
4	300	BUTTWELD
5	300	BUTTWELD
6	300	BUTTWELD
7	300	WELD

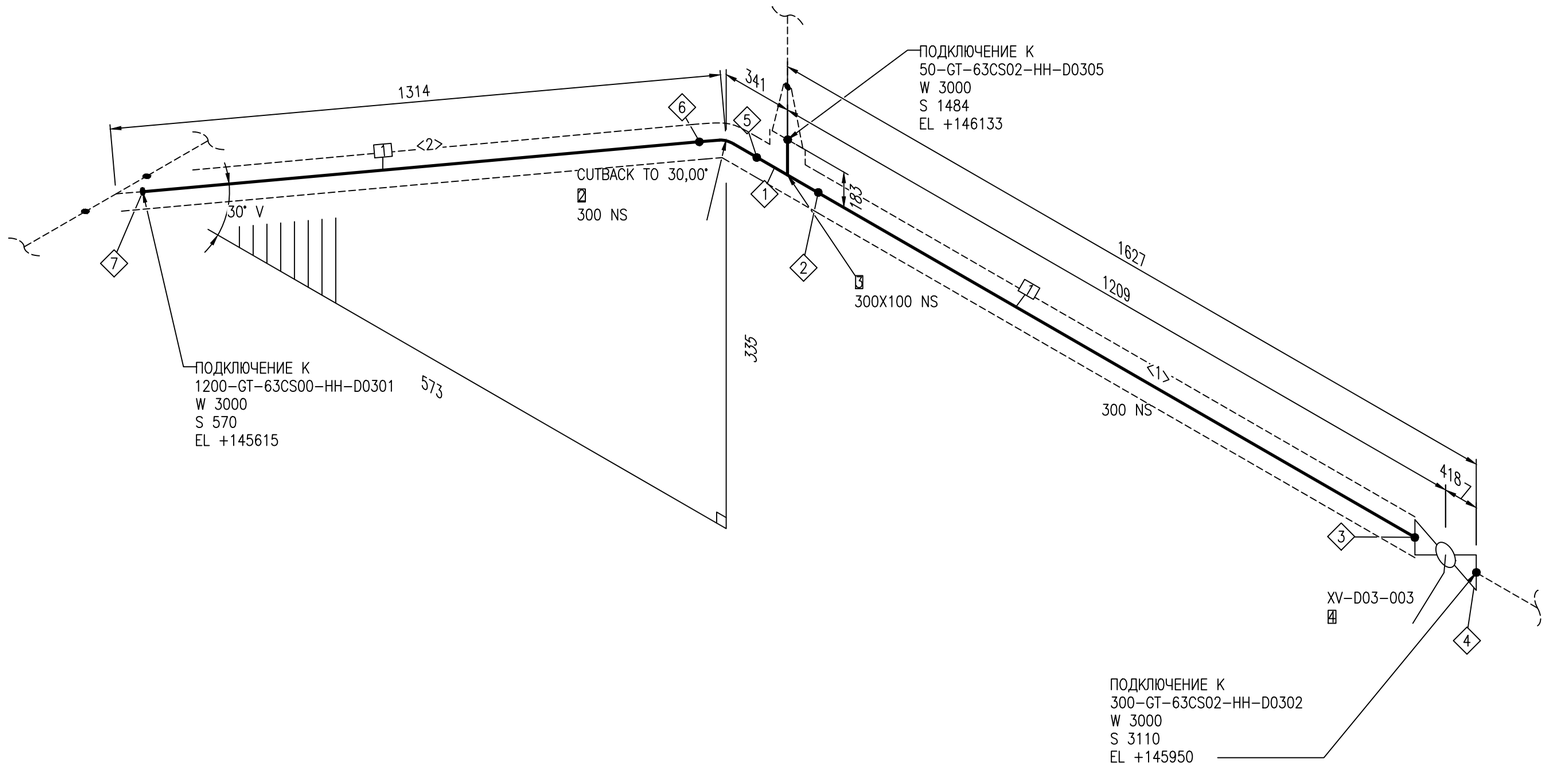

ПЕРЕЧЕНЬ ТРУБНЫХ КАТУШЕК		
№	DN	ДЛИНА
1	300	571ММ
2	300	543ММ

СПЕЦИФИКАЦИЯ ИЗДЕЛИЙ И МАТЕРИАЛОВ				
ПОЗ.	НАИМЕНОВАНИЕ	СТАНДАРТ	КОЛ.	ПРИМЕЧАНИЕ
1	Трубы стальные бесшовные горячедеформированные 09Г2С, 325Х10	ТУ 14-3-1128-2000	1.2М	
2	Отвод ОК I 30-325(10К48)-5,5(6,9)-0,75-1,5DN-30, сталь 09Г2С	ТУ 1469-017-38948552-2015	1	
3	Тройник Т I 325(10К48)-114(5К48)-5,5(6,9)-0,75-30, сталь 09Г2С	ТУ 1469-017-38948552-2015	1	
4	Кран шаровой DN300 PN-6,3 МПа с пневмогидроприводом, приварной, подземный	EWE0426-MGL1-PRE-054-DSH-610121	1	

Трубопровод	ДАННЫЕ ПО ТРУБОПРОВОДУ		
300-GT-63CS02-HH-D0303	Расчетные параметры	Температура	-26,9...+85 °C
		Давление	6,3 MPa
	Рабочие параметры	Температура	-20...+40 °C
		Давление	5,5 MPa
	Параметры испытания	Тип	Гидравлическое
Ссылочные чертежи No		Давление	6,9 MPa
EWE0426-MGL1-PRE-054-SCM-610105	Изоляция	Тип	HH
		Толщина	mm
	Катодная защита	Да или Нет	Да

Рев.	Дата	Назначение ревизии	Проверил	Утвердил
A1	07.09.2026	Утверждено для строительства		
R1	22.06.2026	Выпущено для рассмотрения		

ЗАКАЗЧИК: UTG | ГЕНЕРАЛЬНЫЙ ПОДРЯДЧИК: UET | ПОДРЯДЧИК: PBG | ГЕНЕРАЛЬНЫЙ ПРОЕКТИРОВЩИК: EAST WEST ENGINEERING

Изм.	Кол.уч.	Лист	№док.	Подпись	Дата
ГИП		Кирпичников С.			09.2026
Нач.отд.		Рябинин А.			09.2026
Исполн.		Таштимуров Р.			09.2026
Н.контр		Кирпичников С.			09.2026

EWE0426-MGL1-PRE-054-ISO-720604-A1

«СТРОИТЕЛЬСТВО НОВЫХ НИТОК (УЧАСТКОВ) ГАЗОПРОВОДОВ «ГАЗЛИ - САРИМОЙ» И «АКЧАЛОК - ГАЗЛИ - НУКУС» ОБЩЕЙ ПРОТЯЖЕННОСТЬЮ НЕ МЕНЕЕ 275 КМ».

ГАЗОПРОВОД «ГАЗЛИ-САРИМОЙ» (54 КМ)
Линейный крановый узел DN1200 КУП-D3

Стадия	Лист	Листов
РД	1	1

Изометрический чертеж трубопровода
300-GT-63CS02-HH-D0303

ООО "EAST-WEST Engineering"
г. Ташкент 2026г.

Взам. инв. №

Подпись и дата

Инв.№ подл.

Формат А2 594х420