
Разрез 1 – 1 м 1:25.

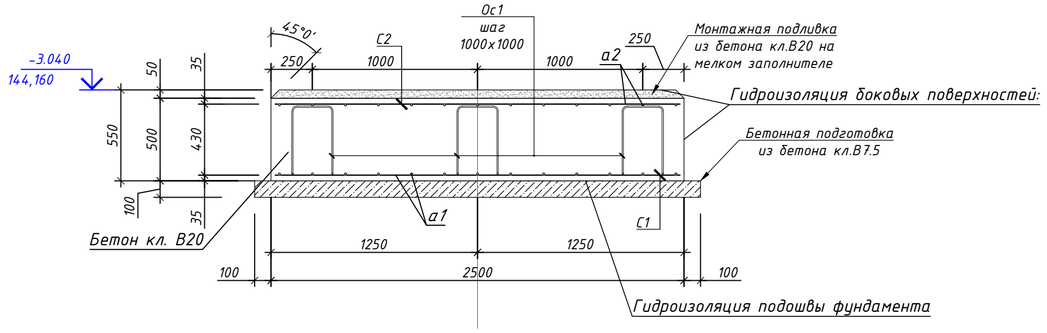

Ведомость деталей


Поз.	Эскиз
Ос1	250, 410, 410, 250, 250, L=1570

Размеры хомутов даны по центру стержня.


Спецификация элементов

Марка Поз.	Обозначение	Наименование	Кол.шт	Масса ед., кг	Прим.
		Фундамент Фом-1			
		Сборные единицы			
С1	См. данный лист	Сетка С1	1		127.18
С2	См. данный лист	Сетка С2	1		56.53
		Сетка С1			
а1	ГОСТ 34028-2016	Ф18 А500 L=2450 мм	26	4.89	127.18
		Детали			
Ос1	ГОСТ 34028-2016	Ф12 А240 L=1570 мм	13	1.39	18.11
		Сетка С2			
а2	ГОСТ 34028-2016	Ф12 А500 L=2450 мм	26	2.17	56.53
		Материалы			
	на подливку	Бетон на мелком заполнителе кл. В20, W6, F50			0.30 м³
		Бетон кл. В20, W6, F50			3.13 м³
	на подготовку	Бетон кл. В7.5			0.73 м³
		Гидроизоляция фундамента на площади:			18,55 м²

План фундамента Фом-1 м 1:50.

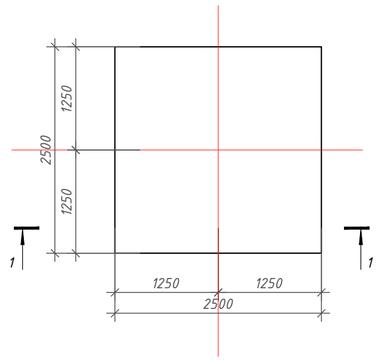

Сетка С1 м 1:50.

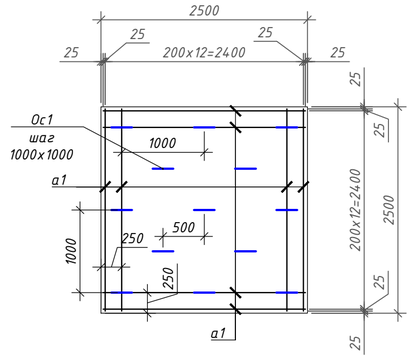

Ведомость расхода стали, кг

Марка элемента	Изделия арматурные					Всего	Общий расход
	Арматура класса						
	А240		А500				
	ГОСТ 34028-2016		ГОСТ 34028-2016				
	Ф12	Итого	Ф18	Ф12	Итого		
Фундамент Фом1	18.11	18.11	127.18	56.53	183.71	201.82	201.82

Примечания:

1. Объединение арматурных стержней в плоские сетки или пространственные каркасы выполнять вязальной стальной отожженной проволокой d=0.8-1.0мм. Применение ручной электродуговой сварки не допускается.
2. Подливку выполнить из бетона кл. В20 на мелком заполнителе.
3. Фундамент Фом-1 разработан под шаровой кран. Бетонирование выполнять после получения оборудования и сверки с паспортными данными.
4. Фиксаторы для крепления двух сеток марки Ос-1 устанавливать в шахматном порядке.
5. Расположение фундамента смотри чертёж: Схема расположения кранового узла КУП-ОЗ.
6. Фундаментов Фом-1 изготовить в количестве - 1шт.
7. Бетон для фундамента применять на сульфатостойком портландцементе.

Гидроизоляция фундамента из двух слоев полимерного покрытия на основе лака ХП-734 по ГОСТ 52165-2003 толщиной 25 мкм.

Рев	Дата	Назначение ревизии	Проверил	Утвердил
А1	09.09.2026	Выпущено для строительства		
R1	24.07.2026	Выпущено для рассмотрения		

ЗАКАЗЧИК: UTG UZTRANSGAZ

ГЕНЕРАЛЬНЫЙ ПОДРЯДЧИК: UET

ПОДРЯДЧИК: PBG

ГЕНЕРАЛЬНЫЙ ПРОЕКТИРОВЩИК: EAST WEST ENGINEERING

EWE0426-MGL1-STR-054-DRW-720504-A1

«СТРОИТЕЛЬСТВО НОВЫХ НИТОК (УЧАСТКОВ) ГАЗОПРОВОДОВ «ГАЗЛИ - САРИМОЙ» И «АКЧАЛОК - ГАЗЛИ - НУКУС» ОБЩЕЙ ПРОТЯЖЕННОСТЬЮ НЕ МЕНЕЕ 275 КМ».

Изм.	Кол.уч.	Лист	№ док.	Подпись	Дата			
ГИП		Кирпичников С.			09.09.26	ГАЗОПРОВОД "ГАЗЛИ-САРИМОЙ" (54 КМ) Линейный крановый узел DN1200 КУП-ОЗ	Стадия	Лист	Листов
Нач.отд.		Каршиев А.			09.09.26		РП	1	1
Исполн.		Хабиров Х.			09.09.26				
Н.контр		Кирпичников С.			09.09.26	Фундамент Фом-1.	ООО "EAST-WEST Engineering" г. Ташкент 2026г.		

Взам. инв. №

Подпись и дата

Инв.№ подл.

Формат / Format A2