Линейный крановый узел КУП-D3.
Схема расположения сетчатого ограждения (1:50).

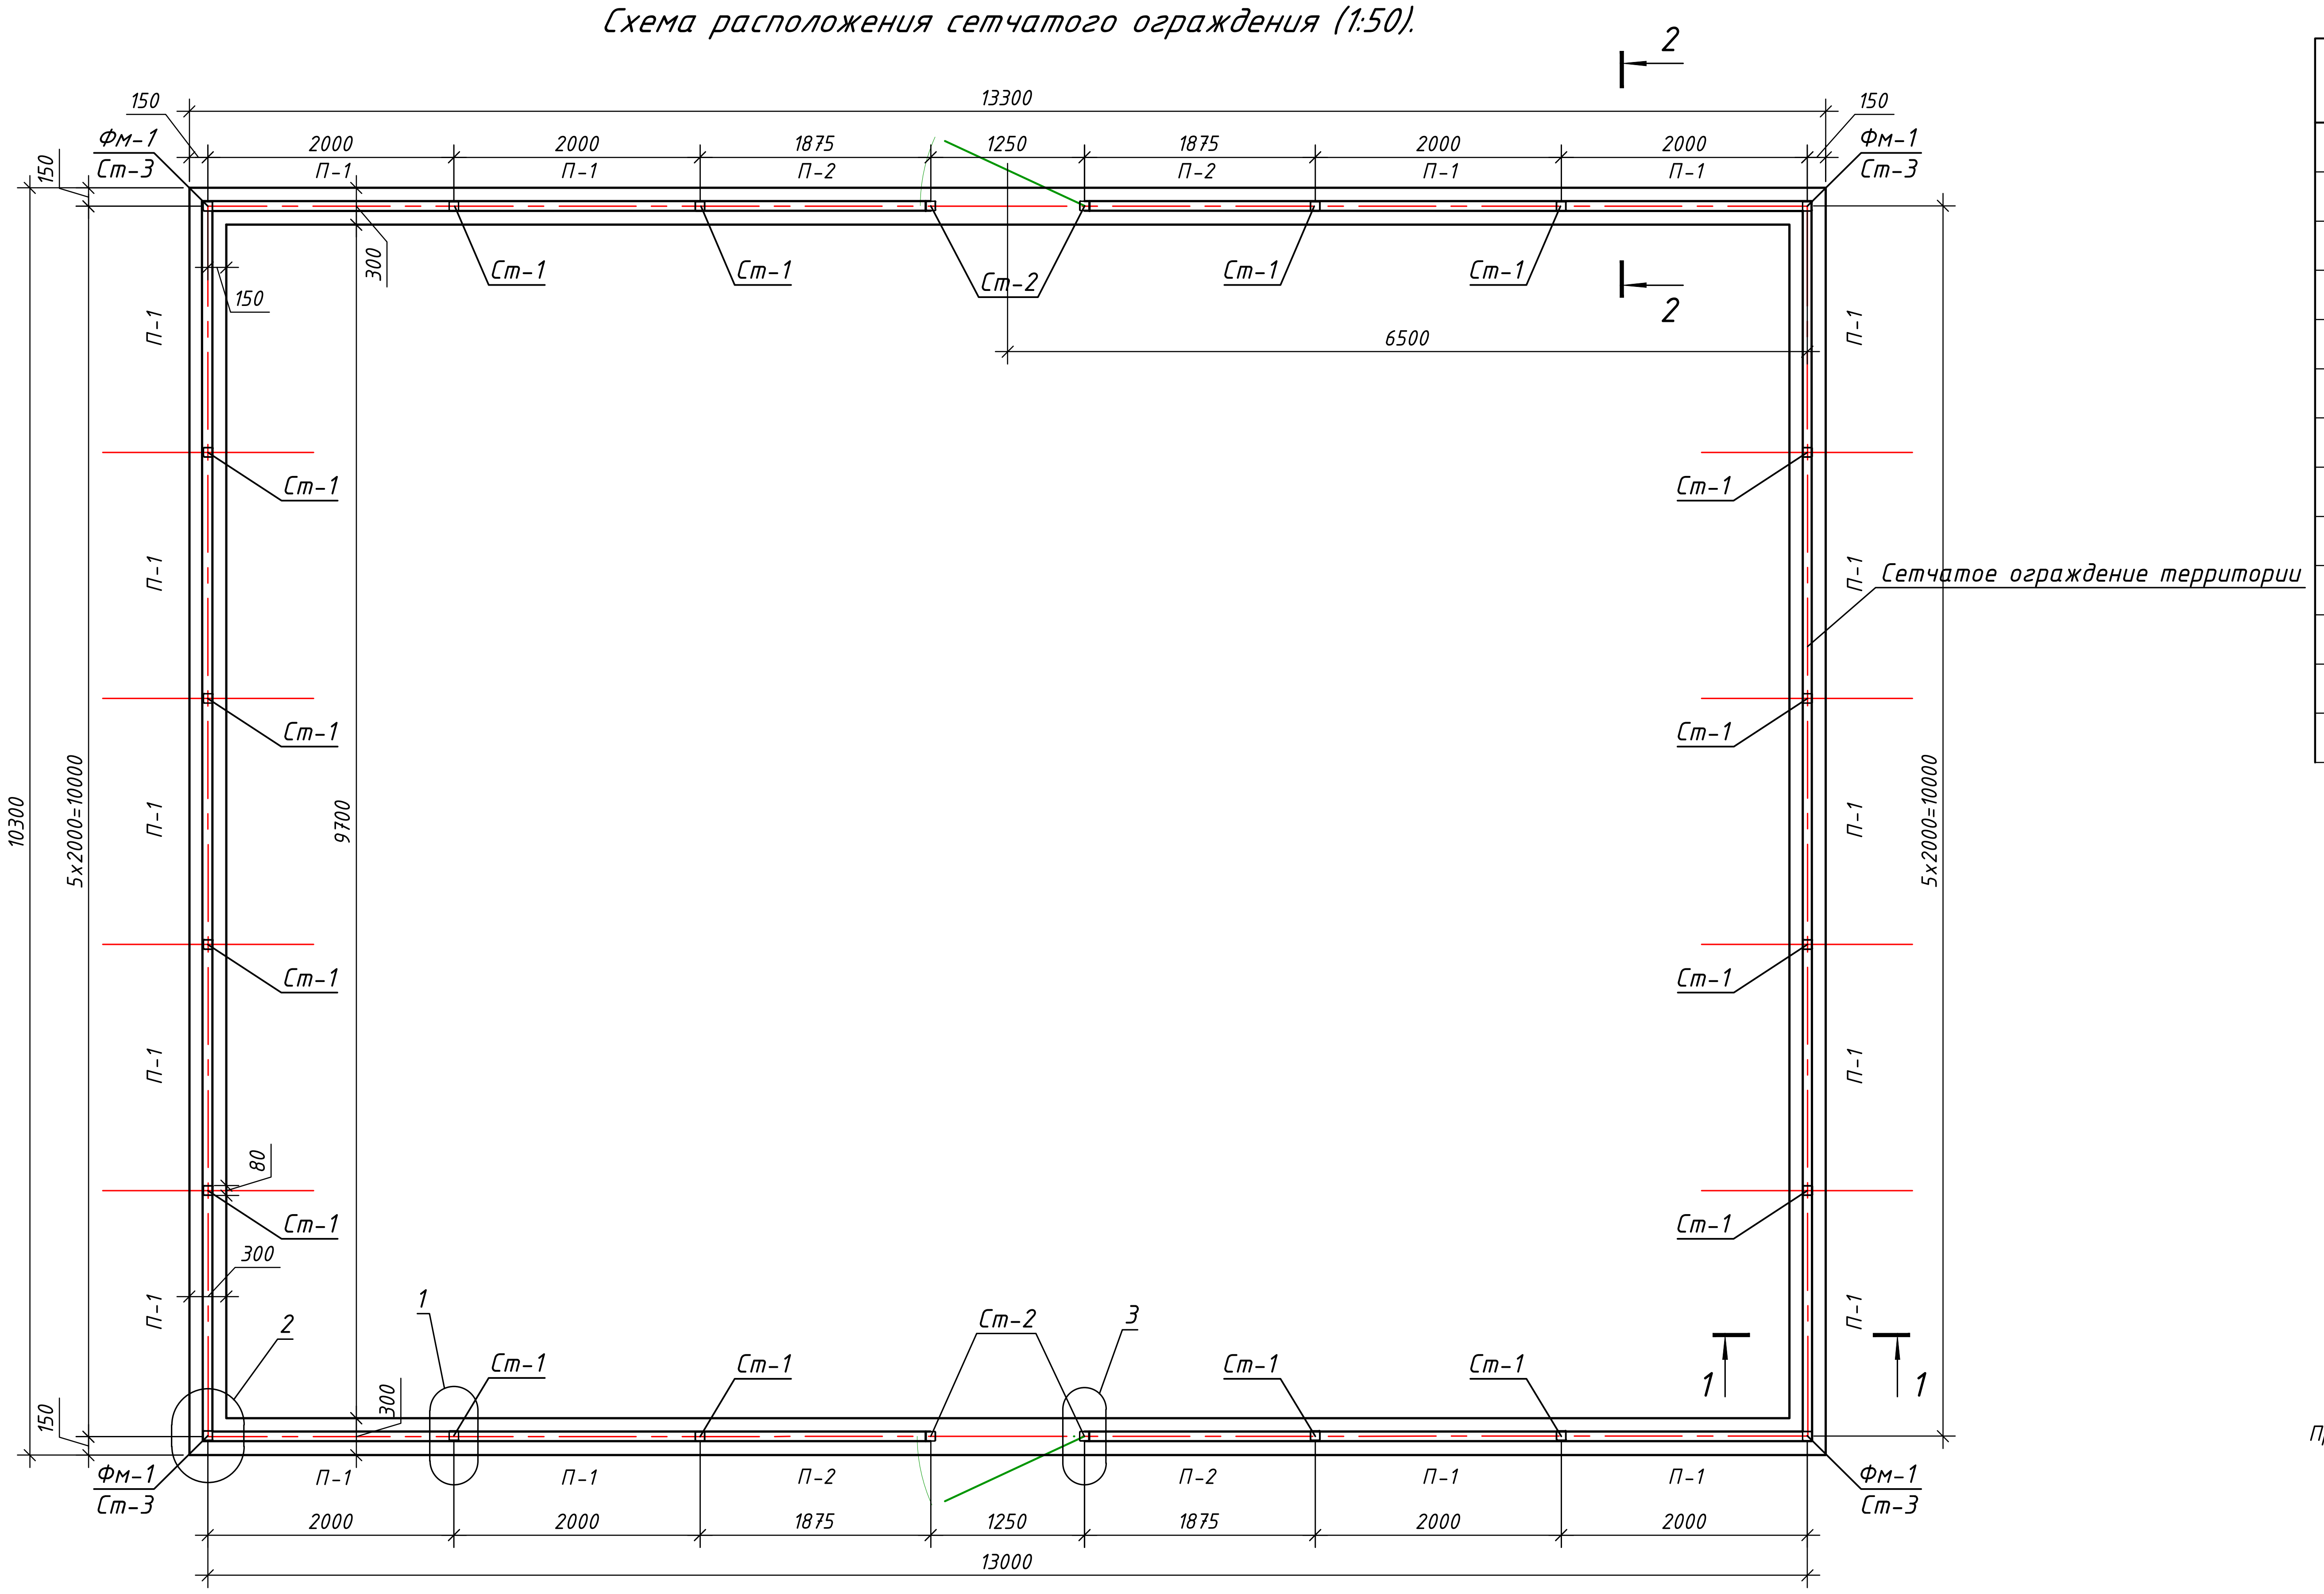

Спецификация элементов

Марка Поз.	Обозначение	Наименование	Кол. шт.	Масса ед.кг	Примеч.
		Линейный крановый узел КУП-D3.			
Фм-1	EWE0426-MGL1-STR-054-DRW-720509	Фундамент ленточный, монолитный Фм-1	1		
Ст-1	EWE0426-MGL1-STR-054-DRW-720510	Стойка ограждения Ст-1	16		
Ст-2	EWE0426-MGL1-STR-054-DRW-720511	Стойка ограждения Ст-2	4		
Ст-3	EWE0426-MGL1-STR-054-DRW-720512	Стойка ограждения Ст-3	4		
П-1	EWE0426-MGL1-STR-054-DRW-720513	Панель ограждения П-1	18		
П-2	EWE0426-MGL1-STR-054-DRW-720514	Панель ограждения П-2	4		
К-1	EWE0426-MGL1-STR-054-DRW-720515	Калитка К-1	2		
КД1	EWE0426-MGL1-STR-054-DRW-720516	Крепежная деталь КД1	24		
КД2	EWE0426-MGL1-STR-054-DRW-720516	Крепежная деталь КД2	32		

Примечания:
1. Данный чертёж читать совместно с ленточным фундаментом Фм-1.
2. Изготовить общее количество узлов:
   - узел 1 - 16шт.
   - узел 2 - 4шт.
   - узел 3 - 4шт.

Узел 1

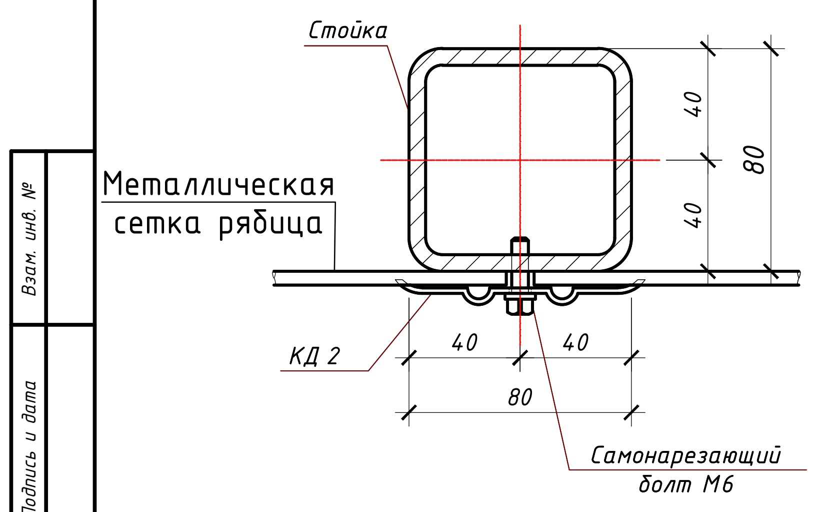

Узел 2

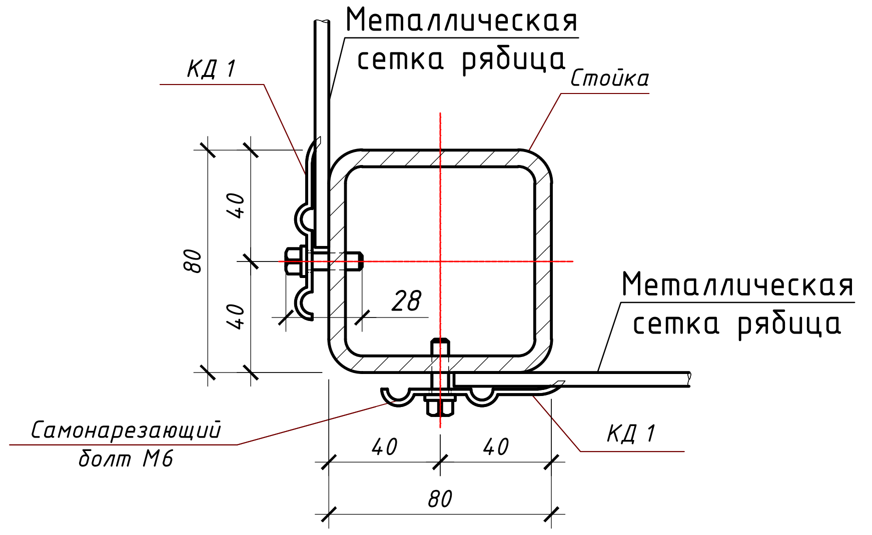

Узел 3

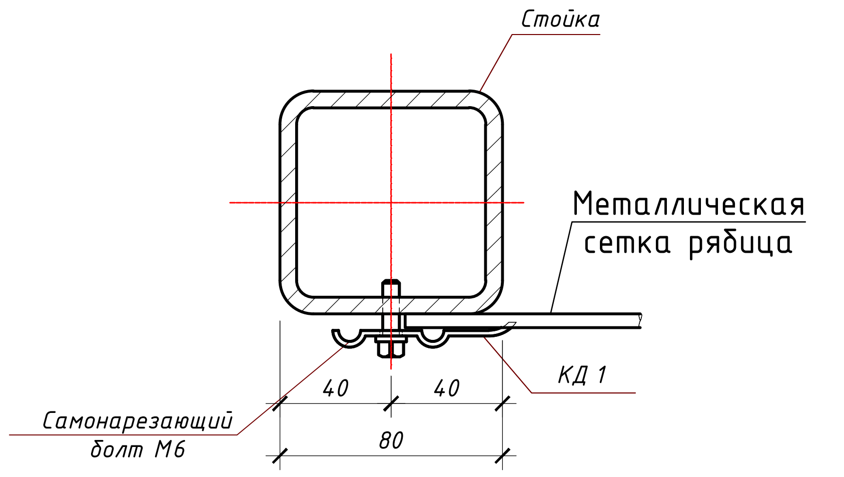

Рев	Дата	Назначение ревизии	Проверил	Утвердил
А1	09.09.2026	Выпущено для строительство		
R1	24.07.2026	Выпущено для рассмотрения		

ЗАКАЗЧИК: UTG UZTRANSGAZ
ГЕНЕРАЛЬНЫЙ ПОДРЯДЧИК: UET UZBEKINNEGOTAMIR
ПОДРЯДЧИК: PBG Pro Build Generation
ГЕНЕРАЛЬНЫЙ ПРОЕКТИРОВЩИК: EAST WEST ENGINEERING

EWE0426-MGL1-STR-054-DRW-720507-A1

«СТРОИТЕЛЬСТВО НОВЫХ НИТОК (УЧАСТКОВ) ГАЗОПРОВОДОВ «ГАЗЛИ - САРИМОЙ» И «АКЧАЛОК - ГАЗЛИ - НУКУС» ОБЩЕЙ ПРОТЯЖЕННОСТЬЮ НЕ МЕНЕЕ 275 КМ».

Изм.	Кол.уч.	Лист	№ док.	Подпись	Дата
ГИП		Кирпичников С.			09.09.26
Нач.отд.		Каршиев А.			09.09.26
Исполн.		Хабиров Х.			09.09.26
Н.контр		Кирпичников С.			09.09.26

ГАЗОПРОВОД "ГАЗЛИ-САРИМОЙ" (54 КМ)
Линейный крановый узел DN1200 КУП-D3

Стадия	Лист	Листов
РП	1	1

Схема расположения сетчатого ограждения.

EAST WEST ENGINEERING
ООО "EAST-WEST Engineering"
г. Ташкент 2026г.

Взам. инв. №
Подпись и дата
Инв.№ подл.

Формат / Format A2