

ВИД

Панель ограждения П-2 м 1:25.

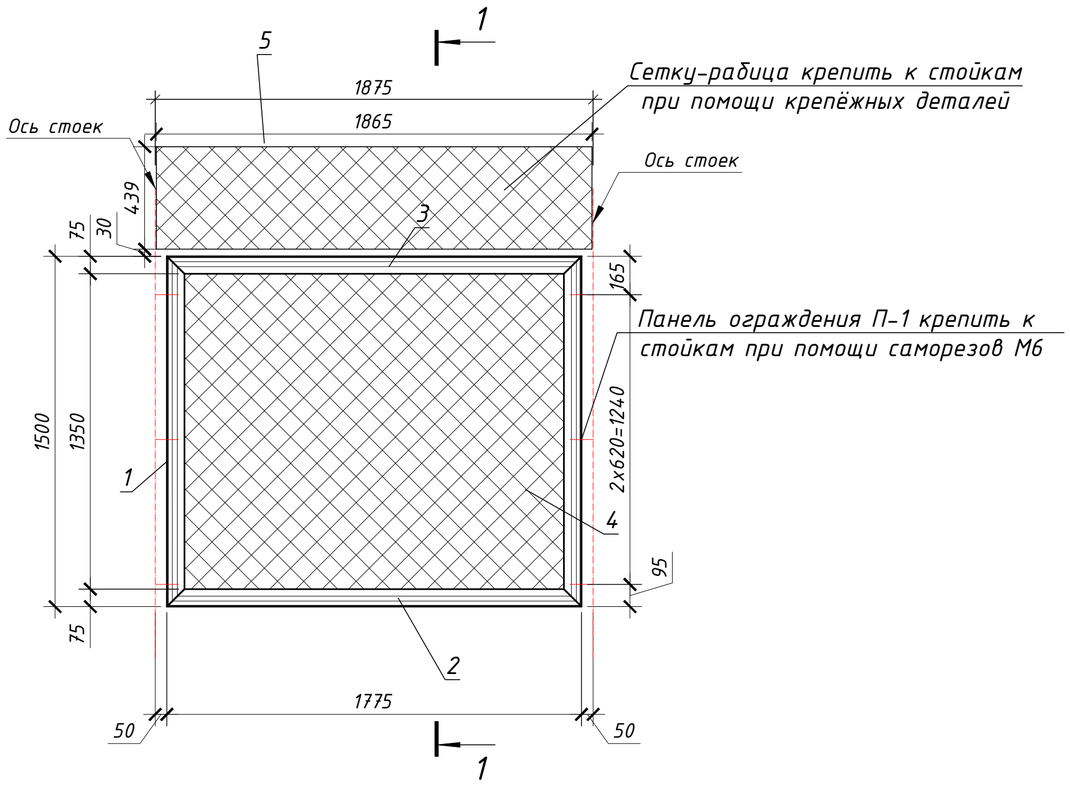

Разрез 1-1 м 1:50.

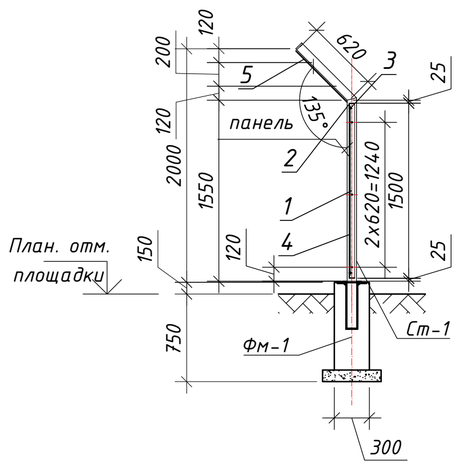

Спецификация расхода материалов

Марка Поз.	Обозначение	Наименование	Кол. шт.	Масса ед.кг.	Примечание
П-2		Панель ограждения П-2		41,63	вес на 1 шт.
1	ГОСТ 8510-93*, Сталь С235	L 75x50x5 L=1500	2	7.19	14.37
2	ГОСТ 8510-93*, Сталь С235	L 75x50x5 L=1775	2	8.50	17.00
3	ГОСТ 34028-2016	Арматура Ф6.0 А240 Lобщ=6200	1	0.222 кг/м.п	1.38
4	ГОСТ 5336-80*	Сетка рабица №50-3.0,размером			
		1450 x 1730мм; S=2.51м2	1	2,42 кг/м2	6.07
5	ГОСТ 5336-80*	Сетка рабица №50-3.0,размером			
		620 x 1865мм; S=1.16м2	1	2,42 кг/м2	2.81
		Материалы:			
		Окраска металлоконструкций масляной краской за 2 раза			1,65м²

Примечания:
1. Сварку вести электродами Э42А ГОСТ9467-75.
2. Конструкция должна быть покрыта масляной краской за 2 раза по грунтовке.

A1	09.09.2026	Выпущено для строительства		
R1	24.07.2026	Выпущено для рассмотрения		
Рев	Дата	Назначение ревизии	Проверил	Утвердил

ЗАКАЗЧИК: UTG UZTRANSGAZ | ГЕНЕРАЛЬНЫЙ ПОДРЯДЧИК: UET UZBEKENERGOTAMIR | ПОДРЯДЧИК: PBG Pro Build Generation | ГЕНЕРАЛЬНЫЙ ПРОЕКТИРОВЩИК: EAST WEST ENGINEERING

Изм.	Кол.уч.	Лист	№ док.	Подпись	Дата
ГИП		Кирпичников С.			09.09.26
Нач.отд.		Каршиев А.			09.09.26
Исполн.		Хабиров Х.			09.09.26
Н.контр		Кирпичников С.			09.09.26

EWE0426-MGL1-STR-054-DRW-720514-A1

«СТРОИТЕЛЬСТВО НОВЫХ НИТОК (УЧАСТКОВ) ГАЗОПРОВОДОВ «ГАЗЛИ - САРИМОЙ» И «АКЧАЛОК - ГАЗЛИ - НУКУС» ОБЩЕЙ ПРОТЯЖЕННОСТЬЮ НЕ МЕНЕЕ 275 КМ».

ГАЗОПРОВОД "ГАЗЛИ-САРИМОЙ" (54 КМ)
Линейный крановый узел DN1200 КУП-D3

Стадия	Лист	Листов
РП	1	1

Панель ограждения П-2.

ООО "EAST-WEST Engineering"
г. Ташкент 2026г.

Взам. инв. №
Подпись и дата
Инв.№ подл.

Формат / Format А3