

План (1:500)

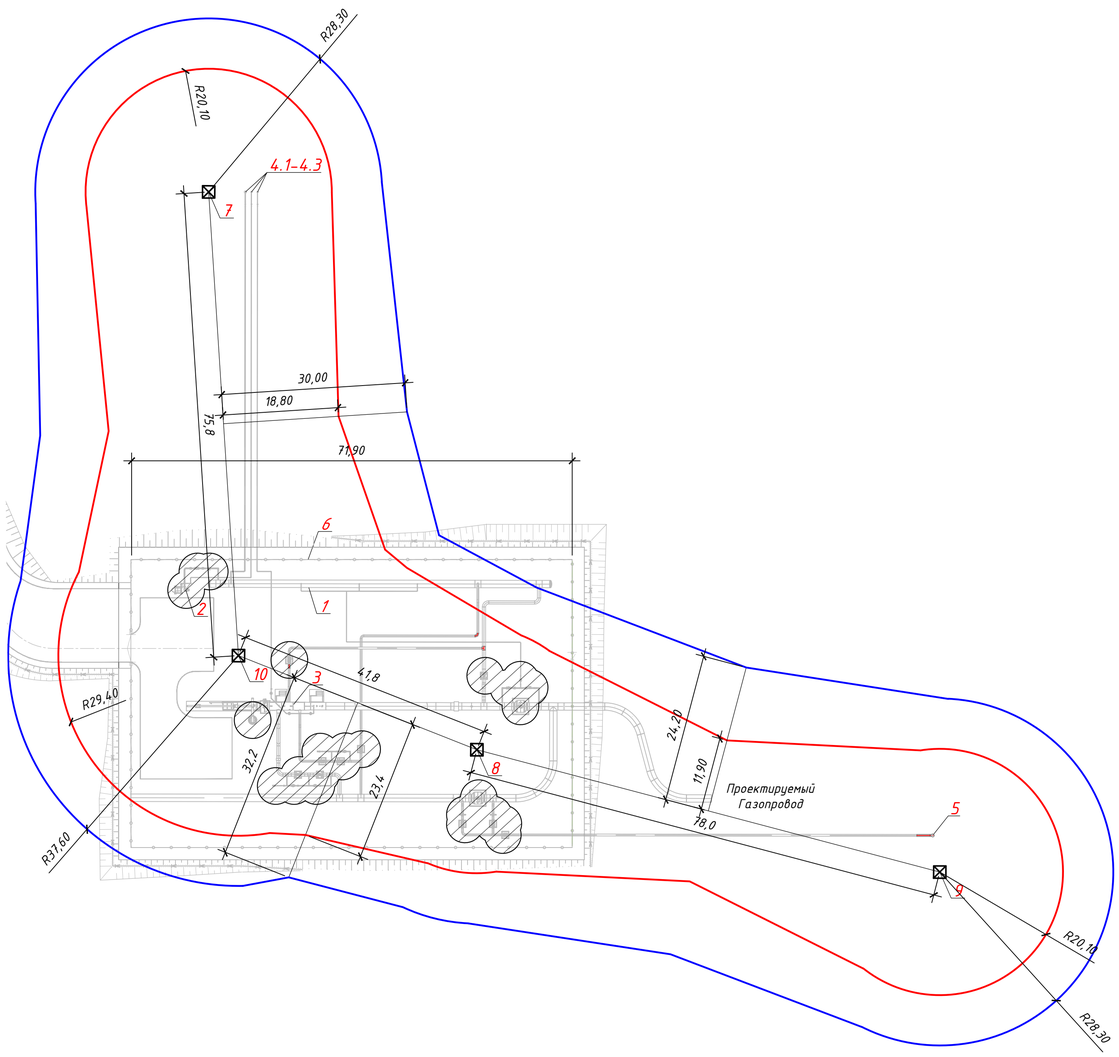

Экспликация зданий и сооружений

Номер на плане	Наименование	Примечание
1	Коллектор-сборник продуктов очистки (DN1200, V=60м3)	
2	Разделитель (V=0,4 м3)	
3	Камера приема пуска СОД D11 DN1200	
4.1-4.3	Свеча рассеивания	
5	Свеча рассеивания	
6	Сетчатое ограждение	
7	Молниеотвод МЖ-24.3	
8	Молниеотвод МЖ-24.3	
9	Молниеотвод МЖ-24.3	
10	Прожекторная мачта ПМЖ-22.8	

Зона защиты двойного стержневого молниеотвода

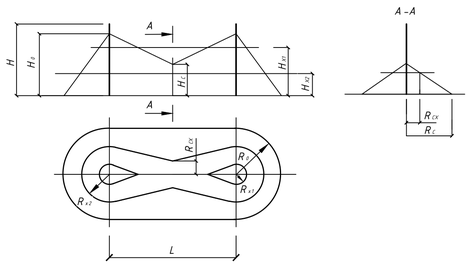

1-й молниеотвод	2-й молниеотвод	L	h1	h2	hx	Rx1	Rx2	Rcx
Для высоты защищаемых объектов не более 10 м.								
ПМ 7	ПМ 10	75,8	24,3	30,5	5,0	28,3	37,6	30,0
ПМ 7	ПМ 10	75,8	24,3	30,5	10,0	20,1	29,4	18,8
ПМ 10	ПМ 8	41,8	30,5	24,3	5,0	37,6	28,3	32,2
ПМ 10	ПМ 8	41,8	30,5	24,3	10,0	29,4	20,1	24,4
ПМ 8	ПМ 9	78	24,3	24,3	5,0	28,3	28,3	24,2
ПМ 8	ПМ 9	78	24,3	24,3	10,0	20,1	20,1	11,9

Условные обозначения

- зона молниезащиты на высоте 5 м
- зона молниезащиты на высоте 10 м
- границы взрывоопасных зон B-Ir (согласно ПУЭ Р4э) сферы радиусом 3 м

Примечания

1. Размеры зон молниезащиты построены в соответствии с РД 34.21.122-87 для зоны Б и II категории молниезащиты.
2. Высота проектируемого прожекторной мачты ПМ 10 (типа ПМЖ-22,8) составляет 30,5 м, высота молниеприемника ПМ 7, ПМ 8, ПМ 9 (Молниеотвод МЖ-24,3) составляет 24,3 м.
3. Материалы заземлителей молниеотводов учтены на чертеже заземления.
4. Класс взрывоопасной зоны согласно ПУЭ - В-Ir.
5. Координаты прожекторных мачт с молниеотводами - согласно разбивочного плана.

Рев.	Дата	Назначение ревизии	Проверил	Утвердил
A1	29.09.2026	Выпущено для строительства		
R1	28.08.2026	Выпущено для рассмотрения		

ЗАКАЗЧИК: | ГЕНЕРАЛЬНЫЙ ПОДРЯДЧИК: | ПОДРЯДЧИК: | ГЕНЕРАЛЬНЫЙ ПРОЕКТИРОВЩИК: EAST WEST ENGINEERING

EWE0426-MGL1-ELE-054-DRW-690402-A1

«СТРОИТЕЛЬСТВО НОВЫХ НИТОК (УЧАСТКОВ) ГАЗОПРОВОДОВ «ГАЗЛИ - САРИМОЙ» И «АКЧАЛОК - ГАЗЛИ - НУКУС» ОБЩЕЙ ПРОТЯЖЕННОСТЬЮ НЕ МЕНЕЕ 275 КМ».

Изм.	Кол. уч.	Лист.	№док.	Подп.	Дата
ГИП		Кирпичников С.			09.2026
Нач.отд.		Гимранов Т.			09.2026
Исполн.		Пац В.			09.2026
Н. контр.		Кирпичников С.			09.2026

ГАЗОПРОВОД «ГАЗЛИ-САРИМОЙ» (54 КМ)
Площадка ЧЗПОУ.
Внутриплощадочные коммуникации

Молниезащита. План.

Стадия	Лист	Листов
РД	1	1

ООО "EAST-WEST Engineering"
г. Ташкент 2026г.

Взам. инв. №
Подпись и дата
Инв.№ подл.

Формат А1