План (1:500)

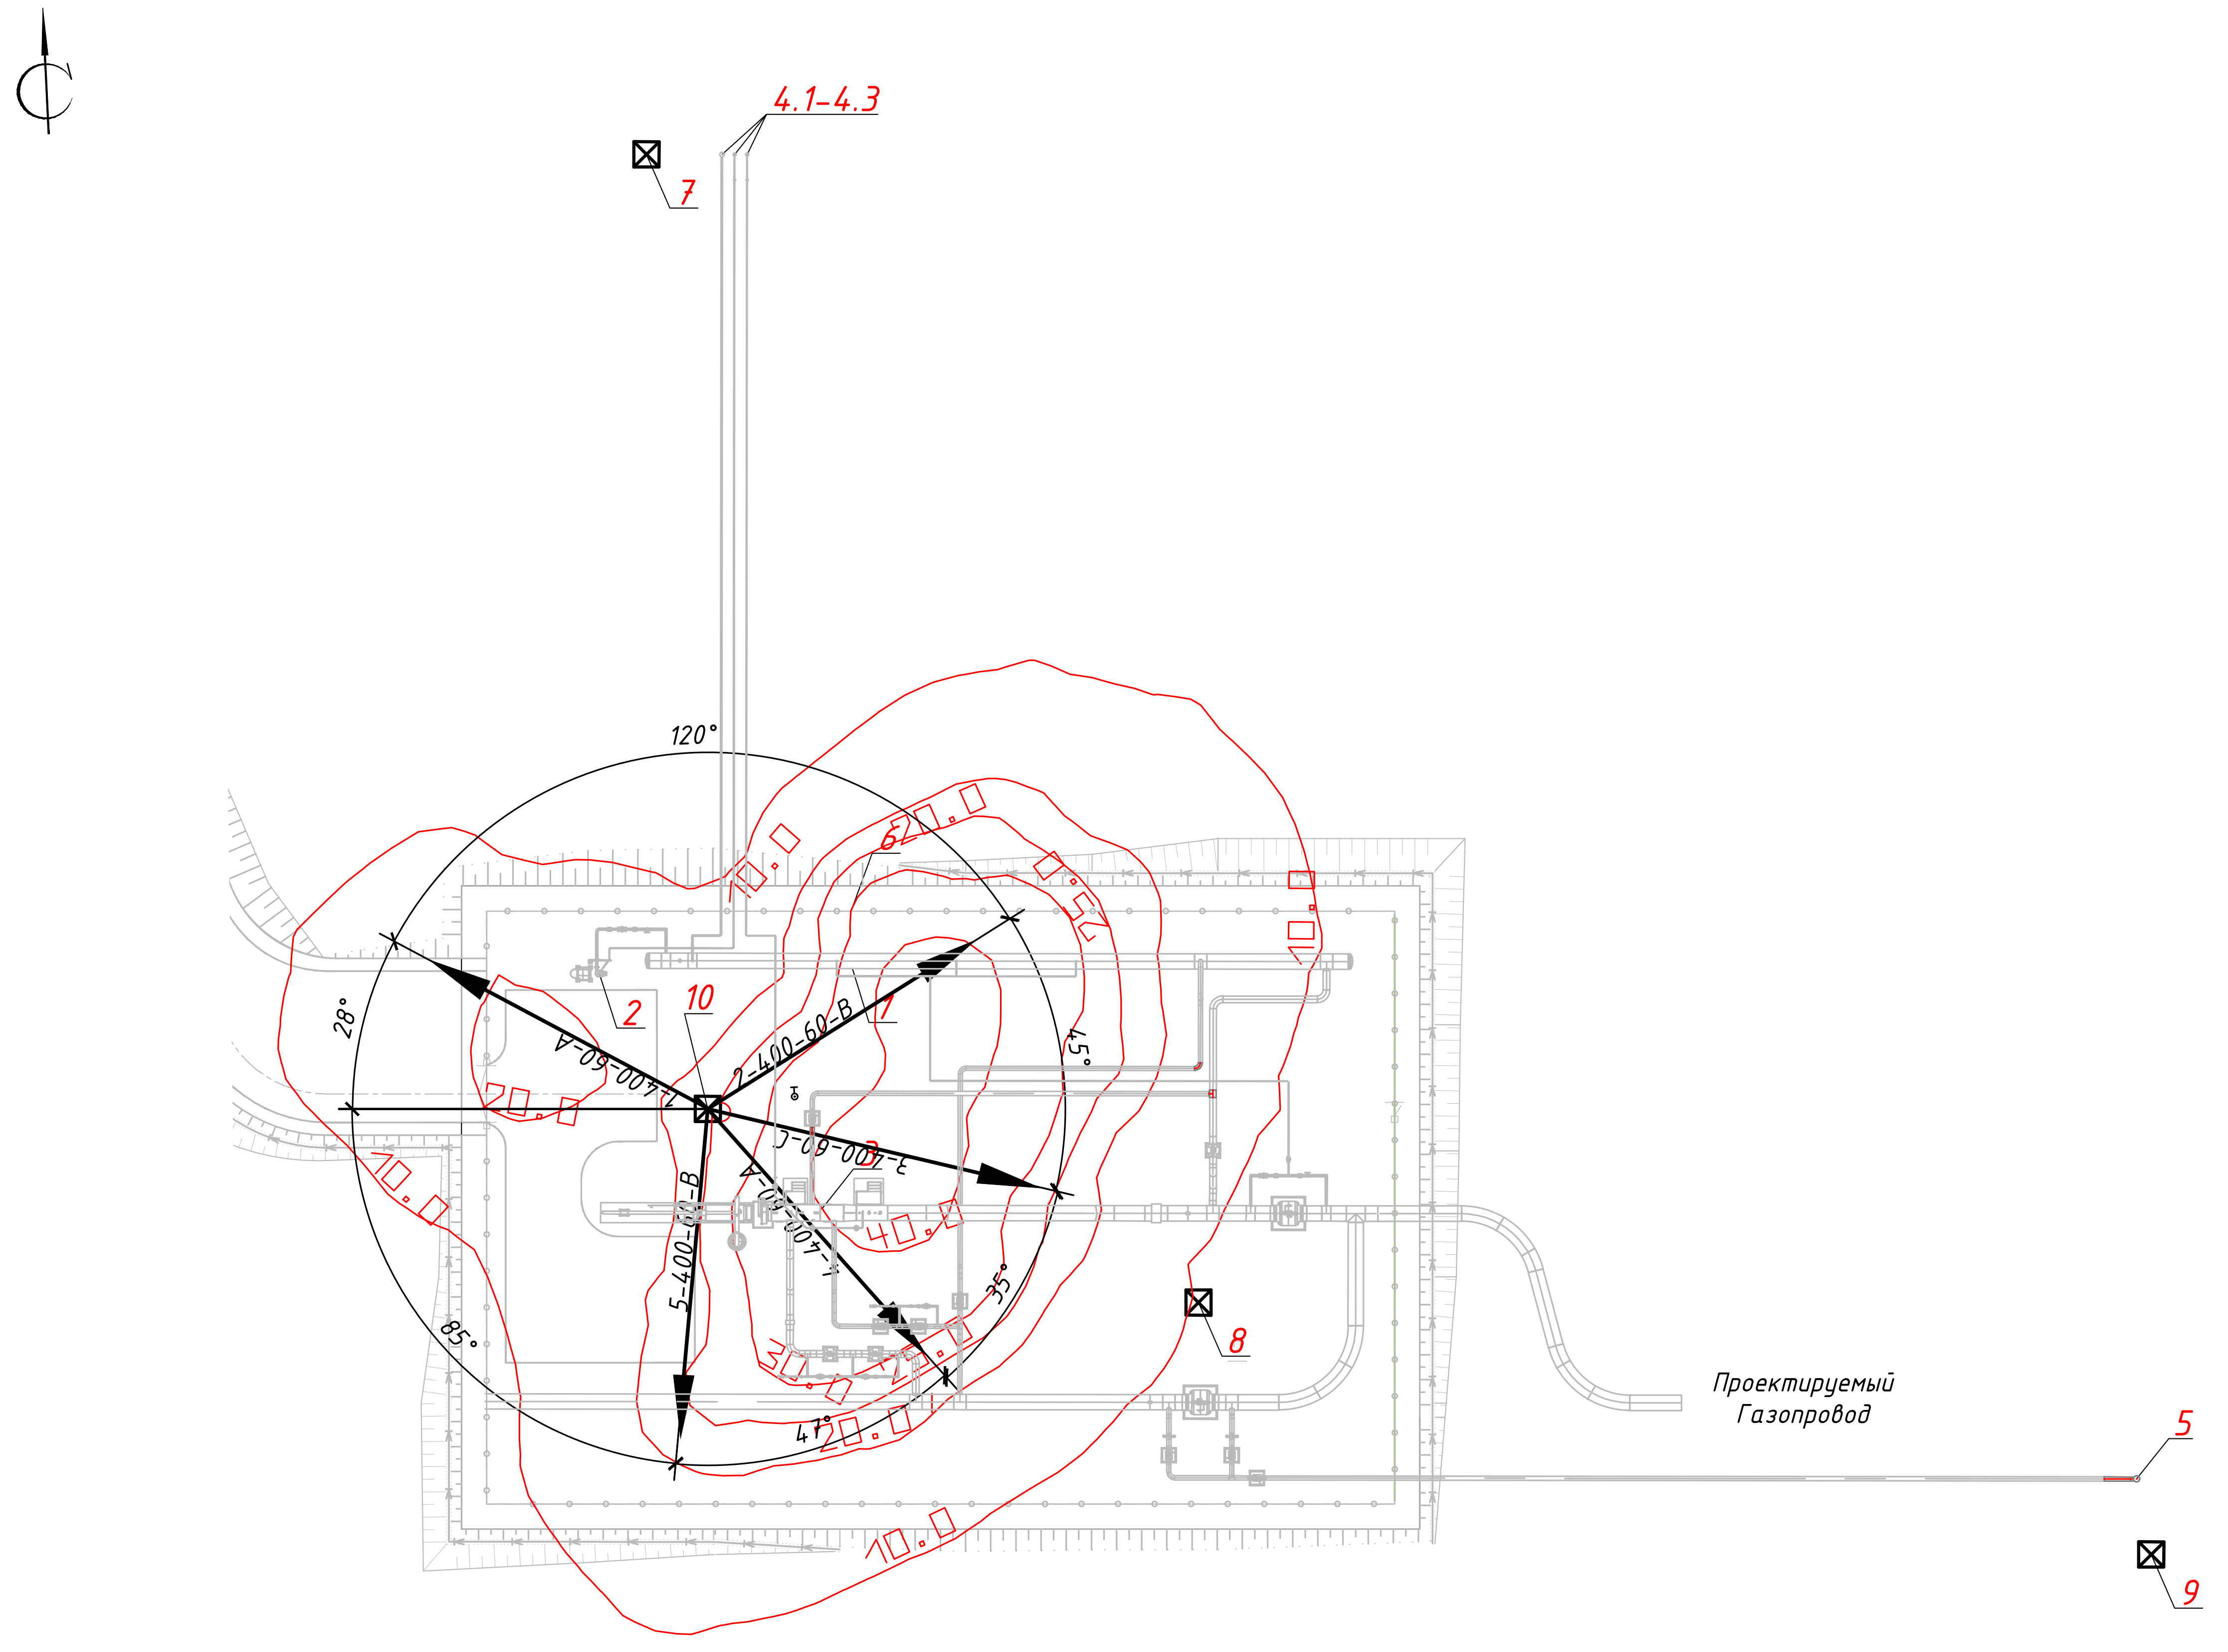
С
4.1-4.3
7
120°
28°
45°
35°
85°
47°
2
10
1
6
3
8
5
9
1-400-60-A
2-400-60-B
3-400-60-C
4-400-30-A
5-400-60-B
10.0
20.0
25.0
30.0
40.0
Проектируемый
Газопровод

Экспликация зданий и сооружений

Номер на плане	Наименование	Примечание
1	Коллектор-сборник продуктов очистки (DN1200, V=60м3)	
2	Разделитель (V=0,4 м3)	
3	Камера приема пуска СОД D11 DN1200	
4.1-43	Свеча рассеивания	
5	Свеча рассеивания	
6	Сетчатое ограждение	
7	Молниеотвод МЖ-24.3	
8	Молниеотвод МЖ-24.3	
9	Молниеотвод МЖ-24.3	
10	Прожекторная мачта ПМЖ-22.8	

СПЕЦИФИКАЦИЯ МАТЕРИАЛОВ ОСВЕЩЕНИЯ

Поз	Наименование	Тип, размер	Параметры, ГОСТ, ТУ	К-во 1 мачту	Количество, всего	Масса ед., кг	Единица измерения
				ПМ 1.7			
1	Светильник общепромышенный модульный, со светодиодным источником света 230 В, 50 Гц, 400 Вт, IP66, крепление на скобе, с фотометрической кривой 60°, со световым потоком 40000 Лм	-	ТУ 3461-015-00213569-2010	5	5	10,0	компл.
2	Кабельный ввод	ВК-Н-ВЗЛ 3-М20	ПИНЮ.687153.002 ТУ IP66	3	3	0,15	шт.
3	Кабель силовой бронированный 3x4	ВБбШвнг(А)-LS	ТУ 16.К01-37-2003	95	95	0,534	м
4	Кабель 3x2,5-660	ВВГнг	ТУ 16.К01-37-2003	10	10	0,144	м
5	Металлорукав негерметичный	Р3-Ц-Х-20	ТУ 4833-019-29124208-00	10	10	0,3	м
6	Скоба	К142 У1		10	10	0,035	шт.
7	Коробка соединительная общепромышленная на 3 ввода	КС12-32-УХЛ1	ТУ 3434-001-00213569-2005	3	3	1,5	шт.
8	Короб кабельный	СП (50x25) УТ 1.5 L=2 м		21	21	3,5	шт.
9	Ящик с выключателем, предохранителями и штепсельным разъемом ЯВЗШ-21-32. Номинальный ток 32 А, номинальное напряжение 220 В, однофазный, 2-полюсный (2P+PE), однофидерный (однонаправленный). Степень защиты IP54	ЯВЗШ-21-32	32 А, 220 В, IP54,	1	1	9,2	компл.
10	Полоса для крепления щита	4x40, L=0,5 м		2	2	0,63	шт.
11	Труба	32x3,2	ГОСТ 3262-75	2	2	3,09	м

Примечания:
1. Условные обозначения по ГОСТ 21.607-2014.
2. Нормируемая освещенность для площадочных проездов и проходов принята 4 Лк согласно КМК 2.01.05-98.
3. Наружное освещение площадки узла замера газа выполнено прожекторами со светодиодными источниками света мощностью 400 Вт, расположенными на одной прожекторной мачте типа ПМЖ (серия 3.407.9-172). Координаты прожекторных мачт согласно разбивочного плана.
4. Питающие кабели прожекторов предусмотерны на чертеже от СТП РУ-0.4 кВ "Электроснабжение 0-54 км".
5. Заземление прожекторных мачт и материалы предусмтрены на чертеже "Заземление. План. Спецификация".
6. Кабель питания прожекторных мачт проложить на протяжении 10 метров около молниеотвода, в трубе по траншее согласно ПУЭ п.4.2.132.
7. Прожекторы подключить так, что бы распределить нагрузку равномерно по фазам. Кабель между щитком и клеммной коробкой на вертикальном участке (по всей высоте) защитить коробом СП (50x25) от наведения потенциала при прохождении тока молнии, а также для механической защиты.
8. Прожекторы и клеммные коробки на отм. +23,500 заземляются при помощи PE жилы питающего кабеля.
9. Расчет освещенности выполнен в программном комплексе Dialux с применением технических данных от завода-изготовителя

Схема сети освещения

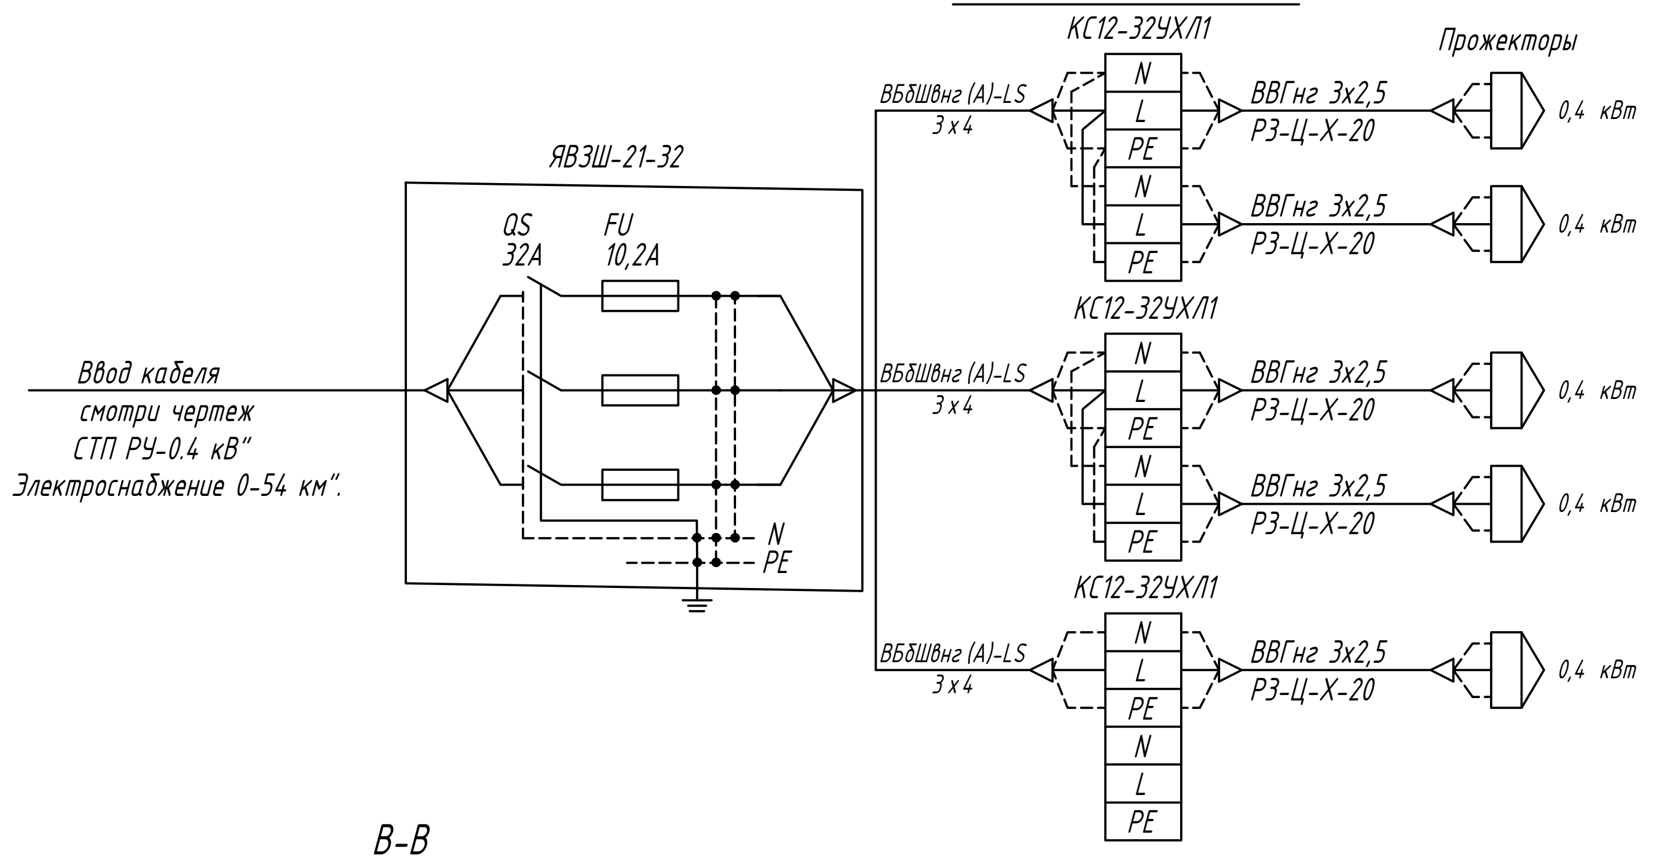
КС12-32УХЛ1
Прожекторы
ВБбШвнг(А)-LS
3x4
N
L
PE
ВВГнг 3x2,5
Р3-Ц-Х-20
0,4 кВт
ЯВЗШ-21-32
QS
32А
FU
10,2А
Ввод кабеля
смотри чертеж
СТП РУ-0.4 кВ"
Электроснабжение 0-54 км".
N
PE

Б

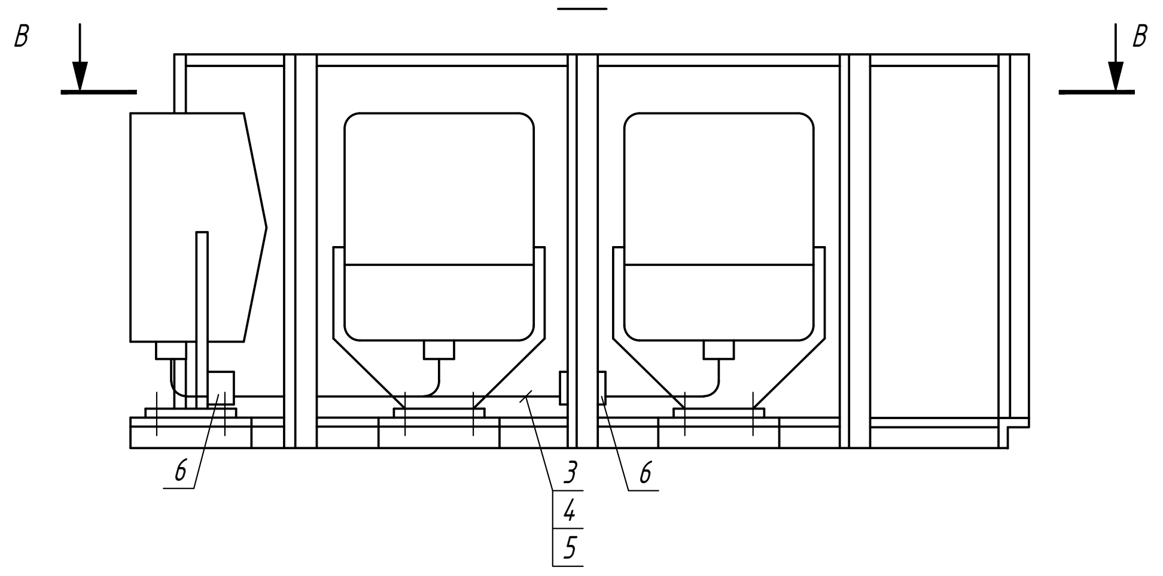

В-В

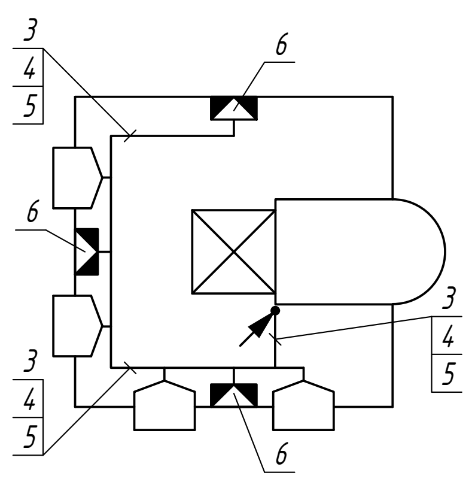
3
4
5
6
6
3
4
5
3
4
5
6

Условные обозначения

- Прожекторная мачта №1.6 с 4-ю прожекторами установленными на отм. +23,400.

1-400-30-А - Номер прожектора-мощнотсть прожектора-угол наклона относительно горизонта-фаза сети к которой подключается прожектор

+10.0 - Изолинии освещенности, люкс.

А

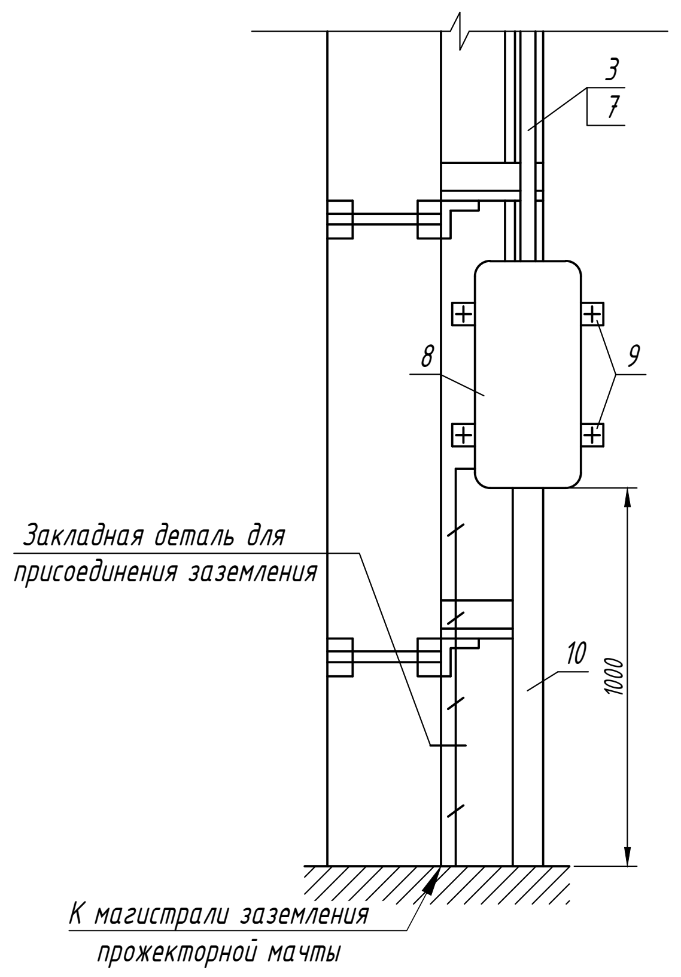
3
7
8
9
10
1000
Закладная деталь для
присоединения заземления
К магистрали заземления
прожекторной мачты

ПМЖ-22,8 (ПМ 10)

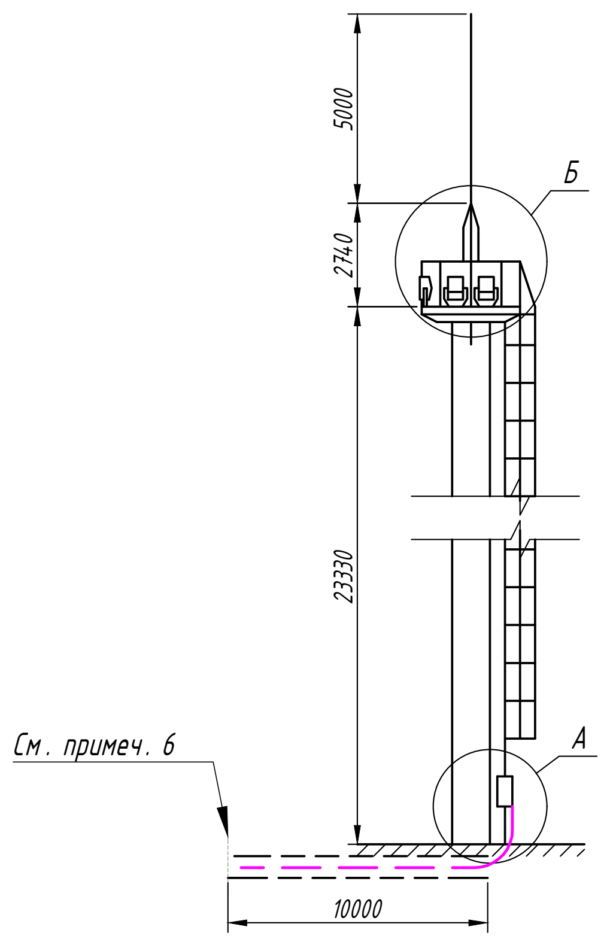
5000
2740
23330
Б
А
См. примеч. 6
10000

Рев.	Дата	Назначение ревизии	Проверил	Утвердил
A1	29.09.2026	Выпущено для строительство		
R1	28.08.2026	Выпущено для рассмотрения		

ЗАКАЗЧИК: UTG UZTRANSGAZ
ГЕНЕРАЛЬНЫЙ ПОДРЯДЧИК: UET UZBEKENERGOTAMIR
ПОДРЯДЧИК: PBG Pro Build Generation
ГЕНЕРАЛЬНЫЙ ПРОЕКТИРОВЩИК: EAST WEST ENGINEERING

EWE0426-MGL1-ELE-054-DRW-690403-A1

«СТРОИТЕЛЬСТВО НОВЫХ НИТОК (УЧАСТКОВ) ГАЗОПРОВОДОВ «ГАЗЛИ - САРИМОЙ» И «АКЧАЛОК - ГАЗЛИ - НУКУС» ОБЩЕЙ ПРОТЯЖЕННОСТЬЮ НЕ МЕНЕЕ 275 КМ».

Изм.	Кол. уч.	Лист.	№док.	Подп.	Дата
ГИП		Кирпичников С.			09.2026
Нач.отд.		Гимранов Т.			09.2026
Исполн.		Пац В.			09.2026
Н. контр.		Кирпичников С.			09.2026

ГАЗОПРОВОД «ГАЗЛИ-САРИМОЙ» (54 КМ)
Площадка УЗПОУ.
Внутриплощадочные коммуникации

Стадия	Лист	Листов
РД	1	1

Наружное освещение. План.
Спецификация

ООО "EAST-WEST Engineering"
г. Ташкент 2026г.

Формат А1

Взам. инв. №
Подпись и дата
Инв.№ подл.