


План (1:500)

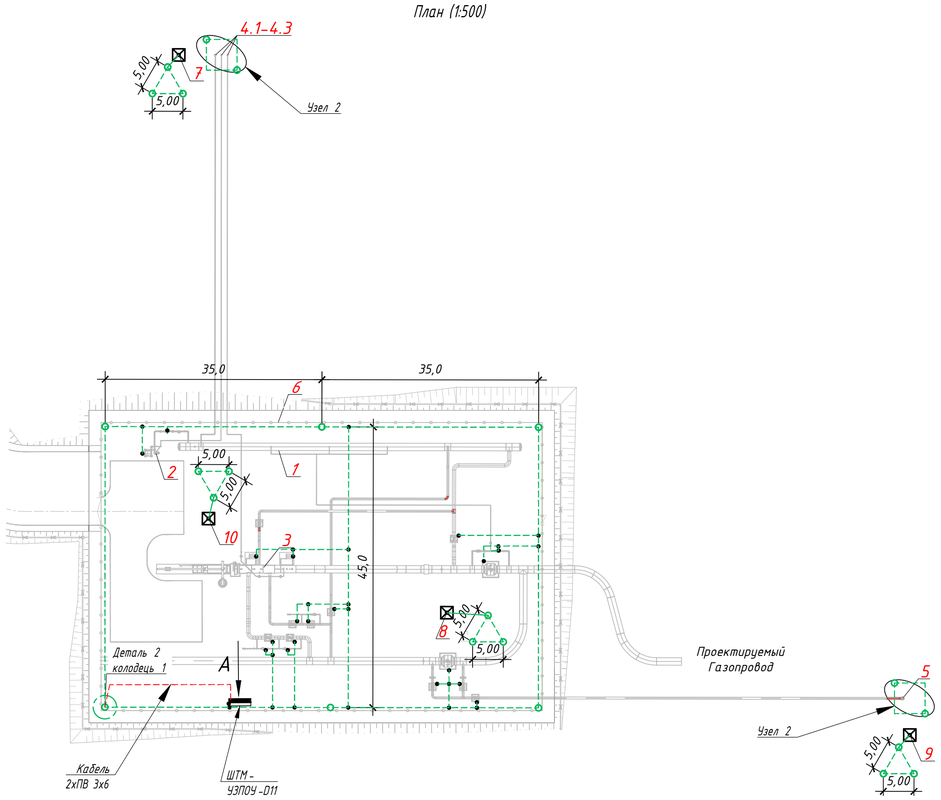

Вид по "А"
Установка шкафа под навесом Б/М

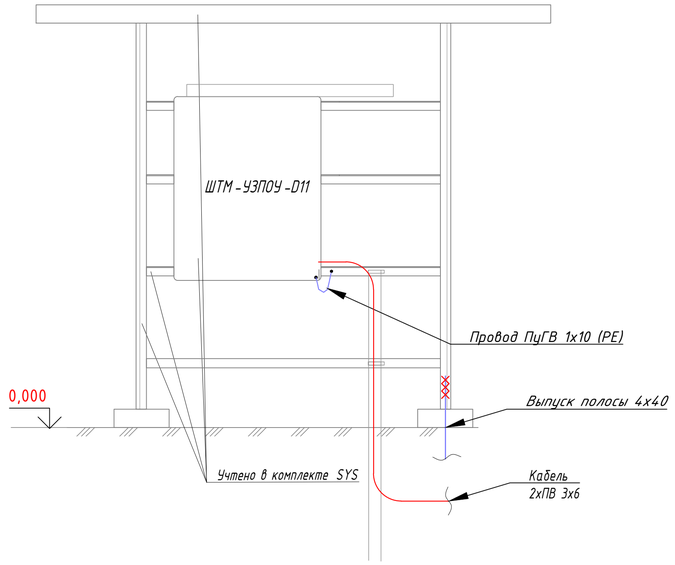

Узел 2
Установка разрядника

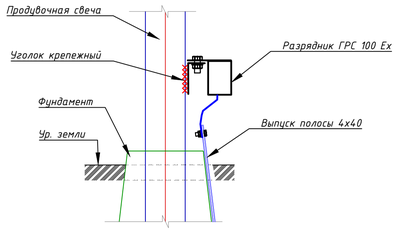


Экспликация зданий и сооружений

Номер на плане	Наименование	Примечание
1	Коллектор-сборник продуктов очистки (DN1200, V=60м3)	
2	Разделитель (V=0,4 м3)	
3	Камера приема пуска СОД D11 DN1200	
4.1–4.3	Свеча рассеивания	
5	Свеча рассеивания	
6	Сетчатое ограждение	
7	Молниеотвод МЖ–24.3	
8	Молниеотвод МЖ–24.3	
9	Молниеотвод МЖ–24.3	
10	Прожекторная мачта ПМЖ–22.8	

СПЕЦИФИКАЦИЯ ОБОРУДОВАНИЯ И МАТЕРИАЛОВ

Поз.	Обозначение (код)	Наименование	Кол.	Масса ед., кг	Примечание
1	ГОСТ 103–2006/3 СП ГОСТ 535–2005	Полоса стальная 4 х 40	580	1,26	м
2	ГОСТ 2590–88/09Г 2 Д ГОСТ 535–2005	Круг стальной Ф16, L=3 м	22	1,60	м
3	ТМЛ 6–5–4 ГОСТ 7386–80	Кабельный наконечник для медного провода сечением 6 мм² луженый под опрессовку	40	0,0039	шт / кг
4	ГОСТ 6323–79*	ПВ 3 х 6 – Провод сечением 6 мм² желто–зеленого цвета	35	0,07	м
5	ТУ 3428–002–79740390–2007	Разрядник ГРС 100 Ex	4	0,45	шт
6	ГОСТ Р МЭК 62561.1–2014 GL–11404	Колодец инспекционный для заземления	1	1,06	шт
7	ГОСТ 15836–79	Мастика изоляционная битумно–резиновая, марки МБР–90	1		кг
8	ТУ 102–340–83	Грунтовка ГТ–760 ИН	1		кг


Узел 1
Установка перемычки заземления

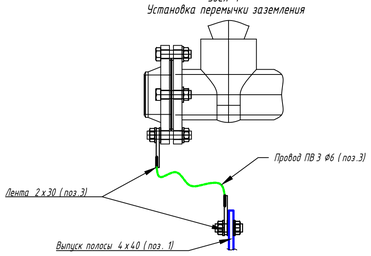

Условные обозначения

- Горизонтальный заземлитель – полоса 4 х 40 прокладываемая горизонтально на глубине 0,7 м
- Вертикальный заземлитель – круг 16 длиной 3 м
- Места присоединения полосы заземления при помощи сварки

Деталь 2
Подключение кабелей функционального заземления к наружному контуру заземления

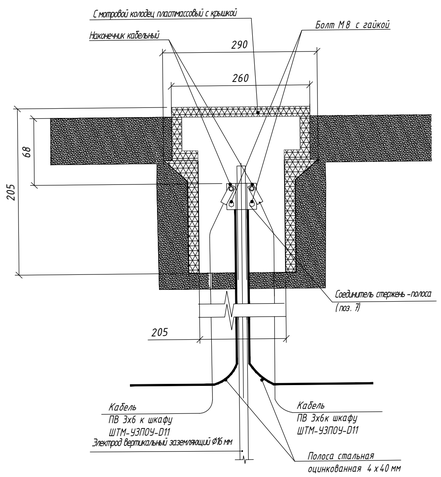

Примечания

1. Вертикальные заземлители выполнить из круглой стали d=16 мм, L=3 м и заглубить до отм. -0,4 м (верх электрода).
2. Горизонтальные заземлители из полосовой стали проложить в траншее на отм. -0,7 м, при пересечении трассы заземления с фундаментами трубопроводов или технологического оборудования так же силовыми кабелями обойти фундамент на расстоянии 0,9 м.
3. Сопротивление контура заземления должно быть не более 4 Ом. При невозможности достичь нормируемого сопротивления контура количеством вертикальных заземлителей указных на чертеже, необходимо увеличить количество и длину вертикальных заземлителей.
4. Горизонтальную полосу заземления соединить сваркой с вертикальными заземлителями и покрыть в месте сварки слоем мастики изоляционной битумно–резиновой, марки МБР–90, ГОСТ 15836–79, по слою грунтовки ГТ–760 ИН.
5. Заземлить наземные фланцевые соединения трубопроводов.
6. Все приборы, коробки, шкафы КИПиА и металлические части оборудования, подлежащие защитному заземлению, присоединить к системе защитного заземления объекта в соответствии с требованиями ПУЭ, ТУ и действующих нормативных документов.
7. В соответствии с требованиями технического задания для шкафа ШТМ-УЗПОУ-D11, предусмотрена отдельная шина функционального заземления (FE) для подключения экранов контрольных и информационных кабелей.
8. Контур функционального заземления соединить с контурами заземления. Подвод к шине функционального заземления проложен кабель от наружного заземляющего устройства, выполненного в соответствии требованиям ГОСТ Р 50571.5.54–2013, ПУЭ РУз.
9. Сварные соединения заземлителей обработать антикоррозийной защитой (в два слоя)

А1	29.09.2026	Выпущено для строительства		
R1	28.08.2026	Выпущено для рассмотрения		
Рев.	Дата	Назначение ревизии	Проверил	Утвердил

ЗАКАЗЧИК: UTG UZTRANSGAZ

ГЕНЕРАЛЬНЫЙ ПОДРЯДЧИК: UET

ПОДРЯДЧИК: PBG

ГЕНЕРАЛЬНЫЙ ПРОЕКТИРОВЩИК: EAST WEST ENGINEERING

Изм.	Кол. уч.	Лист.	№док.	Подп.	Дата
ГИП		Кирпичников С.			09.2026
Нач.отд.		Гимранов Т.			09.2026
Исполн.		Пац В.			09.2026
Н. контр.		Кирпичников С.			09.2026

EWE0426-MGL1-ELE-054-DRW-690404-A1

«СТРОИТЕЛЬСТВО НОВЫХ НИТОК (УЧАСТКОВ) ГАЗОПРОВОДОВ «ГАЗЛИ – САРИМОЙ» И «АКЧАЛОК – ГАЗЛИ – НУКУС» ОБЩЕЙ ПРОТЯЖЕННОСТЬЮ НЕ МЕНЕЕ 275 КМ».

ГАЗОПРОВОД «ГАЗЛИ–САРИМОЙ» (54 КМ)
Площадка УЗПОУ.
Внутриплощадочные коммуникации

Заземление. План. Спецификация

Стадия	Лист	Листов
РД	1	1

ООО "EAST-WEST Engineering" г. Ташкент 2026г.

Взам. инв. №

Подпись и дата

Инв.№ подл.

Формат А1