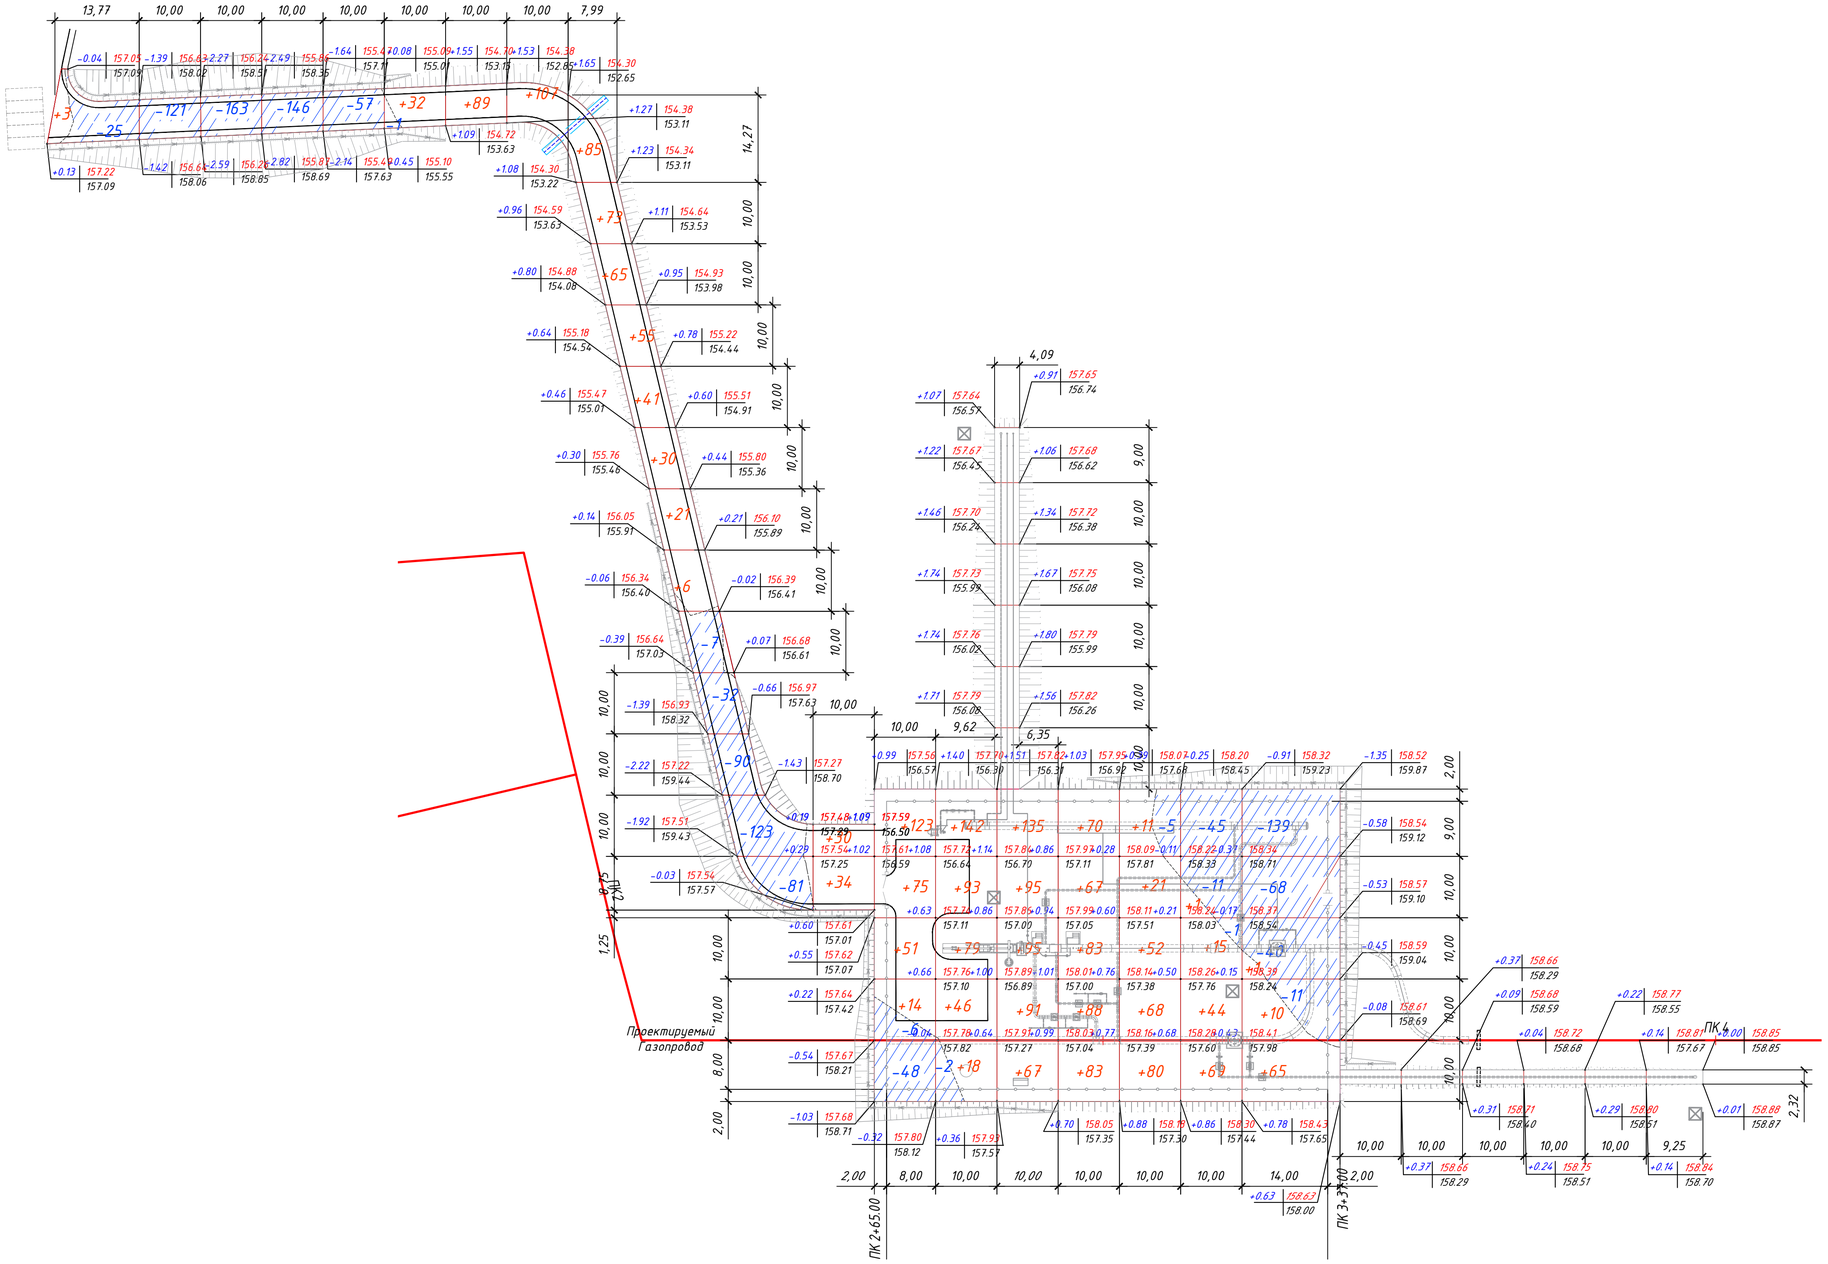


Итого,м3																											Всего,м3	
	Насыпь (+)	+3	--	--	--	--	--	+32	+89	+107	+249	+139	+6	+2	+64	+263	+378	+829	+391	+232	+129	+76	+8	+5	+4	+5	+5	+2		+3018
	Выемка (-)	-1	-42	-121	-163	-146	-57	-1	--	--	--	-1	-196	-136	--	-54	-2	--	--	-5	-57	-258	--	--	--	--	--	--		+1240

Общая площадь насыпи = 4174 м2
Общая площадь выемки = 1690 м2
Общая площадь 0-области = 31 м2
Общая площадь картограммы = 5895 м2

Ведомость объемов земляных масс

Наименование грунта	Количество, м³		Примечание
	Насыпь (+)	Выемка (–)	
1. Грунт планировки территории	3018	1240	
2. Вытесненный грунт, в т.ч. при устройстве:			
а) автодорожных покрытий		690	
б) покрытий площадок		303	
в) водоотводной канавы		175	
г) плодородной почвы на участках насыпи			
д) плодородной почвы на участках выемки			
3. Замена растительного грунта на участках насыпи			
4. Грунт для устройства откосов насыпи	401		
5. Грунт для устройства откосов выемки		518	
6. Поправка на уплотнение	341.9		
Всего пригодного грунта	3760.9	2926	
7. Недостаток пригодного грунта		834.9**	
8. Плодородный грунт, всего в т.ч.:		1768.5	
а) Используемый для озеленения территории			
б) Избыток плодородного грунта	1768.5		
(рекультивация земель)			
9. Итого перерабатываемого грунта	5529.4	5529.4	

* С учетом плодородного грунта.
** В карьере.
Общая площадь картограммы = 5895 м2

Условные обозначения:

+21 — объем насыпи в м³
-48 — объем выемки в м³
-1.35 | 158.52 / 159.87 — рабочая отм. | проектная отм. / отм.сущ.рельефа
откосы насыпи
откосы выемки

Примечания:

При составлении настоящего чертежа были использованы :
1. Сетка картограммы УЗПОУ-D11 привязана линейно к пикету ПК2+65.00.
2. Сетка квадратов объёмы земляных масс разбита на ячейки размерами 10х10м.
3. Производство земляных работ вести в соответствии с требованиями КР 02.01.

Изм.	Дата	Назначение ревизии	Проверил	Утвердил
A1	02.10.2026	Выпущено для строительства		
R1	25.08.2026	Выпущено для рассмотрения		

ЗАКАЗЧИК: UTG — ГЕНЕРАЛЬНЫЙ ПОДРЯДЧИК: UET — ПОДРЯДЧИК: PBG — ГЕНЕРАЛЬНЫЙ ПРОЕКТИРОВЩИК: EAST WEST ENGINEERING

Изм.	Кол.уч.	Лист	№док.	Подпись	Дата	EWE0426-MGL1-GLT-054-DRW-690104-A1			
						«СТРОИТЕЛЬСТВО НОВЫХ НИТОК (УЧАСТКОВ) ГАЗОПРОВОДОВ «ГАЗЛИ – САРИМОЙ» И «АКЧАЛОК – ГАЗЛИ – НУКУС» ОБЩЕЙ ПРОТЯЖЕННОСТЬЮ НЕ МЕНЕЕ 275 км».			
ГИП		Кирпичников С.			10.2026	ГАЗОПРОВОД «ГАЗЛИ-САРИМОЙ» (54 км)	Стадия	Лист	Листов
Нач.отд.		Нигманова Н.			10.2026	Генеральный план и транспорт.	РД	1	1
Исполн.		Горлова О.			10.2026	Площадка УЗПОУ-D11 План земляных масс М 1:500	ООО "EAST-WEST Engineering" г. Ташкент 2026 г.		
Н.контр.		Кирпичников С.			10.2026				

Взам. инв. № | Подпись и дата | Инв.№ подл.

Формат / Format A1