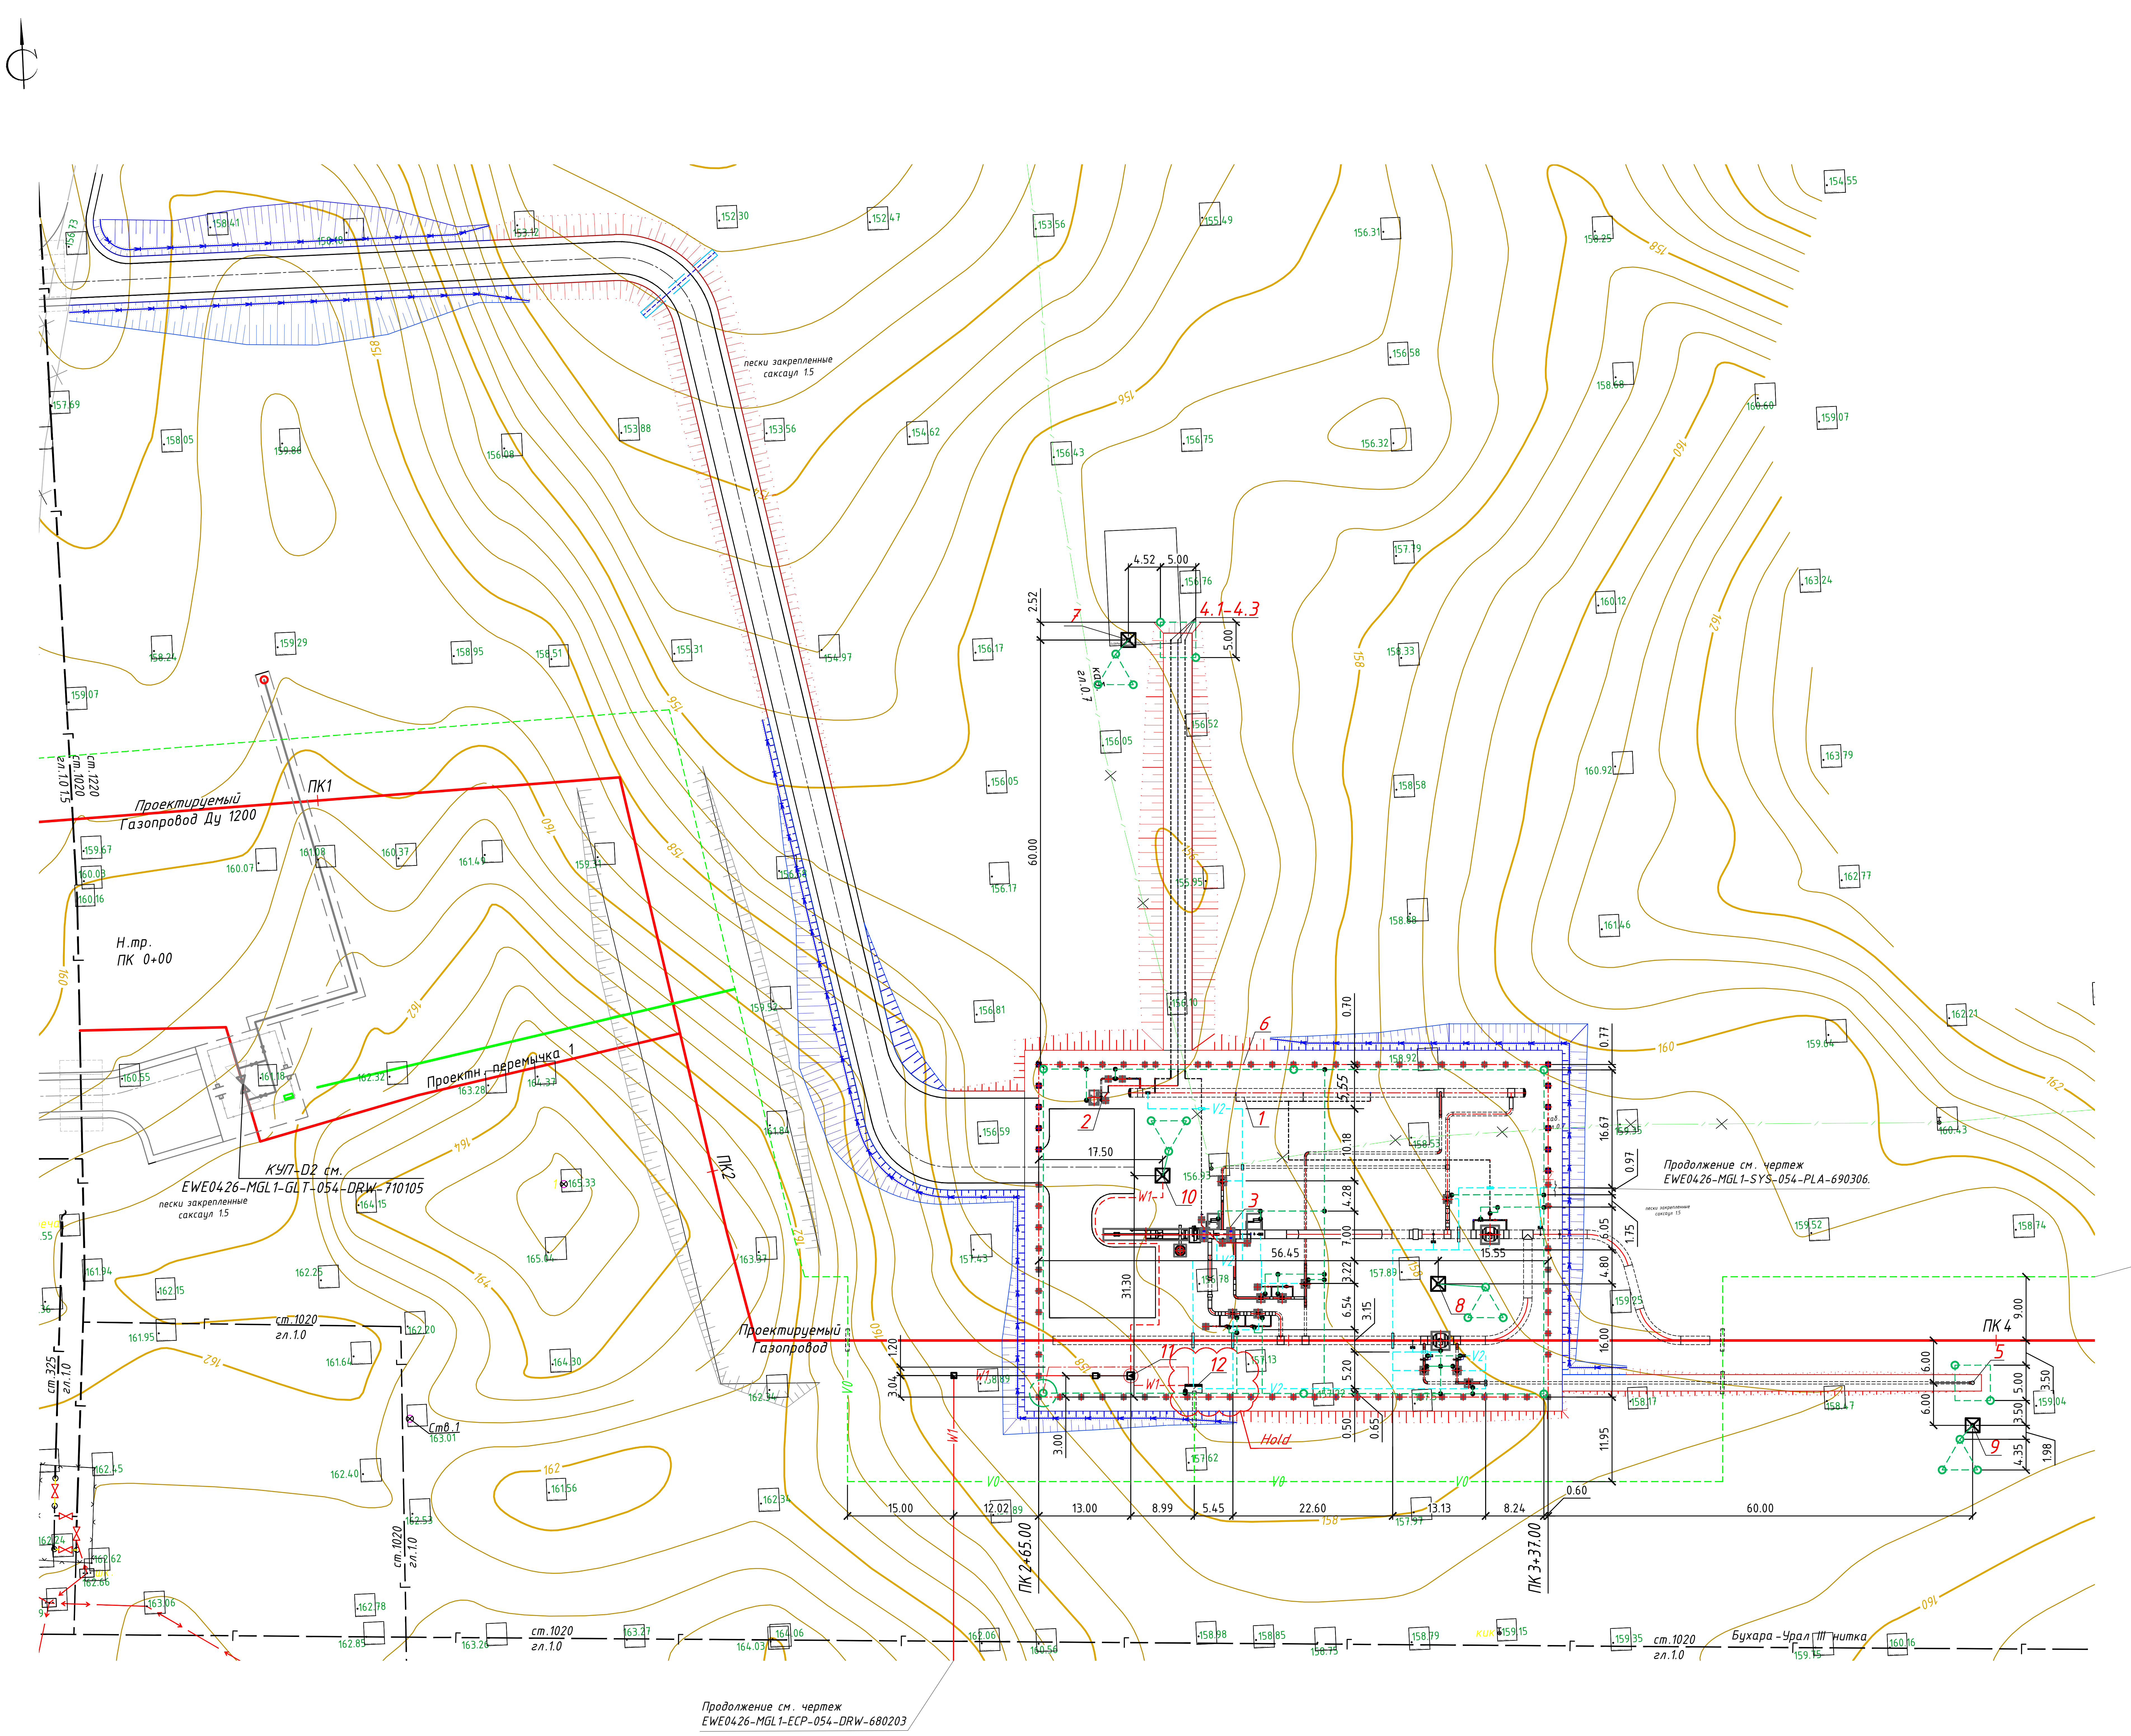

Продолжение см. чертеж
EWE0426-MGL1-ECP-054-DRW-680203

Продолжение см. чертеж
EWE0426-MGL1-COS-054-PLA-670103

Экспликация зданий и сооружений

Номер на плане	Наименование	Примечание
1	Коллектор-сборник продуктов очистки (DN1200, V=60м3)	
2	Разделитель (V=0,4 м3)	
3	Камера приема пуска СОД D11 DN1200	
4.1-43	Свеча рассеивания	
5	Свеча рассеивания	
6	Сетчатое ограждение	
7	Молниеотвод МЖ-24.3	
8	Молниеотвод МЖ-24.3	
9	Молниеотвод МЖ-24.3	
10	Прожекторная мачта ПМЖ-22.8	
11	СТП-10/6/0,23 кВ	
12	Шкаф телемеханики (ШТМ)	

Условные обозначения

—o—o—o—	Ограждение
	Калитка
– – – – –	Граница планировки
—г——г—	Существующий газопровод
——	Проектируемый газопровод ДУ-1200
	Существующая линия связи
×—×—×	Перекладка существующей линии связи
○	Вертикальный заземлитель круг 16 длиной 3м
— — —	Горизонтальный заземлитель - полоса 4х40 прокладываемая горизонтально на глубине 0.7м
●	Места присоединения полосы заземления при помощи сварки
—·—·—	Кабель в траншее
	Стальная труба
	Шкаф телемеханики (ШТМ)
---V2---	Проектный кабель КИПиА в траншее
--V2--	Проектный кабель КИПиА в ПНД трубе
---W1----	Силовой кабель 0.23 кВ в траншее
—W1—	Воздушная линия 6 кВ
◪	Опора ВЛ 6 кВ
---V0---	Проектируемый волоконно-оптический кабель в траншее
--V0--	Проектируемый волоконно-оптический кабель в трубе

Примечания:

При составлении настоящего чертежа были использованы :
1. Материалы топографо-геодезической съемки, предоставлены АО "O'ZLITINEFTGAZ".
2. Площадка УЗПОУ привязана линейно к пикету ПК 2+65.00 газопровода Ду 1200.
3. Расстояние по горизонтали (в свету) от подземных инженерных сетей до зданий и сооружений следует принимать не менее указанных в табл.9 см. ШНК 2.09.17-21 "Проектирование генеральных планов промышленных предприятий".
4. Расположение оборудования и прокладку кабелей уточнить по месту при монтаже.
5. Данный лист смотри совместно с листами разделов PIL, PRE, ELE, STR, SYS.
6. Детальный план кранового узла см. EWE0426-MGL1-PRE-054-DRW-690203.
7. Детальный план сетей КИПиА см. EWE0426-MGL1-SYS-054-PLA-690306.
8. Детальный план сетей заземления см. EWE0426-MGL1-ELE-054-DRW-690404.
9. Детальный план ограждения см. EWE0426-MGL1-STR-054-DRW-690502
10. Место расположения шкафа телемеханики (ШТМ) габаритный размер и высотные отметки будут уточнены после получения КД.

Рев.	Дата	Назначение ревизии	Проверил	Утвердил
R1	29.09.2026	Выпущено для рассмотрения		

ЗАКАЗЧИК: UTG UZTRANSGAZ
ГЕНЕРАЛЬНЫЙ ПОДРЯДЧИК: UET UZBEKENERGOTAMIR
ПОДРЯДЧИК: PBG Pro Build Generation
ГЕНЕРАЛЬНЫЙ ПРОЕКТИРОВЩИК: EAST WEST ENGINEERING

EWE0426-MGL1-GLT-054-DRW-690105-R1

«СТРОИТЕЛЬСТВО НОВЫХ НИТОК (УЧАСТКОВ) ГАЗОПРОВОДОВ «ГАЗЛИ - САРИМОЙ» И «АКЧАЛОК - ГАЗЛИ - НУКУС» ОБЩЕЙ ПРОТЯЖЕННОСТЬЮ НЕ МЕНЕЕ 275 км».

Изм.	Кол.уч.	Лист	№ док.	Подпись	Дата
ГИП		Кирпичников С.			09.2026
Нач.отд.		Нигманова Н.			09.2026
Исполн.		Горлова О.			09.2026
Н.контр		Кирпичников С.			09.2026

ГАЗОПРОВОД «ГАЗЛИ-САРИМОЙ» (54 км)
Генеральный план и транспорт.

Стадия	Лист	Листов
РД	1	1

Площадка УЗПОУ
Сводный план инженерных сетей
М 1:500

EAST WEST ENGINEERING
ООО "EAST-WEST Engineering"
г. Ташкент 2026г.

Взам. инв. №
Подпись и дата
Инв.№ подл.

Формат / Format A4x3