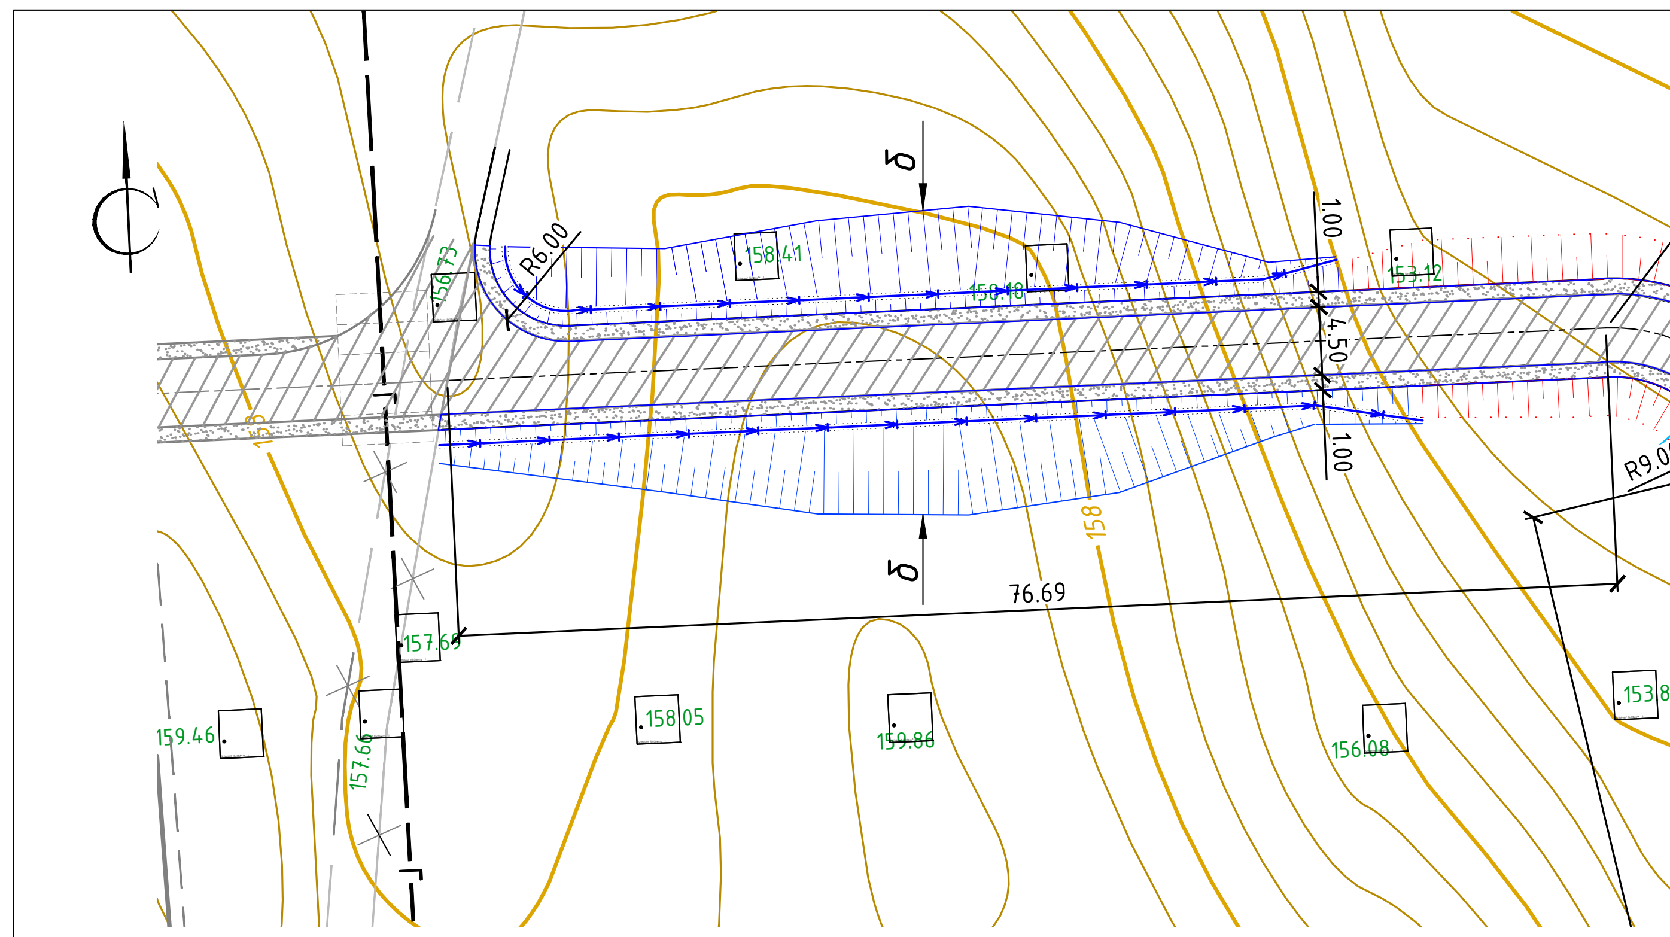

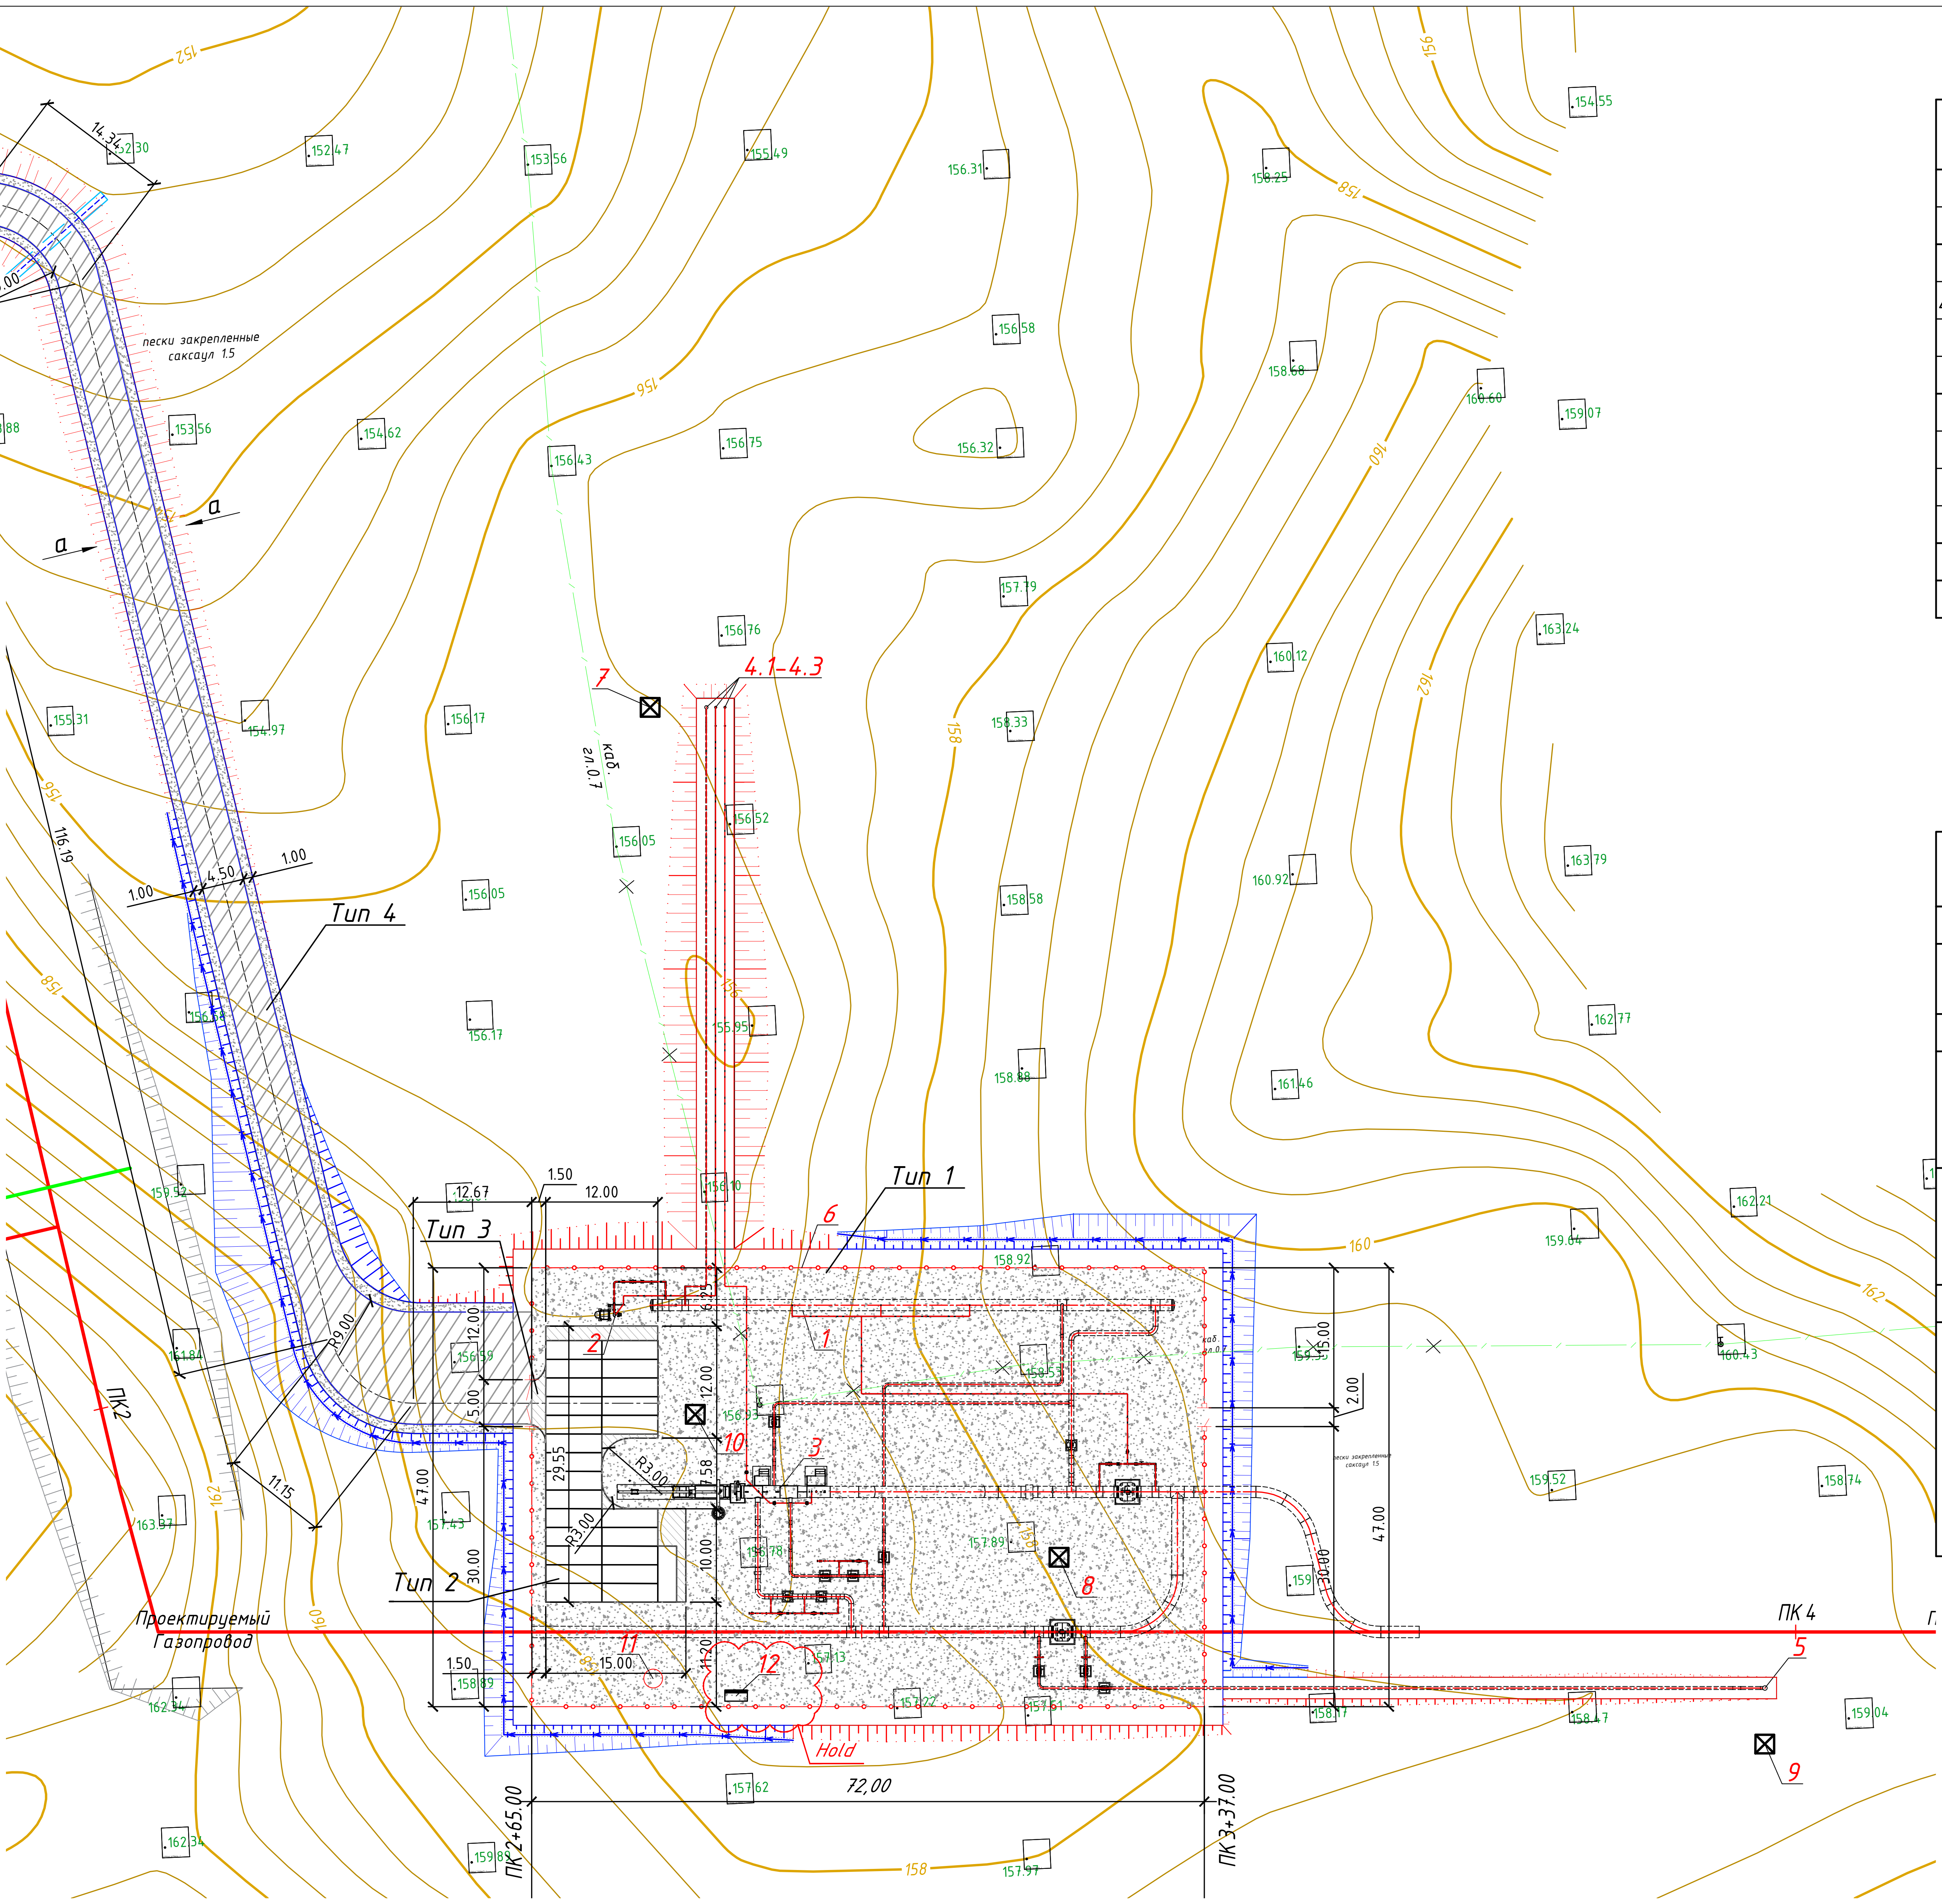

Тип 1

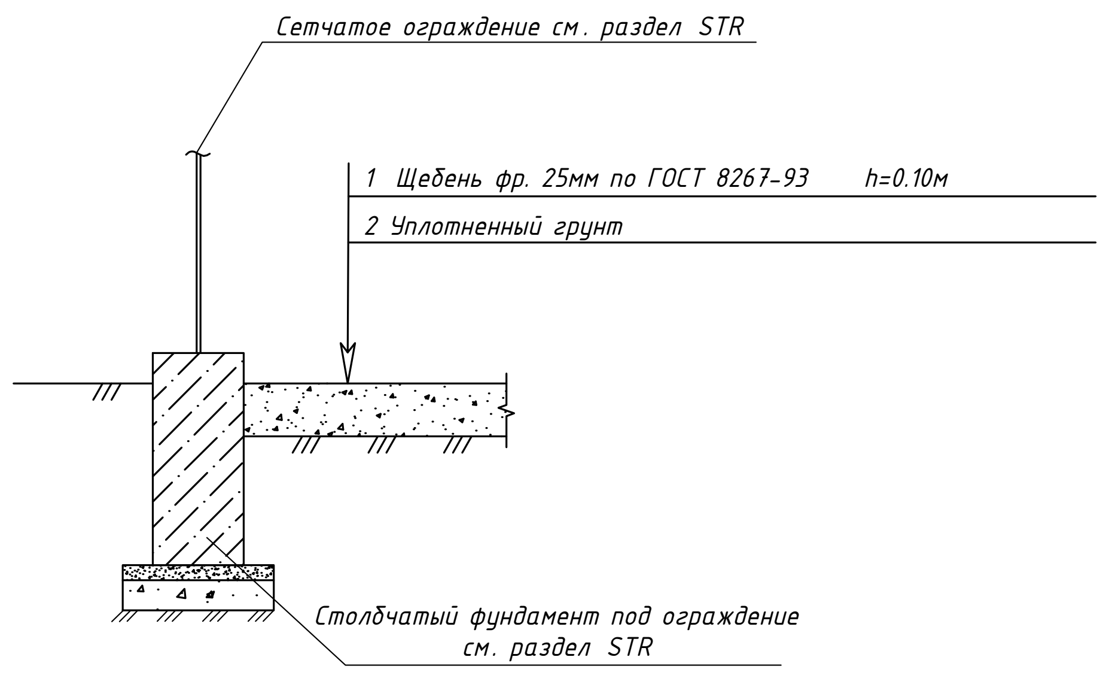
Сетчатое ограждение см. раздел STR
1 Щебень фр. 25мм по ГОСТ 8267-93 h=0.10м
2 Уплотненный грунт
Столбчатый фундамент под ограждение см. раздел STR

Тип 2

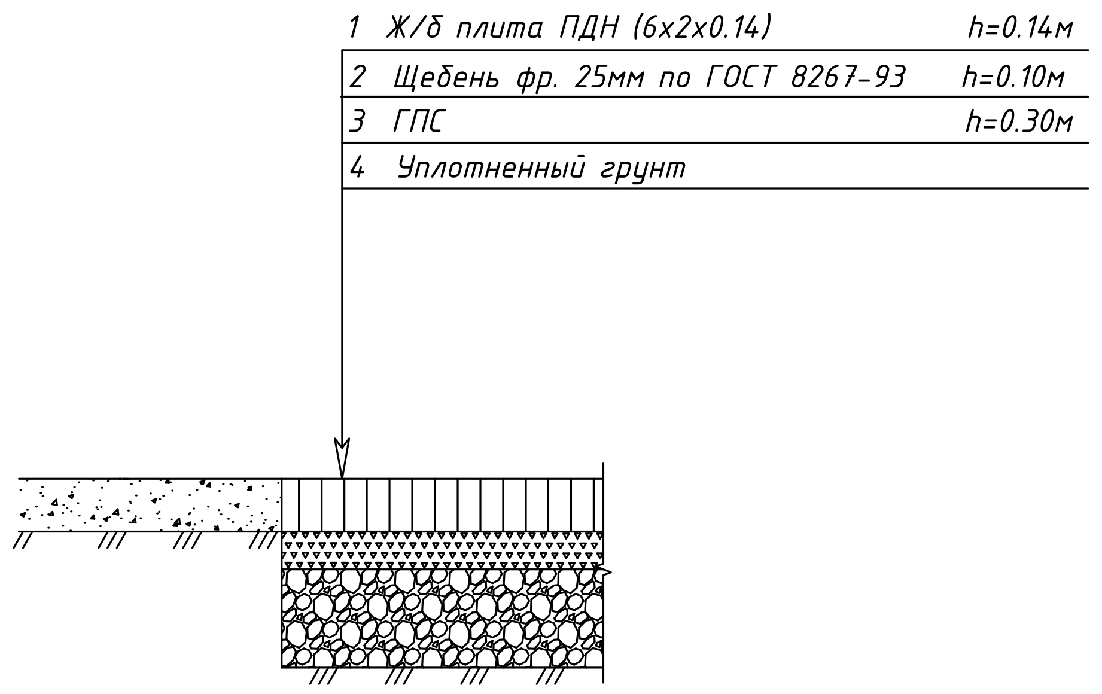
1 Ж/б плита ПДН (6х2х0.14) h=0.14м
2 Щебень фр. 25мм по ГОСТ 8267-93 h=0.10м
3 ГПС h=0.30м
4 Уплотненный грунт

Тип 3

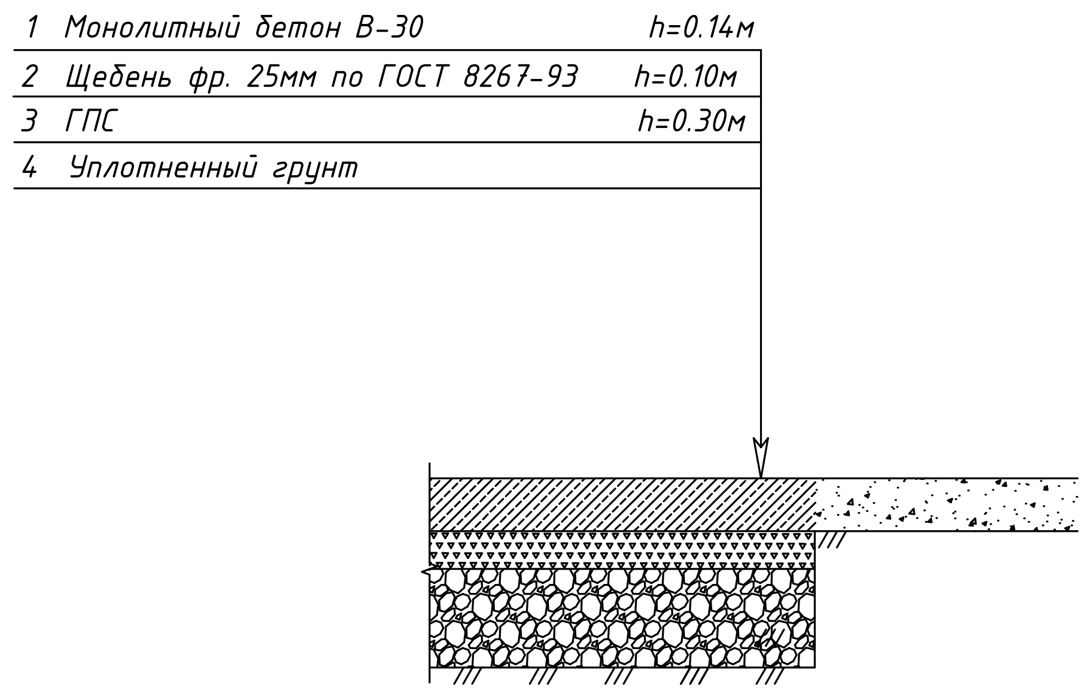
1 Монолитный бетон В-30 h=0.14м
2 Щебень фр. 25мм по ГОСТ 8267-93 h=0.10м
3 ГПС h=0.30м
4 Уплотненный грунт

Тип 4

а-а

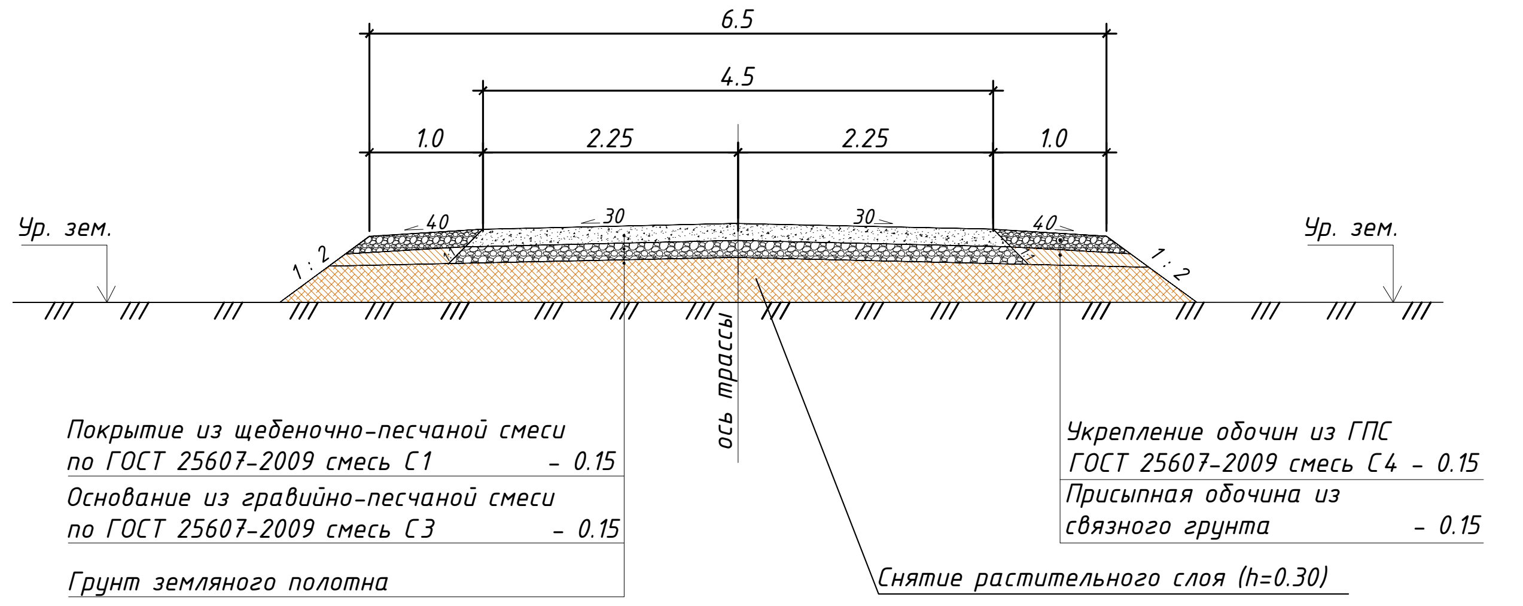
6.5
4.5
1.0
2.25
2.25
1.0
40
30
30
40
1 : 2
1 : 2
Ур. зем.
Ур. зем.
ось трассы
Покрытие из щебеночно-песчаной смеси по ГОСТ 25607-2009 смесь С1 - 0.15
Основание из гравийно-песчаной смеси по ГОСТ 25607-2009 смесь С3 - 0.15
Грунт земляного полотна
Снятие растительного слоя (h=0.30)
Укрепление обочин из ГПС ГОСТ 25607-2009 смесь С4 - 0.15
Присыпная обочина из связного грунта - 0.15

б-б

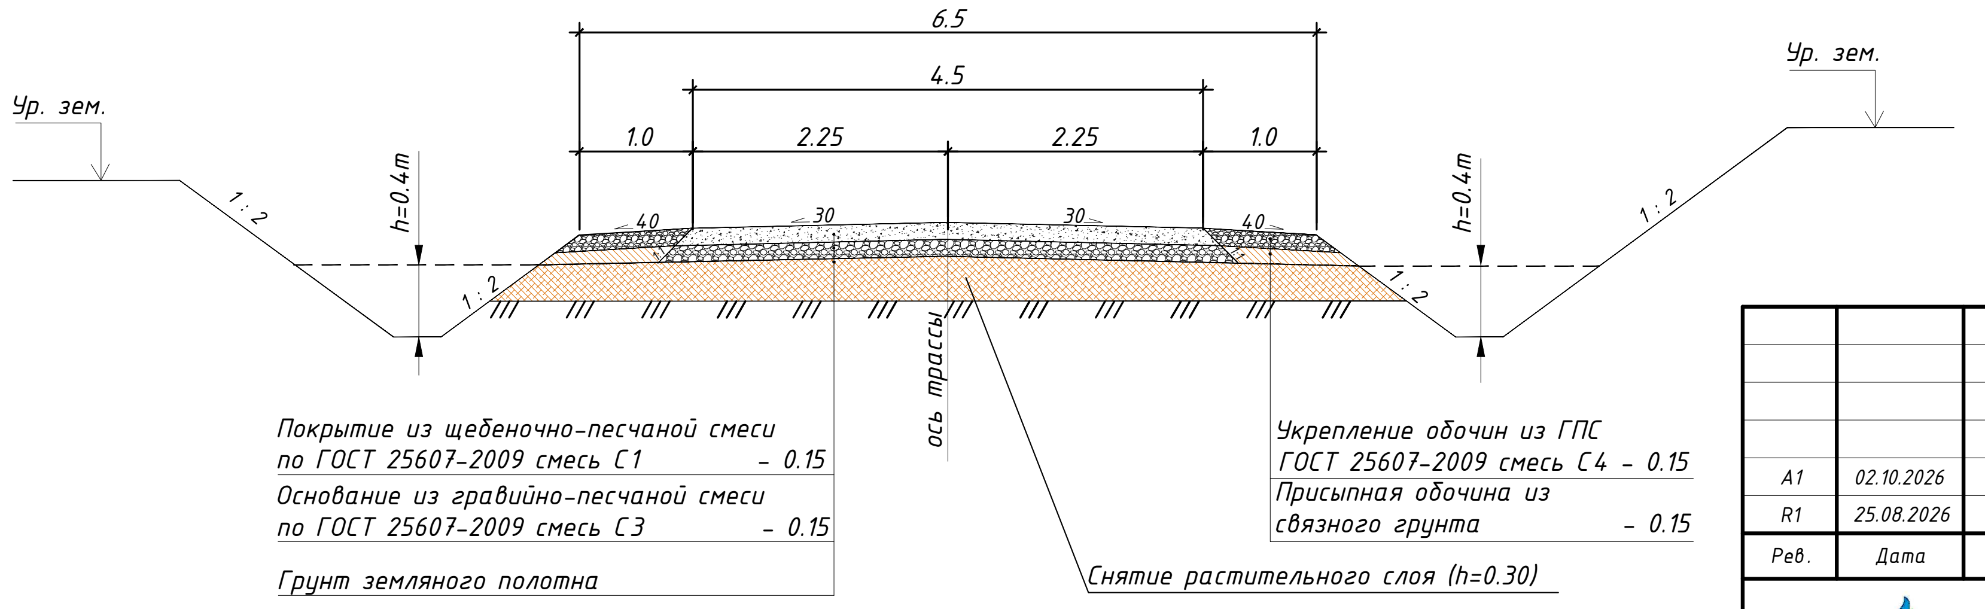
6.5
4.5
1.0
2.25
2.25
1.0
40
30
30
40
1 : 2
1 : 2
1 : 2
1 : 2
h=0.4m
h=0.4m
Ур. зем.
Ур. зем.
ось трассы
Покрытие из щебеночно-песчаной смеси по ГОСТ 25607-2009 смесь С1 - 0.15
Основание из гравийно-песчаной смеси по ГОСТ 25607-2009 смесь С3 - 0.15
Грунт земляного полотна
Снятие растительного слоя (h=0.30)
Укрепление обочин из ГПС ГОСТ 25607-2009 смесь С4 - 0.15
Присыпная обочина из связного грунта - 0.15

Экспликация зданий и сооружений

Номер на плане	Наименование	Примечание
1	Коллектор-сборник продуктов очистки (DN1200, V=60м3)	
2	Разделитель (V=0,4 м3)	
3	Камера приема пуска СОД D11 DN1200	
4.1-4.3	Свеча рассеивания	
5	Свеча рассеивания	
6	Сетчатое ограждение	
7	Молниеотвод МЖ-24.3	
8	Молниеотвод МЖ-24.3	
9	Молниеотвод МЖ-24.3	
10	Прожекторная мачта ПМЖ-22.8	
11	СТП-10/6/0,23 кВ	
12	Шкаф телемеханики (ШТМ)	

Ведомость тротуаров, дорожек и площадок

Тип	Обозначение	Наименование	Ед. изм.	Примечание
		Покрытие площадки		
1	▨	Покрытие из щебня по ГОСТ 8267-93, h=0.10	$м^2$	3032.0
		Покрытие разворотной площадки		
2	▦	Ж/б плита ПДН (6 х 2 х 0.14) h=0.14 м Щебень фр. 25мм по ГОСТ 8267-93 h=0.10 м ГПС h=0.30 м	$м^2$ шт	300.0 25
3	▨	Монолитный бетон В-30 h=0.14 м Щебень фр. 25мм по ГОСТ 8267-93 h=0.10 м ГПС h=0.30 м	$м^2$	52.0
		Покрытие подъездной дороги		
4	▨	Покрытие из щебеночно-песчаной смеси по ГОСТ 25607-2009 смесь С1 h=0,15 м Основание из гравийно-песчаной смеси по ГОСТ 25607-2009 смесь С3 h=0,15 м	$м^2$	3384.0
		Укрепление обочин из ГПС ГОСТ 25607-2009 смесь С4 h=0,15 м	$м^2$	352.0
	▭	Труба металлическая d=0.325 м	м шт	13.0 1

Примечания:

При составлении настоящего чертежа были использованы :
1. Материалы топографо-геодезической съемки, предоставлены АО "O'ZLITINEFTGAZ".
2. Система координат местная. Высотные отметки даны в Балтийской системе.
3. Размеры даны в метрах.
4. Площадка УЗПОУ-D11 привязана линейно к пикету ПК 2+65.00 газопровода Ду1200.
5. Данный лист смотри совместно с листами разделов PIL, PRE, ELE, STR, SYS.
6. Детальный план кранового узла см. EWE0426-MGL1-PRE-054-DRW-690203.
7. Hold - место расположения шкафа телемеханики (ШТМ) габаритный размер и высотные отметки будут уточнены после получения КД.

Рев.	Дата	Назначение ревизии	Проверил	Утвердил
A1	02.10.2026	Выпущено для строительства		
R1	25.08.2026	Выпущено для рассмотрения		

ЗАКАЗЧИК: UTG UZTRANSGAZ
ГЕНЕРАЛЬНЫЙ ПОДРЯДЧИК: UET UZBEKENERGOTAMIR
ПОДРЯДЧИК: PBG Pro Build Generation
ГЕНЕРАЛЬНЫЙ ПРОЕКТИРОВЩИК: EAST WEST ENGINEERING

EWE0426-MGL1-GLT-054-DRW-690106-A1

«СТРОИТЕЛЬСТВО НОВЫХ НИТОК (УЧАСТКОВ) ГАЗОПРОВОДОВ «ГАЗЛИ - САРИМОЙ» И «АКЧАЛОК - ГАЗЛИ - НУКУС» ОБЩЕЙ ПРОТЯЖЕННОСТЬЮ НЕ МЕНЕЕ 275 км».

Изм.	Кол.уч.	Лист	№ док.	Подпись	Дата
ГИП		Кирпичников С.			10.2026
Нач.отд.		Нигманова Н.			10.2026
Исполн.		Горлова О.			10.2026
Н.контр		Кирпичников С.			10.2026

ГАЗОПРОВОД «ГАЗЛИ-САРИМОЙ» (54 км)
Генеральный план и транспорт.

Стадия	Лист	Листов
РД	1	1

Площадка УЗПОУ-D11
План благоустройства территории
М 1:500

EAST WEST ENGINEERING
ООО "EAST-WEST Engineering"
г. Ташкент 2026г.

Взам. инв. №
Подпись и дата
Инв.№ подл.

Формат / Format A4x3