
ПЕРЕЧЕНЬ СВАРНЫХ ШВОВ		
№	DN	ТИП
1	1200	BUTTWELD
2	1200	BUTTWELD
3	1200	BUTTWELD
4	1200	FIELDWELD
5	1200	BUTTWELD
6	1200	BUTTWELD
7	1200	FIELDWELD
8	1200	FIELDWELD
9	1200	FIELDWELD

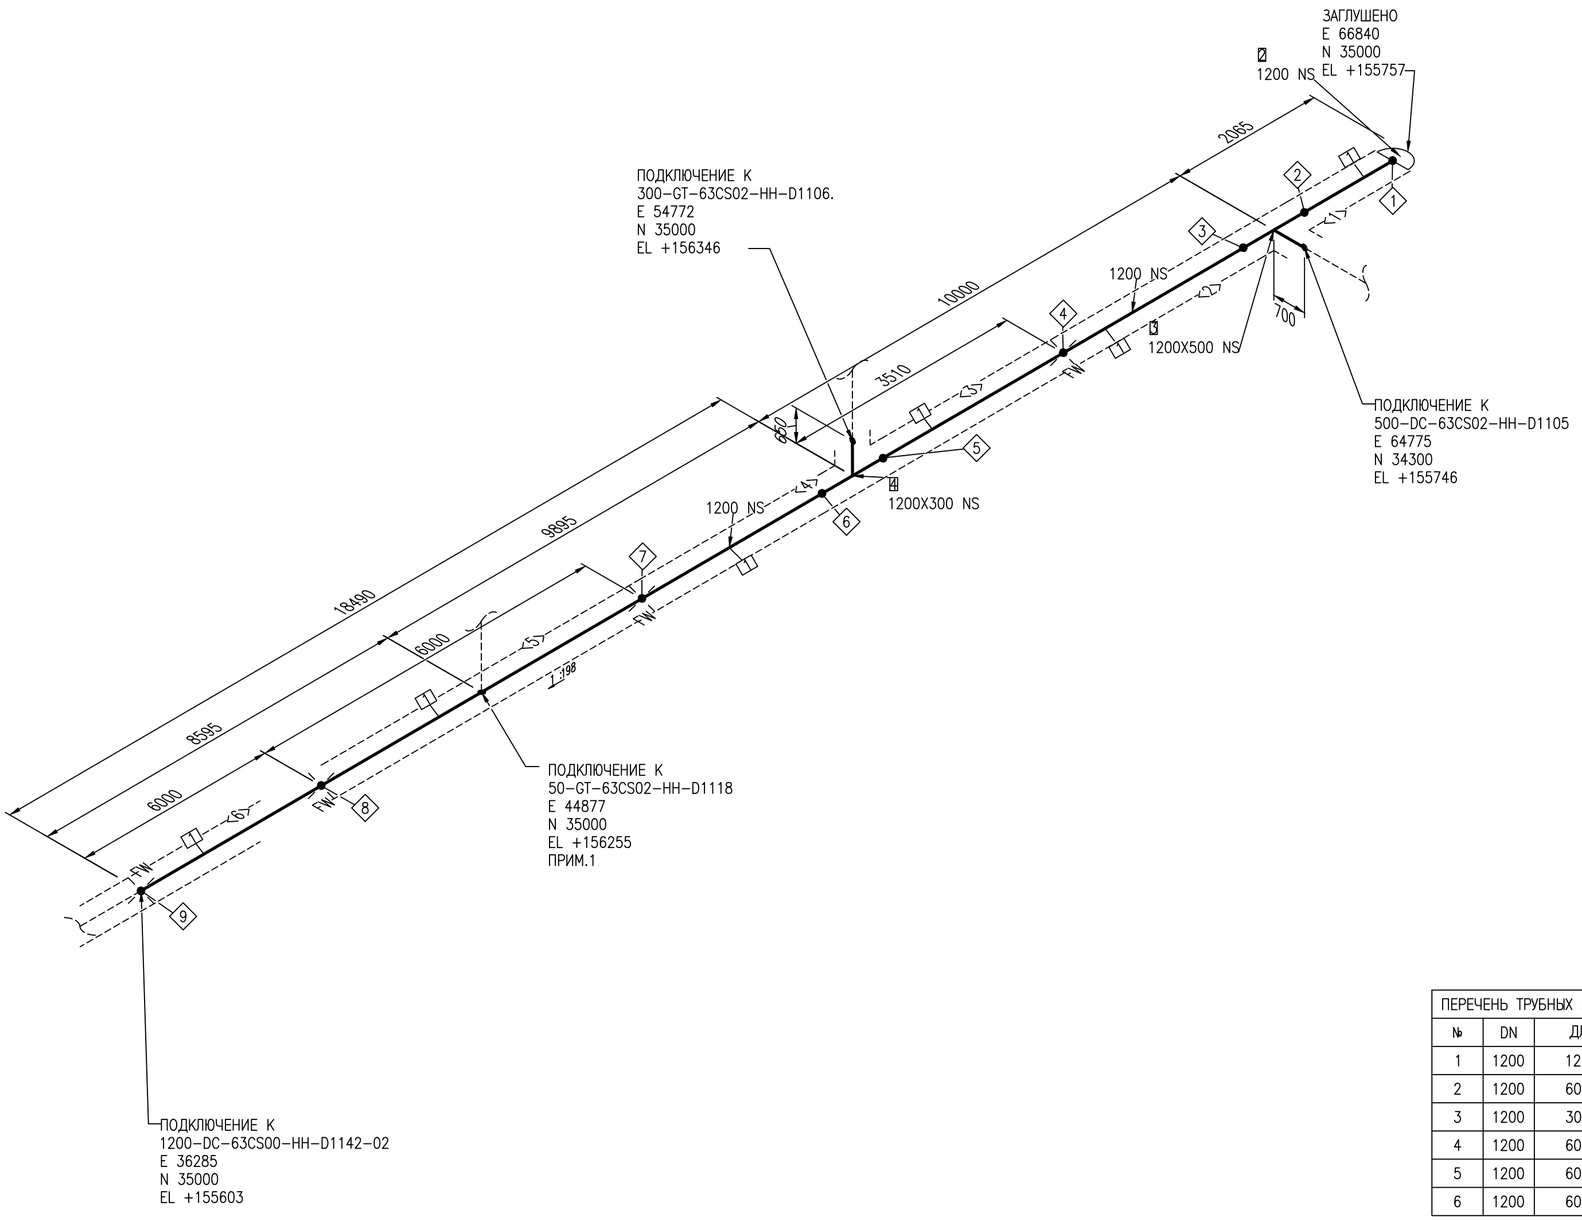

ПЕРЕЧЕНЬ ТРУБНЫХ КАТУШЕК		
№	DN	ДЛИНА
1	1200	1236MM
2	1200	6000MM
3	1200	3021MM
4	1200	6000MM
5	1200	6000MM
6	1200	6000MM

СПЕЦИФИКАЦИЯ ИЗДЕЛИЙ И МАТЕРИАЛОВ

ПОЗ.	НАИМЕНОВАНИЕ	СТАНДАРТ	КОЛ.	ПРИМЕЧАНИЕ
1	Трубы стальные сварные прямошовные, тип 3, К60, 1220Х16	ГОСТ 31447-2012	28.3М	
2	Днище Д I 1220(16К60)-5,5(6,9)-075-30, сталь К60	ТУ 1469-017-38948552-2015	1	
3	Тройник Т I 1220(16К60)-530(8К60)-5,5(6,9)-0,75-30, сталь К60	ТУ 1469-017-38948552-2015	1	
4	Тройник Т I 1220(16К60)-325(10К48)-5,5(6,9)-0,75-30, сталь К60	ТУ 1469-017-38948552-2015	1	

ПРИМЕЧАНИЕ:

1. Точку подключения см. совместно с документами EWE0426-MGL1-PRE-054-ISO-690621, EWE0426-MGL1-PRE-054-DRW-690203, Лист 2 Разрез 1-1, Лист 3 Вид "Д"
2. Точку подключения см. совместно с документами EWE0426-MGL1-PRE-054-ISO-690617, EWE0426-MGL1-PRE-054-DRW-690203, Лист 3 Разрез 10-10, Вид "С"

Трубопровод	ДАННЫЕ ПО ТРУБОПРОВОДУ		
1200-DC-63CS00-HH-D1142	Расчетные параметры	Температура	-26,9...+85 °C
		Давление	6,3 MPa
	Рабочие параметры	Температура	-20...+40 °C
		Давление	5,5 MPa
	Параметры испытания	Тип	Гидравлическое
Ссылочные чертежи No		Давление	6,9 MPa
EWE0426-MGL1-PRE-054-SCM-610102	Изоляция	Тип	HH
		Толщина	mm
	Катодная защита	Да или Нет	Да

Рев.	Дата	Назначение ревизии	Проверил	Утвердил
A1	25.09.2026	Утверждено для строительства		
R1	27.08.2026	Выпущено для рассмотрения		

ЗАКАЗЧИК: ГЕНЕРАЛЬНЫЙ ПОДРЯДЧИК: ПОДРЯДЧИК: ГЕНЕРАЛЬНЫЙ ПРОЕКТИРОВЩИК:

EWE0426-MGL1-PRE-054-ISO-690602-A1

«СТРОИТЕЛЬСТВО НОВЫХ НИТОК (УЧАСТКОВ) ГАЗОПРОВОДОВ «ГАЗЛИ - САРИМОЙ» И «АКЧАЛОК - ГАЗЛИ - НУКУС» ОБЩЕЙ ПРОТЯЖЕННОСТЬЮ НЕ МЕНЕЕ 275 КМ».

Изм.	Кол.уч.	Лист	№док.	Подпись	Дата
ГИП		Кирпичников С.			09.2026
Нач.отд.		Рябинин А.			09.2026
Исполн.		Таштимуров Р.			09.2026
Н.контр		Кирпичников С.			09.2026

ГАЗОПРОВОД «ГАЗЛИ-САРИМОЙ» (54 КМ)
Узел приема/запуска очистных устройств DN1200.УЗПОУ-D11.

Стадия	Лист	Листов
РД	1	2

Изометрический чертеж трубопровода
1200-DC-63CS00-HH-D1142


ООО "EAST-WEST Engineering"
г. Ташкент 2026г.

Взам. инв. №
Подпись и дата
Инв.№ подл.

Формат А2 594x420

СЕВЕР

ПЕРЕЧЕНЬ СВАРНЫХ ШВОВ		
№	DN	ТИП
1	1200	BUTTWELD
2	1200	BUTTWELD
3	1200	BUTTWELD
4	1200	BUTTWELD
5	1200	BUTTWELD
6	1200	FIELDWELD
7	1200	FIELDWELD
8	1200	FIELDWELD

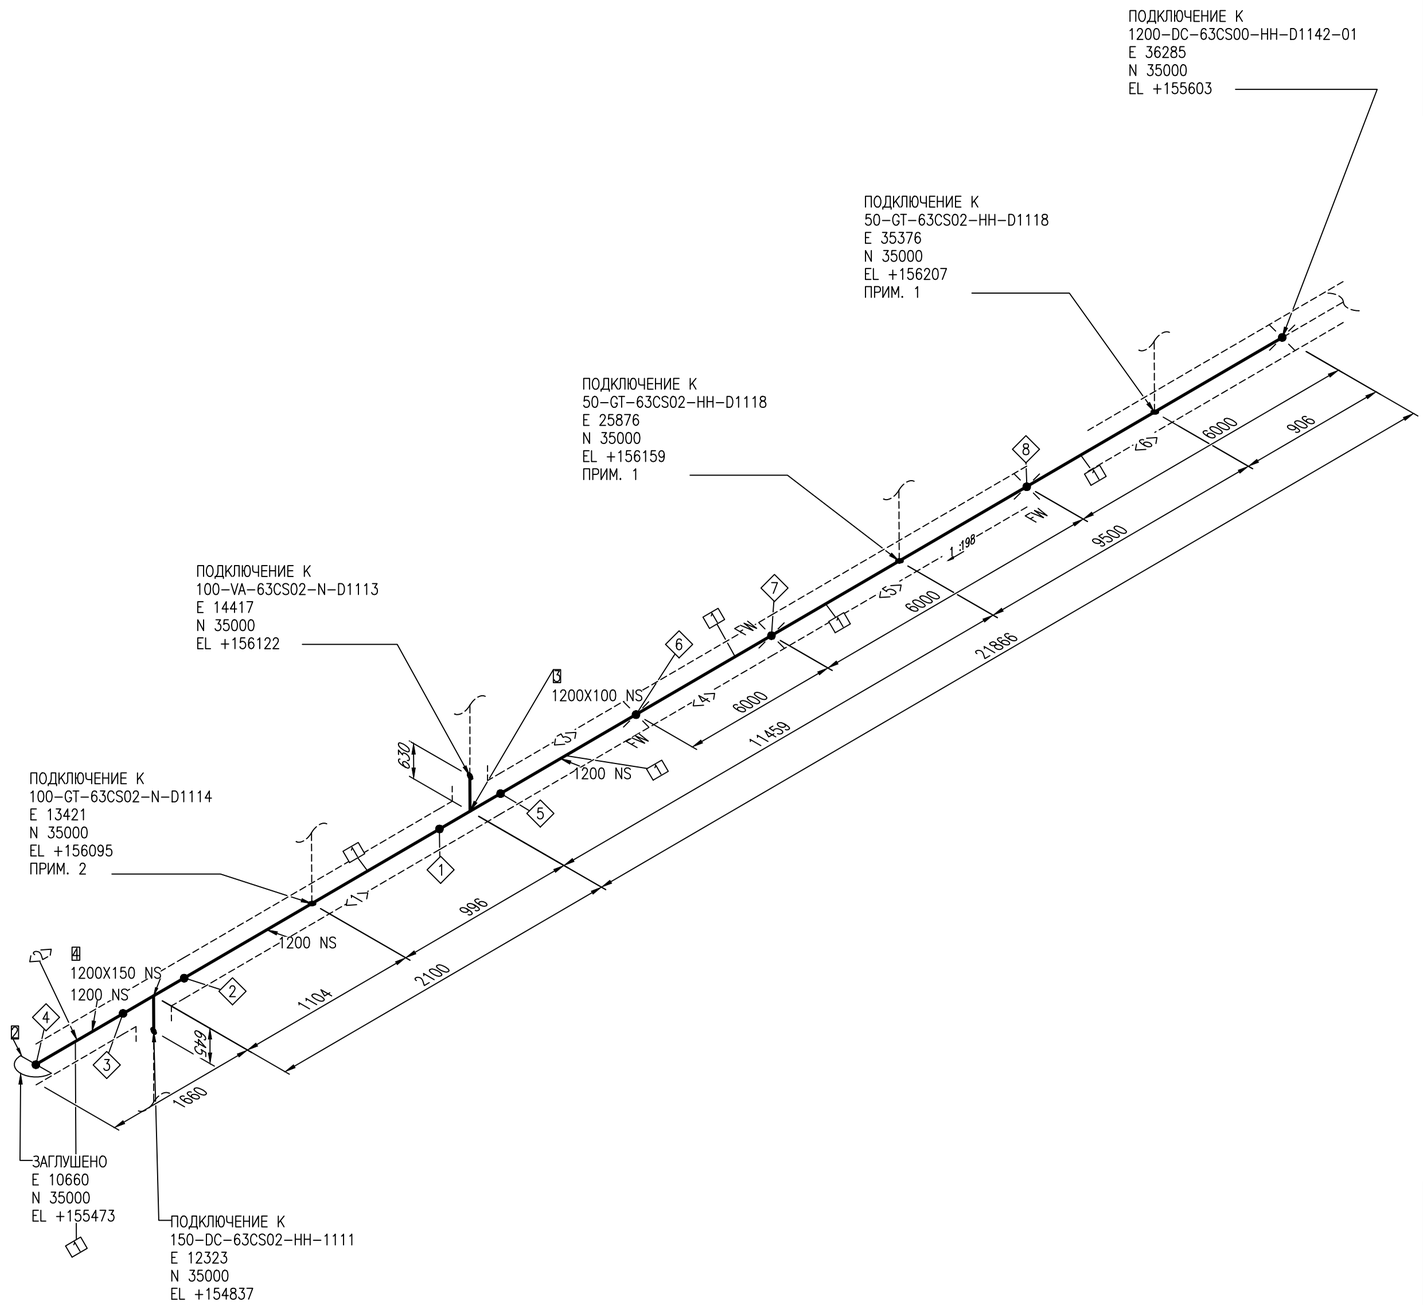

ПЕРЕЧЕНЬ ТРУБНЫХ КАТУШЕК		
№	DN	ДЛИНА
1	1200	1391MM
2	1200	961MM
3	1200	3516MM
4	1200	6000MM
5	1200	6000MM
6	1200	6000MM

СПЕЦИФИКАЦИЯ ИЗДЕЛИЙ И МАТЕРИАЛОВ

ПОЗ.	НАИМЕНОВАНИЕ	СТАНДАРТ	КОЛ.	ПРИМЕЧАНИЕ
1	Трубы стальные сварные прямошовные, типа 3, К60, 1220Х16	ГОСТ 31447-2012	23.9М	
2	Днище Д I 1220(16К60)-5,5(6,9)-075-30, сталь К60	ТУ 1469-017-38948552-2015	1	
3	Тройник Т I 1220(16К60)-114(5К48)-5,5(6,9)-0,75-30, сталь К60	ТУ 1469-017-38948552-2015	1	
4	Тройник Т I 1220(16К60)-159(6К48)-5,5(6,9)-0,75-30, сталь К60	ТУ 1469-017-38948552-2015	1	

Трубопровод	ДАННЫЕ ПО ТРУБОПРОВОДУ		
1200-DC-63CS00-HH-D1142	Расчетные параметры	Температура	-26,9...+85 °C
		Давление	6,3 MPa
	Рабочие параметры	Температура	-20...+40 °C
		Давление	5,5 MPa
Ссылочные чертежи No	Параметры испытания	Тип	Гидравлическое
EWE0426-MGL1-PRE-054-SCM-610102		Давление	6,9 MPa
	Изоляция	Тип	HH
		Толщина	mm
	Катодная защита	Да или Нет	Да

Рев.	Дата	Назначение ревизии	Проверил	Утвердил
A1	25.09.2026	Утверждено для строительства		
R1	27.08.2026	Выпущено для рассмотрения		

ЗАКАЗЧИК: | ГЕНЕРАЛЬНЫЙ ПОДРЯДЧИК: | ПОДРЯДЧИК: | ГЕНЕРАЛЬНЫЙ ПРОЕКТИРОВЩИК: EAST WEST ENGINEERING

EWE0426-MGL1-PRE-054-ISO-690602-A1

«СТРОИТЕЛЬСТВО НОВЫХ НИТОК (УЧАСТКОВ) ГАЗОПРОВОДОВ «ГАЗЛИ - САРИМОЙ» И «АКЧАЛОК - ГАЗЛИ - НУКУС» ОБЩЕЙ ПРОТЯЖЕННОСТЬЮ НЕ МЕНЕЕ 275 КМ».

Изм.	Кол.уч.	Лист	№док.	Подпись	Дата			
ГИП		Кирпичников С.			09.2026	ГАЗОПРОВОД «ГАЗЛИ-САРИМОЙ» (54 КМ) Узел приема/запуска очистных устройств DN1200.УЗПОУ-D11.	Стадия	Лист	Листов
Нач.отд.		Рябинин А.			09.2026		РД	2	2
Исполн.		Таштимуров Р.			09.2026				
Н.контр		Кирпичников С.			09.2026	Изометрический чертеж трубопровода 1200-DC-63CS00-HH-D1142	EAST WEST ENGINEERING	ООО "EAST-WEST Engineering" г. Ташкент 2026г.	

Взам. инв. №

Подпись и дата

Инв.№ подл.

Формат А2 594x420