
ПЕРЕЧЕНЬ СВАРНЫХ ШВОВ		
№	DN	ТИП
1	1200	FIELDWELD
2	1200	BUTTWELD
3	1200	BUTTWELD
4	1200	FIELDWELD
5	1200	FIELDWELD
6	1200	BUTTWELD
7	1200	BUTTWELD

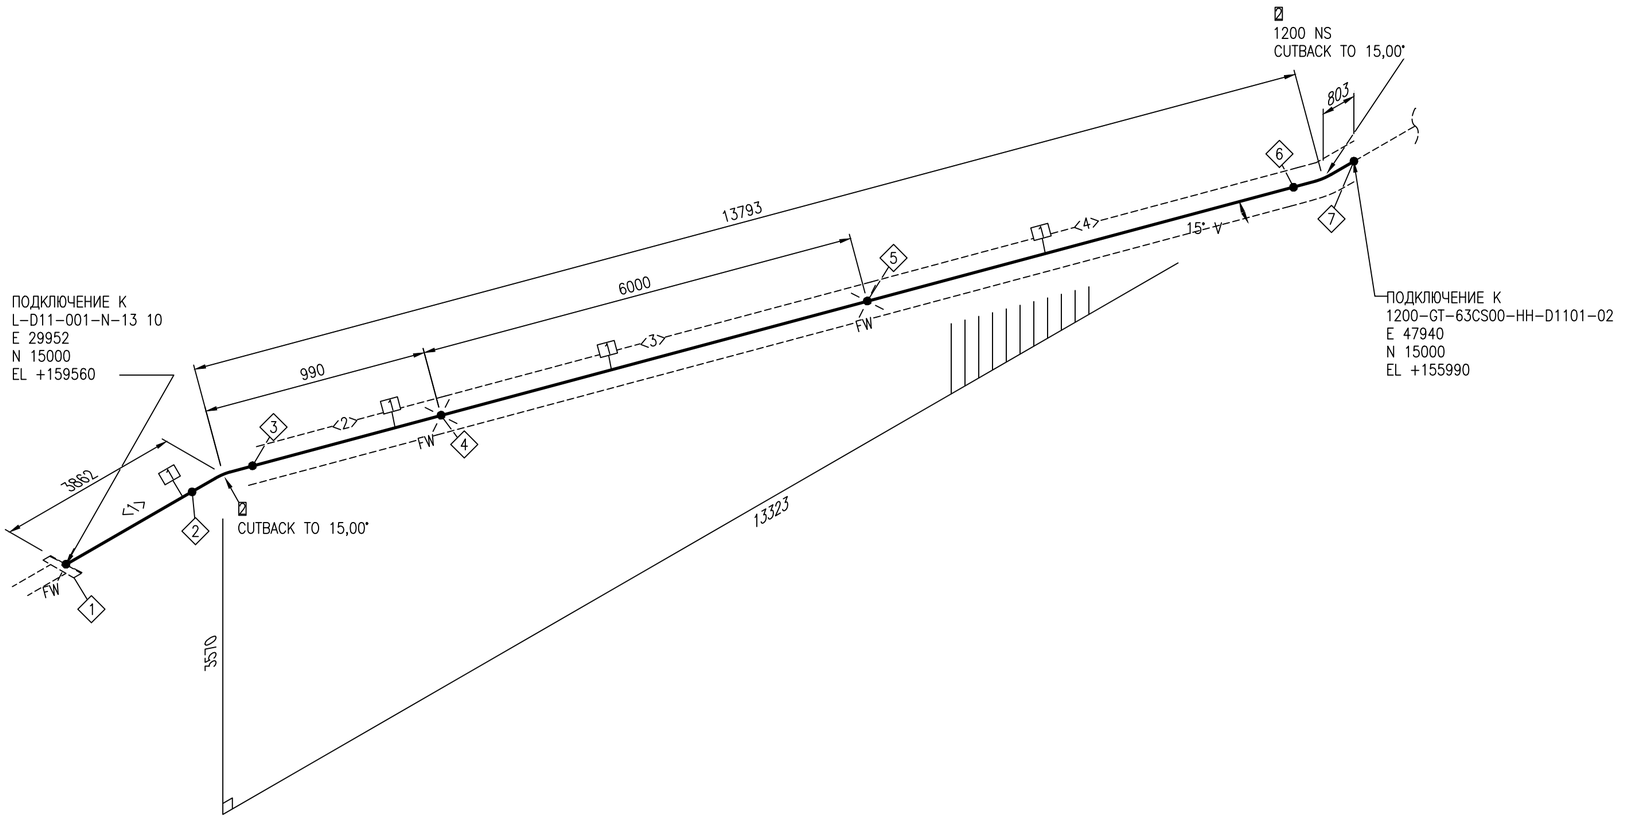

ПЕРЕЧЕНЬ ТРУБНЫХ КАТУШЕК		
№	DN	ДЛИНА
1	1200	3059MM
2	1200	188MM
3	1200	6000MM
4	1200	6000MM

СПЕЦИФИКАЦИЯ ИЗДЕЛИЙ И МАТЕРИАЛОВ				
ПОЗ.	НАИМЕНОВАНИЕ	СТАНДАРТ	КОЛ.	ПРИМЕЧАНИЕ
1	Трубы стальные сварные прямошовные, типа 3, К60, 1220Х12	ГОСТ 31447-2012	15.3М	
2	ОСС 15°-5Д-1220 (12К60)-5,5-075-У ТУ51-29-81	ТУ 51-29-81	2	

Трубопровод	ДАННЫЕ ПО ТРУБОПРОВОДУ		
1200-GT-63CS00-HH-D1101	Расчетные параметры	Температура	-26,9...+85 °C
		Давление	6,3 MPa
	Рабочие параметры	Температура	-20...+40 °C
		Давление	5,5 MPa
	Параметры испытания	Тип	Гидравлическое
Ссылочные чертежи No		Давление	6,9 MPa
EWE0426-MGL1-PRE-054-SCM-610102	Изоляция	Тип	HH
		Толщина	mm
	Катодная защита	Да или Нет	Да

Рев.	Дата	Назначение ревизии	Проверил	Утвердил
A1	25.09.2026	Утверждено для строительства		
R1	27.08.2026	Выпущено для рассмотрения		

ЗАКАЗЧИК: UTG ГЕНЕРАЛЬНЫЙ ПОДРЯДЧИК: UET ПОДРЯДЧИК: PBG ГЕНЕРАЛЬНЫЙ ПРОЕКТИРОВЩИК: EAST WEST ENGINEERING

Изм.	Кол.уч.	Лист	№док.	Подпись	Дата	EWE0426-MGL1-PRE-054-ISO-690603-A1		
						«СТРОИТЕЛЬСТВО НОВЫХ НИТОК (УЧАСТКОВ) ГАЗОПРОВОДОВ «ГАЗЛИ - САРИМОЙ» И «АКЧАЛОК - ГАЗЛИ - НУКУС» ОБЩЕЙ ПРОТЯЖЕННОСТЬЮ НЕ МЕНЕЕ 275 КМ».		
ГИП		Кирпичников С.			09.2026	ГАЗОПРОВОД «ГАЗЛИ-САРИМОЙ» (54 КМ) Узел приема/запуска очистных устройств DN1200.УЗПОУ-D11.	Стадия	Лист	Листов
Нач.отд.		Рябинин А.			09.2026		РД	1	4
Исполн.		Ташпимуров Р.			09.2026	Изометрический чертеж трубопровода 1200-GT-63CS00-HH-D1101	EAST WEST ENGINEERING	ООО "EAST-WEST Engineering" г. Ташкент 2026г.	
Н.контр		Кирпичников С.			09.2026				

Взам. инв. №


Подпись и дата

Инв.№ подл.

Формат А2 594x420

СЕВЕР

ПЕРЕЧЕНЬ СВАРНЫХ ШВОВ		
№	DN	ТИП
1	1200	BUTTWELD
2	1200	BUTTWELD
3	1200	BUTTWELD
4	1200	BUTTWELD

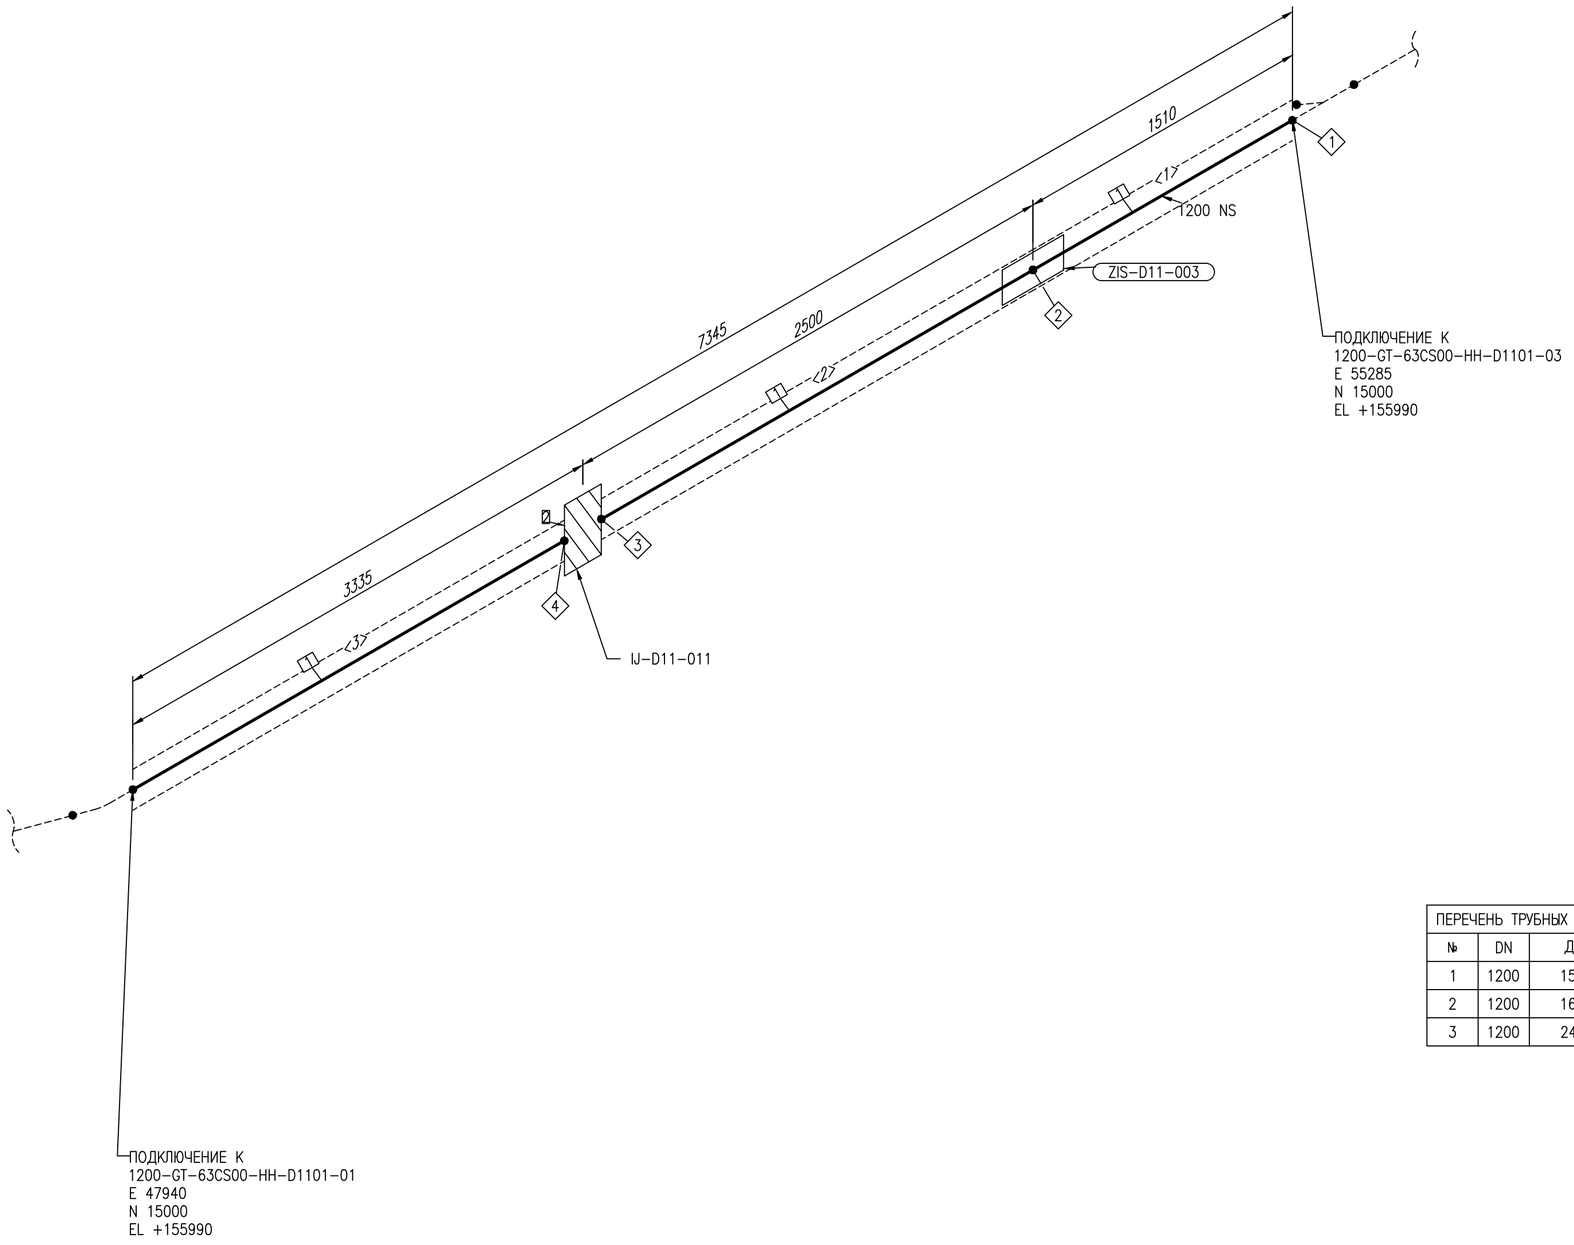

ПЕРЕЧЕНЬ ТРУБНЫХ КАТУШЕК		
№	DN	ДЛИНА
1	1200	1510MM
2	1200	1600MM
3	1200	2436MM

СПЕЦИФИКАЦИЯ ИЗДЕЛИЙ И МАТЕРИАЛОВ				
ПОЗ.	НАИМЕНОВАНИЕ	СТАНДАРТ	КОЛ.	ПРИМЕЧАНИЕ
1	Трубы стальные сварные прямошовные, тип 3, К60, 1220Х12	ГОСТ 31447-2012	5.6М	
2	Изолирующее соединение приварное, 6.3 МПа, 1220х12	EWE0426-MGL1-PRE-054-DSH-610135	1	

Трубопровод	ДАННЫЕ ПО ТРУБОПРОВОДУ		
1200-GT-63CS00-HH-D1101	Расчетные параметры	Температура	-26,9...+85 °C
		Давление	6,3 MPa
	Рабочие параметры	Температура	-20...+40 °C
		Давление	5,5 MPa
	Параметры испытания	Тип	Гидравлическое
Ссылочные чертежи No		Давление	6,9 MPa
EWE0426-MGL1-PRE-054-SCM-610102	Изоляция	Тип	HH
		Толщина	mm
	Катодная защита	Да или Нет	Да

Рев.	Дата	Назначение ревизии	Проверил	Утвердил
A1	25.09.2026	Утверждено для строительства		
R1	27.08.2026	Выпущено для рассмотрения		

ЗАКАЗЧИК: UTG ГЕНЕРАЛЬНЫЙ ПОДРЯДЧИК: UET ПОДРЯДЧИК: PBG ГЕНЕРАЛЬНЫЙ ПРОЕКТИРОВЩИК: EAST WEST ENGINEERING

Изм.	Кол.уч.	Лист	№док.	Подпись	Дата
ГИП		Кирпичников С.			09.2026
Нач.отд.		Рябинин А.			09.2026
Исполн.		Таштимуров Р.			09.2026
Н.контр		Кирпичников С.			09.2026

EWE0426-MGL1-PRE-054-ISO-690603-A1

«СТРОИТЕЛЬСТВО НОВЫХ НИТОК (УЧАСТКОВ) ГАЗОПРОВОДОВ «ГАЗЛИ - САРИМОЙ» И «АКЧАЛОК - ГАЗЛИ - НУКУС» ОБЩЕЙ ПРОТЯЖЕННОСТЬЮ НЕ МЕНЕЕ 275 КМ».

ГАЗОПРОВОД «ГАЗЛИ-САРИМОЙ» (54 КМ)
Узел приема/запуска очистных устройств DN1200.УЗПОУ-D11.

Стадия	Лист	Листов
РД	2	4

Изометрический чертеж трубопровода
1200-GT-63CS00-HH-D1101


ООО "EAST-WEST Engineering"
г. Ташкент 2026г.

Взам. инв. №
Подпись и дата
Инв.№ подл.

Формат А2 594х420

N
СЕВЕР

ПЕРЕЧЕНЬ СВАРНЫХ ШВОВ		
№	DN	ТИП
1	1200	BUTTWELD
2	1200	BUTTWELD
3	500	BUTTWELD
4	1200	BUTTWELD
5	1200	BUTTWELD

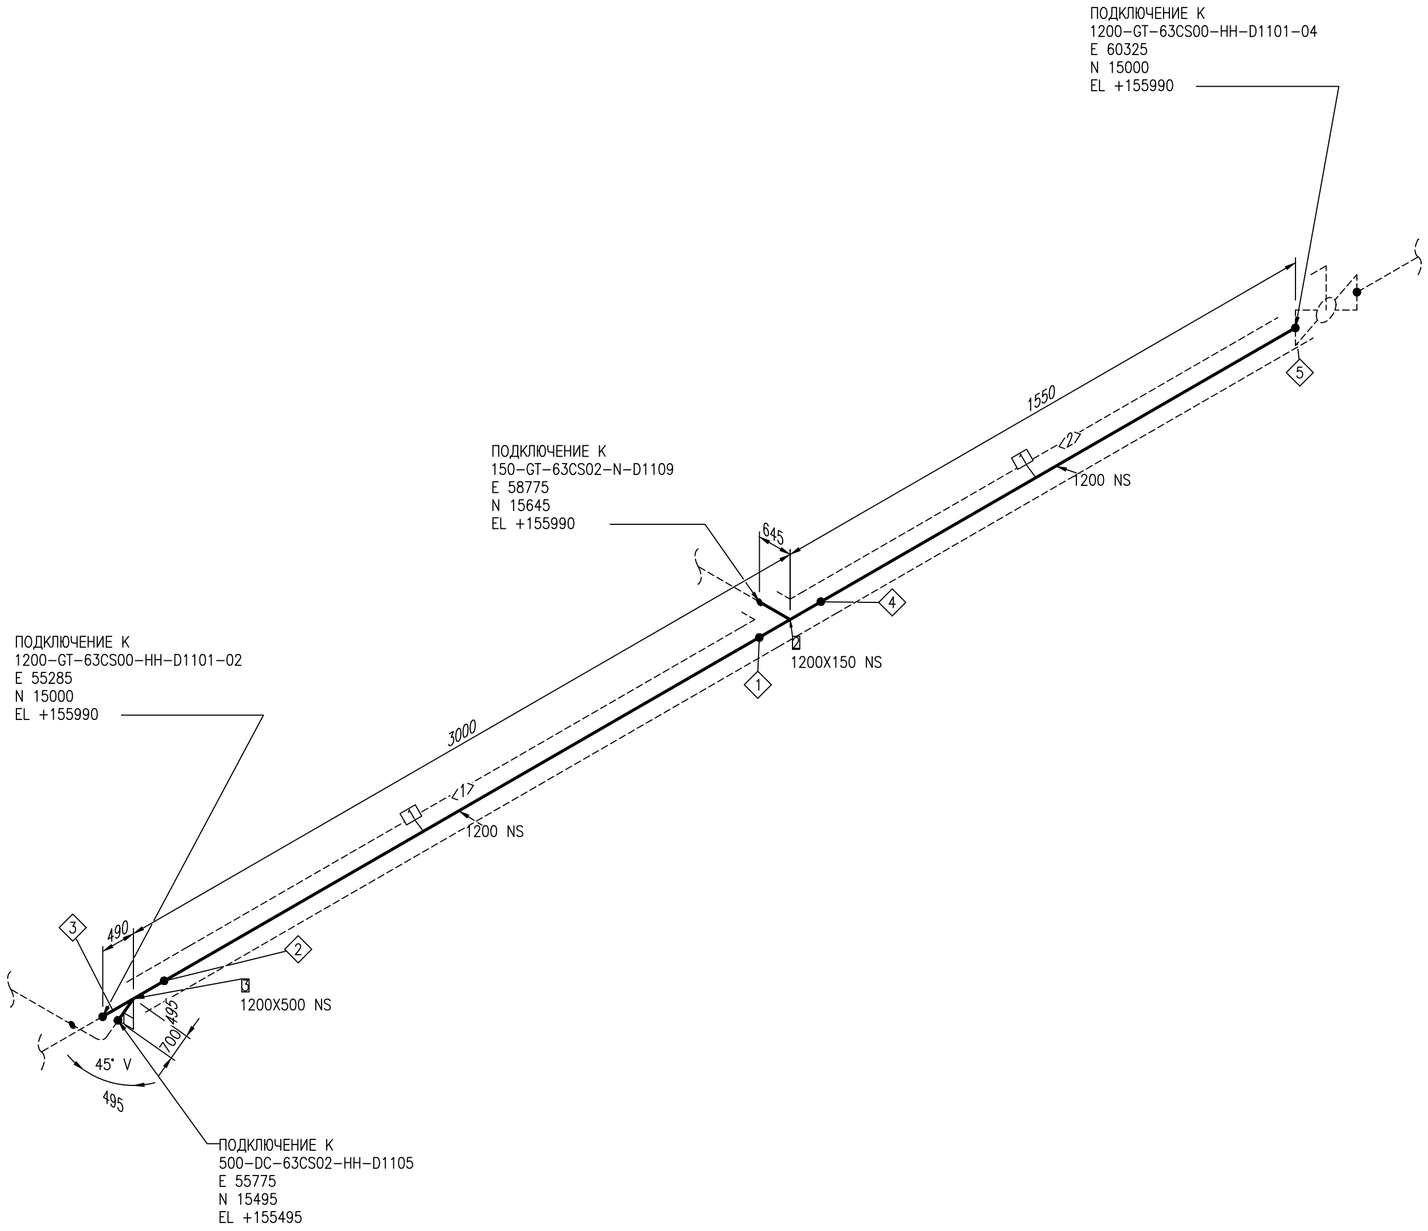

ПЕРЕЧЕНЬ ТРУБНЫХ КАТУШЕК		
№	DN	ДЛИНА
1	1200	2150ММ
2	1200	1190ММ

СПЕЦИФИКАЦИЯ ИЗДЕЛИЙ И МАТЕРИАЛОВ				
ПОЗ.	НАИМЕНОВАНИЕ	СТАНДАРТ	КОЛ.	ПРИМЕЧАНИЕ
1	Трубы стальные сварные прямошовные, типа 3, К60, 1220Х12	ГОСТ 31447-2012	3.4М	
2	Тройник Т I 1220(13К60)-159(6К48)-5,5(6,9)-0,75-30, сталь К60	ТУ 1469-017-38948552-2015	1	
3	Тройник Т I 1220(13К60)-530(8К48)-5,5(6,9)-0,75-30, сталь К60	ТУ 1469-017-38948552-2015	1	

Трубопровод	ДАННЫЕ ПО ТРУБОПРОВОДУ		
1200-GT-63CS00-HH-D1101	Расчетные параметры	Температура	-26,9...+85 °C
		Давление	6,3 MPa
	Рабочие параметры	Температура	-20...+40 °C
		Давление	5,5 MPa
Ссылочные чертежи No	Параметры испытания	Тип	Гидравлическое
EWE0426-MGL1-PRE-054-SCM-610102		Давление	6,9 MPa
	Изоляция	Тип	НН
		Толщина	mm
	Катодная защита	Да или Нет	Да

Рев.	Дата	Назначение ревизии	Проверил	Утвердил
A1	25.09.2026	Утверждено для строительства		
R1	27.08.2026	Выпущено для рассмотрения		

ЗАКАЗЧИК: UTG ИСТИКЛОЛ | ГЕНЕРАЛЬНЫЙ ПОДРЯДЧИК: UET UZBEKISTANOTAMIR | ПОДРЯДЧИК: PBG Pre Build Connection | ГЕНЕРАЛЬНЫЙ ПРОЕКТИРОВЩИК: EAST WEST ENGINEERING

Изм.	Кол.уч.	Лист	№док.	Подпись	Дата	EWE0426-MGL1-PRE-054-ISO-690603-A1			
						«СТРОИТЕЛЬСТВО НОВЫХ НИТОК (УЧАСТКОВ) ГАЗОПРОВОДОВ «ГАЗЛИ - САРИМОЙ» И «АКЧАЛОК - ГАЗЛИ - НУКУС» ОБЩЕЙ ПРОТЯЖЕННОСТЬЮ НЕ МЕНЕЕ 275 КМ».			
ГИП		Кирпичников С.			09.2026	ГАЗОПРОВОД «ГАЗЛИ-САРИМОЙ» (54 КМ) Узел приема/запуска очистных устройств DN1200.УЗПОУ-D11.	Стадия	Лист	Листов
Нач.отд.		Рябинин А.			09.2026		РД	3	4
Исполн.		Таштимуров Р.			09.2026	Изометрический чертеж трубопровода 1200-GT-63CS00-HH-D1101	EAST WEST ENGINEERING	ООО "EAST-WEST Engineering" г. Ташкент 2026г.	
Н.контр		Кирпичников С.			09.2026				


Взам. инв. №

Подпись и дата

Инв.№ подл.

Формат А2 594x420

ПЕРЕЧЕНЬ СВАРНЫХ ШВОВ		
№	DN	ТИП
1	1200	WELD
2	1200	BUTTWELD
3	1200	BUTTWELD
4	1200	BUTTWELD

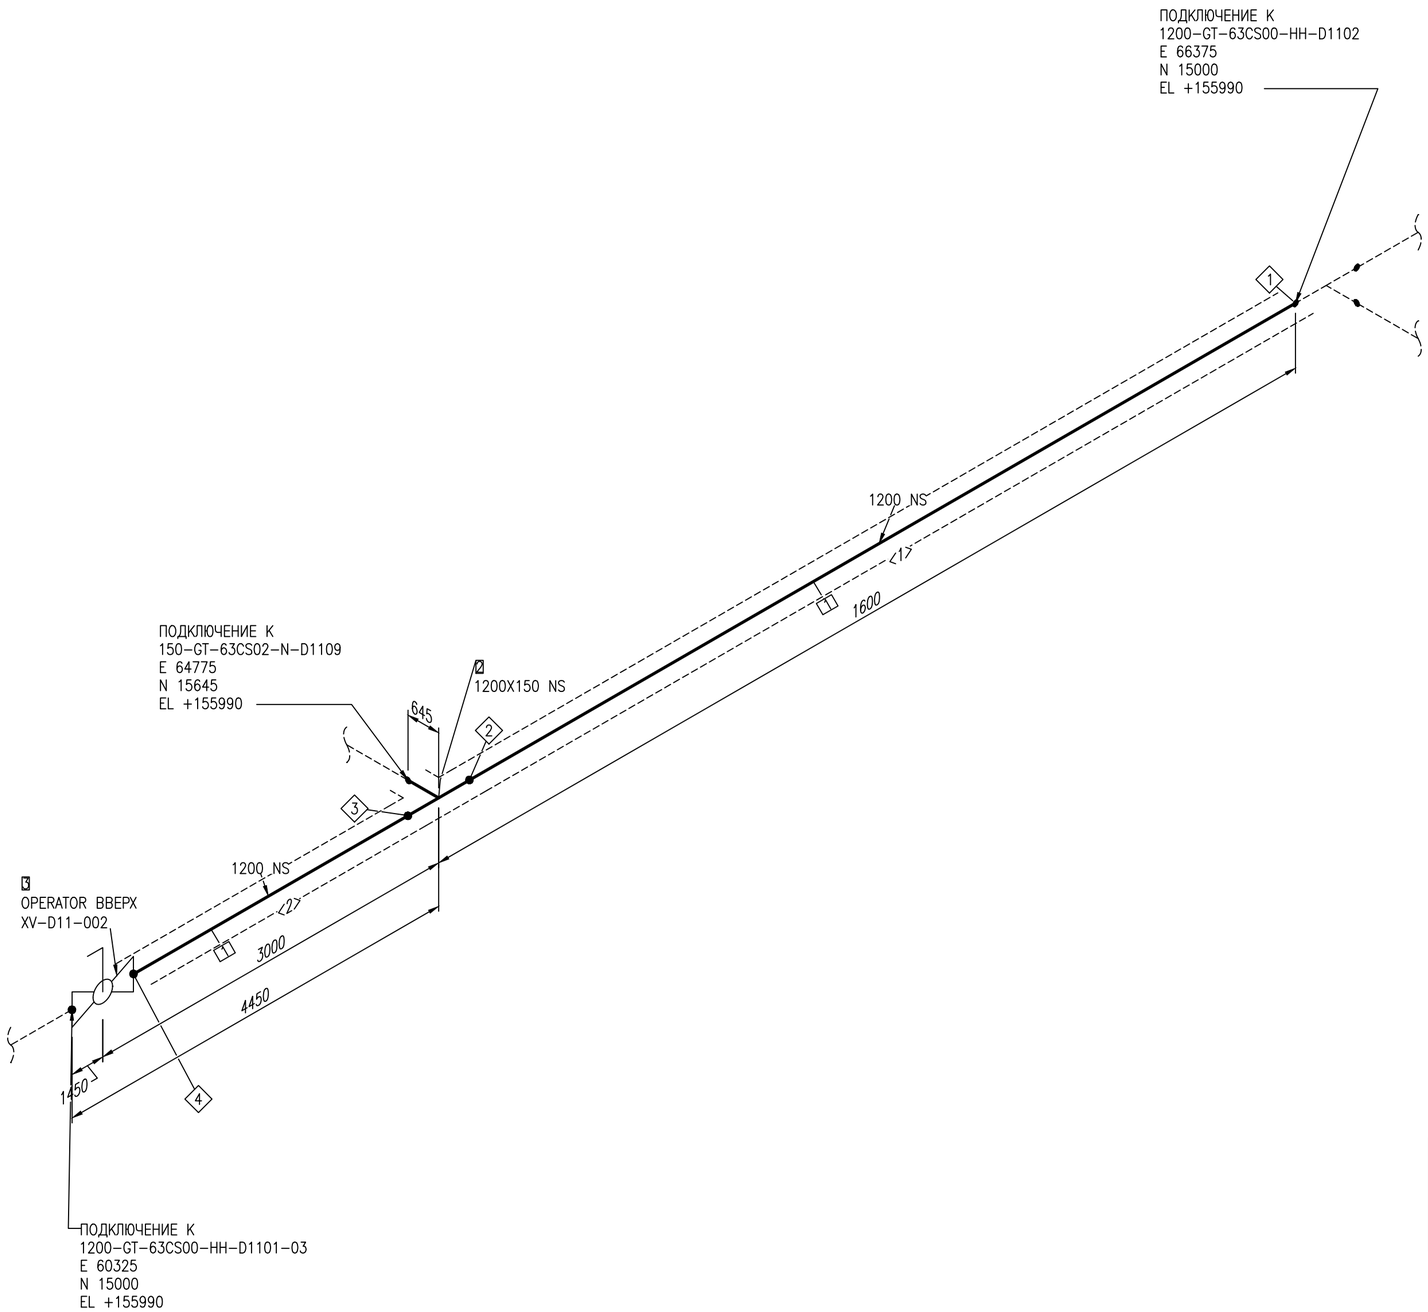

ПЕРЕЧЕНЬ ТРУБНЫХ КАТУШЕК		
№	DN	ДЛИНА
1	1200	1240MM
2	1200	1190MM

СПЕЦИФИКАЦИЯ ИЗДЕЛИЙ И МАТЕРИАЛОВ				
ПОЗ.	НАИМЕНОВАНИЕ	СТАНДАРТ	КОЛ.	ПРИМЕЧАНИЕ
1	Трубы стальные сварные прямошовные, типа 3, К60, 1220Х12	ГОСТ 31447-2012	2.5М	
2	Тройник Т I 1220(13К60)-159(6К48)-5,5(6,9)-0,75-30, сталь К60	ТУ 1469-017-38948552-2015	1	
3	Кран шаровой DN1200 PN-6,3 МПа с пневмогидроприводом, приварной, подземный	EWE0426-MGL1-PRE-054-DSH-610127	1	

Трубопровод	ДАННЫЕ ПО ТРУБОПРОВОДУ		
1200-GT-63CS00-HH-D1101	Расчетные параметры	Температура	-26,9...+85 °C
		Давление	6,3 MPa
	Рабочие параметры	Температура	-20...+40 °C
		Давление	5,5 MPa
	Параметры испытания	Тип	Гидравлическое
Ссылочные чертежи No		Давление	6,9 MPa
EWE0426-MGL1-PRE-054-SCM-610102	Изоляция	Тип	HH
		Толщина	mm
	Катодная защита	Да или Нет	Да

Рев.	Дата	Назначение ревизии	Проверил	Утвердил
A1	25.09.2026	Утверждено для строительства		
R1	27.08.2026	Выпущено для рассмотрения		

ЗАКАЗЧИК: UTG ГЕНЕРАЛЬНЫЙ ПОДРЯДЧИК: UET ПОДРЯДЧИК: PBG ГЕНЕРАЛЬНЫЙ ПРОЕКТИРОВЩИК: EAST WEST ENGINEERING

Изм.	Кол.уч.	Лист	№док.	Подпись	Дата
ГИП		Кирпичников С.			09.2026
Нач.отд.		Рябинин А.			09.2026
Исполн.		Таштимуров Р.			09.2026
Н.контр		Кирпичников С.			09.2026

EWE0426-MGL1-PRE-054-ISO-690603-A1

«СТРОИТЕЛЬСТВО НОВЫХ НИТОК (УЧАСТКОВ) ГАЗОПРОВОДОВ «ГАЗЛИ - САРИМОЙ» И «АКЧАЛОК - ГАЗЛИ - НУКУС» ОБЩЕЙ ПРОТЯЖЕННОСТЬЮ НЕ МЕНЕЕ 275 КМ».

ГАЗОПРОВОД «ГАЗЛИ-САРИМОЙ» (54 КМ)
Узел приема/запуска очистных устройств DN1200.УЗПОУ-D11.

Стадия	Лист	Листов
РД	4	4

Изометрический чертеж трубопровода
1200-GT-63CS00-HH-D1101

ООО "EAST-WEST Engineering"
г. Ташкент 2026г.

Взам. инв. №
Подпись и дата
Инв.№ подл.

Формат А2 594x420