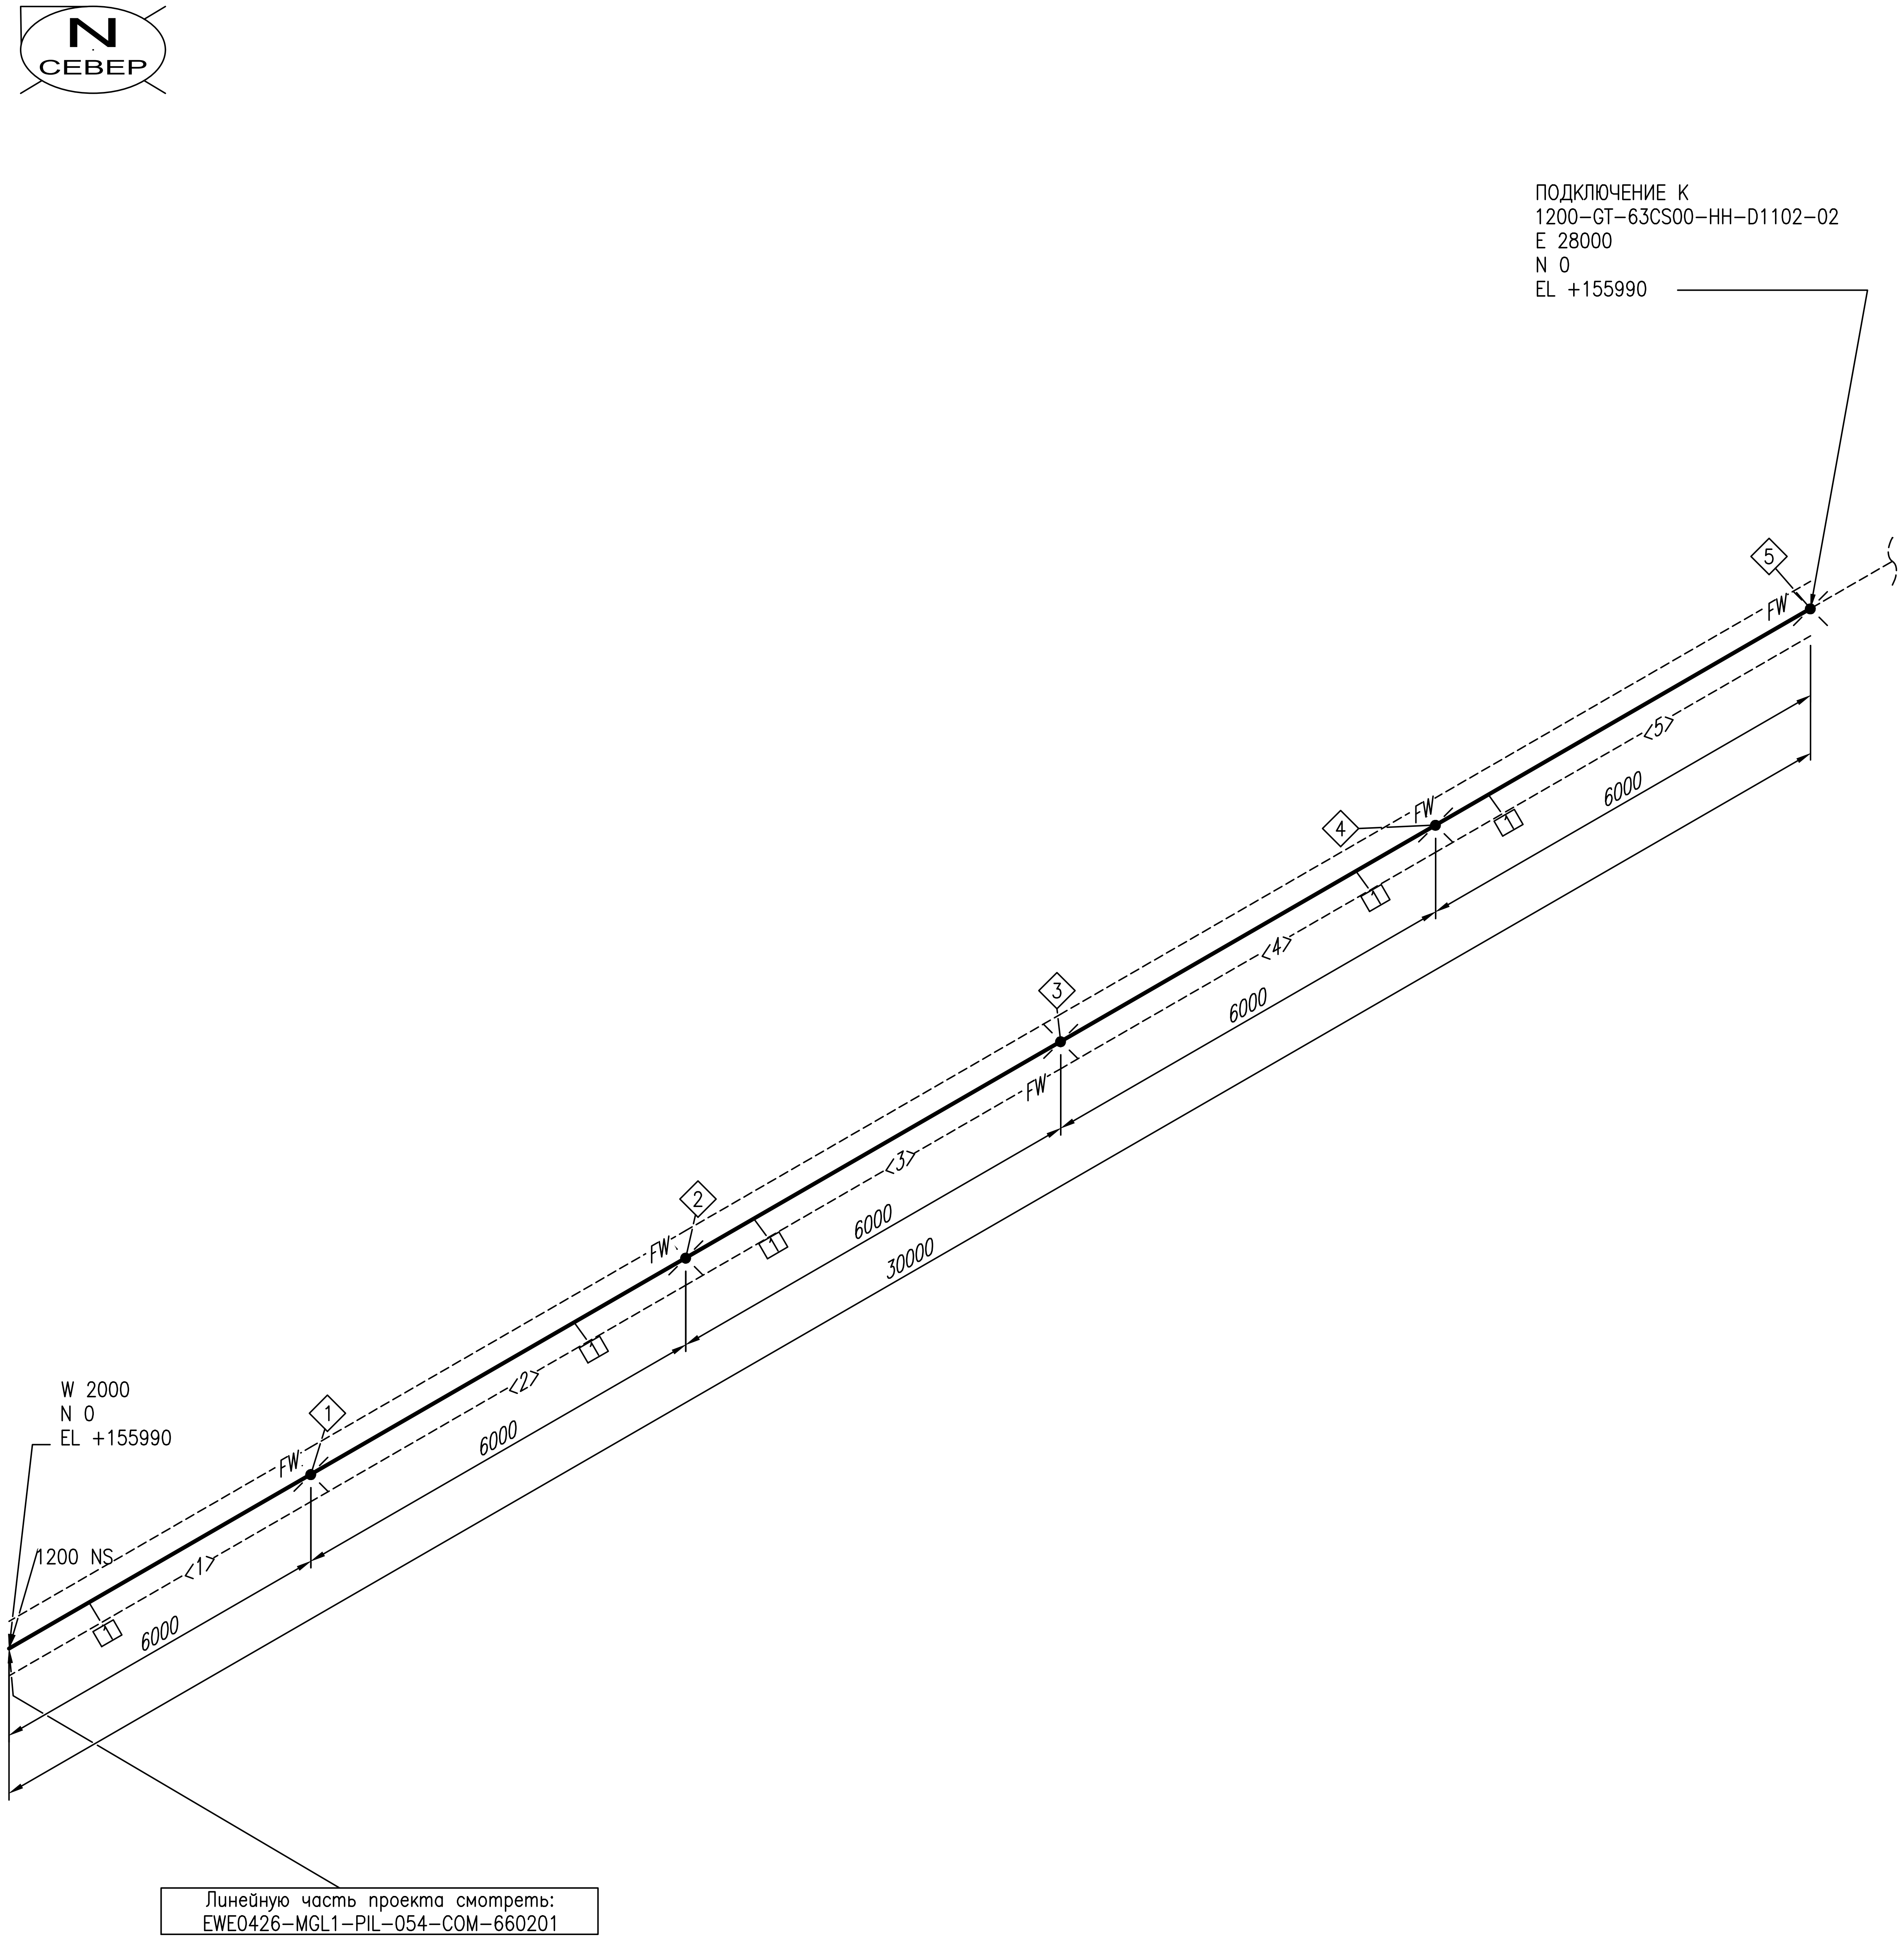

ПЕРЕЧЕНЬ СВАРНЫХ ШВОВ

| № | DN | ТИП |
|---|---|---|
| 1 | 1200 | FIELDWELD |
| 2 | 1200 | FIELDWELD |
| 3 | 1200 | FIELDWELD |
| 4 | 1200 | FIELDWELD |
| 5 | 1200 | FIELDWELD |

ПЕРЕЧЕНЬ ТРУБНЫХ КАТУШЕК

| № | DN | ДЛИНА |
|---|---|---|
| 1 | 1200 | 6000ММ |
| 2 | 1200 | 6000ММ |
| 3 | 1200 | 6000ММ |
| 4 | 1200 | 6000ММ |
| 5 | 1200 | 6000ММ |

СПЕЦИФИКАЦИЯ ИЗДЕЛИЙ И МАТЕРИАЛОВ

| ПОЗ. | НАИМЕНОВАНИЕ | СТАНДАРТ | КОЛ. | ПРИМЕЧАНИЕ |
|---|---|---|---|---|
| 1 | Трубы стальные сварные прямошовные, типа 3, К60, 1220Х12 | ГОСТ 31447-2012 | 30.0М | ТРУБА УЧТЕНА В ЛИНЕЙНОЙ ЧАСТИ ПРОЕКТА |

| Трубопровод |
|---|
| 1200-GT-63CS00-HH-D1102 |
| |
| |
| |
| Ссылочные чертежи No |
| EWE0426-MGL1-PRE-054-SCM-610102 |
| |
| |
| |

ДАННЫЕ ПО ТРУБОПРОВОДУ

| | | |
|---|---|---|
| Расчетные параметры | Температура | -26,9...+85 °С |
| | Давление | 6,3 MPa |
| Рабочие параметры | Температура | -20...+40 °С |
| | Давление | 5,5 MPa |
| Параметры испытания | Тип | Гидравлическое |
| | Давление | 6,9 MPa |
| Изоляция | Тип | НН |
| | Толщина | mm |
| Катодная защита | Да или Нет | Да |

| Рев. | Дата | Назначение ревизии | Проверил | Утвердил |
|---|---|---|---|---|
| A1 | 25.09.2026 | Утверждено для строительства | | |
| R1 | 27.08.2026 | Выпущено для рассмотрения | | |

ЗАКАЗЧИК: ГЕНЕРАЛЬНЫЙ ПОДРЯДЧИК: ПОДРЯДЧИК: ГЕНЕРАЛЬНЫЙ ПРОЕКТИРОВЩИК:

EWE0426-MGL1-PRE-054-ISO-690604-A1

«СТРОИТЕЛЬСТВО НОВЫХ НИТОК (УЧАСТКОВ) ГАЗОПРОВОДОВ «ГАЗЛИ - САРИМОЙ» И «АКЧАЛОК - ГАЗЛИ - НУКУС» ОБЩЕЙ ПРОТЯЖЕННОСТЬЮ НЕ МЕНЕЕ 275 КМ».

| Изм. | Кол.уч. | Лист | №док. | Подпись | Дата |
|---|---|---|---|---|---|
| ГИП | | Кирпичников С. | | | 09.2026 |
| Нач.отд. | | Рябинин А. | | | 09.2026 |
| Исполн. | | Таштимуров Р. | | | 09.2026 |
| | | | | | |
| | | | | | |
| Н.контр | | Кирпичников С. | | | 09.2026 |

ГАЗОПРОВОД «ГАЗЛИ-САРИМОЙ» (54 КМ)
Узел приема/запуска очистных устройств DN1200.УЗПОУ-D11.

| Стадия | Лист | Листов |
|---|---|---|
| РД | 1 | 8 |

Изометрический чертеж трубопровода
1200-GT-63CS00-HH-D1102

ООО "EAST-WEST Engineering"
г. Ташкент 2026г.

Взам. инв. №

Подпись и дата

Инв.№ подл.

Формат A2 594x420

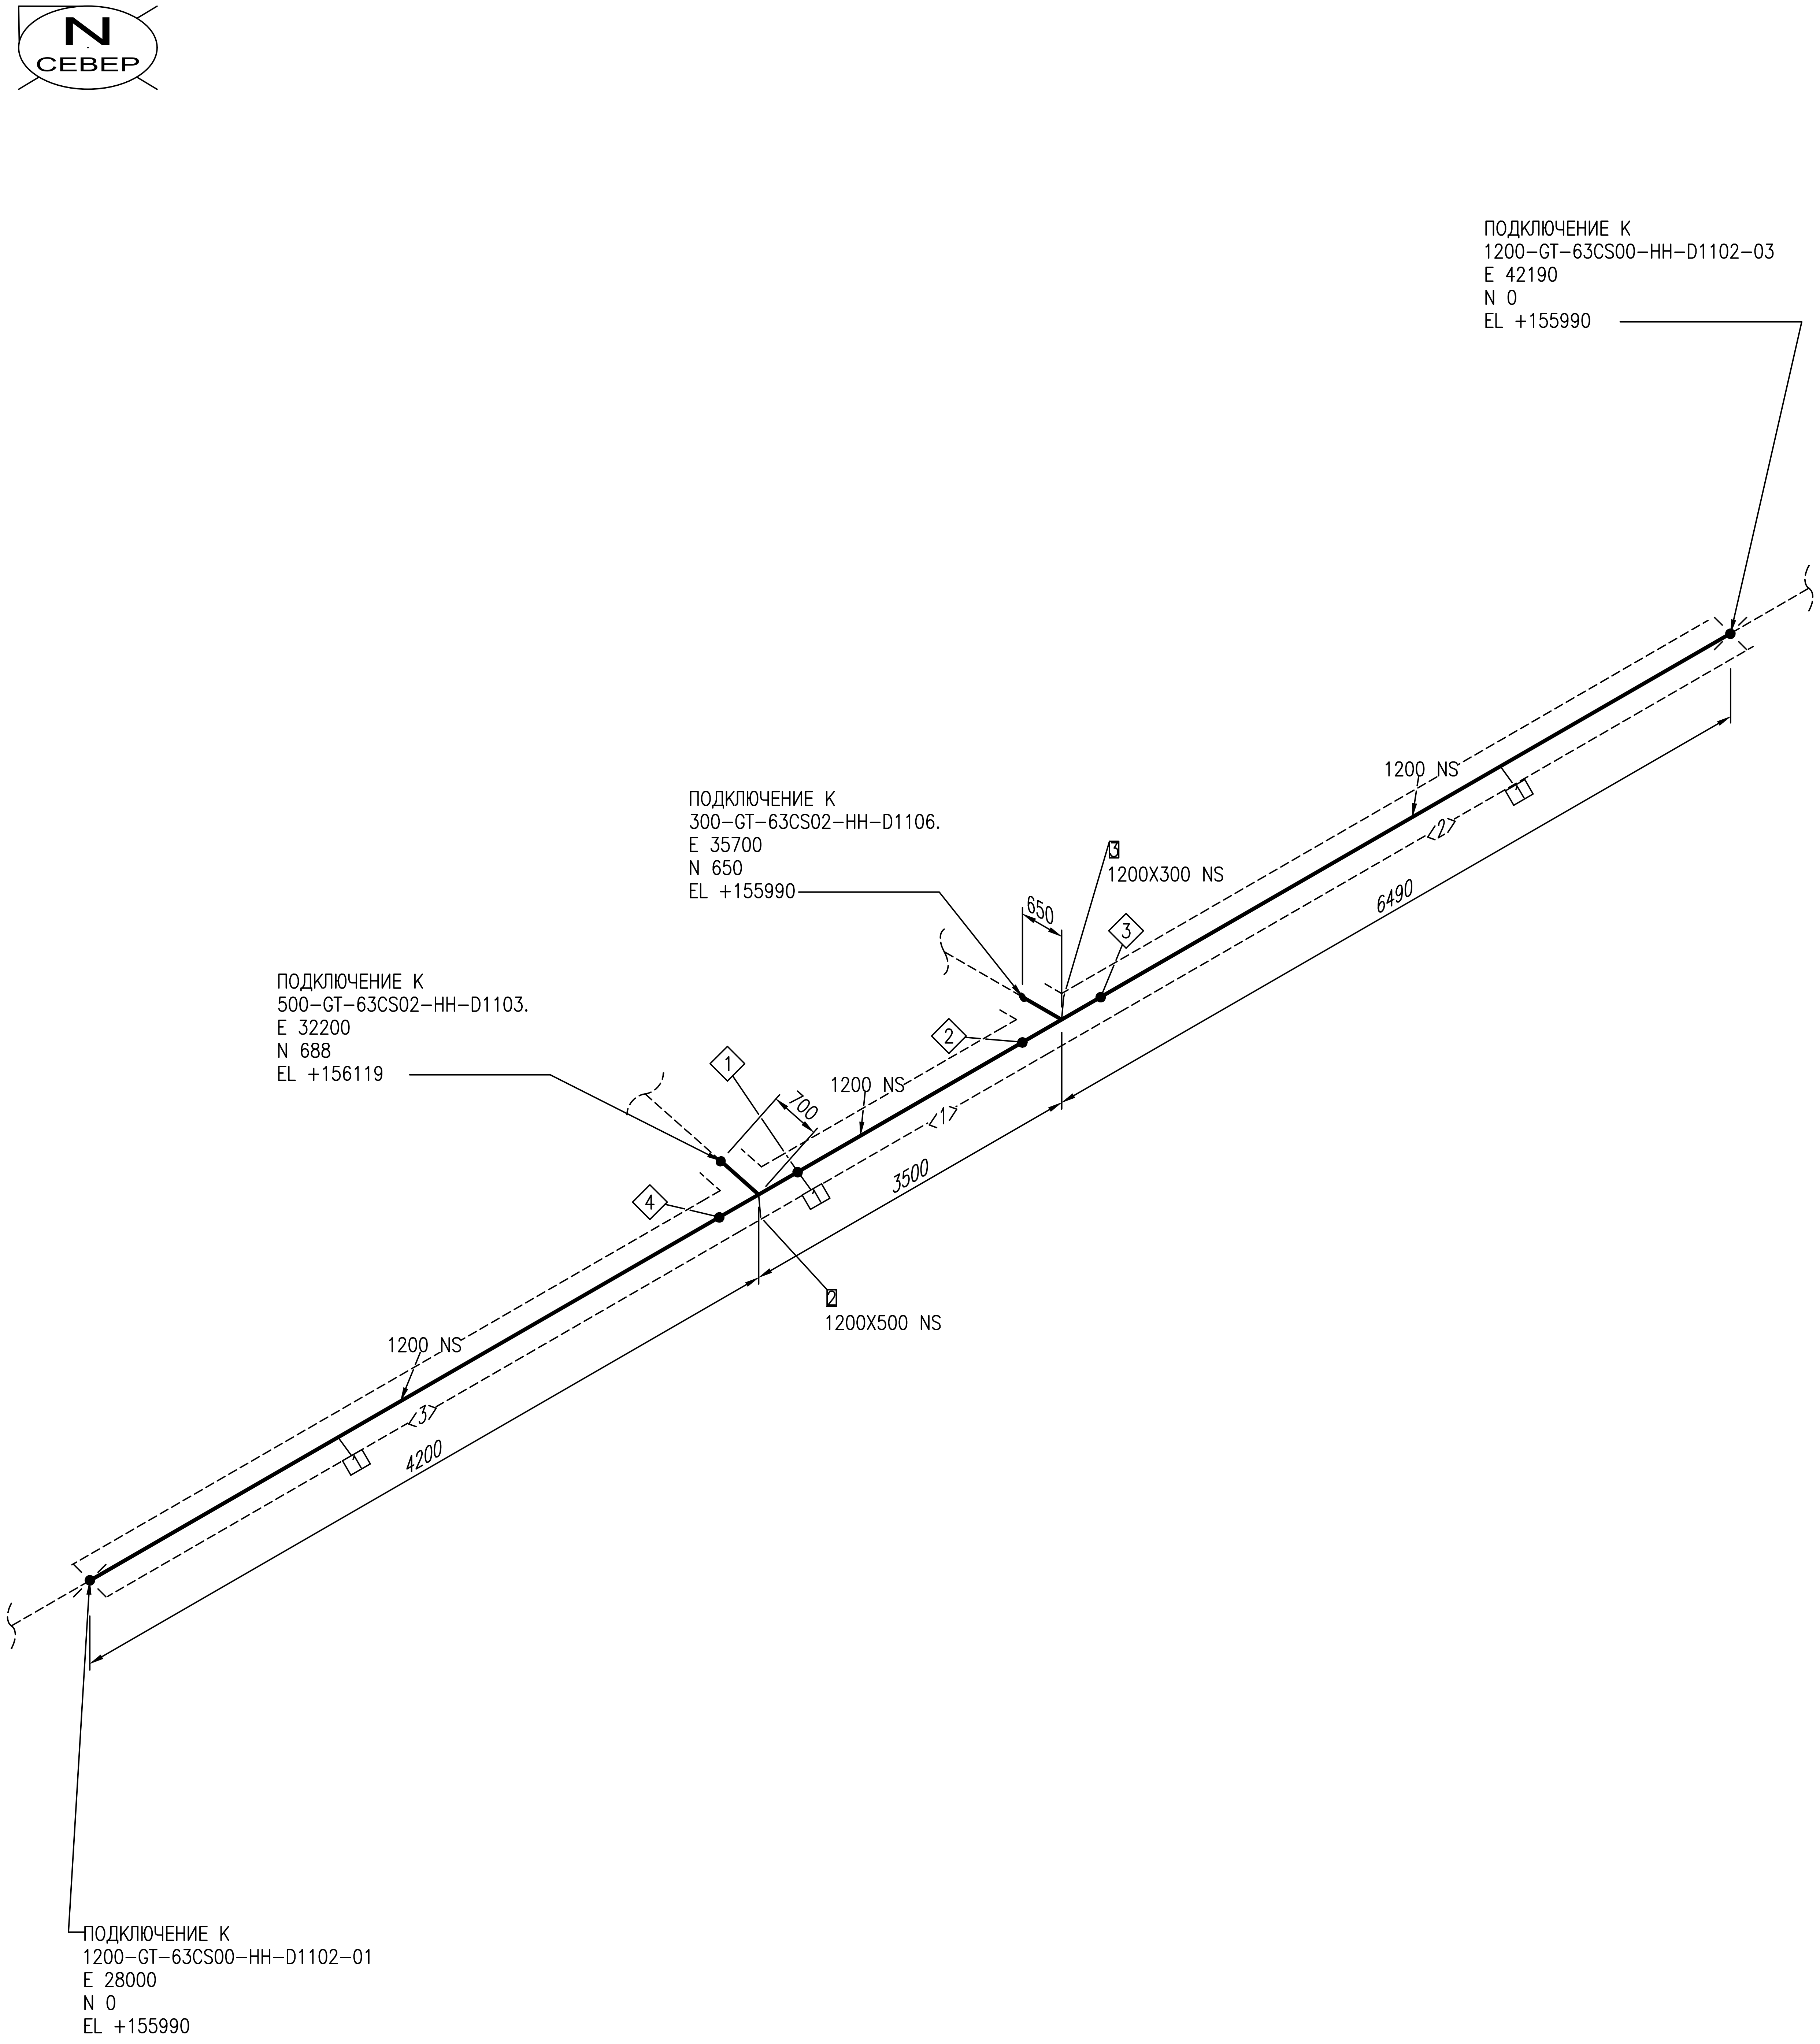

### ПЕРЕЧЕНЬ СВАРНЫХ ШВОВ

| № | DN | ТИП |
|---|---|---|
| 1 | 1200 | BUTTWELD |
| 2 | 1200 | BUTTWELD |
| 3 | 1200 | BUTTWELD |
| 4 | 1200 | BUTTWELD |

### ПЕРЕЧЕНЬ ТРУБНЫХ КАТУШЕК

| № | DN | ДЛИНА |
|---|---|---|
| 1 | 1200 | 2520ММ |
| 2 | 1200 | 6000ММ |
| 3 | 1200 | 3710ММ |

### СПЕЦИФИКАЦИЯ ИЗДЕЛИЙ И МАТЕРИАЛОВ

| ПОЗ. | НАИМЕНОВАНИЕ | СТАНДАРТ | КОЛ. | ПРИМЕЧАНИЕ |
|---|---|---|---|---|
| 1 | Трубы стальные сварные прямошовные, типа 3, К60, 1220Х12 | ГОСТ 31447-2012 | 12.3М | ТРУБА УЧТЕНА В ЛИНЕЙНОЙ ЧАСТИ ПРОЕКТА |
| 2 | Тройник Т I 1220(13К60)-530(8К60)-5,5(6,9)-0,75-30, сталь К60 | ТУ 1469-017-38948552-2015 | 1 | |
| 3 | Тройник Т I 1220(13К60)-325(10К48)-5,5(6,9)-0,75-30, сталь К60 | ТУ 1469-017-38948552-2015 | 1 | |

| Трубопровод | ДАННЫЕ ПО ТРУБОПРОВОДУ | | |
|---|---|---|---|
| 1200-GT-63CS00-HH-D1102 | Расчетные параметры | Температура | -26,9...+85 °C |
| | | Давление | 6,3 MPa |
| | Рабочие параметры | Температура | -20...+40 °C |
| | | Давление | 5,5 MPa |
| Ссылочные чертежи No | Параметры испытания | Тип | Гидравлическое |
| EWE0426-MGL1-PRE-054-SCM-610102 | | Давление | 6,9 MPa |
| | Изоляция | Тип | НН |
| | | Толщина | mm |
| | Катодная защита | Да или Нет | Да |

| Рев. | Дата | Назначение ревизии | Проверил | Утвердил |
|---|---|---|---|---|
| A1 | 25.09.2026 | Утверждено для строительства | | |
| R1 | 27.08.2026 | Выпущено для рассмотрения | | |

ЗАКАЗЧИК: UTG UZTRANSGAZ
ГЕНЕРАЛЬНЫЙ ПОДРЯДЧИК: UET UZBEKENERGOTAMIR
ПОДРЯДЧИК: PBG Pro Build Generation
ГЕНЕРАЛЬНЫЙ ПРОЕКТИРОВЩИК: EAST WEST ENGINEERING

EWE0426-MGL1-PRE-054-ISO-690604-A1

«СТРОИТЕЛЬСТВО НОВЫХ НИТОК (УЧАСТКОВ) ГАЗОПРОВОДОВ «ГАЗЛИ - САРИМОЙ» И «АКЧАЛОК - ГАЗЛИ - НУКУС» ОБЩЕЙ ПРОТЯЖЕННОСТЬЮ НЕ МЕНЕЕ 275 КМ».

| Изм. | Кол.уч. | Лист | №док. | Подпись | Дата |
|---|---|---|---|---|---|
| ГИП | | Кирпичников С. | | | 09.2026 |
| Нач.отд. | | Рябинин А. | | | 09.2026 |
| Исполн. | | Таштимуров Р. | | | 09.2026 |
| Н.контр | | Кирпичников С. | | | 09.2026 |

ГАЗОПРОВОД «ГАЗЛИ-САРИМОЙ» (54 КМ)
Узел приема/запуска очистных устройств DN1200.УЗПОУ-D11.

| Стадия | Лист | Листов |
|---|---|---|
| РД | 2 | 8 |

Изометрический чертеж трубопровода
1200-GT-63CS00-HH-D1102

EAST WEST ENGINEERING
ООО "EAST-WEST Engineering"
г. Ташкент 2026г.

Взам. инв. №
Подпись и дата
Инв.№ подл.

Формат А2 594х420

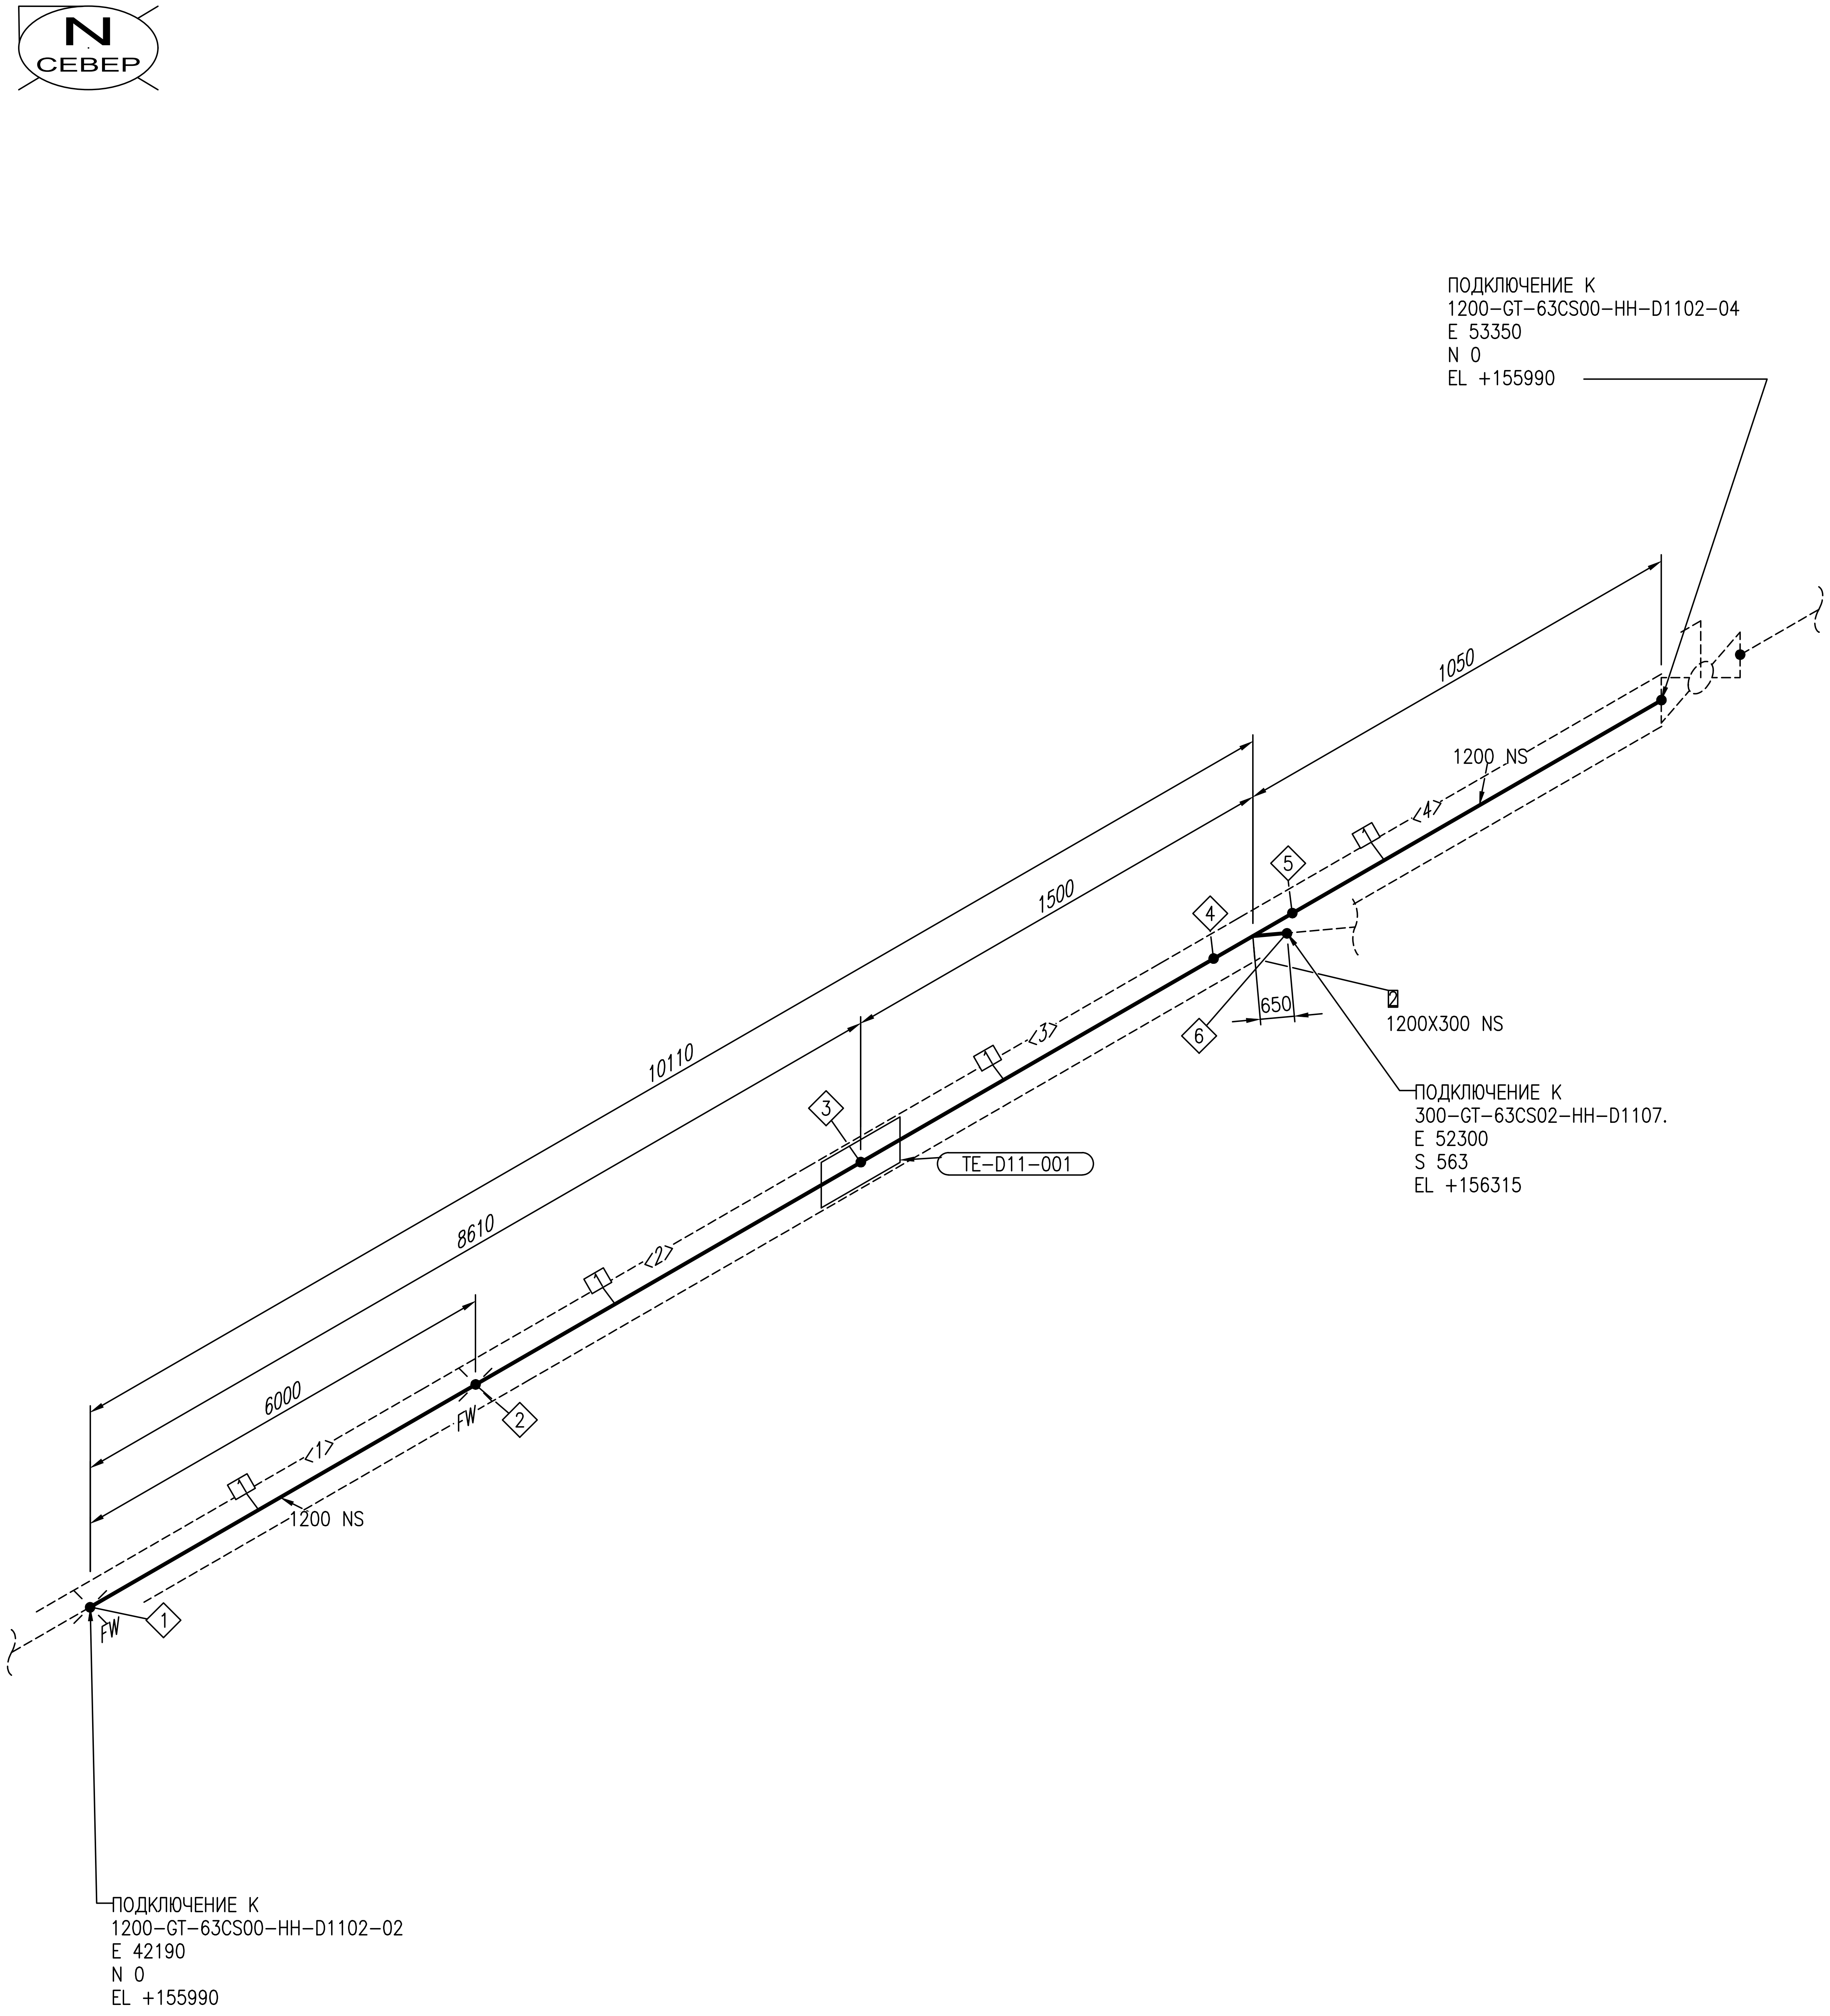

ПЕРЕЧЕНЬ СВАРНЫХ ШВОВ

| № | DN | ТИП |
|---|---|---|
| 1 | 1200 | FIELDWELD |
| 2 | 1200 | FIELDWELD |
| 3 | 1200 | INSTRUMENT |
| 4 | 1200 | BUTTWELD |
| 5 | 1200 | BUTTWELD |
| 6 | 300 | BUTTWELD |

СПЕЦИФИКАЦИЯ ИЗДЕЛИЙ И МАТЕРИАЛОВ

| ПОЗ. | НАИМЕНОВАНИЕ | СТАНДАРТ | КОЛ. | ПРИМЕЧАНИЕ |
|---|---|---|---|---|
| 1 | Трубы стальные сварные прямошовные, типа 3, К60, 1220Х12 | ГОСТ 31447–2012 | 10.2М | ТРУБА УЧТЕНА В ЛИНЕЙНОЙ ЧАСТИ ПРОЕКТА |
| 2 | Тройник Т I 1220(13К60)–325(10К48)–5,5(6,9)–0,75–30, сталь К60 | ТУ 1469–017–38948552–2015 | 1 | |

ПЕРЕЧЕНЬ ТРУБНЫХ КАТУШЕК

| № | DN | ДЛИНА |
|---|---|---|
| 1 | 1200 | 6000ММ |
| 2 | 1200 | 2610ММ |
| 3 | 1200 | 1010ММ |
| 4 | 1200 | 560ММ |

| Трубопровод | ДАННЫЕ ПО ТРУБОПРОВОДУ | | |
|---|---|---|---|
| 1200-GT-63CS00-HH-D1102 | Расчетные параметры | Температура | -26,9...+85 °C |
| | | Давление | 6,3 MPa |
| | Рабочие параметры | Температура | -20...+40 °C |
| | | Давление | 5,5 MPa |
| | Параметры испытания | Тип | Гидравлическое |
| Ссылочные чертежи No | | Давление | 6,9 MPa |
| EWE0426-MGL1-PRE-054-SCM-610102 | Изоляция | Тип | HH |
| | | Толщина | mm |
| | Катодная защита | Да или Нет | Да |

| Рев. | Дата | Назначение ревизии | Проверил | Утвердил |
|---|---|---|---|---|
| A1 | 25.09.2026 | Утверждено для строительства | | |
| R1 | 27.08.2026 | Выпущено для рассмотрения | | |

ЗАКАЗЧИК: UTG UZTRANSGAZ

ГЕНЕРАЛЬНЫЙ ПОДРЯДЧИК: UET UZBEKENERGOTAMIR

ПОДРЯДЧИК: PBG Pre Build Generation

ГЕНЕРАЛЬНЫЙ ПРОЕКТИРОВЩИК: EAST WEST ENGINEERING

EWE0426-MGL1-PRE-054-ISO-690604-A1

«СТРОИТЕЛЬСТВО НОВЫХ НИТОК (УЧАСТКОВ) ГАЗОПРОВОДОВ «ГАЗЛИ – САРИМОЙ» И «АКЧАЛОК – ГАЗЛИ – НУКУС» ОБЩЕЙ ПРОТЯЖЕННОСТЬЮ НЕ МЕНЕЕ 275 КМ».

| Изм. | Кол.уч. | Лист | №док. | Подпись | Дата |
|---|---|---|---|---|---|
| ГИП | | Кирпичников С. | | | 09.2026 |
| Нач.отд. | | Рябинин А. | | | 09.2026 |
| Исполн. | | Таштимуров Р. | | | 09.2026 |
| Н.контр | | Кирпичников С. | | | 09.2026 |

ГАЗОПРОВОД «ГАЗЛИ-САРИМОЙ» (54 КМ)
Узел приема/запуска очистных устройств DN1200.УЗПОУ-D11.

| Стадия | Лист | Листов |
|---|---|---|
| РД | 3 | 8 |

Изометрический чертеж трубопровода
1200-GT-63CS00-HH-D1102

ООО "EAST-WEST Engineering"
г. Ташкент 2026г.

Взам. инв. №
Подпись и дата
Инв.№ подл.

Формат А2 594x420

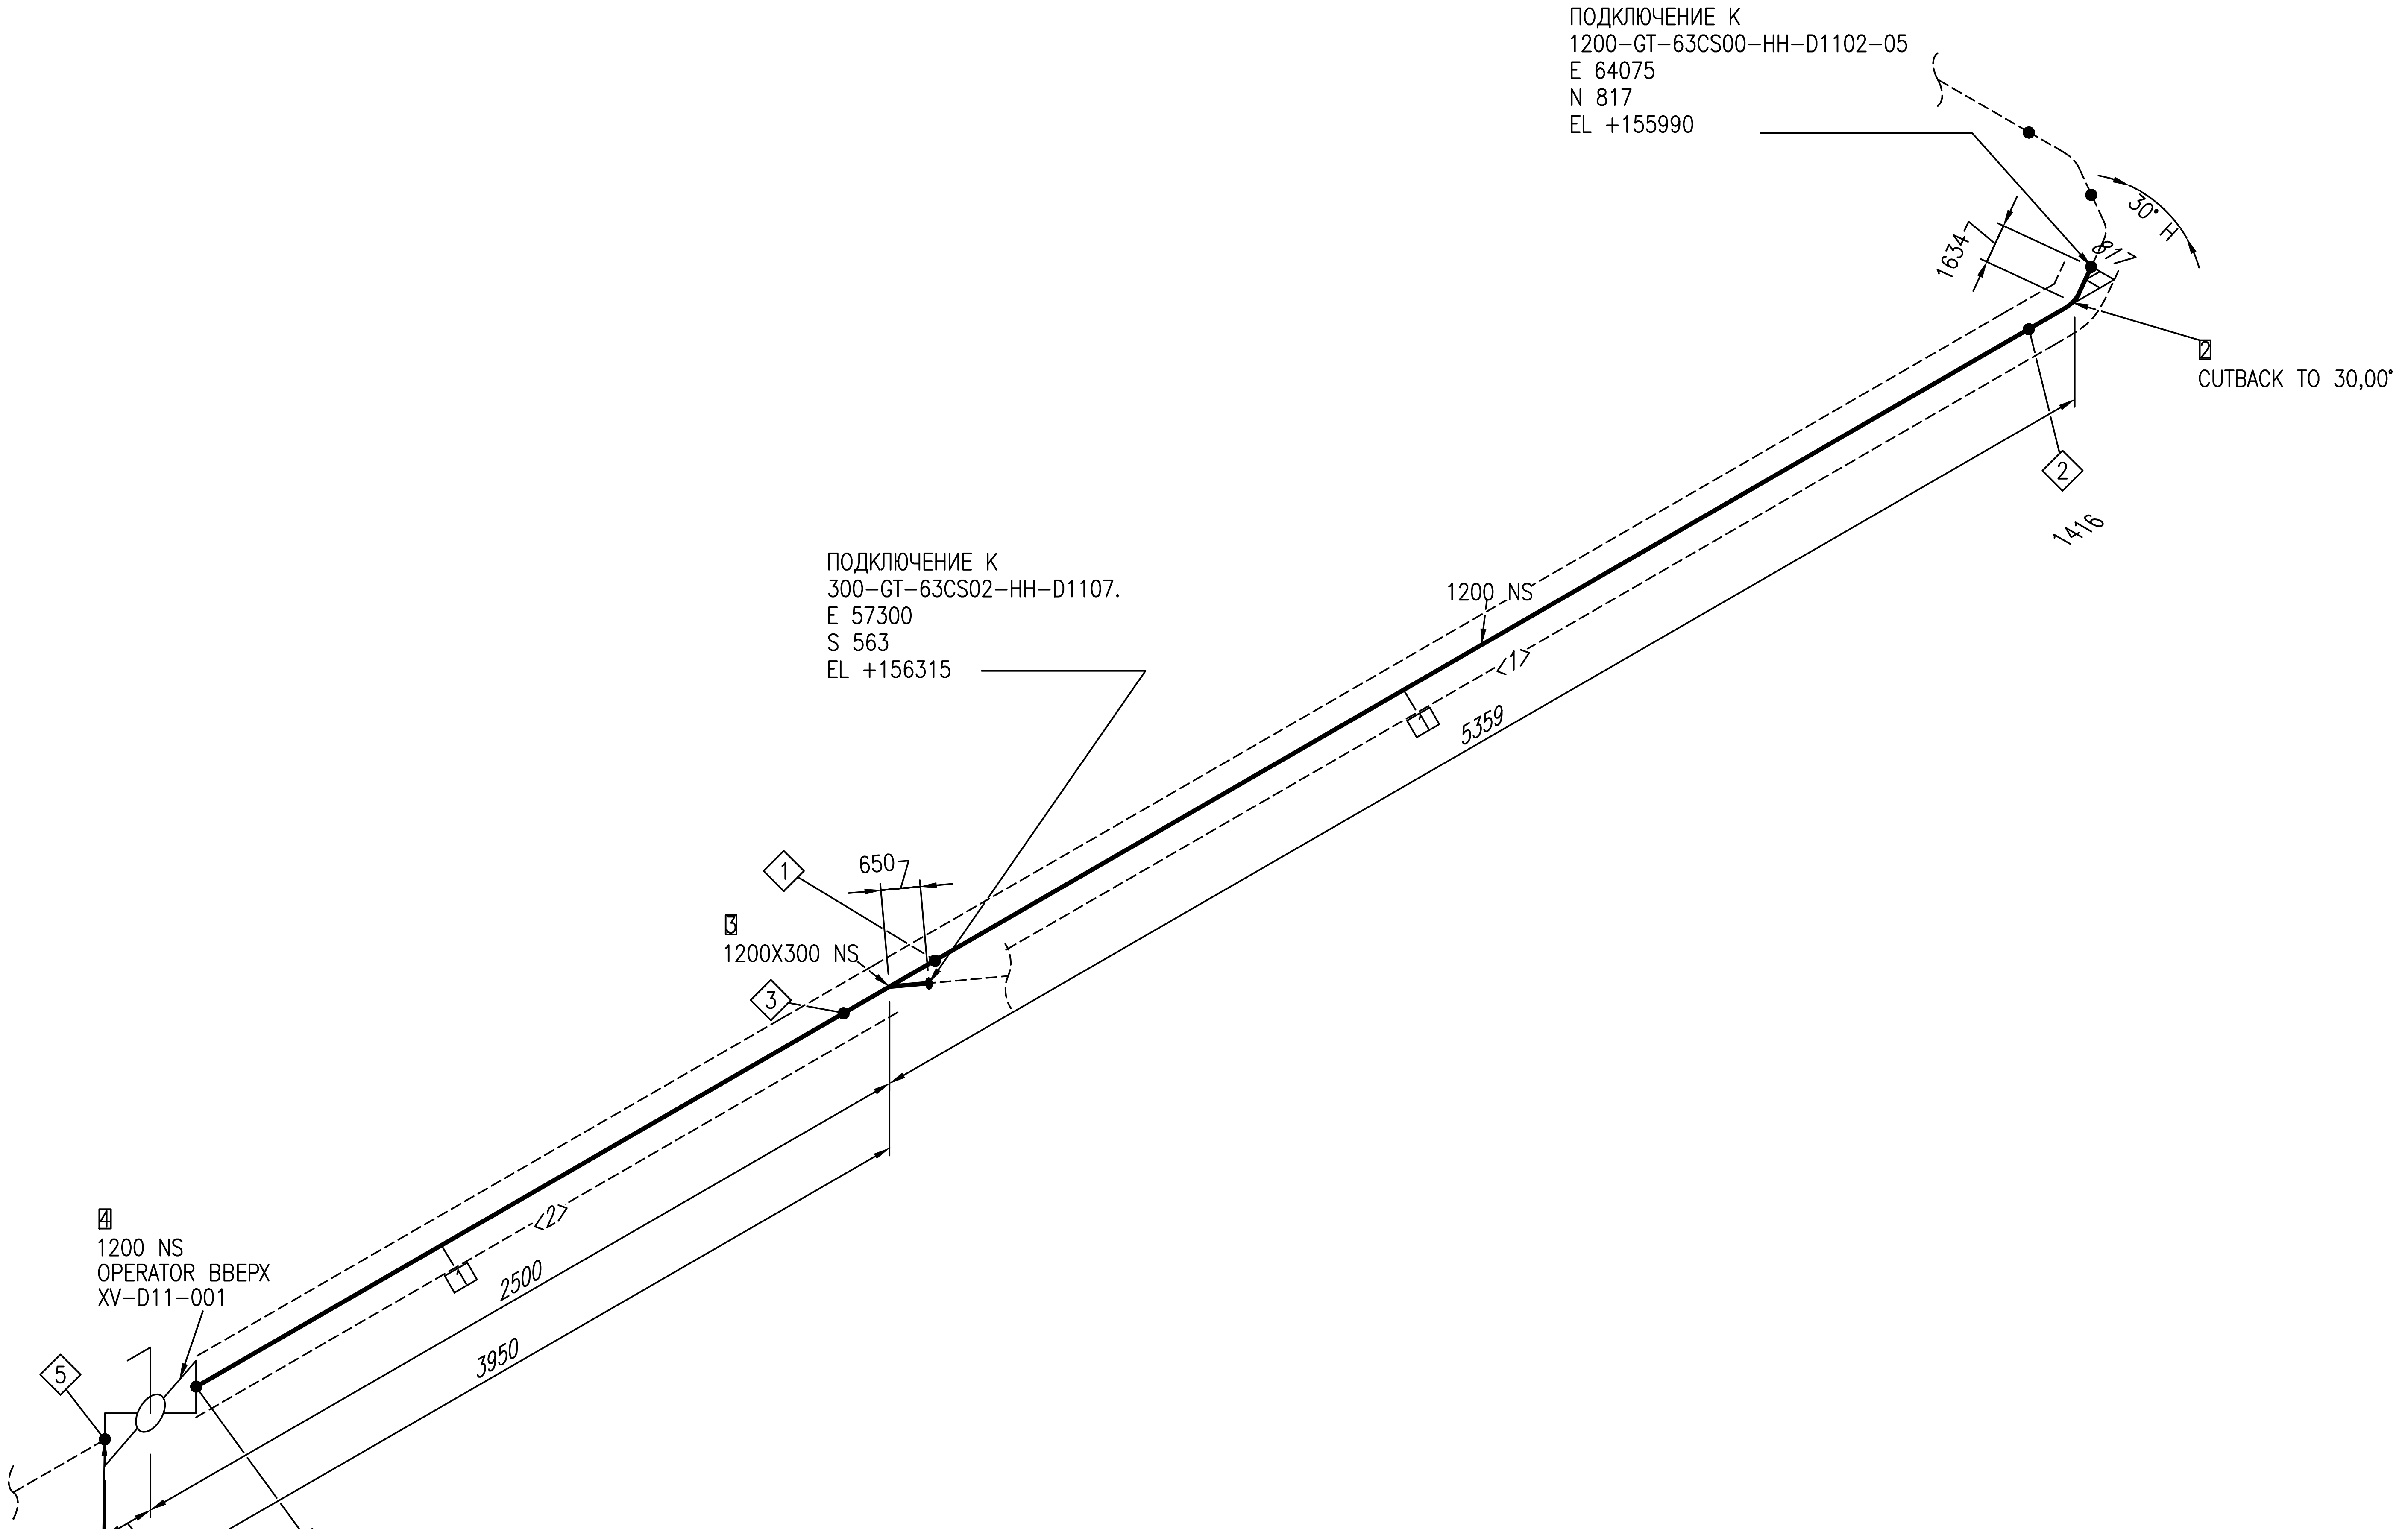

ПЕРЕЧЕНЬ СВАРНЫХ ШВОВ

| № | DN | ТИП |
|---|---|---|
| 1 | 1200 | BUTTWELD |
| 2 | 1200 | BUTTWELD |
| 3 | 1200 | BUTTWELD |
| 4 | 1200 | BUTTWELD |
| 5 | 1200 | BUTTWELD |

ПЕРЕЧЕНЬ ТРУБНЫХ КАТУШЕК

| № | DN | ДЛИНА |
|---|---|---|
| 1 | 1200 | 3235MM |
| 2 | 1200 | 560MM |

СПЕЦИФИКАЦИЯ ИЗДЕЛИЙ И МАТЕРИАЛОВ

| ПОЗ. | НАИМЕНОВАНИЕ | СТАНДАРТ | КОЛ. | ПРИМЕЧАНИЕ |
|---|---|---|---|---|
| 1 | Трубы стальные сварные прямошовные, типа 3, К60, 1220X12 | ГОСТ 31447-2012 | 3.8M | ТРУБА УЧТЕНА В ЛИНЕЙНОЙ ЧАСТИ ПРОЕКТА |
| 2 | ОСС 30°-5Д-1220 (12К60)-5,5-075-У ТУ51-29-81 | ТУ 51-29-81 | 1 | |
| 3 | Тройник Т I 1220(13К60)-325(10К48)-5,5(6,9)-0,75-30, сталь К60 | ТУ 1469-017-38948552-2015 | 1 | |
| 4 | Кран шаровой DN1200 PN-6,3 МПа с пневмогидроприводом, приварной, подземный | EWE0426-MGL1-PRE-054-DSH-610127 | 1 | |

| Трубопровод | ДАННЫЕ ПО ТРУБОПРОВОДУ | | |
|---|---|---|---|
| 1200-GT-63CS00-HH-D1102 | Расчетные параметры | Температура | -26,9...+85 °C |
| | | Давление | 6,3 MPa |
| | Рабочие параметры | Температура | -20...+40 °C |
| | | Давление | 5,5 MPa |
| | Параметры испытания | Тип | Гидравлическое |
| Ссылочные чертежи No | | Давление | 6,9 MPa |
| EWE0426-MGL1-PRE-054-SCM-610102 | Изоляция | Тип | HH |
| | | Толщина | mm |
| | Катодная защита | Да или Нет | Да |

| Рев. | Дата | Назначение ревизии | Проверил | Утвердил |
|---|---|---|---|---|
| A1 | 25.09.2026 | Утверждено для строительства | | |
| R1 | 27.08.2026 | Выпущено для рассмотрения | | |

ЗАКАЗЧИК: UTG UZTRANSGAZ

ГЕНЕРАЛЬНЫЙ ПОДРЯДЧИК: UET UZBEKENERGOTAMIR

ПОДРЯДЧИК: PBG Pre Build Generation

ГЕНЕРАЛЬНЫЙ ПРОЕКТИРОВЩИК: EAST WEST ENGINEERING

## EWE0426-MGL1-PRE-054-ISO-690604-A1

«СТРОИТЕЛЬСТВО НОВЫХ НИТОК (УЧАСТКОВ) ГАЗОПРОВОДОВ «ГАЗЛИ - САРИМОЙ» И «АКЧАЛОК - ГАЗЛИ - НУКУС» ОБЩЕЙ ПРОТЯЖЕННОСТЬЮ НЕ МЕНЕЕ 275 КМ».

| Изм. | Кол.уч. | Лист | №док. | Подпись | Дата |
|---|---|---|---|---|---|
| ГИП | | Кирпичников С. | | | 09.2026 |
| Нач.отд. | | Рябинин А. | | | 09.2026 |
| Исполн. | | Таштимуров Р. | | | 09.2026 |
| Н.контр | | Кирпичников С. | | | 09.2026 |

ГАЗОПРОВОД «ГАЗЛИ-САРИМОЙ» (54 КМ)
Узел приема/запуска очистных устройств DN1200.УЗПОУ-D11.

| Стадия | Лист | Листов |
|---|---|---|
| РД | 4 | 8 |

Изометрический чертеж трубопровода
1200-GT-63CS00-HH-D1102

ООО "EAST-WEST Engineering"
г. Ташкент 2026г.

Взам. инв. №
Подпись и дата
Инв.№ подл.

Формат А2 594x420

N
СЕВЕР

| ПЕРЕЧЕНЬ СВАРНЫХ ШВОВ | | |
|---|---|---|
| № | DN | ТИП |
| 1 | 1200 | BUTTWELD |
| 2 | 1200 | BUTTWELD |
| 3 | 1200 | BUTTWELD |
| 4 | 1200 | FIELDWELD |
| 5 | 1200 | BUTTWELD |

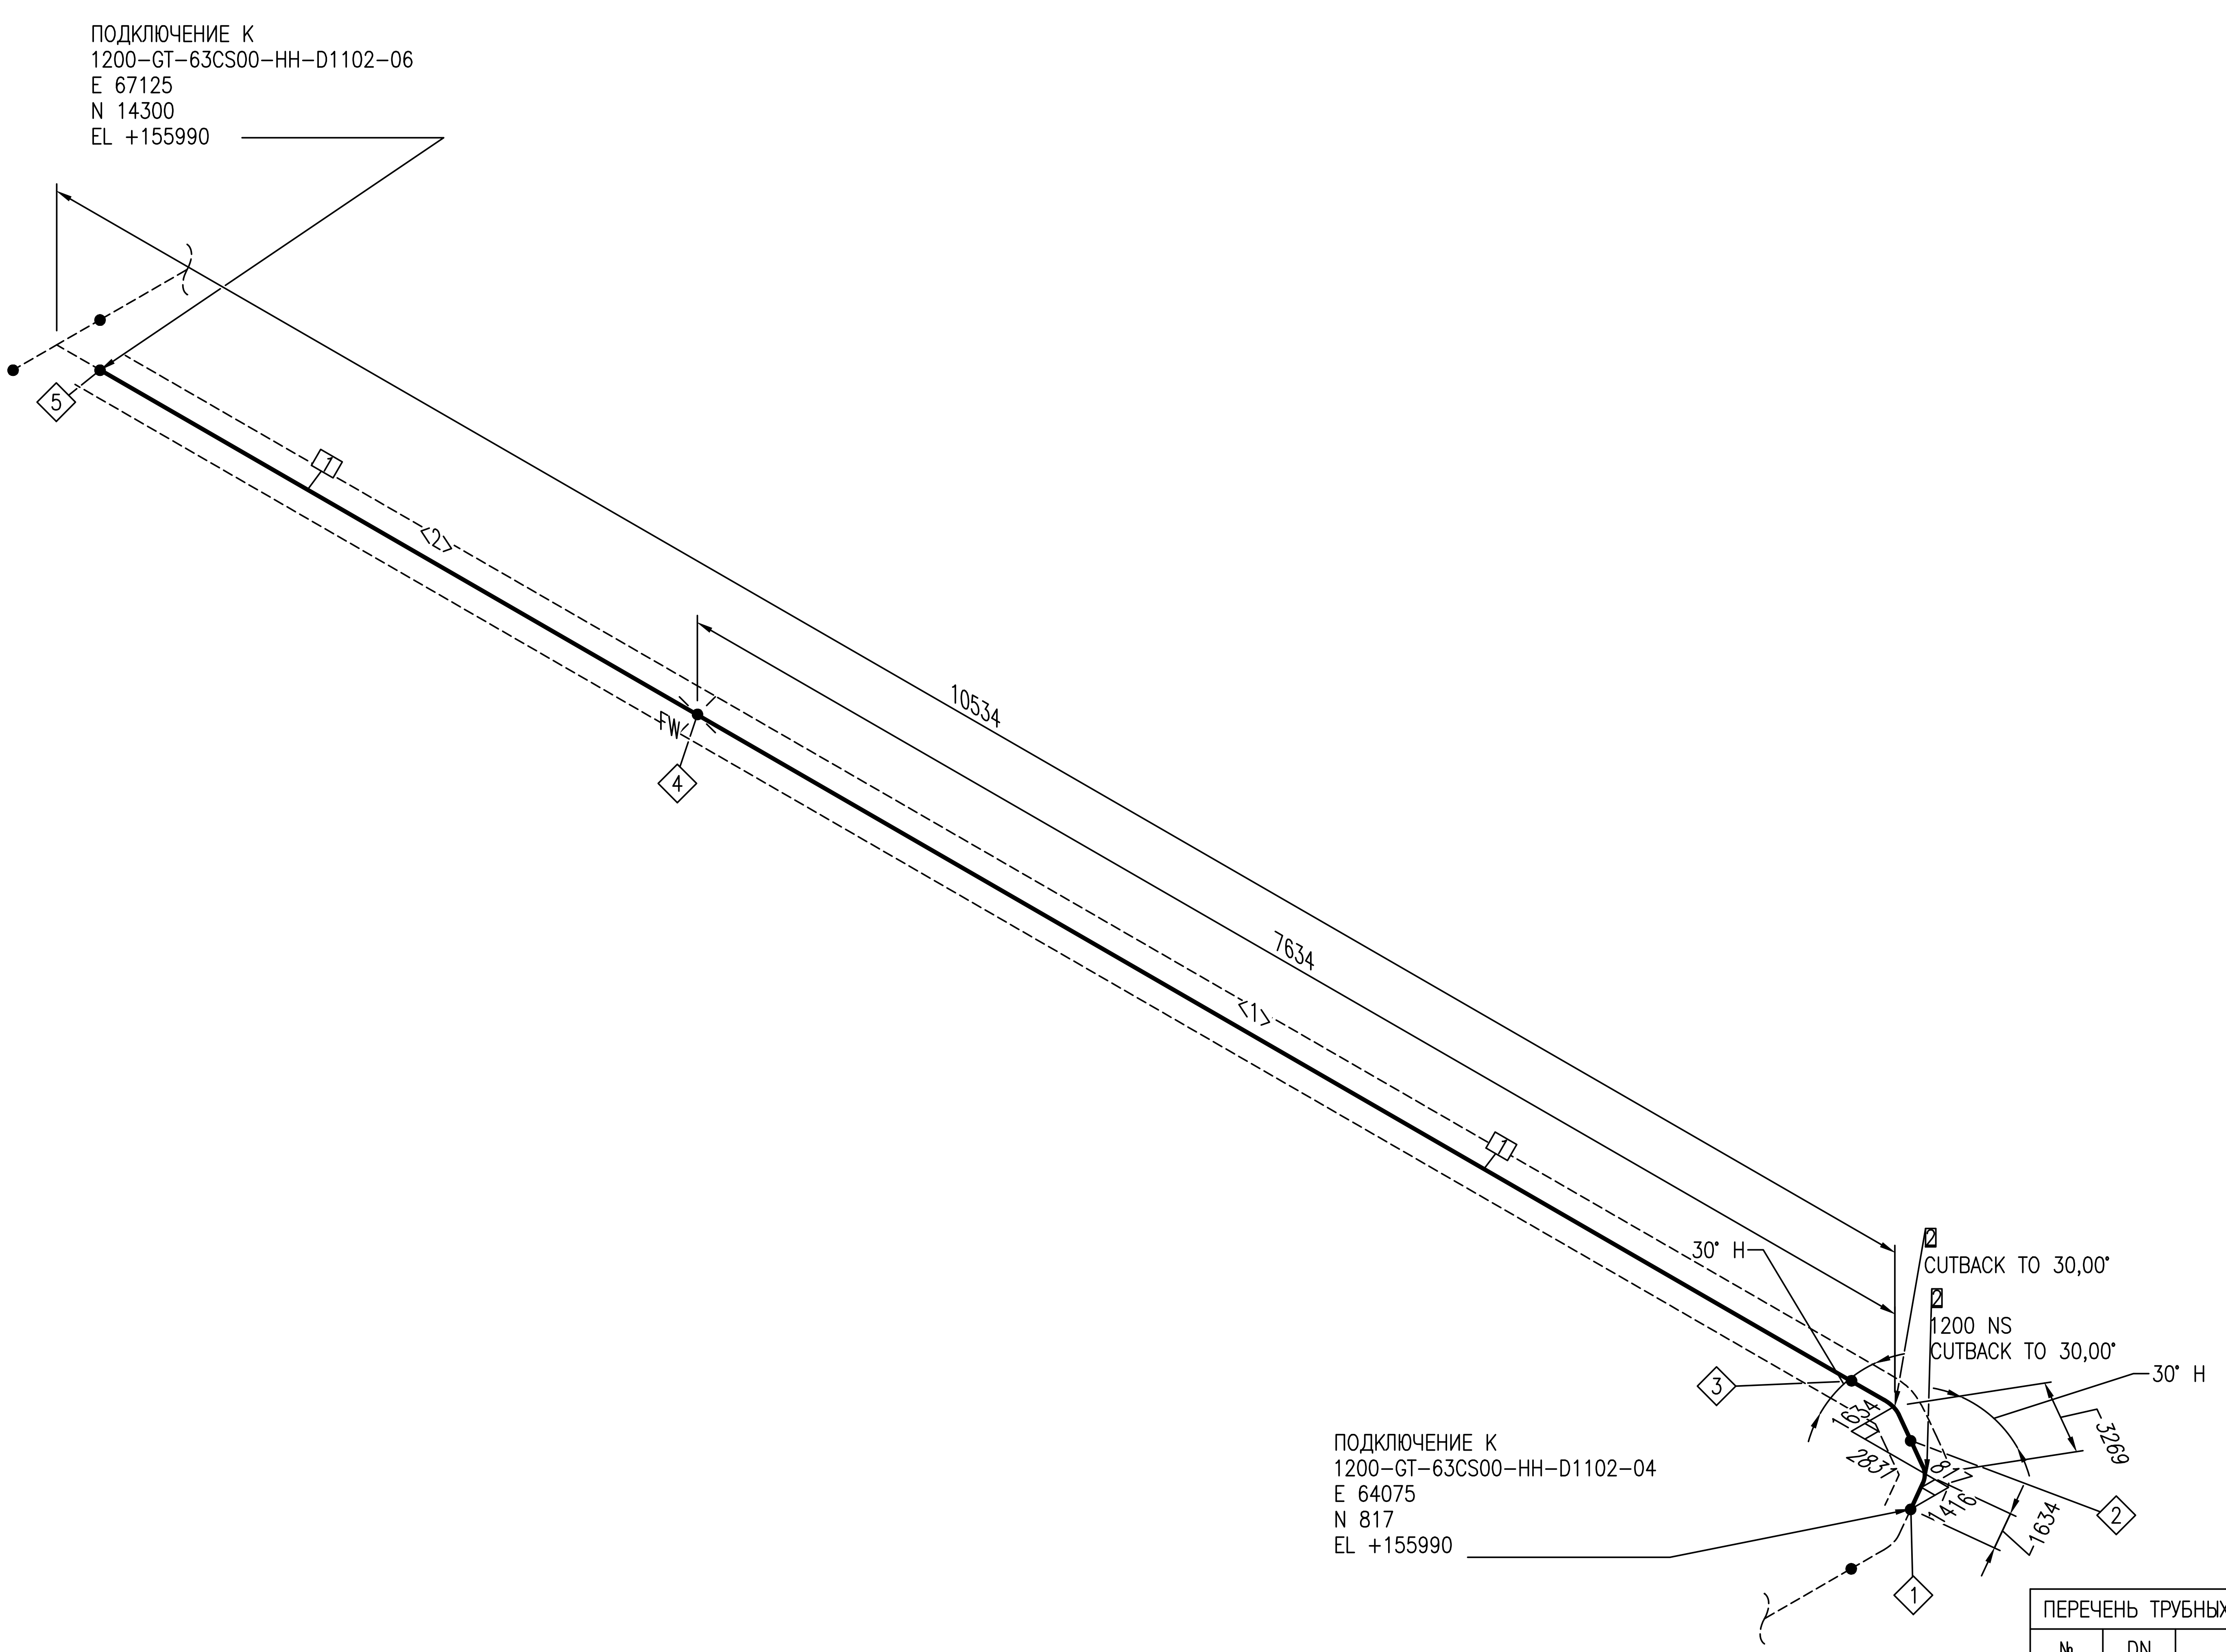

| ПЕРЕЧЕНЬ ТРУБНЫХ КАТУШЕК | | |
|---|---|---|
| № | DN | ДЛИНА |
| 1 | 1200 | 6000ММ |
| 2 | 1200 | 2200ММ |

## СПЕЦИФИКАЦИЯ ИЗДЕЛИЙ И МАТЕРИАЛОВ

| ПОЗ. | НАИМЕНОВАНИЕ | СТАНДАРТ | КОЛ. | ПРИМЕЧАНИЕ |
|---|---|---|---|---|
| 1 | Трубы стальные сварные прямошовные, типа 3, К60, 1220Х12 | ГОСТ 31447-2012 | 8.2М | ТРУБА УЧТЕНА В ЛИНЕЙНОЙ ЧАСТИ ПРОЕКТА |
| 2 | ОСС 30°-5Д-1220 (12К60)-5,5-075-У ТУ51-29-81 | ТУ 51-29-81 | 2 | |

| Трубопровод | ДАННЫЕ ПО ТРУБОПРОВОДУ | | |
|---|---|---|---|
| 1200-GT-63CS00-HH-D1102 | Расчетные параметры | Температура | -26,9...+85 °C |
| | | Давление | 6,3 MPa |
| | Рабочие параметры | Температура | -20...+40 °C |
| | | Давление | 5,5 MPa |
| Ссылочные чертежи No | Параметры испытания | Тип | Гидравлическое |
| EWE0426-MGL1-PRE-054-SCM-610102 | | Давление | 6,9 MPa |
| | Изоляция | Тип | НН |
| | | Толщина | mm |
| | Катодная защита | Да или Нет | Да |

| Рев. | Дата | Назначение ревизии | Проверил | Утвердил |
|---|---|---|---|---|
| | | | | |
| | | | | |
| A1 | 25.09.2026 | Утверждено для строительства | | |
| R1 | 27.08.2026 | Выпущено для рассмотрения | | |

ЗАКАЗЧИК: UTG UZTRANSGAZ
ГЕНЕРАЛЬНЫЙ ПОДРЯДЧИК: UET UZBEKENERGOTAMIR
ПОДРЯДЧИК: PBG Pre Build Generation
ГЕНЕРАЛЬНЫЙ ПРОЕКТИРОВЩИК: EAST WEST ENGINEERING

# EWE0426-MGL1-PRE-054-ISO-690604-A1

«СТРОИТЕЛЬСТВО НОВЫХ НИТОК (УЧАСТКОВ) ГАЗОПРОВОДОВ «ГАЗЛИ - САРИМОЙ» И «АКЧАЛОК - ГАЗЛИ - НУКУС» ОБЩЕЙ ПРОТЯЖЕННОСТЬЮ НЕ МЕНЕЕ 275 КМ».

| Изм. | Кол.уч. | Лист | №док. | Подпись | Дата |
|---|---|---|---|---|---|
| ГИП | | Кирпичников С. | | | 09.2026 |
| Нач.отд. | | Рябинин А. | | | 09.2026 |
| Исполн. | | Таштимуров Р. | | | 09.2026 |
| | | | | | |
| | | | | | |
| Н.контр | | Кирпичников С. | | | 09.2026 |

ГАЗОПРОВОД «ГАЗЛИ-САРИМОЙ» (54 КМ)
Узел приема/запуска очистных устройств DN1200.УЗПОУ-D11.

| Стадия | Лист | Листов |
|---|---|---|
| РД | 5 | 8 |

Изометрический чертеж трубопровода
1200-GT-63CS00-HH-D1102

EAST WEST ENGINEERING
ООО "EAST-WEST Engineering"
г. Ташкент 2026г.

Взам. инв. №
Подпись и дата
Инв.№ подл.

Формат А2 594х420

| ПЕРЕЧЕНЬ СВАРНЫХ ШВОВ | | |
|---|---|---|
| № | DN | ТИП |
| 1 | 1200 | BUTTWELD |
| 2 | 1200 | INSTRUMENT |
| 3 | 1200 | FIELDWELD |
| 4 | 1200 | BUTTWELD |
| 5 | 1200 | BUTTWELD |
| 6 | 1200 | BUTTWELD |

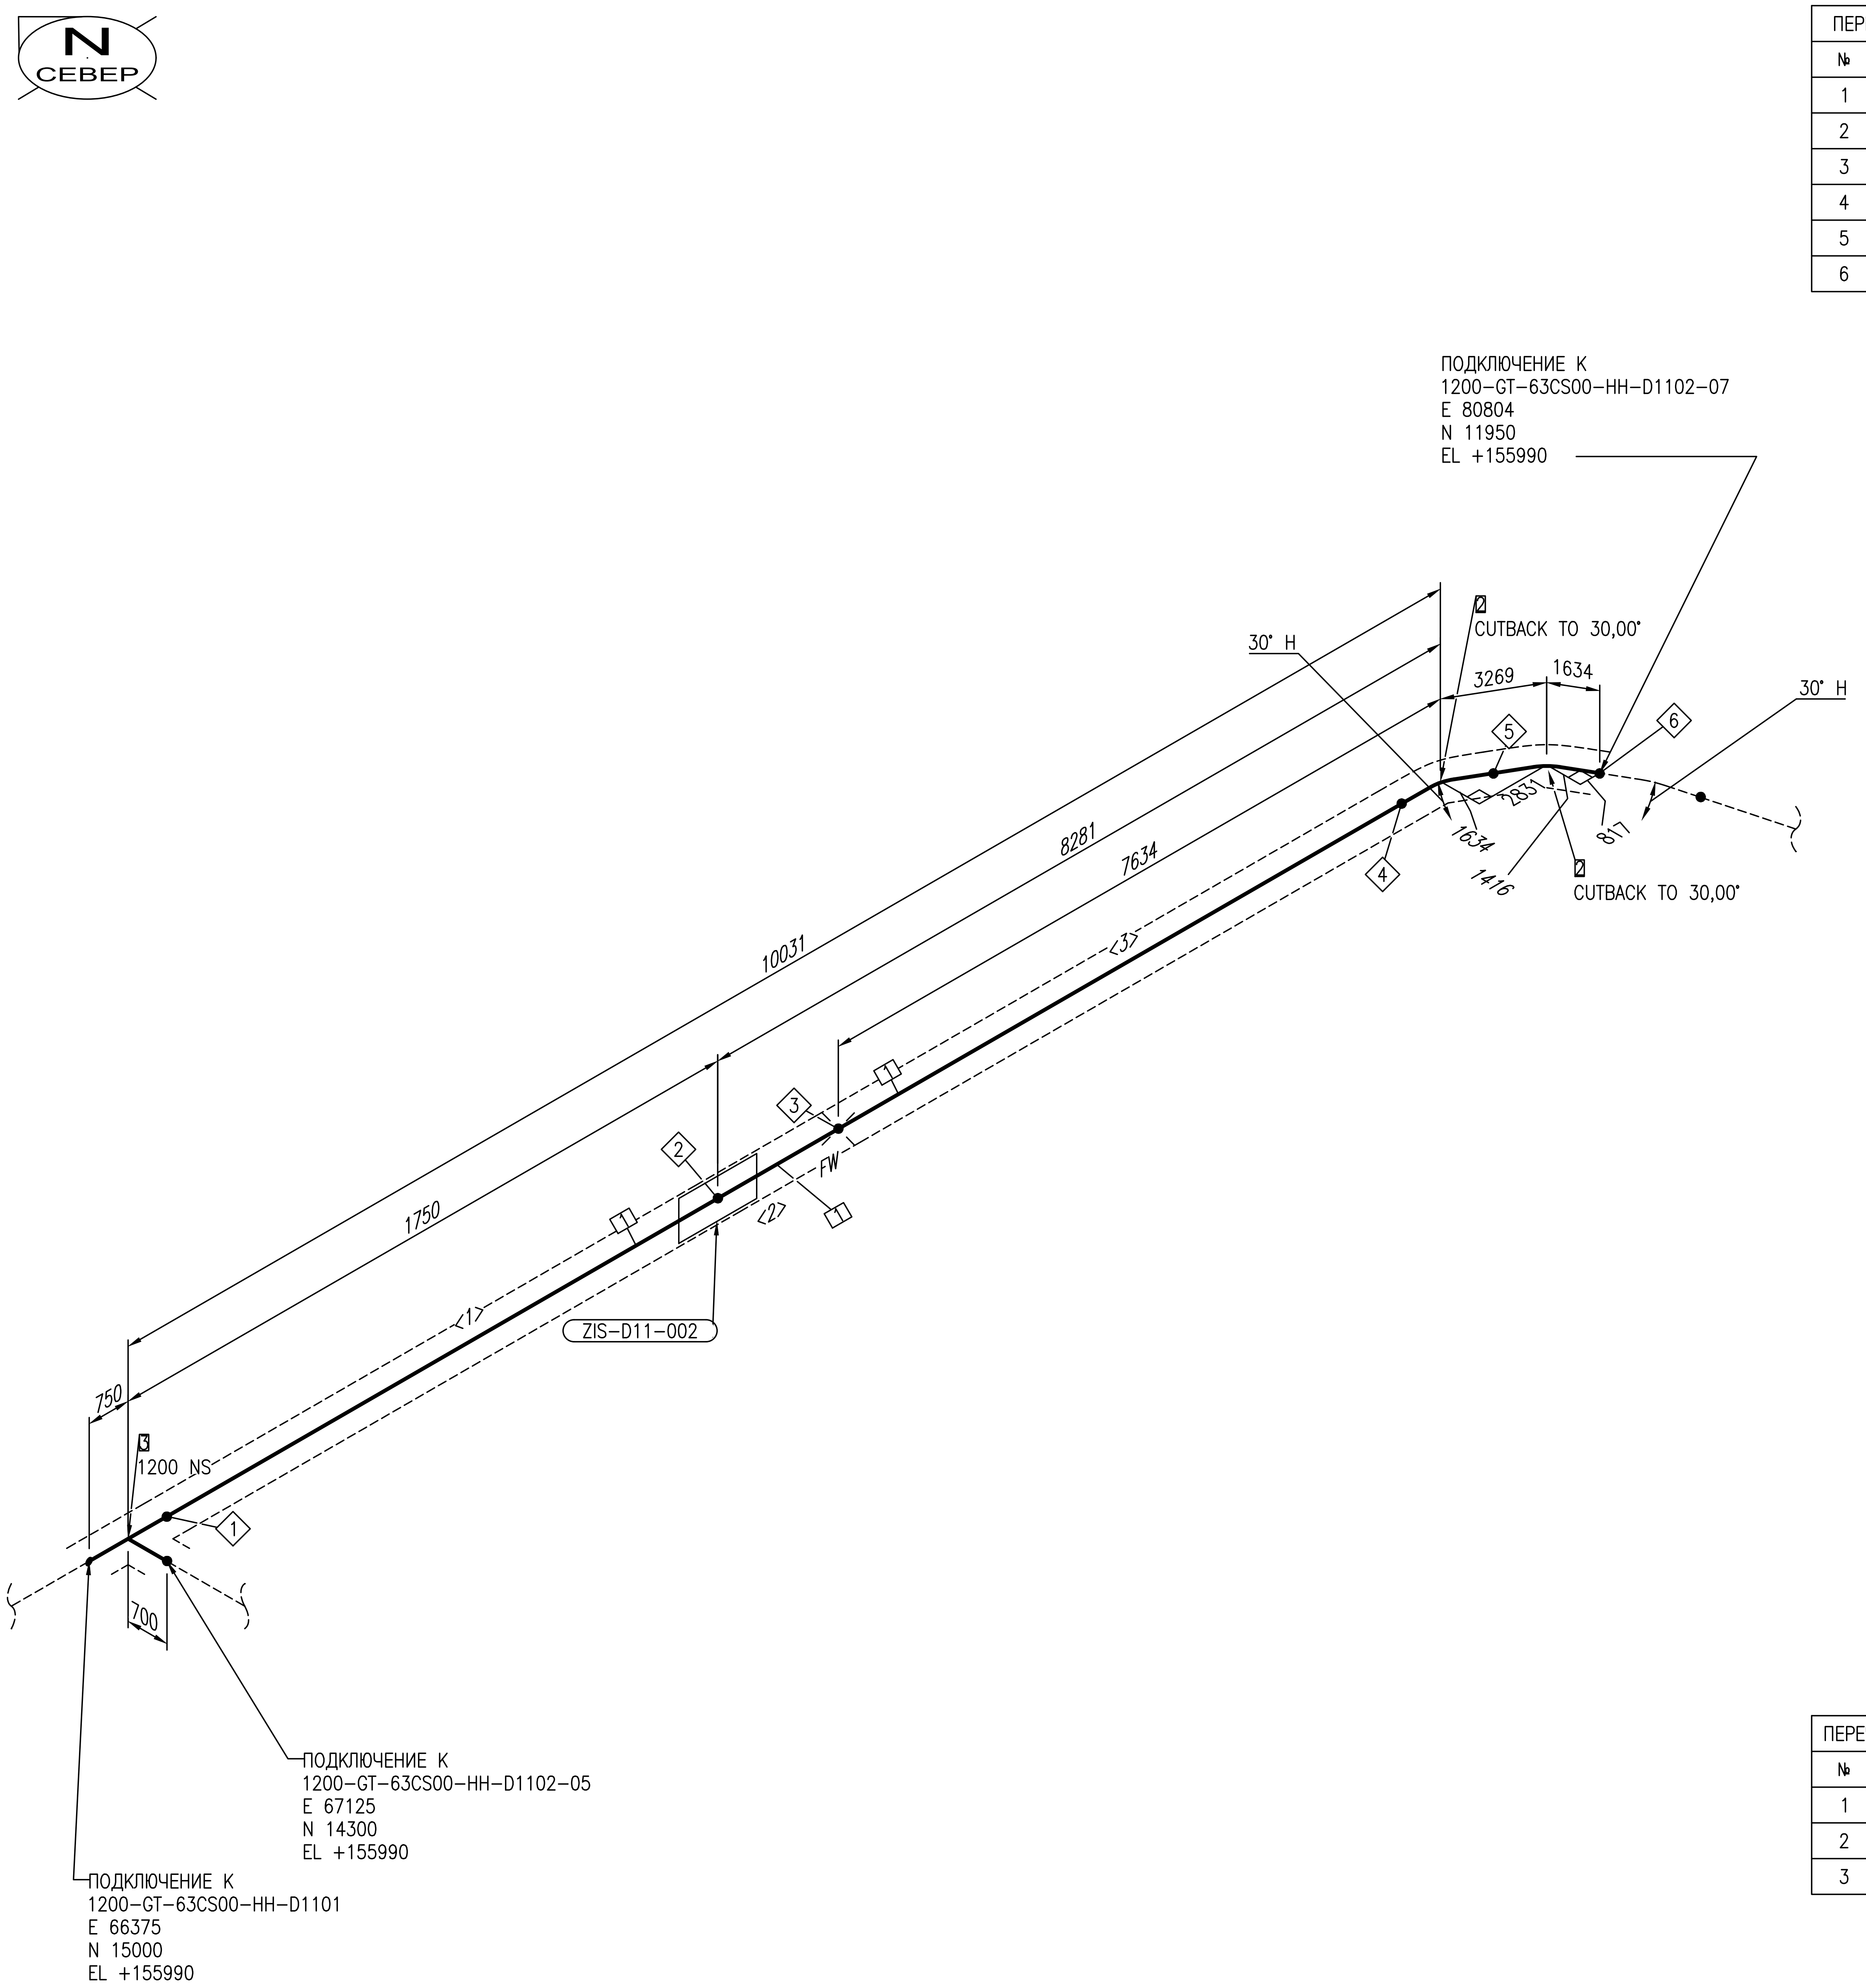

| ПЕРЕЧЕНЬ ТРУБНЫХ КАТУШЕК | | |
|---|---|---|
| № | DN | ДЛИНА |
| 1 | 1200 | 1000ММ |
| 2 | 1200 | 647ММ |
| 3 | 1200 | 6000ММ |

## СПЕЦИФИКАЦИЯ ИЗДЕЛИЙ И МАТЕРИАЛОВ

| ПОЗ. | НАИМЕНОВАНИЕ | СТАНДАРТ | КОЛ. | ПРИМЕЧАНИЕ |
|---|---|---|---|---|
| 1 | Трубы стальные сварные прямошовные, типа 3, К60, 1220Х12 | ГОСТ 31447-2012 | 7.7М | |
| 2 | ОСС 30°-5Д-1220 (12К60)-5,5-075-У ТУ51-29-81 | ТУ 51-29-81 | 2 | |
| 3 | Тройник ТР I 1220(13К60)-5,5(6,9)-0,75-30, сталь К60 | ТУ 1469-017-38948552-2015 | 1 | |

| Трубопровод | ДАННЫЕ ПО ТРУБОПРОВОДУ | | |
|---|---|---|---|
| 1200-GT-63CS00-HH-D1102 | Расчетные параметры | Температура | -26,9...+85 °C |
| | | Давление | 6,3 MPa |
| | Рабочие параметры | Температура | -20...+40 °C |
| | | Давление | 5,5 MPa |
| Ссылочные чертежи No | Параметры испытания | Тип | Гидравлическое |
| EWE0426-MGL1-PRE-054-SCM-610102 | | Давление | 6,9 MPa |
| | Изоляция | Тип | HH |
| | | Толщина | mm |
| | Катодная защита | Да или Нет | Да |

| Рев. | Дата | Назначение ревизии | Проверил | Утвердил |
|---|---|---|---|---|
| A1 | 25.09.2026 | Утверждено для строительства | | |
| R1 | 27.08.2026 | Выпущено для рассмотрения | | |

ЗАКАЗЧИК: UTG UZTRANSGAZ

ГЕНЕРАЛЬНЫЙ ПОДРЯДЧИК: UET UZBEKENERGOTAMIR

ПОДРЯДЧИК: PBG Pro Build Generation

ГЕНЕРАЛЬНЫЙ ПРОЕКТИРОВЩИК: EAST WEST ENGINEERING

# EWE0426-MGL1-PRE-054-ISO-690604-A1

«СТРОИТЕЛЬСТВО НОВЫХ НИТОК (УЧАСТКОВ) ГАЗОПРОВОДОВ «ГАЗЛИ - САРИМОЙ» И «АКЧАЛОК - ГАЗЛИ - НУКУС» ОБЩЕЙ ПРОТЯЖЕННОСТЬЮ НЕ МЕНЕЕ 275 КМ».

| Изм. | Кол.уч. | Лист | №док. | Подпись | Дата |
|---|---|---|---|---|---|
| ГИП | | Кирпичников С. | | | 09.2026 |
| Нач.отд. | | Рябинин А. | | | 09.2026 |
| Исполн. | | Ташимуров Р. | | | 09.2026 |
| Н.контр | | Кирпичников С. | | | 09.2026 |

ГАЗОПРОВОД «ГАЗЛИ-САРИМОЙ» (54 КМ)
Узел приема/запуска очистных устройств DN1200.УЗПОУ-D11.

| Стадия | Лист | Листов |
|---|---|---|
| РД | 6 | 8 |

Изометрический чертеж трубопровода
1200-GT-63CS00-HH-D1102

EAST WEST ENGINEERING
ООО "EAST-WEST Engineering"
г. Ташкент 2026г.

Формат А2 594х420

Взам. инв. №
Подпись и дата
Инв.№ подл.

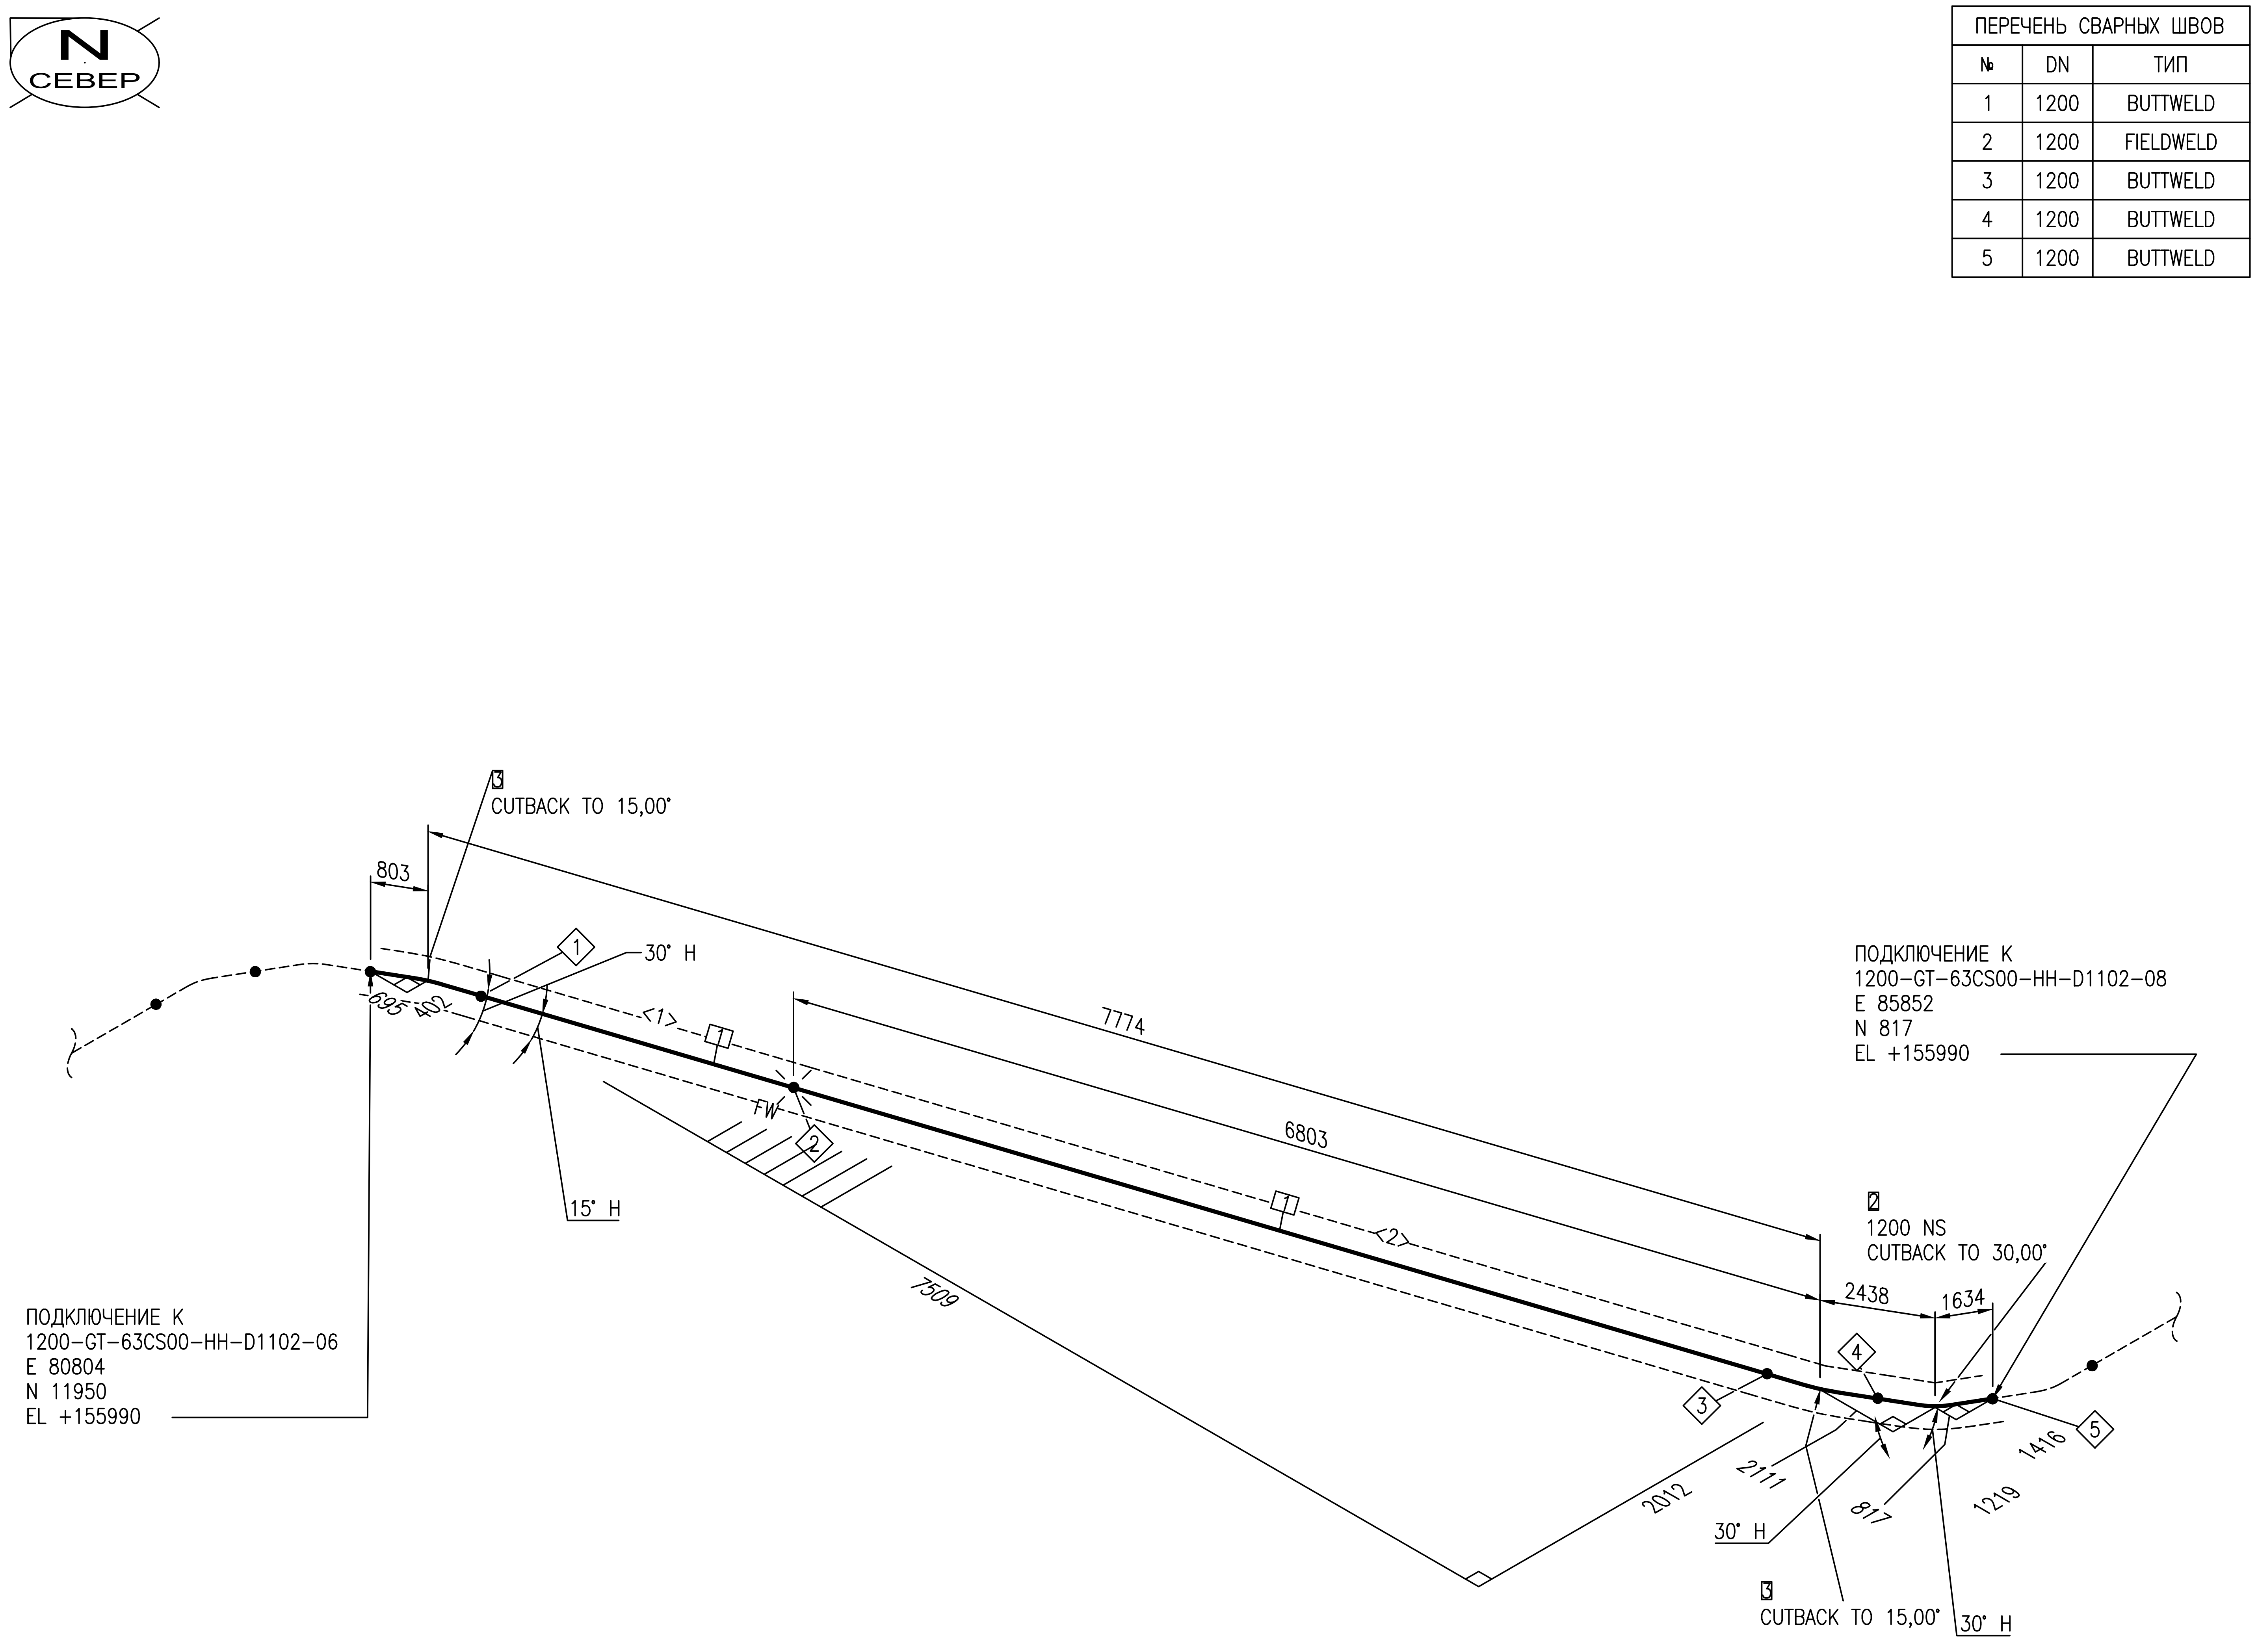

| ПЕРЕЧЕНЬ СВАРНЫХ ШВОВ | | |
|---|---|---|
| № | DN | ТИП |
| 1 | 1200 | BUTTWELD |
| 2 | 1200 | FIELDWELD |
| 3 | 1200 | BUTTWELD |
| 4 | 1200 | BUTTWELD |
| 5 | 1200 | BUTTWELD |

СПЕЦИФИКАЦИЯ ИЗДЕЛИЙ И МАТЕРИАЛОВ

| ПОЗ. | НАИМЕНОВАНИЕ | СТАНДАРТ | КОЛ. | ПРИМЕЧАНИЕ |
|---|---|---|---|---|
| 1 | Трубы стальные сварные прямошовные, типа 3, К60, 1220Х12 | ГОСТ 31447–2012 | 6.2М | |
| 2 | ОСС 30°–5Д–1220 (12К60)–5,5–075–У ТУ51–29–81 | ТУ 51–29–81 | 1 | |
| 3 | ОСС 15°–5Д–1220 (12К60)–5,5–075–У ТУ51–29–81 | ТУ 51–29–81 | 2 | |

| ПЕРЕЧЕНЬ ТРУБНЫХ КАТУШЕК | | |
|---|---|---|
| № | DN | ДЛИНА |
| 1 | 1200 | 168ММ |
| 2 | 1200 | 6000ММ |

| Трубопровод | ДАННЫЕ ПО ТРУБОПРОВОДУ | | |
|---|---|---|---|
| 1200–GT–63CS00–HH–D1102 | Расчетные параметры | Температура | -26,9...+85 °С |
| | | Давление | 6,3 MPa |
| | Рабочие параметры | Температура | -20...+40 °С |
| | | Давление | 5,5 MPa |
| | Параметры испытания | Тип | Гидравлическое |
| Ссылочные чертежи No | | Давление | 6,9 MPa |
| EWE0426-MGL1-PRE-054-SCM-610102 | Изоляция | Тип | HH |
| | | Толщина | mm |
| | Катодная защита | Да или Нет | Да |

| Рев. | Дата | Назначение ревизии | Проверил | Утвердил |
|---|---|---|---|---|
| A1 | 25.09.2026 | Утверждено для строительства | | |
| R1 | 27.08.2026 | Выпущено для рассмотрения | | |

ЗАКАЗЧИК: UTG UZTRANSGAZ

ГЕНЕРАЛЬНЫЙ ПОДРЯДЧИК: UET UZBEKENERGOTAMIR

ПОДРЯДЧИК: PBG Pre Build Generation

ГЕНЕРАЛЬНЫЙ ПРОЕКТИРОВЩИК: EAST WEST ENGINEERING

# EWE0426–MGL1–PRE–054–ISO–690604–A1

«СТРОИТЕЛЬСТВО НОВЫХ НИТОК (УЧАСТКОВ) ГАЗОПРОВОДОВ «ГАЗЛИ – САРИМОЙ» И «АКЧАЛОК – ГАЗЛИ – НУКУС» ОБЩЕЙ ПРОТЯЖЕННОСТЬЮ НЕ МЕНЕЕ 275 КМ».

| Изм. | Кол.уч. | Лист | №док. | Подпись | Дата |
|---|---|---|---|---|---|
| ГИП | | Кирпичников С. | | | 09.2026 |
| Нач.отд. | | Рябинин А. | | | 09.2026 |
| Исполн. | | Таштимуров Р. | | | 09.2026 |
| Н.контр | | Кирпичников С. | | | 09.2026 |

ГАЗОПРОВОД «ГАЗЛИ-САРИМОЙ» (54 КМ)
Узел приема/запуска очистных устройств DN1200.УЗПОУ-D11.

| Стадия | Лист | Листов |
|---|---|---|
| РД | 7 | 8 |

Изометрический чертеж трубопровода
1200–GT–63CS00–HH–D1102

EAST WEST ENGINEERING
ООО "EAST-WEST Engineering"
г. Ташкент 2026г.

Взам. инв. №
Подпись и дата
Инв.№ подл.

Формат А2 594х420

| ПЕРЕЧЕНЬ СВАРНЫХ ШВОВ | | |
|---|---|---|
| № | DN | ТИП |
| 1 | 1200 | BUTTWELD |

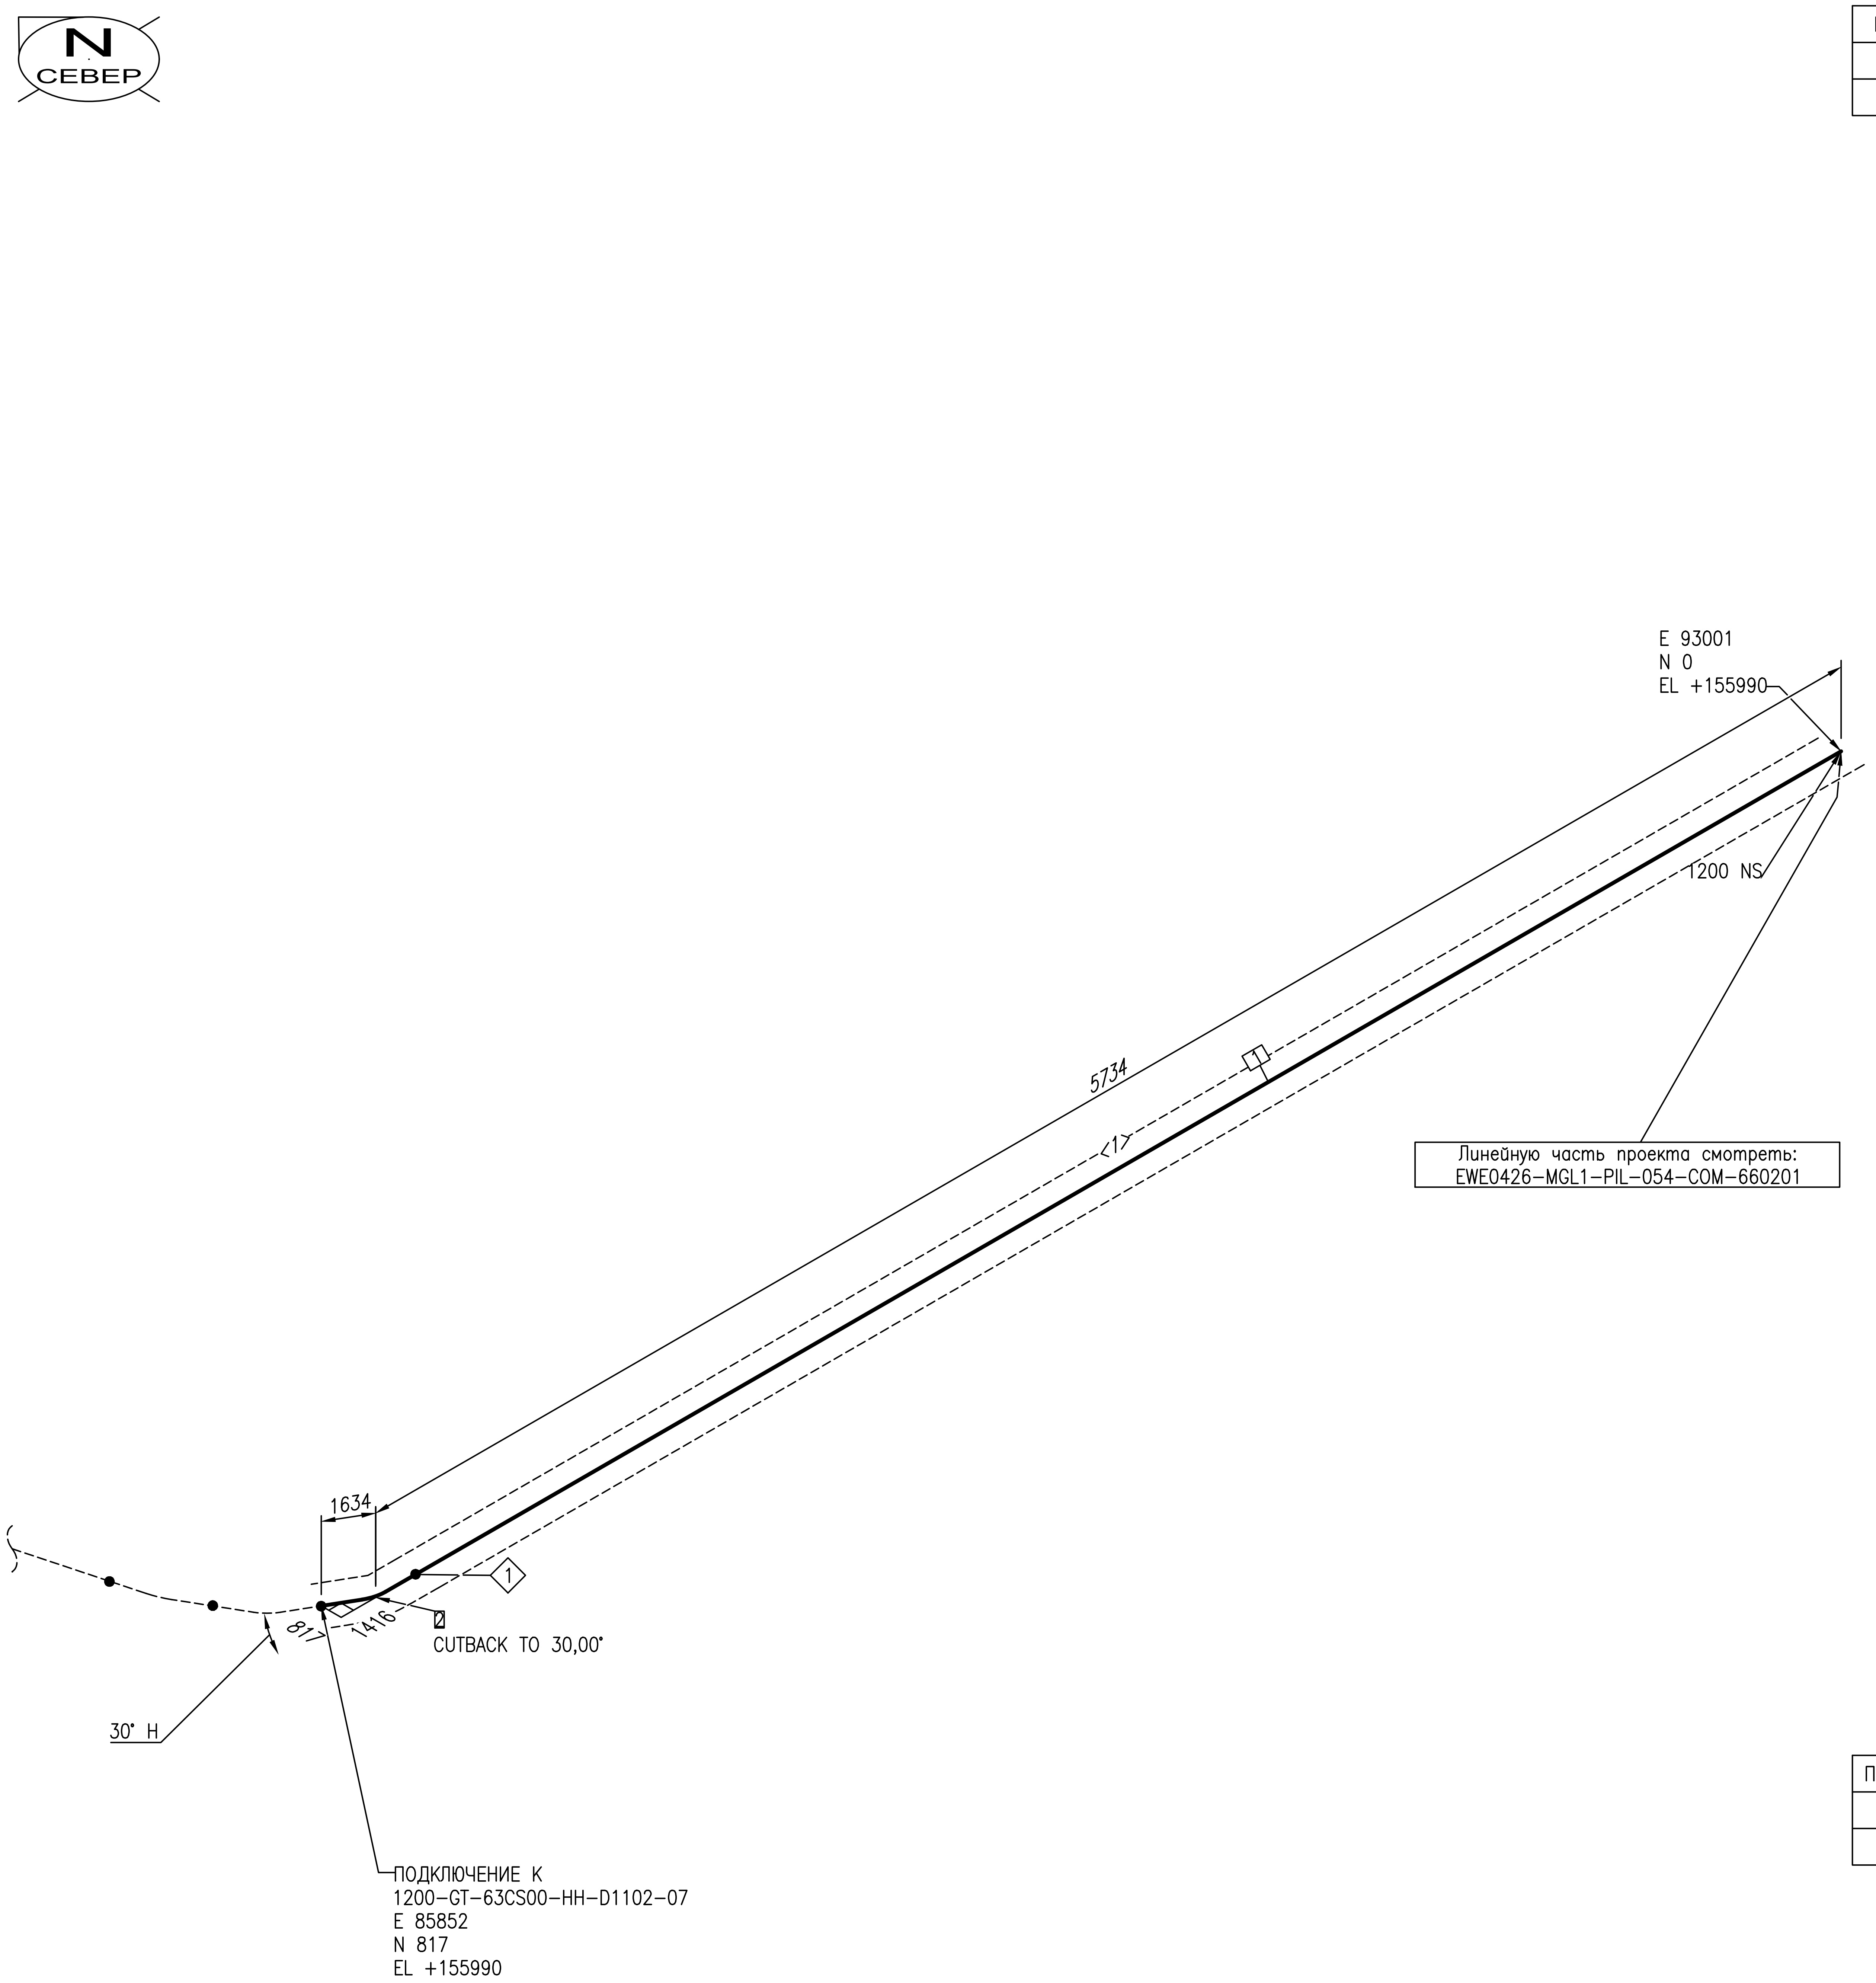

| ПЕРЕЧЕНЬ ТРУБНЫХ КАТУШЕК | | |
|---|---|---|
| № | DN | ДЛИНА |
| 1 | 1200 | 4100MM |

## СПЕЦИФИКАЦИЯ ИЗДЕЛИЙ И МАТЕРИАЛОВ

| ПОЗ. | НАИМЕНОВАНИЕ | СТАНДАРТ | КОЛ. | ПРИМЕЧАНИЕ |
|---|---|---|---|---|
| 1 | Трубы стальные сварные прямошовные, типа 3, К60, 1220Х12 | ГОСТ 31447-2012 | 4.1M | |
| 2 | ОСС 30°-5Д-1220 (12К60)-5,5-075-У ТУ51-29-81 | ТУ 51-29-81 | 1 | |

| Трубопровод | ДАННЫЕ ПО ТРУБОПРОВОДУ | | |
|---|---|---|---|
| 1200-GT-63CS00-HH-D1102 | Расчетные параметры | Температура | -26,9...+85 °C |
| | | Давление | 6,3 MPa |
| | Рабочие параметры | Температура | -20...+40 °C |
| | | Давление | 5,5 MPa |
| | Параметры испытания | Тип | Гидравлическое |
| Ссылочные чертежи No | | Давление | 6,9 MPa |
| EWE0426-MGL1-PRE-054-SCM-610102 | Изоляция | Тип | HH |
| | | Толщина | mm |
| | Катодная защита | Да или Нет | Да |

| Рев. | Дата | Назначение ревизии | Проверил | Утвердил |
|---|---|---|---|---|
| A1 | 25.09.2026 | Утверждено для строительства | | |
| R1 | 27.08.2026 | Выпущено для рассмотрения | | |

ЗАКАЗЧИК: UTG UZTRANSGAZ
ГЕНЕРАЛЬНЫЙ ПОДРЯДЧИК: UET UZBEKENERGOTAMIR
ПОДРЯДЧИК: PBG Pro Build Generation
ГЕНЕРАЛЬНЫЙ ПРОЕКТИРОВЩИК: EAST WEST ENGINEERING

# EWE0426-MGL1-PRE-054-ISO-690604-A1

«СТРОИТЕЛЬСТВО НОВЫХ НИТОК (УЧАСТКОВ) ГАЗОПРОВОДОВ «ГАЗЛИ - САРИМОЙ» И «АКЧАЛОК - ГАЗЛИ - НУКУС» ОБЩЕЙ ПРОТЯЖЕННОСТЬЮ НЕ МЕНЕЕ 275 КМ».

| Изм. | Кол.уч. | Лист | №док. | Подпись | Дата |
|---|---|---|---|---|---|
| ГИП | | Кирпичников С. | | | 09.2026 |
| Нач.отд. | | Рябинин А. | | | 09.2026 |
| Исполн. | | Таштимуров Р. | | | 09.2026 |
| Н.контр | | Кирпичников С. | | | 09.2026 |

ГАЗОПРОВОД «ГАЗЛИ-САРИМОЙ» (54 КМ)
Узел приема/запуска очистных устройств DN1200.УЗПОУ-D11.

| Стадия | Лист | Листов |
|---|---|---|
| РД | 8 | 8 |

Изометрический чертеж трубопровода
1200-GT-63CS00-HH-D1102

EAST WEST ENGINEERING
ООО "EAST-WEST Engineering"
г. Ташкент 2026г.

Взам. инв. №
Подпись и дата
Инв.№ подл.

Формат А2 594x420