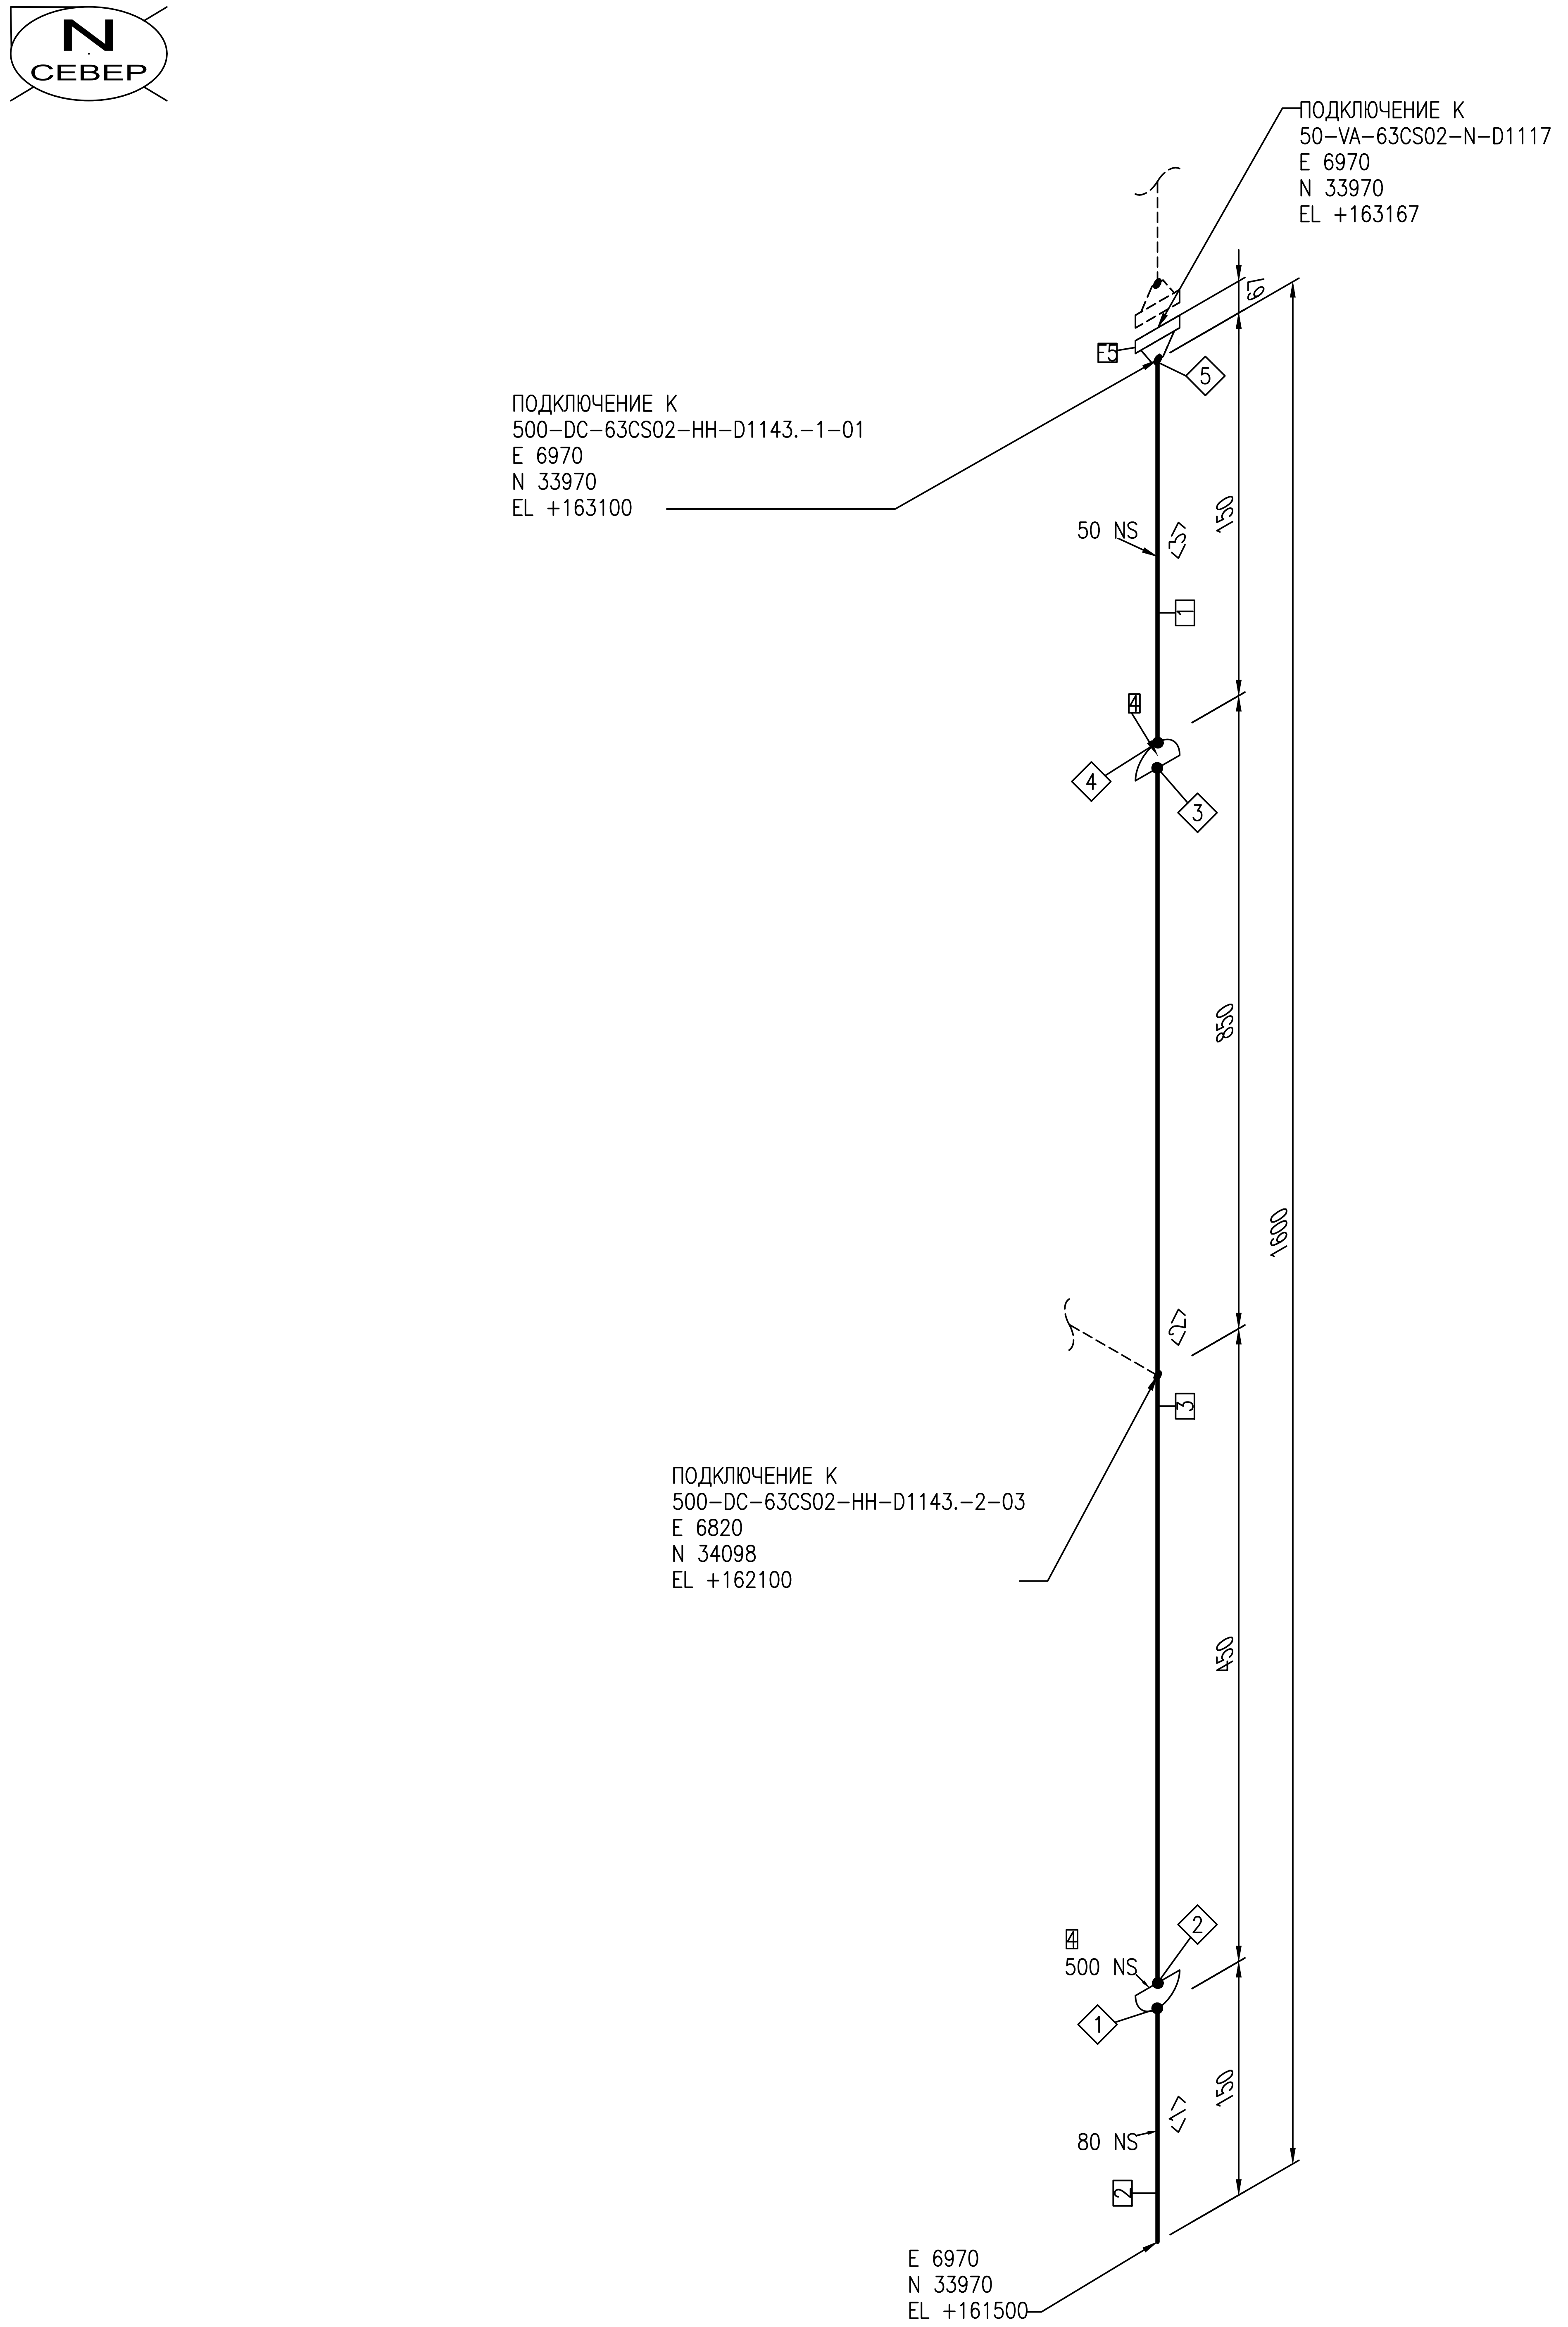

ПЕРЕЧЕНЬ СВАРНЫХ ШВОВ

№	DN	ТИП
1	500	TAPWELD
2	500	BUTTWELD
3	500	BUTTWELD
4	500	TAPWELD
5	500	BUTTWELD

ПЕРЕЧЕНЬ ТРУБНЫХ КАТУШЕК

№	DN	ДЛИНА
1	80	150MM
2	500	1000MM
3	50	150MM

СПЕЦИФИКАЦИЯ ИЗДЕЛИЙ И МАТЕРИАЛОВ

ПОЗ.	НАИМЕНОВАНИЕ	СТАНДАРТ	КОЛ.	ПРИМЕЧАНИЕ
1	Трубы стальные бесшовные горячедеформированные Ст20, 57Х10	ГОСТ 8732-78/ ГОСТ 8731-74	0.2M	РАЗДЕЛИТЕЛЬ, СМ. ДОКУМЕНТ EWE0426-MGL1-PRE-054-DRW-690203, ЛИСТ 3
2	Трубы стальные бесшовные горячедеформированные Ст20, 89Х10	ГОСТ 8732-78/ ГОСТ 8731-74	0.2M	РАЗДЕЛИТЕЛЬ, СМ. ДОКУМЕНТ EWE0426-MGL1-PRE-054-DRW-690203, ЛИСТ 3, РАЗРЕЗ 14-14
3	Трубы стальные сварные прямошовные, типа 3, К60, 530Х10	ГОСТ 31447-2012	1.0M	РАЗДЕЛИТЕЛЬ, СМ. ДОКУМЕНТ EWE0426-MGL1-PRE-054-DRW-690203, ЛИСТ 3
4	Днище Д I 530(8К60)-5,5(6,9)-075-30, сталь К60	ТУ 1469-017-38948552-2015	2	РАЗДЕЛИТЕЛЬ, СМ. ДОКУМЕНТ EWE0426-MGL1-PRE-054-DRW-690203, ЛИСТ 3
5	Фланец стальной приварной встык, тип 11, исполнение J, ряд 1, 6.3 МПа, Ст20, 57Х10	ГОСТ 33259-2015	1	РАЗДЕЛИТЕЛЬ, СМ. ДОКУМЕНТ EWE0426-MGL1-PRE-054-DRW-690203, ЛИСТ 3

ПРИМЕЧАНИЕ:

1. Внутреннюю часть Разделителя см. документ EWE0426-MGL1-PRE-054-ISO-690606, Лист 3, сборку Разделителя см. документ EWE0426-MGL1-PRE-054-DRW-690203, Лист 3, Разрез 14-14

Трубопровод	ДАННЫЕ ПО ТРУБОПРОВОДУ		
500-DC-63CS02-HH-D1143	Расчетные параметры	Температура	-26,9...+85 °C
		Давление	6,3 MPa
	Рабочие параметры	Температура	-20...+40 °C
		Давление	5,5 MPa
	Параметры испытания	Тип	Гидравлическое
Ссылочные чертежи No		Давление	6,9 MPa
EWE0426-MGL1-PRE-054-SCM-610102	Изоляция	Тип	N
		Толщина	mm
	Катодная защита	Да или Нет	Да

Рев.	Дата	Назначение ревизии	Проверил	Утвердил
A1	25.09.2026	Утверждено для строительства		
R1	27.08.2026	Выпущено для рассмотрения		

ЗАКАЗЧИК: UTG UZTRANSGAZ

ГЕНЕРАЛЬНЫЙ ПОДРЯДЧИК: UET UZBEKENERGOTAMIR

ПОДРЯДЧИК: PBG Pre Build Generation

ГЕНЕРАЛЬНЫЙ ПРОЕКТИРОВЩИК: EAST WEST ENGINEERING

EWE0426-MGL1-PRE-054-ISO-690606-A1

«СТРОИТЕЛЬСТВО НОВЫХ НИТОК (УЧАСТКОВ) ГАЗОПРОВОДОВ «ГАЗЛИ - САРИМОЙ» И «АКЧАЛОК - ГАЗЛИ - НУКУС» ОБЩЕЙ ПРОТЯЖЕННОСТЬЮ НЕ МЕНЕЕ 275 КМ».

Изм.	Кол.уч.	Лист	№док.	Подпись	Дата
ГИП		Кирпичников С.			09.2026
Нач.отд.		Рябинин А.			09.2026
Исполн.		Таштимуров Р.			09.2026
Н.контр		Кирпичников С.			09.2026

ГАЗОПРОВОД «ГАЗЛИ-САРИМОЙ» (54 КМ)
Узел приема/запуска очистных устройств DN1200.УЗПОУ-D11.

Стадия	Лист	Листов
РД	1	3

Изометрический чертеж трубопровода
500-DC-63CS02-HH-D1143

EAST WEST ENGINEERING
ООО "EAST-WEST Engineering"
г. Ташкент 2026г.

Взам. инв. №
Подпись и дата
Инв.№ подл.

Формат А2 594х420

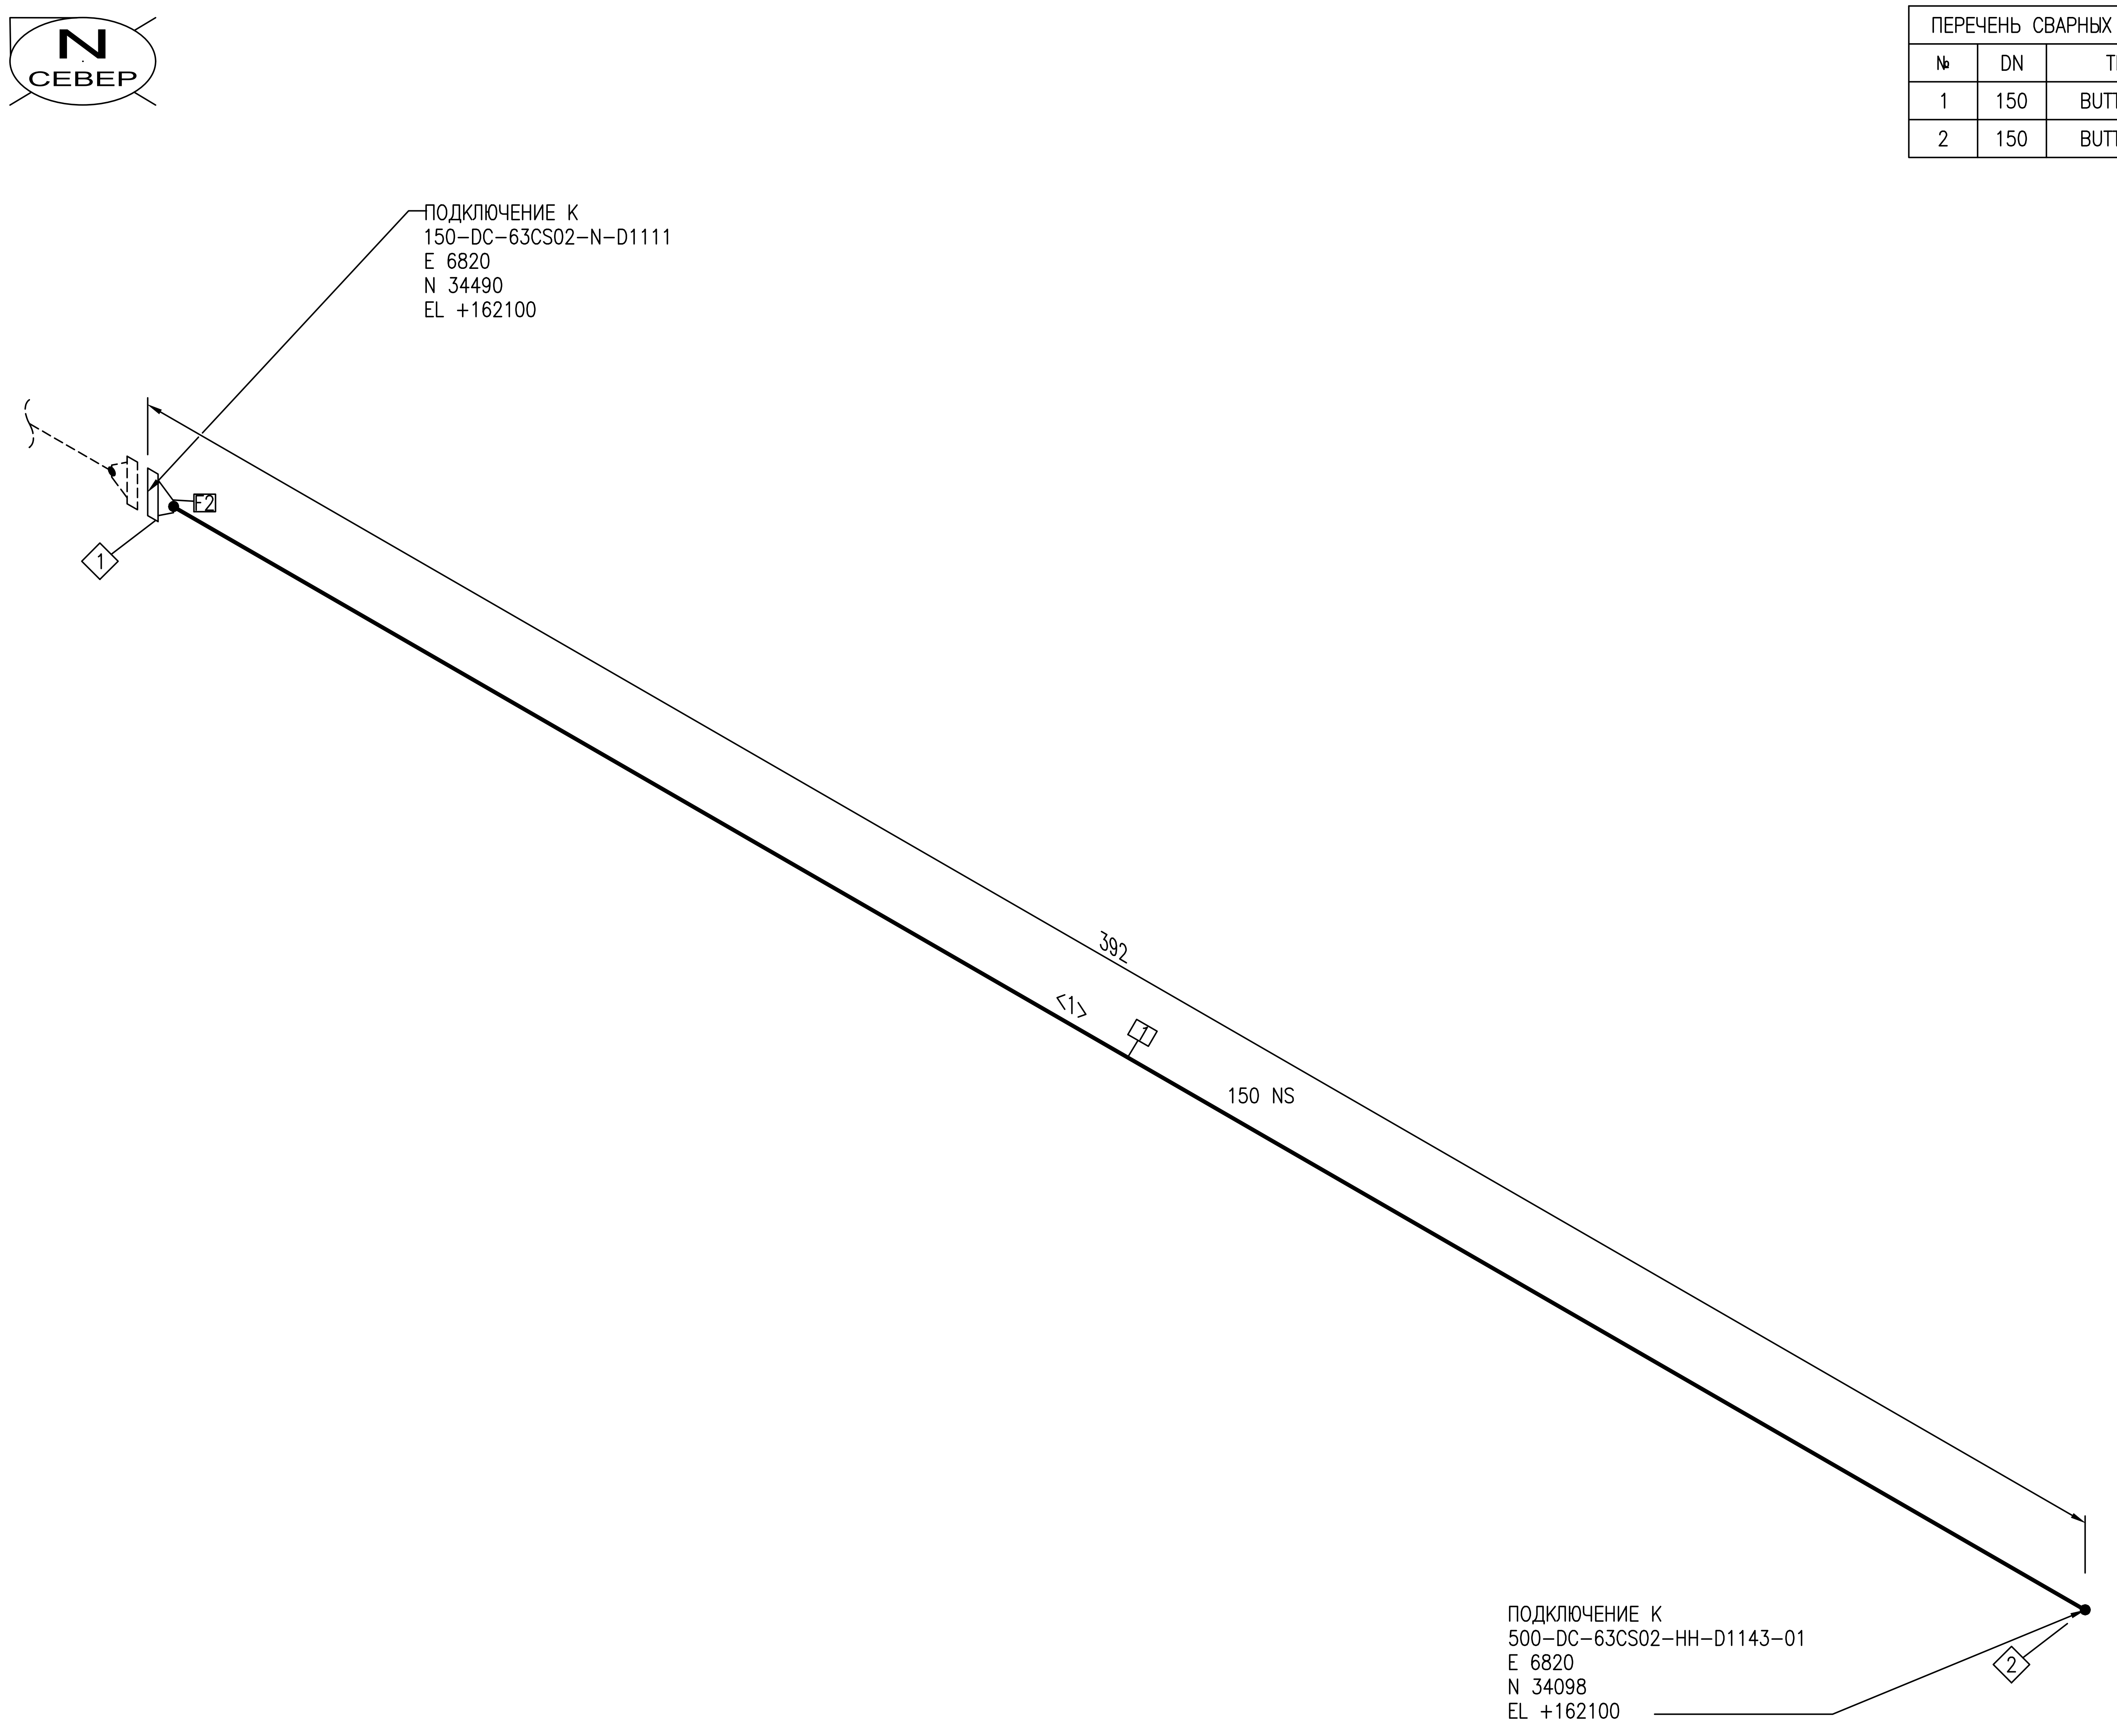

ПОДКЛЮЧЕНИЕ К
150-DC-63CS02-N-D1111
E 6820
N 34490
EL +162100

ПОДКЛЮЧЕНИЕ К
500-DC-63CS02-HH-D1143-01
E 6820
N 34098
EL +162100

ПЕРЕЧЕНЬ СВАРНЫХ ШВОВ

№	DN	ТИП
1	150	BUTTWELD
2	150	BUTTWELD

ПЕРЕЧЕНЬ ТРУБНЫХ КАТУШЕК

№	DN	ДЛИНА
1	150	287ММ

СПЕЦИФИКАЦИЯ ИЗДЕЛИЙ И МАТЕРИАЛОВ

ПОЗ.	НАИМЕНОВАНИЕ	СТАНДАРТ	КОЛ.	ПРИМЕЧАНИЕ
1	Трубы стальные бесшовные горячедеформированные 09Г2С, 159Х10	ТУ 14-3-1128-2000	0.3М	РАЗДЕЛИТЕЛЬ, СМ. ДОКУМЕНТ EWE0426-MGL1-PRE-054-DRW-690203, ЛИСТ 3
2	Фланец стальной приварной встык, тип 11, исполнение J, ряд 1, 6.3 МПа, сталь 09Г2С, 159Х10	ГОСТ 33259-2015	1	РАЗДЕЛИТЕЛЬ, СМ. ДОКУМЕНТ EWE0426-MGL1-PRE-054-DRW-690203, ЛИСТ 3

Трубопровод	ДАННЫЕ ПО ТРУБОПРОВОДУ		
500-DC-63CS02-HH-D1143	Расчетные параметры	Температура	-26,9…+85 °С
		Давление	6,3 MPa
	Рабочие параметры	Температура	-20…+40 °С
		Давление	5,5 MPa
	Параметры испытания	Тип	Гидравлическое
Ссылочные чертежи No		Давление	6,9 MPa
EWE0426-MGL1-PRE-054-SCM-610102	Изоляция	Тип	N
		Толщина	mm
	Катодная защита	Да или Нет	Да

Рев.	Дата	Назначение ревизии	Проверил	Утвердил
A1	25.09.2026	Утверждено для строительства		
R1	27.08.2026	Выпущено для рассмотрения		

ЗАКАЗЧИК: UTG UZTRANSGAZ
ГЕНЕРАЛЬНЫЙ ПОДРЯДЧИК: UET UZBEKENERGOTAMIR
ПОДРЯДЧИК: PBG Pro Build Generation
ГЕНЕРАЛЬНЫЙ ПРОЕКТИРОВЩИК: EAST WEST ENGINEERING

EWE0426-MGL1-PRE-054-ISO-690606-A1

«СТРОИТЕЛЬСТВО НОВЫХ НИТОК (УЧАСТКОВ) ГАЗОПРОВОДОВ «ГАЗЛИ – САРИМОЙ» И «АКЧАЛОК – ГАЗЛИ – НУКУС» ОБЩЕЙ ПРОТЯЖЕННОСТЬЮ НЕ МЕНЕЕ 275 КМ».

Изм.	Кол.уч.	Лист	№док.	Подпись	Дата
ГИП		Кирпичников С.			09.2026
Нач.отд.		Рябинин А.			09.2026
Исполн.		Таштимуров Р.			09.2026
Н.контр		Кирпичников С.			09.2026

ГАЗОПРОВОД «ГАЗЛИ-САРИМОЙ» (54 КМ)
Узел приема/запуска очистных устройств DN1200.УЗПОУ-D11.

Стадия	Лист	Листов
РД	2	3

Изометрический чертеж трубопровода
500-DC-63CS02-HH-D1143

ООО "EAST-WEST Engineering"
г. Ташкент 2026г.

Формат А2 594x420

Взам. инв. №
Подпись и дата
Инв.№ подл.

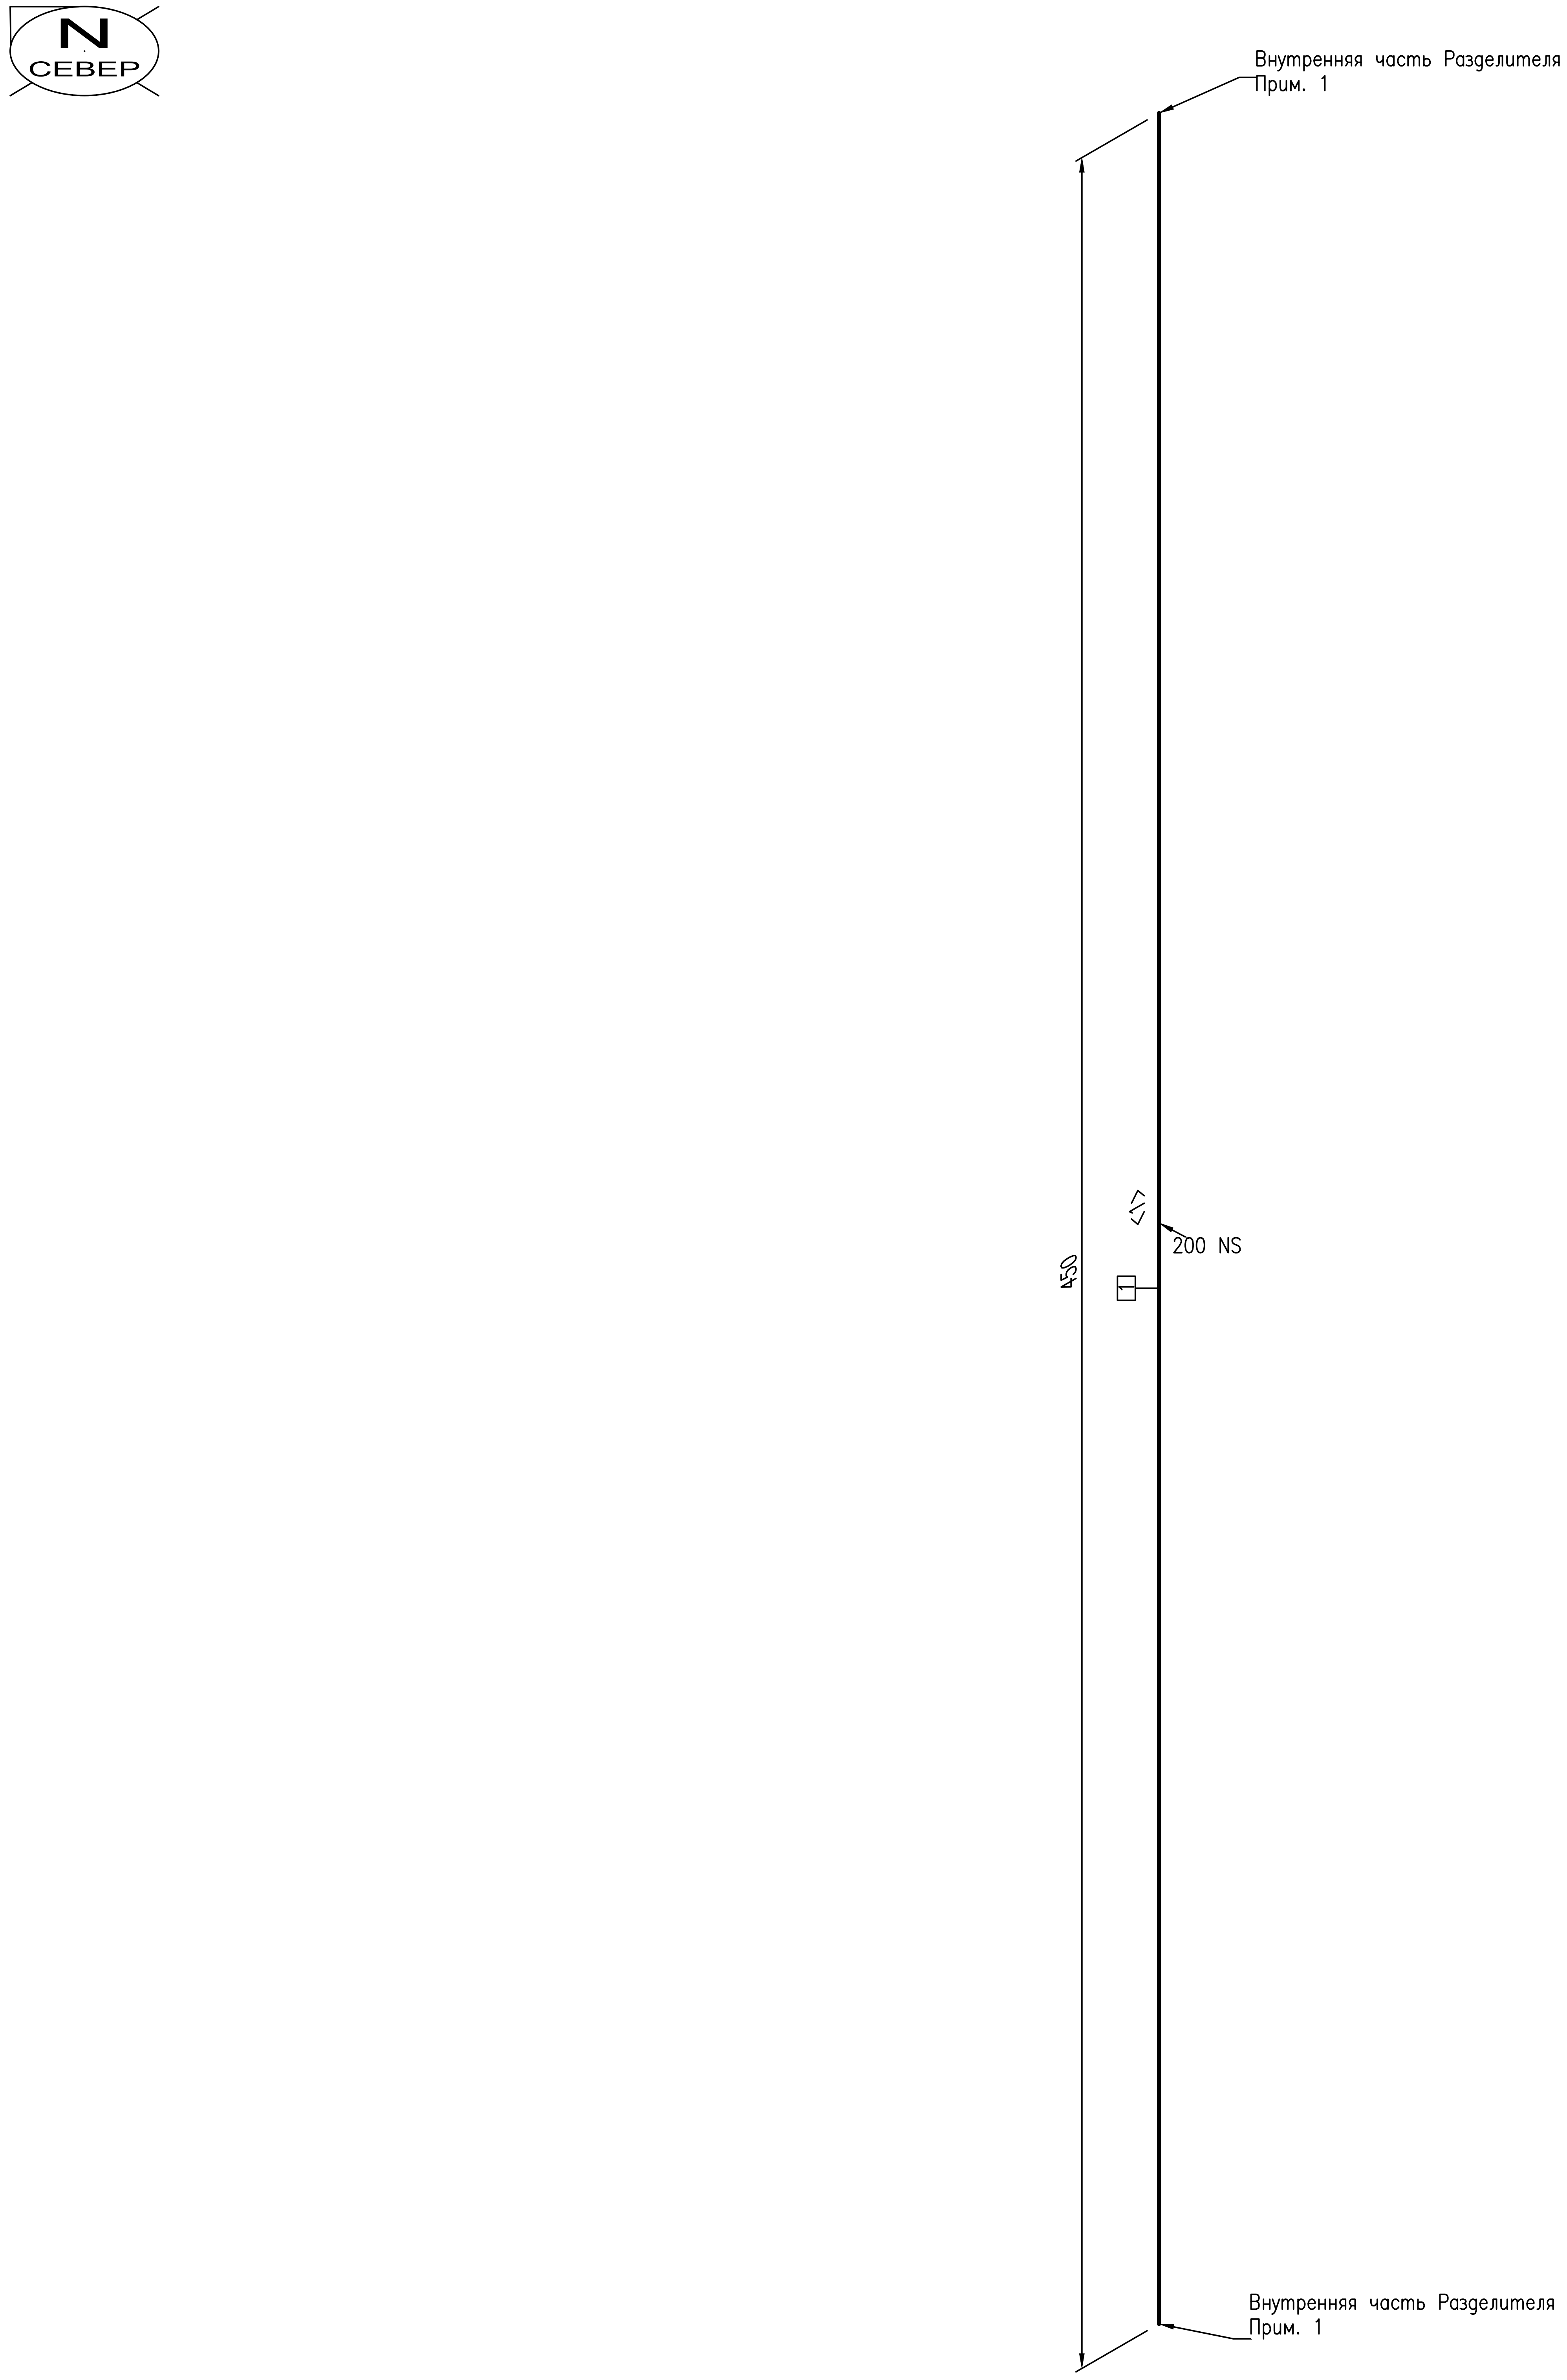

СПЕЦИФИКАЦИЯ ИЗДЕЛИЙ И МАТЕРИАЛОВ

ПОЗ.	НАИМЕНОВАНИЕ	СТАНДАРТ	КОЛ.	ПРИМЕЧАНИЕ
1	Трубы стальные бесшовные горячедеформированные 09Г2С, 219x8	ТУ 14-3-1128-2000	0.5M	РАЗДЕЛИТЕЛЬ, СМ. ДОКУМЕНТ EWE0426-MGL1-PRE-054-DRW-690203, ЛИСТ 3, РАЗРЕЗ 14-14

ПЕРЕЧЕНЬ ТРУБНЫХ КАТУШЕК

№	DN	ДЛИНА
1	200	450MM

Трубопровод	ДАННЫЕ ПО ТРУБОПРОВОДУ		
500-DC-63CS02-HH-D1143	Расчетные параметры	Температура	-26,9...+85 °C
		Давление	6,3 MPa
	Рабочие параметры	Температура	-20...+40 °C
		Давление	5,5 MPa
Ссылочные чертежи No	Параметры испытания	Тип	Гидравлическое
EWE0426-MGL1-PRE-054-SCM-610102		Давление	6,9 MPa
	Изоляция	Тип	N
		Толщина	mm
	Катодная защита	Да или Нет	Да

Рев.	Дата	Назначение ревизии	Проверил	Утвердил
A1	25.09.2026	Утверждено для строительства		
R1	27.08.2026	Выпущено для рассмотрения		

ЗАКАЗЧИК: UTG UZTRANSGAZ

ГЕНЕРАЛЬНЫЙ ПОДРЯДЧИК: UET UZBEKENERGOTAMIR

ПОДРЯДЧИК: PBG Pro Build Generation

ГЕНЕРАЛЬНЫЙ ПРОЕКТИРОВЩИК: EAST WEST ENGINEERING

EWE0426-MGL1-PRE-054-ISO-690606-A1

«СТРОИТЕЛЬСТВО НОВЫХ НИТОК (УЧАСТКОВ) ГАЗОПРОВОДОВ «ГАЗЛИ - САРИМОЙ» И «АКЧАЛОК - ГАЗЛИ - НУКУС» ОБЩЕЙ ПРОТЯЖЕННОСТЬЮ НЕ МЕНЕЕ 275 КМ».

Изм.	Кол.уч.	Лист	№док.	Подпись	Дата
ГИП		Кирпичников С.			09.2026
Нач.отд.		Рябинин А.			09.2026
Исполн.		Таштимуров Р.			09.2026
Н.контр		Кирпичников С.			09.2026

ГАЗОПРОВОД «ГАЗЛИ-САРИМОЙ» (54 КМ)
Узел приема/запуска очистных устройств
DN1200.УЗПОУ-D11.

Стадия	Лист	Листов
РД	3	3

Изометрический чертеж трубопровода
500-DC-63CS02-HH-D1143

EAST WEST ENGINEERING
ООО "EAST-WEST Engineering"
г. Ташкент 2026г.

Формат A2 594x420

Взам. инв. №
Подпись и дата
Инв.№ подл.