
N
СЕВЕР

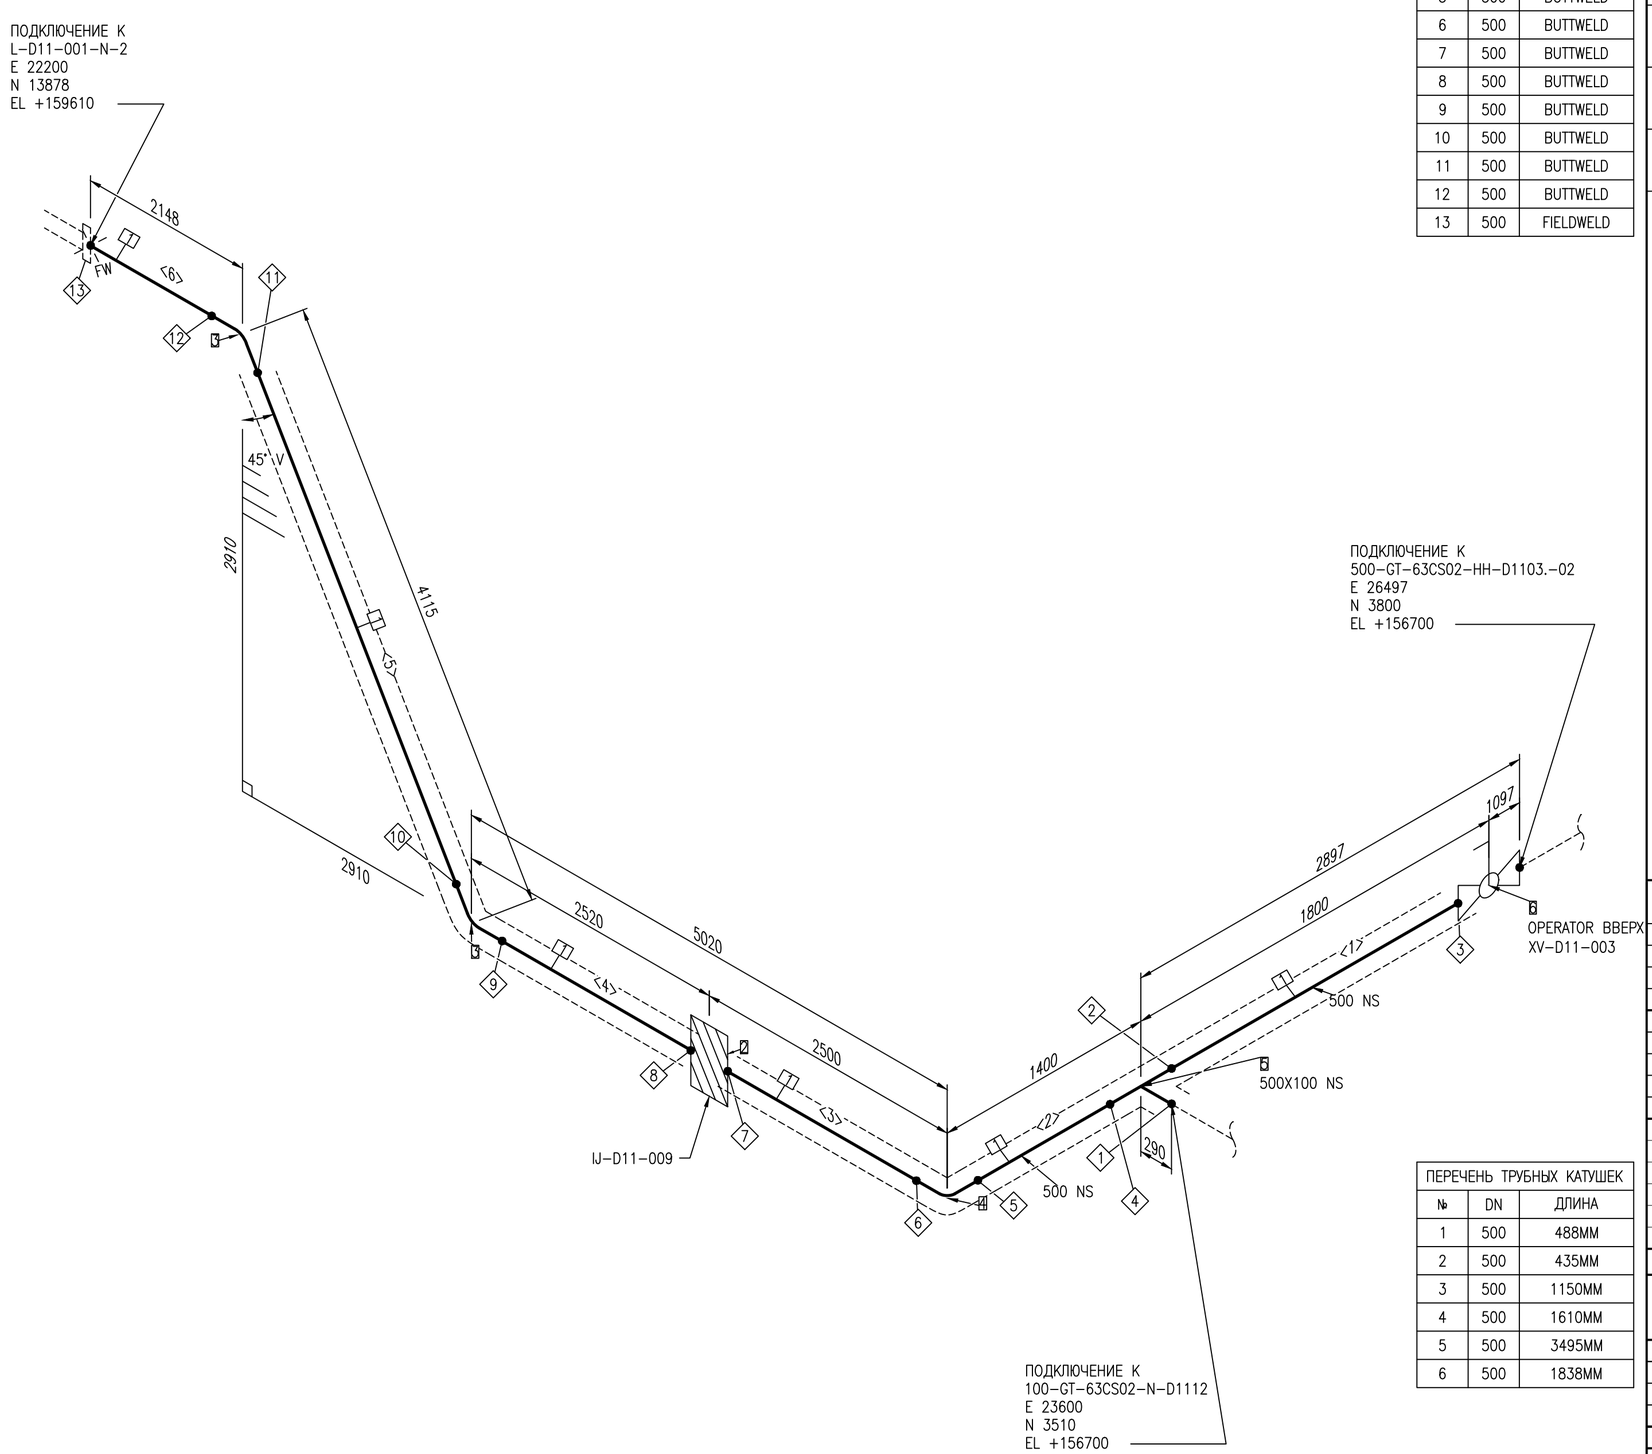

ПЕРЕЧЕНЬ СВАРНЫХ ШВОВ		
№	DN	ТИП
1	100	BUTTWELD
2	500	BUTTWELD
3	500	BUTTWELD
4	500	BUTTWELD
5	500	BUTTWELD
6	500	BUTTWELD
7	500	BUTTWELD
8	500	BUTTWELD
9	500	BUTTWELD
10	500	BUTTWELD
11	500	BUTTWELD
12	500	BUTTWELD
13	500	FIELDWELD

ПЕРЕЧЕНЬ ТРУБНЫХ КАТУШЕК		
№	DN	ДЛИНА
1	500	488MM
2	500	435MM
3	500	1150MM
4	500	1610MM
5	500	3495MM
6	500	1838MM

СПЕЦИФИКАЦИЯ ИЗДЕЛИЙ И МАТЕРИАЛОВ

ПОЗ.	НАИМЕНОВАНИЕ	СТАНДАРТ	КОЛ.	ПРИМЕЧАНИЕ
1	Трубы стальные сварные прямошовные, типа 3, К60, 530Х8	ГОСТ 31447-2012	9.1М	
2	Изолирующее соединение приварное, 6.3 МПа, 530Х8	EWE0426-MGL1-PRE-054-DSH-610135	1	
3	Отвод ОК I 45-530(8К60)-5,5(6,9)-0,75-1,5DN-30, сталь 60	ТУ 1469-017-38948552-2015	2	
4	Отвод ОК I 90-530(8К60)-5,5(6,9)-0,75-1,5DN-30, сталь 60	ТУ 1469-017-38948552-2015	1	
5	Тройник Т I 530(8К60)-114(5К48)-5,5(6,9)-0,75-30, сталь К60	ТУ 1469-017-38948552-2015	1	
6	Кран шаровой DN500 PN-6,3 МПа с пневмогидроприводом, приварной, подземный	EWE0426-MGL1-PRE-054-DSH-610127	1	

Трубопровод	ДАННЫЕ ПО ТРУБОПРОВОДУ		
500-GT-63CS02-HH-D1103	Расчетные параметры	Температура	-26,9...+85 °C
		Давление	6,3 MPa
	Рабочие параметры	Температура	-20...+40 °C
		Давление	5,5 MPa
Ссылочные чертежи No	Параметры испытания	Тип	Гидравлическое
EWE0426-MGL1-PRE-054-SCM-610102		Давление	6,9 MPa
	Изоляция	Тип	HH
		Толщина	mm
	Катодная защита	Да или Нет	Да

Рев.	Дата	Назначение ревизии	Проверил	Утвердил
A1	25.09.2026	Утверждено для строительства		
R1	27.08.2026	Выпущено для рассмотрения		

ЗАКАЗЧИК: UTG | ГЕНЕРАЛЬНЫЙ ПОДРЯДЧИК: UET | ПОДРЯДЧИК: PBG | ГЕНЕРАЛЬНЫЙ ПРОЕКТИРОВЩИК: EAST WEST ENGINEERING

Изм.	Кол.уч.	Лист	№док.	Подпись	Дата	
ГИП		Кирпичников С.			09.2026	
Нач.отд.		Рябинин А.			09.2026	
Исполн.		Таштимуров Р.			09.2026	
Н.контр		Кирпичников С.			09.2026	

EWE0426-MGL1-PRE-054-ISO-690607-A1

«СТРОИТЕЛЬСТВО НОВЫХ НИТОК (УЧАСТКОВ) ГАЗОПРОВОДОВ «ГАЗЛИ - САРИМОЙ» И «АКЧАЛОК - ГАЗЛИ - НУКУС» ОБЩЕЙ ПРОТЯЖЕННОСТЬЮ НЕ МЕНЕЕ 275 КМ».

ГАЗОПРОВОД «ГАЗЛИ-САРИМОЙ» (54 КМ)
Узел приема/запуска очистных устройств DN1200.УЗПОУ-D11.

Стадия	Лист	Листов
РД	1	3


Изометрический чертеж трубопровода
500-GT-63CS02-HH-D1103

ООО "EAST-WEST Engineering"
г. Ташкент 2026г.

Взам. инв. №
Подпись и дата
Инв.№ подл.

Формат А2 594x420

ПЕРЕЧЕНЬ СВАРНЫХ ШВОВ		
№	DN	ТИП
1	100	BUTTWELD
2	500	BUTTWELD
3	500	BUTTWELD
4	500	BUTTWELD
5	500	BUTTWELD

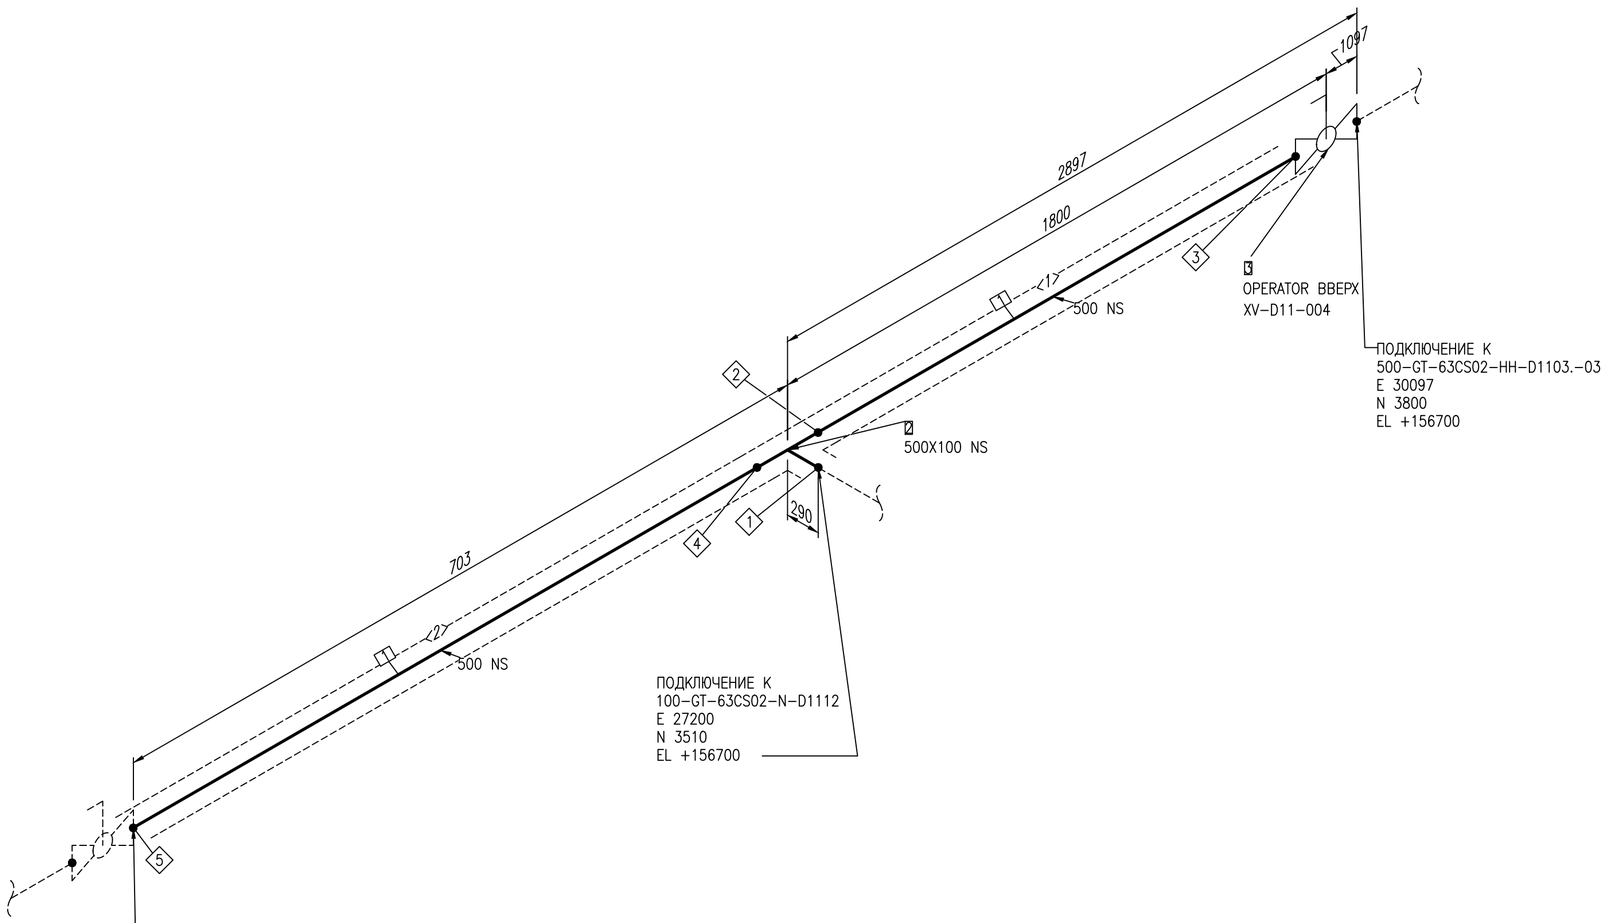

ПЕРЕЧЕНЬ ТРУБНЫХ КАТУШЕК		
№	DN	ДЛИНА
1	500	488ММ
2	500	488ММ

СПЕЦИФИКАЦИЯ ИЗДЕЛИЙ И МАТЕРИАЛОВ

ПОЗ.	НАИМЕНОВАНИЕ	СТАНДАРТ	КОЛ.	ПРИМЕЧАНИЕ
1	Трубы стальные сварные прямошовные, типа 3, К60, 530Х8	ГОСТ 31447-2012	1.0М	
2	Тройник Т I 530(8К60)-114(5К48)-5,5(6,9)-0,75-30, сталь К60	ТУ 1469-017-38948552-2015	1	
3	Кран шаровой DN500 PN-6,3 МПа с пневмогидроприводом, приварной, подземный	EWE0426-MGL1-PRE-054-DSH-610127	1	

Трубопровод	ДАННЫЕ ПО ТРУБОПРОВОДУ		
500-GT-63CS02-HH-D1103	Расчетные параметры	Температура	-26,9...+85 °C
		Давление	6,3 MPa
	Рабочие параметры	Температура	-20...+40 °C
		Давление	5,5 MPa
	Параметры испытания	Тип	Гидравлическое
Ссылочные чертежи No		Давление	6,9 MPa
EWE0426-MGL1-PRE-054-SCM-610102	Изоляция	Тип	НН
		Толщина	mm
	Катодная защита	Да или Нет	Да

Рев.	Дата	Назначение ревизии	Проверил	Утвердил
A1	25.09.2026	Утверждено для строительства		
R1	27.08.2026	Выпущено для рассмотрения		

ЗАКАЗЧИК: UTG ГЕНЕРАЛЬНЫЙ ПОДРЯДЧИК: UET ПОДРЯДЧИК: PBG ГЕНЕРАЛЬНЫЙ ПРОЕКТИРОВЩИК: EAST WEST ENGINEERING

Изм.	Кол.уч.	Лист	№док.	Подпись	Дата
ГИП		Кирпичников С.			09.2026
Нач.отд.		Рябинин А.			09.2026
Исполн.		Таштимуров Р.			09.2026
Н.контр		Кирпичников С.			09.2026

EWE0426-MGL1-PRE-054-ISO-690607-A1

«СТРОИТЕЛЬСТВО НОВЫХ НИТОК (УЧАСТКОВ) ГАЗОПРОВОДОВ «ГАЗЛИ - САРИМОЙ» И «АКЧАЛОК - ГАЗЛИ - НУКУС» ОБЩЕЙ ПРОТЯЖЕННОСТЬЮ НЕ МЕНЕЕ 275 КМ».

ГАЗОПРОВОД «ГАЗЛИ-САРИМОЙ» (54 КМ) Узел приема/запуска очистных устройств DN1200.УЗПОУ-D11.

Стадия	Лист	Листов
РД	2	3

Изометрический чертеж трубопровода 500-GT-63CS02-HH-D1103

ООО "EAST-WEST Engineering" г. Ташкент 2026г.


Взам. инв. №

Подпись и дата

Инв.№ подл.

Формат А2 594x420

ПЕРЕЧЕНЬ СВАРНЫХ ШВОВ		
№	DN	ТИП
1	100	BUTTWELD
2	500	BUTTWELD
3	500	BUTTWELD
4	500	BUTTWELD
5	500	WELD
6	500	BUTTWELD
7	500	BUTTWELD

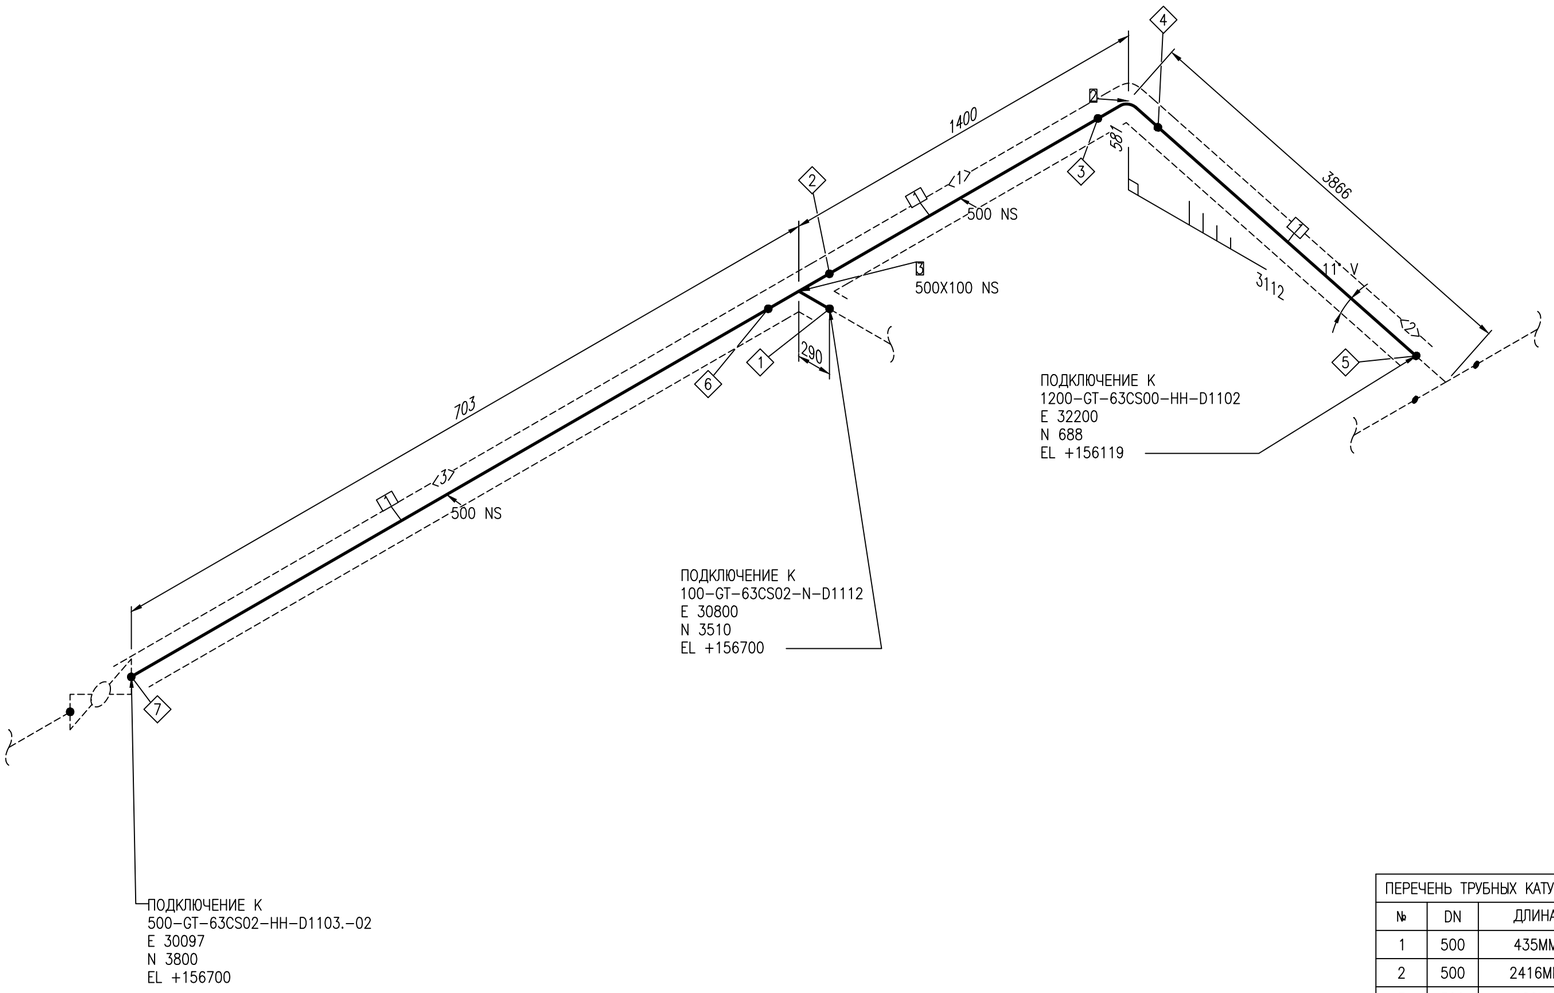

ПЕРЕЧЕНЬ ТРУБНЫХ КАТУШЕК		
№	DN	ДЛИНА
1	500	435MM
2	500	2416MM
3	500	488MM

СПЕЦИФИКАЦИЯ ИЗДЕЛИЙ И МАТЕРИАЛОВ				
ПОЗ.	НАИМЕНОВАНИЕ	СТАНДАРТ	КОЛ.	ПРИМЕЧАНИЕ
1	Трубы стальные сварные прямошовные, тип 3, К60, 530Х8	ГОСТ 31447-2012	3.4М	
2	Отвод ОК I 90-530(8К60)-5,5(6,9)-0,75-1,5DN-30, сталь 60	ТУ 1469-017-38948552-2015	1	
3	Тройник Т I 530(8К60)-114(5К48)-5,5(6,9)-0,75-30, сталь К60	ТУ 1469-017-38948552-2015	1	

Трубопровод	ДАННЫЕ ПО ТРУБОПРОВОДУ		
500-GT-63CS02-HH-D1103	Расчетные параметры	Температура	-26,9...+85 °C
		Давление	6,3 MPa
	Рабочие параметры	Температура	-20...+40 °C
		Давление	5,5 MPa
Ссылочные чертежи No	Параметры испытания	Тип	Гидравлическое
EWE0426-MGL1-PRE-054-SCM-610102		Давление	6,9 MPa
	Изоляция	Тип	HH
		Толщина	mm
	Катодная защита	Да или Нет	Да

Рев.	Дата	Назначение ревизии	Проверил	Утвердил
A1	25.09.2026	Утверждено для строительства		
R1	27.08.2026	Выпущено для рассмотрения		

ЗАКАЗЧИК: UTG ГЕНЕРАЛЬНЫЙ ПОДРЯДЧИК: UET ПОДРЯДЧИК: PBG ГЕНЕРАЛЬНЫЙ ПРОЕКТИРОВЩИК: EAST WEST ENGINEERING

Изм.	Кол.уч.	Лист	№док.	Подпись	Дата
ГИП		Кирпичников С.			09.2026
Нач.отд.		Рябинин А.			09.2026
Исполн.		Таштимуров Р.			09.2026
Н.контр		Кирпичников С.			09.2026

EWE0426-MGL1-PRE-054-ISO-690607-A1

«СТРОИТЕЛЬСТВО НОВЫХ НИТОК (УЧАСТКОВ) ГАЗОПРОВОДОВ «ГАЗЛИ - САРИМОЙ» И «АКЧАЛОК - ГАЗЛИ - НУКУС» ОБЩЕЙ ПРОТЯЖЕННОСТЬЮ НЕ МЕНЕЕ 275 КМ».

ГАЗОПРОВОД «ГАЗЛИ-САРИМОЙ» (54 КМ)
Узел приема/запуска очистных устройств DN1200.УЗПОЧ-D11.

Стадия	Лист	Листов
РД	3	3

Изометрический чертеж трубопровода
500-GT-63CS02-HH-D1103

ООО "EAST-WEST Engineering"
г. Ташкент 2026г.

Взам. инв. №
Подпись и дата
Инв.№ подл.

Формат А2 594х420