
ПЕРЕЧЕНЬ СВАРНЫХ ШВОВ		
№	DN	ТИП
1	150	BUTTWELD
2	150	BUTTWELD
3	150	BUTTWELD
4	150	BUTTWELD
5	150	BUTTWELD
6	150	BUTTWELD
7	150	TAPWELD
8	15	WELD
9	15	SOCKETWELD
10	150	TAPWELD
11	15	WELD
12	15	SOCKETWELD

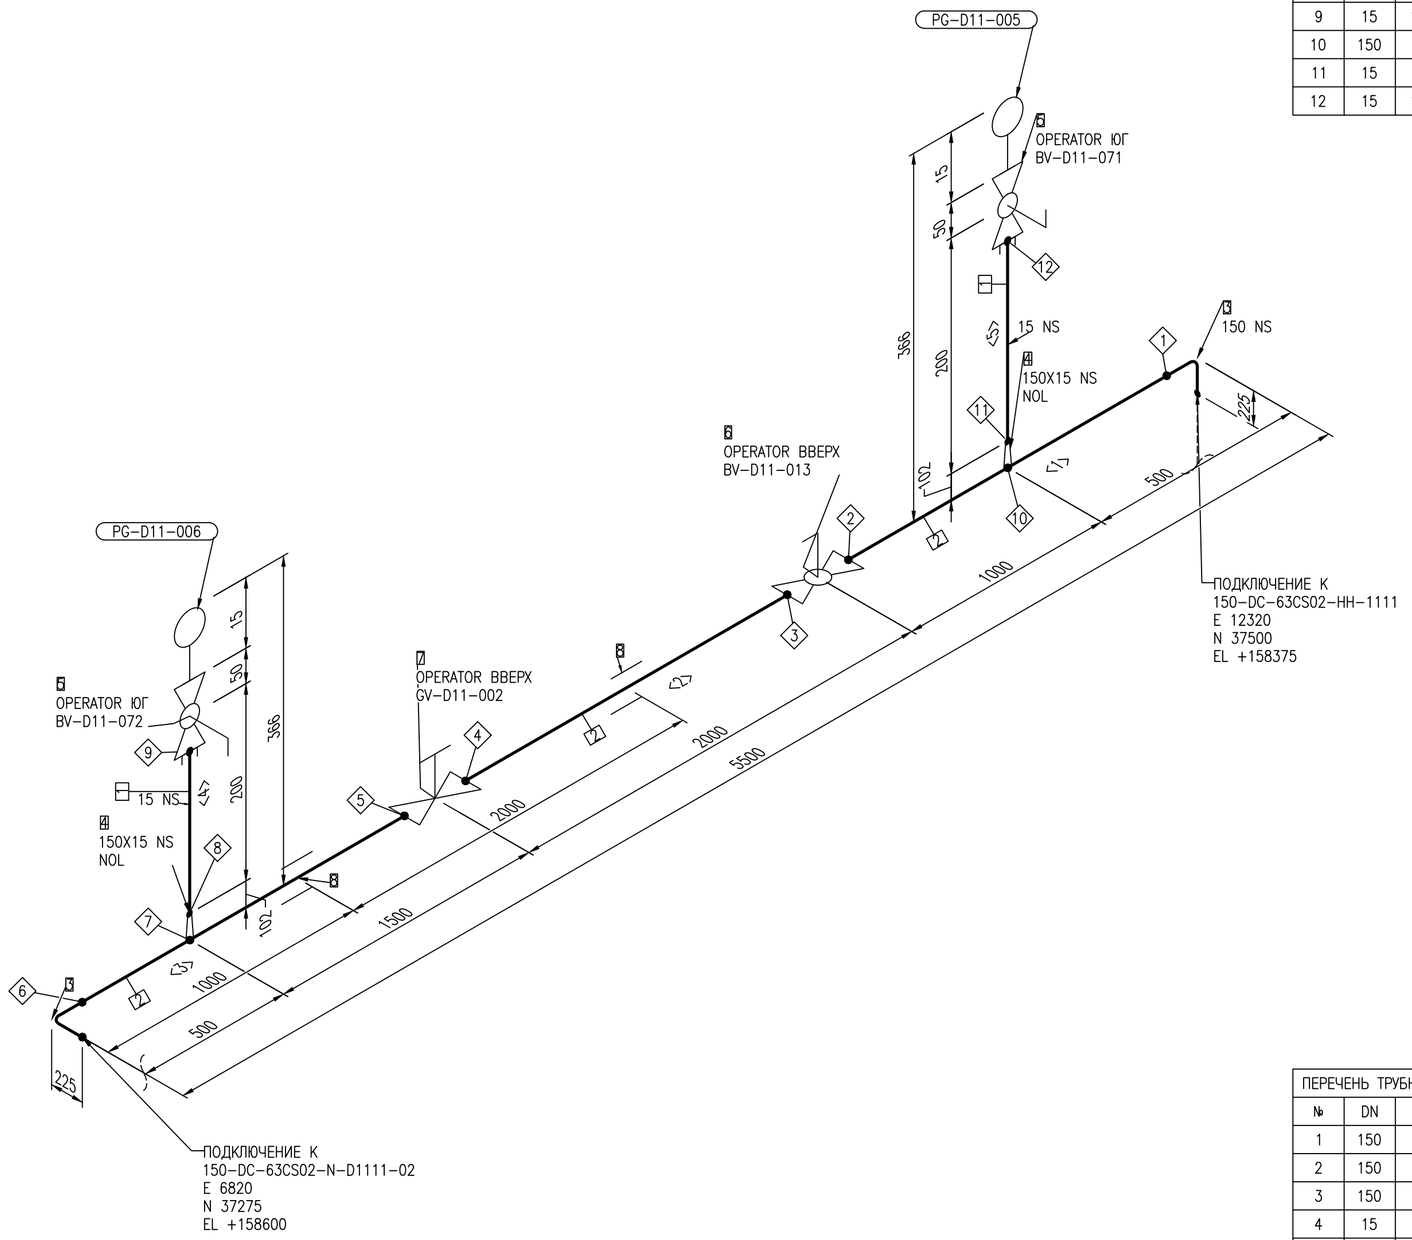

ПЕРЕЧЕНЬ ТРУБНЫХ КАТУШЕК		
№	DN	ДЛИНА
1	150	996MM
2	150	1399MM
3	150	1453MM
4	15	150MM
5	15	150MM

СПЕЦИФИКАЦИЯ ИЗДЕЛИЙ И МАТЕРИАЛОВ

ПОЗ.	НАИМЕНОВАНИЕ	СТАНДАРТ	КОЛ.	ПРИМЕЧАНИЕ
1	Трубы стальные бесшовные холоднодеформированные Ст20, 22Х3	ГОСТ 8734-75/ ГОСТ 8733-74	0.3М	
2	Трубы стальные бесшовные горячедеформированные 09Г2С, 159Х6	ТУ 14-3-1128-2000	3.9М	
3	Отвод ОК I 90-159(6К48)-5,5(6,9)-0,75-1,5DN-30, сталь 09Г2С	ТУ 1469-017-38948552-2015	2	
4	Штуцер приварной ШУсТ-1-150-22Х3.0-6,3-20-2	ТУ 3600-010-88626180-2012	2	
5	Кран шаровой DN15 PN-6,3 МПа с ручным приводом, приварной х резьбовой, 1/2" NPT F, надземный	EWE0426-MGL1-PRE-054-DSH-610127	2	
6	Кран шаровой DN150 PN-6,3 МПа с ручным приводом	EWE0426-MGL1-PRE-054-DSH-610127	1	
7	Клапан запорно-регулирующий DN150 PN-6,3МПа с ручным приводом	EWE0426-MGL1-PRE-054-DSH-610128	1	
8	ОПОРА 159-КХ-А11-ВСт3пс	ОСТ 36-146-88	2	

Трубопровод	ДАННЫЕ ПО ТРУБОПРОВОДУ		
150-DC-63CS02-N-D1111	Расчетные параметры	Температура	-26,9...+85 °C
		Давление	6,3 MPa
	Рабочие параметры	Температура	-20...+40 °C
		Давление	5,5 MPa
	Параметры испытания	Тип	Гидравлическое
Ссылочные чертежи No		Давление	6,9 MPa
EWE0426-MGL1-PRE-054-SCM-610102	Изоляция	Тип	N
		Толщина	mm
	Катодная защита	Да или Нет	Да

Рев.	Дата	Назначение ревизии	Проверил	Утвердил
A1	25.09.2026	Утверждено для строительства		
R1	27.08.2026	Выпущено для рассмотрения		

ЗАКАЗЧИК: UTG ГЕНЕРАЛЬНЫЙ ПОДРЯДЧИК: UET ПОДРЯДЧИК: PBG ГЕНЕРАЛЬНЫЙ ПРОЕКТИРОВЩИК: EAST WEST ENGINEERING

EWE0426-MGL1-PRE-054-ISO-690614-A1

«СТРОИТЕЛЬСТВО НОВЫХ НИТОК (УЧАСТКОВ) ГАЗОПРОВОДОВ «ГАЗЛИ - САРИМОЙ» И «АКЧАЛОК - ГАЗЛИ - НУКУС» ОБЩЕЙ ПРОТЯЖЕННОСТЬЮ НЕ МЕНЕЕ 275 КМ».

Изм.	Кол.уч.	Лист	№док.	Подпись	Дата			
ГИП		Кирпичников С.			09.2026	ГАЗОПРОВОД «ГАЗЛИ-САРИМОЙ» (54 КМ) Узел приема/запуска очистных устройств DN1200.УЗПОУ-D11.	Стадия	Лист	Листов
Нач.отд.		Рябинин А.			09.2026		РД	1	2
Исполн.		Таштимуров Р.			09.2026				
Н.контр		Кирпичников С.			09.2026	Изометрический чертеж трубопровода 150-DC-63CS02-N-D1111	EAST WEST ENGINEERING	ООО "EAST-WEST Engineering" г. Ташкент 2026г.	

Взам. инв. №


Подпись и дата

Инв.№ подл.

Формат А2 594x420

СЕВЕР

ПЕРЕЧЕНЬ СВАРНЫХ ШВОВ		
№	DN	ТИП
1	150	BUTTWELD
2	150	BUTTWELD
3	150	BUTTWELD
4	150	BUTTWELD
5	150	BUTTWELD
6	150	BUTTWELD

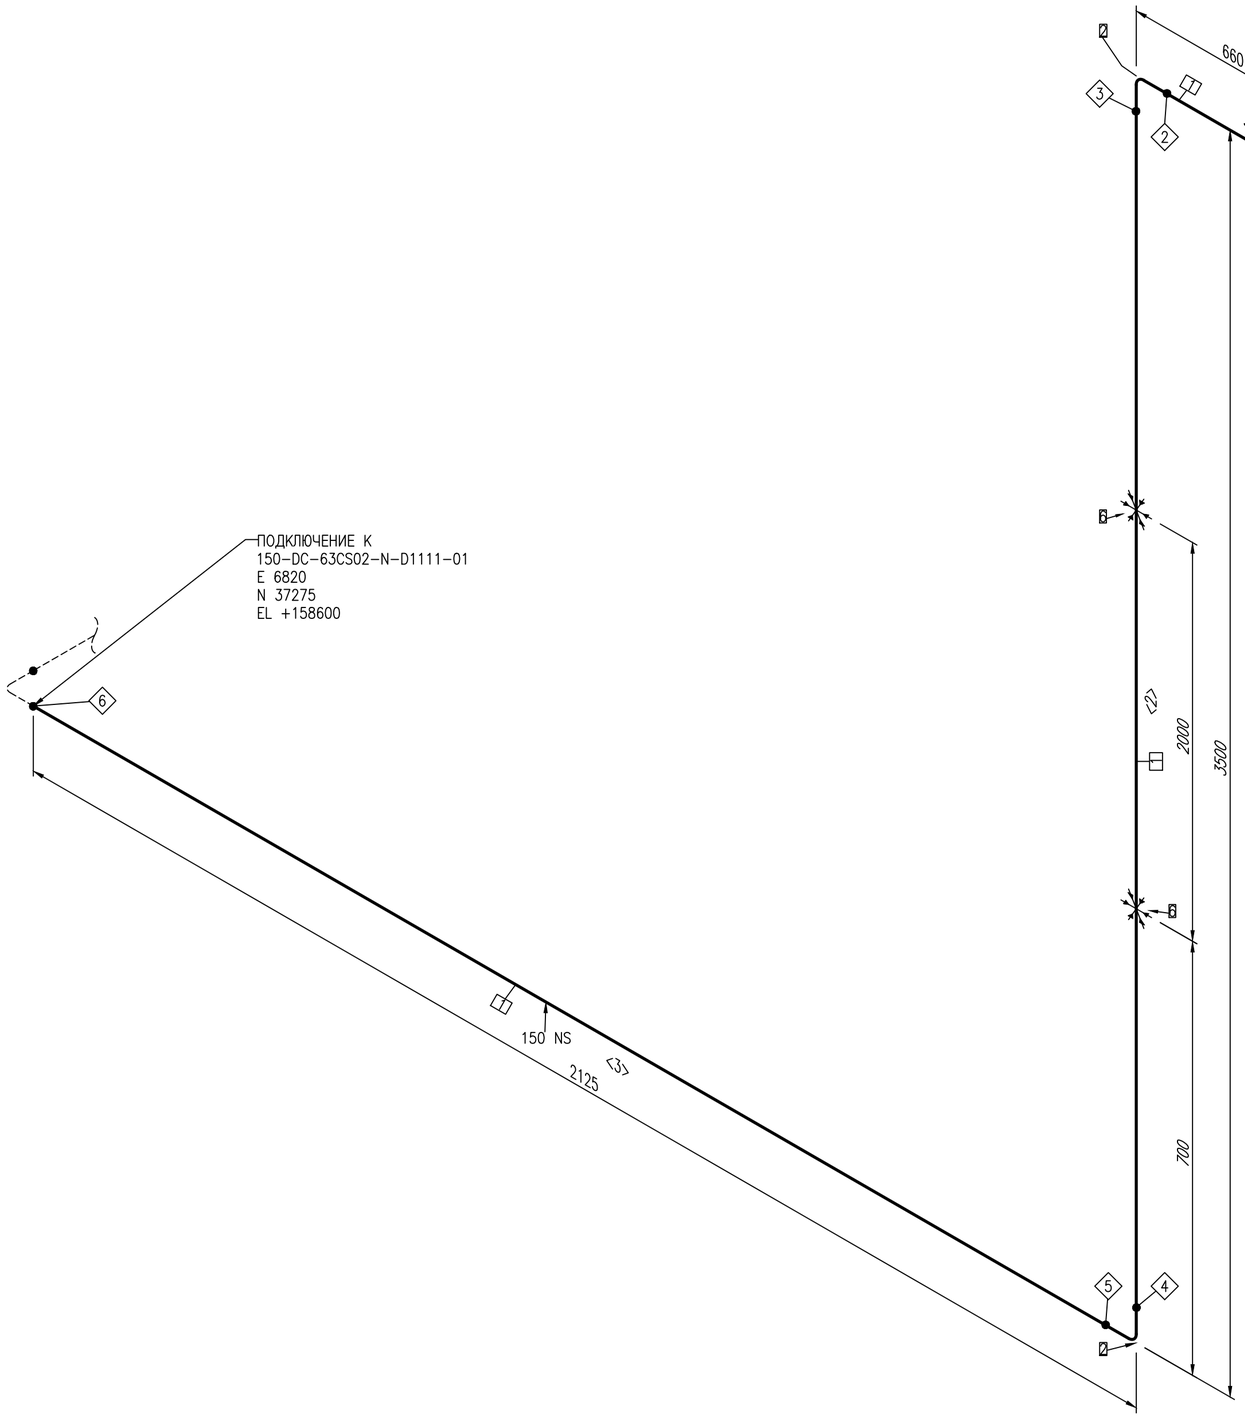

ПЕРЕЧЕНЬ ТРУБНЫХ КАТУШЕК		
№	DN	ДЛИНА
1	150	328ММ
2	150	3050ММ
3	150	1900ММ

СПЕЦИФИКАЦИЯ ИЗДЕЛИЙ И МАТЕРИАЛОВ

ПОЗ.	НАИМЕНОВАНИЕ	СТАНДАРТ	КОЛ.	ПРИМЕЧАНИЕ
1	Трубы стальные бесшовные горячедеформированные 09Г2С, 159Х6	ТУ 14-3-1128-2000	5.3М	
2	Отвод ОК I 90-159(6К48)-5,5(6,9)-0,75-1,5DN-30, сталь 09Г2С	ТУ 1469-017-38948552-2015	2	
3	Фланец стальной приварной встык, тип 11, исполнение J, ряд 1, 6.3 МПа, сталь 09Г2С, 159Х6	ГОСТ 33259-2015	1	
4	Крепежный комплект 2-1-М30х150, шпильки Ст35, шайбы Ст20, гайки Ст25, для Ду 150	ОСТ 26-2040-96	8	
5	Прокладка овального сечения, линзовая стальная, тип 1, Сталь 08КП, 6.3 МПа, Ду 150	ГОСТ 34655-2020	1	
6	ОПОРА 159-ХБ-А-ВСт3пс	ОСТ 36-146-88	2	

Трубопровод	ДАННЫЕ ПО ТРУБОПРОВОДУ		
150-DC-63CS02-N-D1111	Расчетные параметры	Температура	-26,9...+85 °C
		Давление	6,3 MPa
	Рабочие параметры	Температура	-20...+40 °C
		Давление	5,5 MPa
	Параметры испытания	Тип	Гидравлическое
Ссылочные чертежи No		Давление	6,9 MPa
EWE0426-MGL1-PRE-054-SCM-610102	Изоляция	Тип	N
		Толщина	mm
	Катодная защита	Да или Нет	Да

Рев.	Дата	Назначение ревизии	Проверил	Утвердил
A1	25.09.2026	Утверждено для строительства		
R1	27.08.2026	Выпущено для рассмотрения		

ЗАКАЗЧИК: UTG ГЕНЕРАЛЬНЫЙ ПОДРЯДЧИК: UET ПОДРЯДЧИК: PBG ГЕНЕРАЛЬНЫЙ ПРОЕКТИРОВЩИК: EAST WEST ENGINEERING

Изм.	Кол.уч.	Лист	№док.	Подпись	Дата
ГИП		Кирпичников С.			09.2026
Нач.отд.		Рябинин А.			09.2026
Исполн.		Таштимуров Р.			09.2026
Н.контр		Кирпичников С.			09.2026

EWE0426-MGL1-PRE-054-ISO-690614-A1

«СТРОИТЕЛЬСТВО НОВЫХ НИТОК (УЧАСТКОВ) ГАЗОПРОВОДОВ «ГАЗЛИ - САРИМОЙ» И «АКЧАЛОК - ГАЗЛИ - НУКУС» ОБЩЕЙ ПРОТЯЖЕННОСТЬЮ НЕ МЕНЕЕ 275 КМ».

ГАЗОПРОВОД «ГАЗЛИ-САРИМОЙ» (54 КМ)
Узел приема/запуска очистных устройств DN1200.УЗПОУ-D11.

Стадия	Лист	Листов
РД	2	2

Изометрический чертеж трубопровода
150-DC-63CS02-N-D1111

EAST WEST ENGINEERING
ООО "EAST-WEST Engineering"
г. Ташкент 2026г.

Взам. инв. №
Подпись и дата
Инв.№ подл.

Формат А2 594x420