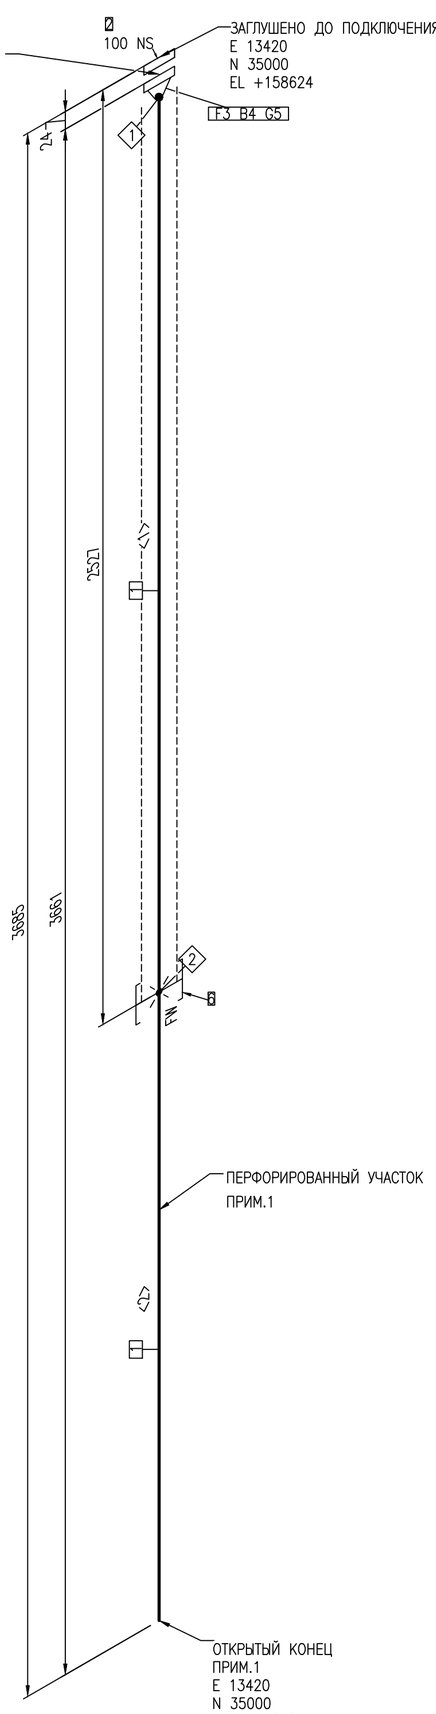


ПЕРЕЧЕНЬ СВАРНЫХ ШВОВ		
№	DN	ТИП
1	100	BUTTWELD
2	100	FIELDWELD

ПЕРЕЧЕНЬ ТРУБНЫХ КАТУШЕК		
№	DN	ДЛИНА
1	100	2426ММ
2	100	1159ММ

СПЕЦИФИКАЦИЯ ИЗДЕЛИЙ И МАТЕРИАЛОВ

ПОЗ.	НАИМЕНОВАНИЕ	СТАНДАРТ	КОЛ.	ПРИМЕЧАНИЕ
1	Трубы стальные бесшовные горячедеформированные 09Г2С, 114Х5	ТУ 14-3-1128-2000	3.6М	
2	Заглушка фланцевая стальная АТК 24.200.02-90, исполнение 4, 6.3 МПа, сталь 09Г2С, DN100	АТК 24.200.02-90	1	
3	Фланец стальной приварной встык, тип 11, исполнение J, ряд 1, 6.3 МПа, сталь 09Г2С, 114Х5	ГОСТ 33259-2015	1	
4	Крепежный комплект 2-1-М24х130, шпильки Ст35, шайбы Ст20, гайки Ст25, для Ду 100	ОСТ 26-2040-96	8	
5	Прокладка овального сечения, линзовая стальная, тип 1, Сталь 08КП, 6.3 МПа, Ду 100	ГОСТ 34655-2020	1	
6	УСИЛИВАЮЩАЯ НАКЛАДКА, 1220(16К60) типа 3, ГОСТ 31447-2012 Х 114(5К42) 09Г2С, ТУ 14-3-1128-2000		1	СМ. ДОКУМЕНТ EWE0426-MGL1-PRE-054-DRW-690203, ЛИСТ 3, ВИД "С"

ПРИМЕЧАНИЕ:

1. Узел с детальным изображением участка трубы с отверстиями внутри коллектора-сборника предоставлен в документе: EWE0426-MGL1-PRE-054-DRW-690203, лист 3, Разрез 10-10

Трубопровод	ДАННЫЕ ПО ТРУБОПРОВОДУ		
100-GT-63CS02-N-D1114	Расчетные параметры	Температура	-26,9...+85 °C
		Давление	6,3 MPa
	Рабочие параметры	Температура	-20...+40 °C
		Давление	5,5 MPa
	Параметры испытания	Тип	Гидравлическое
Ссылочные чертежи No		Давление	6,9 MPa
EWE0426-MGL1-PRE-054-SCM-610102	Изоляция	Тип	N
		Толщина	mm
	Катодная защита	Да или Нет	Да

Рев.	Дата	Назначение ревизии	Проверил	Утвердил
A1	25.09.2026	Утверждено для строительства		
R1	27.08.2026	Выпущено для рассмотрения		

ЗАКАЗЧИК: UTG | ГЕНЕРАЛЬНЫЙ ПОДРЯДЧИК: UET | ПОДРЯДЧИК: PBG | ГЕНЕРАЛЬНЫЙ ПРОЕКТИРОВЩИК: EAST WEST ENGINEERING

Изм.	Кол.уч.	Лист	№док.	Подпись	Дата
ГИП		Кирпичников С.			09.2026
Нач.отд.		Рябинин А.			09.2026
Исполн.		Таштимуров Р.			09.2026
Н.контр		Кирпичников С.			09.2026

EWE0426-MGL1-PRE-054-ISO-690617-A1

«СТРОИТЕЛЬСТВО НОВЫХ НИТОК (УЧАСТКОВ) ГАЗОПРОВОДОВ «ГАЗЛИ - САРИМОЙ» И «АКЧАЛОК - ГАЗЛИ - НУКУС» ОБЩЕЙ ПРОТЯЖЕННОСТЬЮ НЕ МЕНЕЕ 275 КМ».

ГАЗОПРОВОД «ГАЗЛИ-САРИМОЙ» (54 КМ)
Узел приема/запуска очистных устройств DN1200.УЗПОУ-D11.

Стадия	Лист	Листов
РД	1	1

Изометрический чертеж трубопровода
100-GT-63CS02-N-D1114

ООО "EAST-WEST Engineering"
г. Ташкент 2026г.

Взам. инв. №

Подпись и дата

Инв.№ подл.

Формат А2 594х420