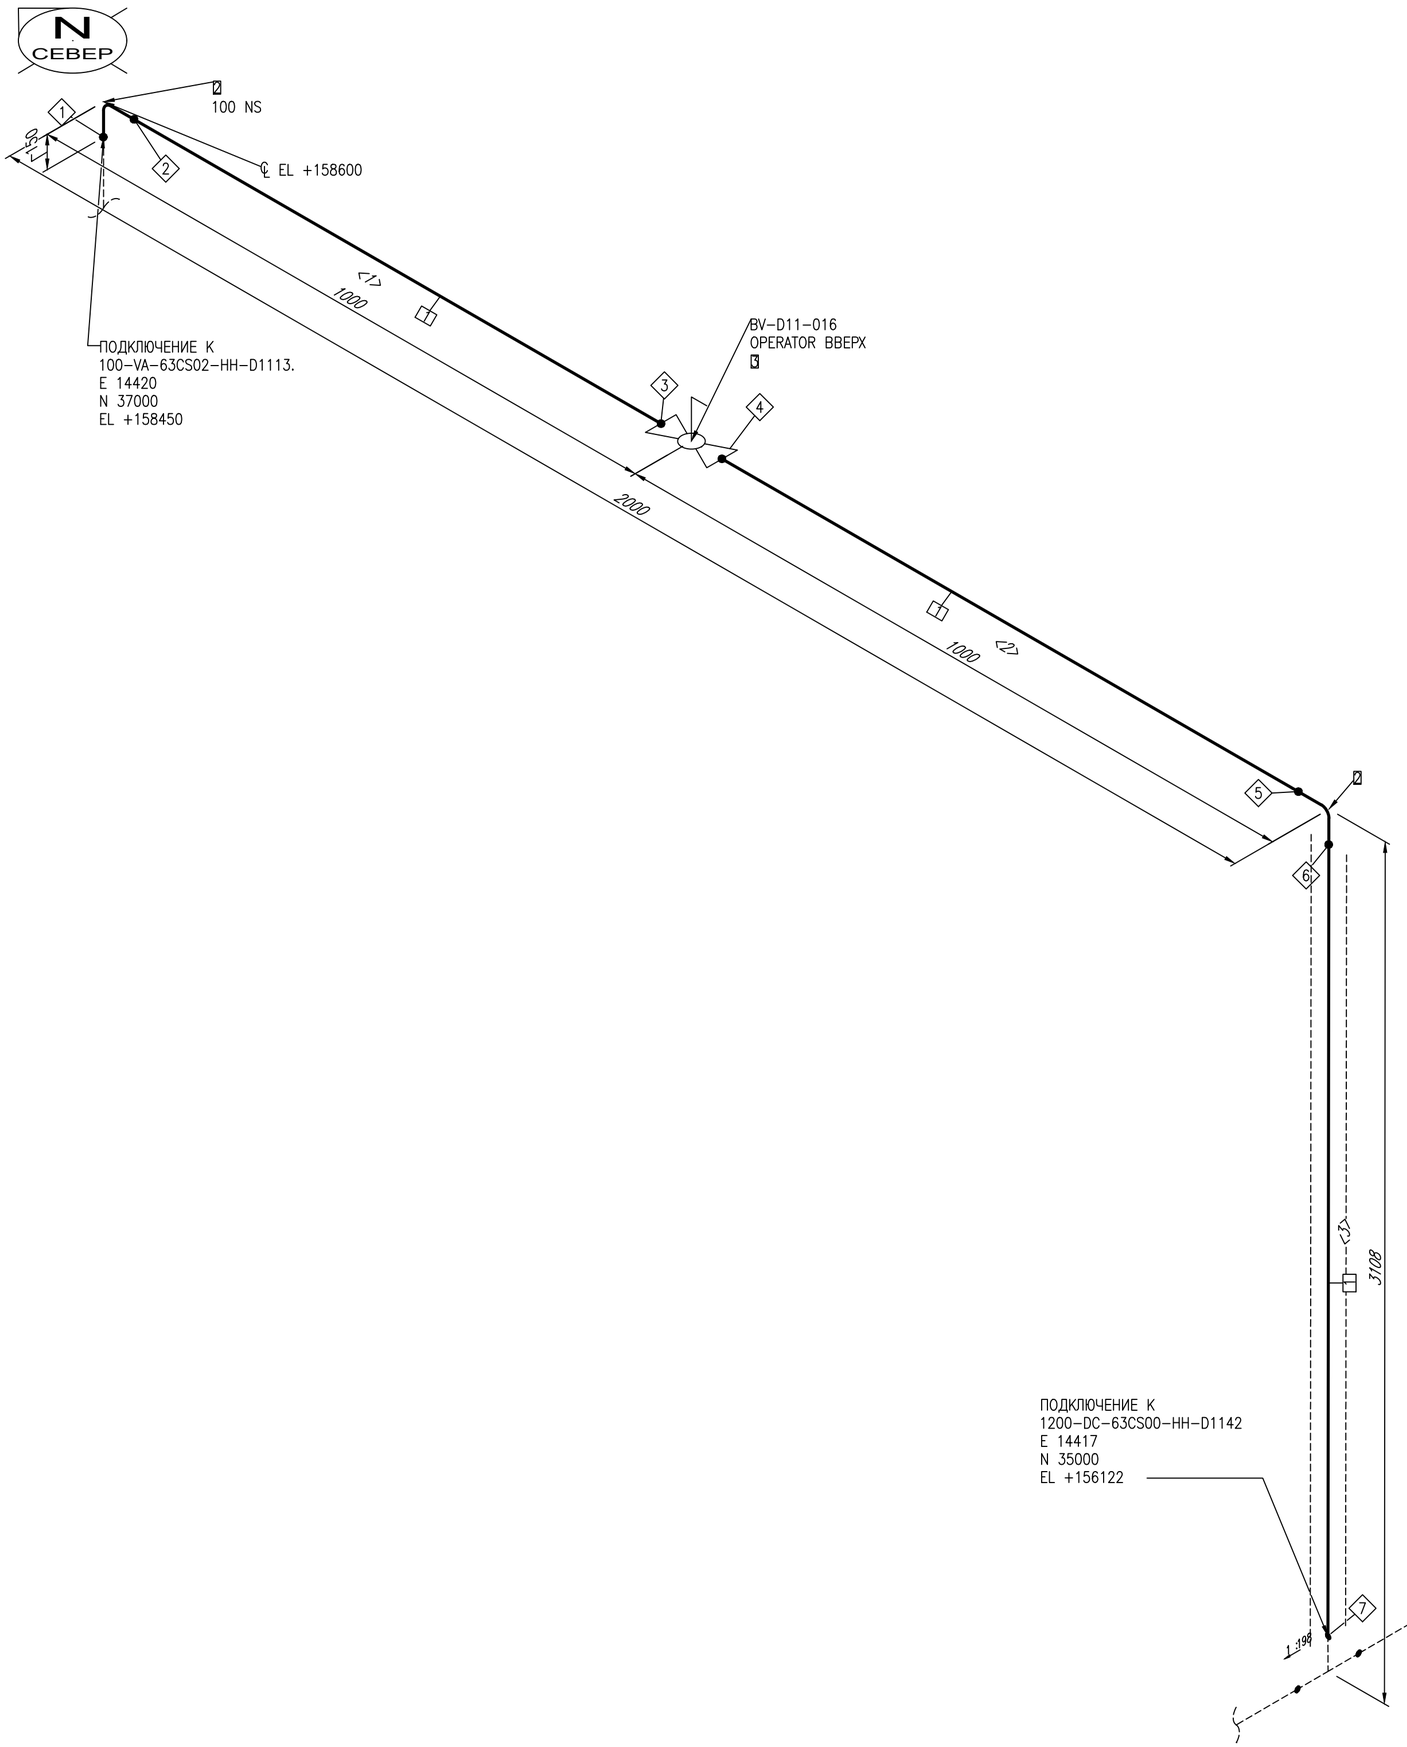


ПЕРЕЧЕНЬ СВАРНЫХ ШВОВ		
№	DN	ТИП
1	100	BUTTWELD
2	100	BUTTWELD
3	100	BUTTWELD
4	100	BUTTWELD
5	100	BUTTWELD
6	100	BUTTWELD
7	100	WELD

ПЕРЕЧЕНЬ ТРУБНЫХ КАТУШЕК		
№	DN	ДЛИНА
1	100	634ММ
2	100	634ММ
3	100	2328ММ

СПЕЦИФИКАЦИЯ ИЗДЕЛИЙ И МАТЕРИАЛОВ

ПОЗ.	НАИМЕНОВАНИЕ	СТАНДАРТ	КОЛ.	ПРИМЕЧАНИЕ
1	Трубы стальные бесшовные горячедеформированные 09Г2С, 114Х5	ТУ 14-3-1128-2000	3.6М	
2	Отвод ОК I 90-114(5К48)-5,5(6,9)-0,75-1,5DN-30, сталь 09Г2С	ТУ 1469-017-38948552-2015	2	
3	Кран шаровой DN100 PN-6,3 МПа с ручным приводом	EWE0426-MGL1-PRE-054-DSH-610127	1	

Трубопровод	ДАННЫЕ ПО ТРУБОПРОВОДУ		
100-VA-63CS02-N-D1113	Расчетные параметры	Температура	-26,9...+85 °C
		Давление	6,3 MPa
	Рабочие параметры	Температура	-20...+40 °C
		Давление	5,5 MPa
	Параметры испытания	Тип	Гидравлическое
Ссылочные чертежи No		Давление	6,9 MPa
EWE0426-MGL1-PRE-054-SCM-610102	Изоляция	Тип	N
		Толщина	mm
	Катодная защита	Да или Нет	Да

Рев.	Дата	Назначение ревизии	Проверил	Утвердил
A1	25.09.2026	Утверждено для строительства		
R1	27.08.2026	Выпущено для рассмотрения		

ЗАКАЗЧИК: UTG ГЕНЕРАЛЬНЫЙ ПОДРЯДЧИК: UET ПОДРЯДЧИК: PBG ГЕНЕРАЛЬНЫЙ ПРОЕКТИРОВЩИК: EAST WEST ENGINEERING

Изм.	Кол.уч.	Лист	№док.	Подпись	Дата	EWE0426-MGL1-PRE-054-ISO-690620-A1			
						«СТРОИТЕЛЬСТВО НОВЫХ НИТОК (УЧАСТКОВ) ГАЗОПРОВОДОВ «ГАЗЛИ - САРИМОЙ» И «АКЧАЛОК - ГАЗЛИ - НУКУС» ОБЩЕЙ ПРОТЯЖЕННОСТЬЮ НЕ МЕНЕЕ 275 КМ».			
ГИП		Кирпичников С.			09.2026	ГАЗОПРОВОД «ГАЗЛИ-САРИМОЙ» (54 КМ) Узел приема/запуска очистных устройств DN1200.УЗПОУ-D11.	Стадия	Лист	Листов
Нач.отд.		Рябинин А.			09.2026		РД	1	1
Исполн.		Таштимуров Р.			09.2026				
Н.контр		Кирпичников С.			09.2026	Изометрический чертеж трубопровода 100-VA-63CS02-N-D1113	EAST WEST ENGINEERING	ООО "EAST-WEST Engineering" г. Ташкент 2026г.	

Взам. инв. №

Подпись и дата

Инв.№ подл.

Формат А2 594x420