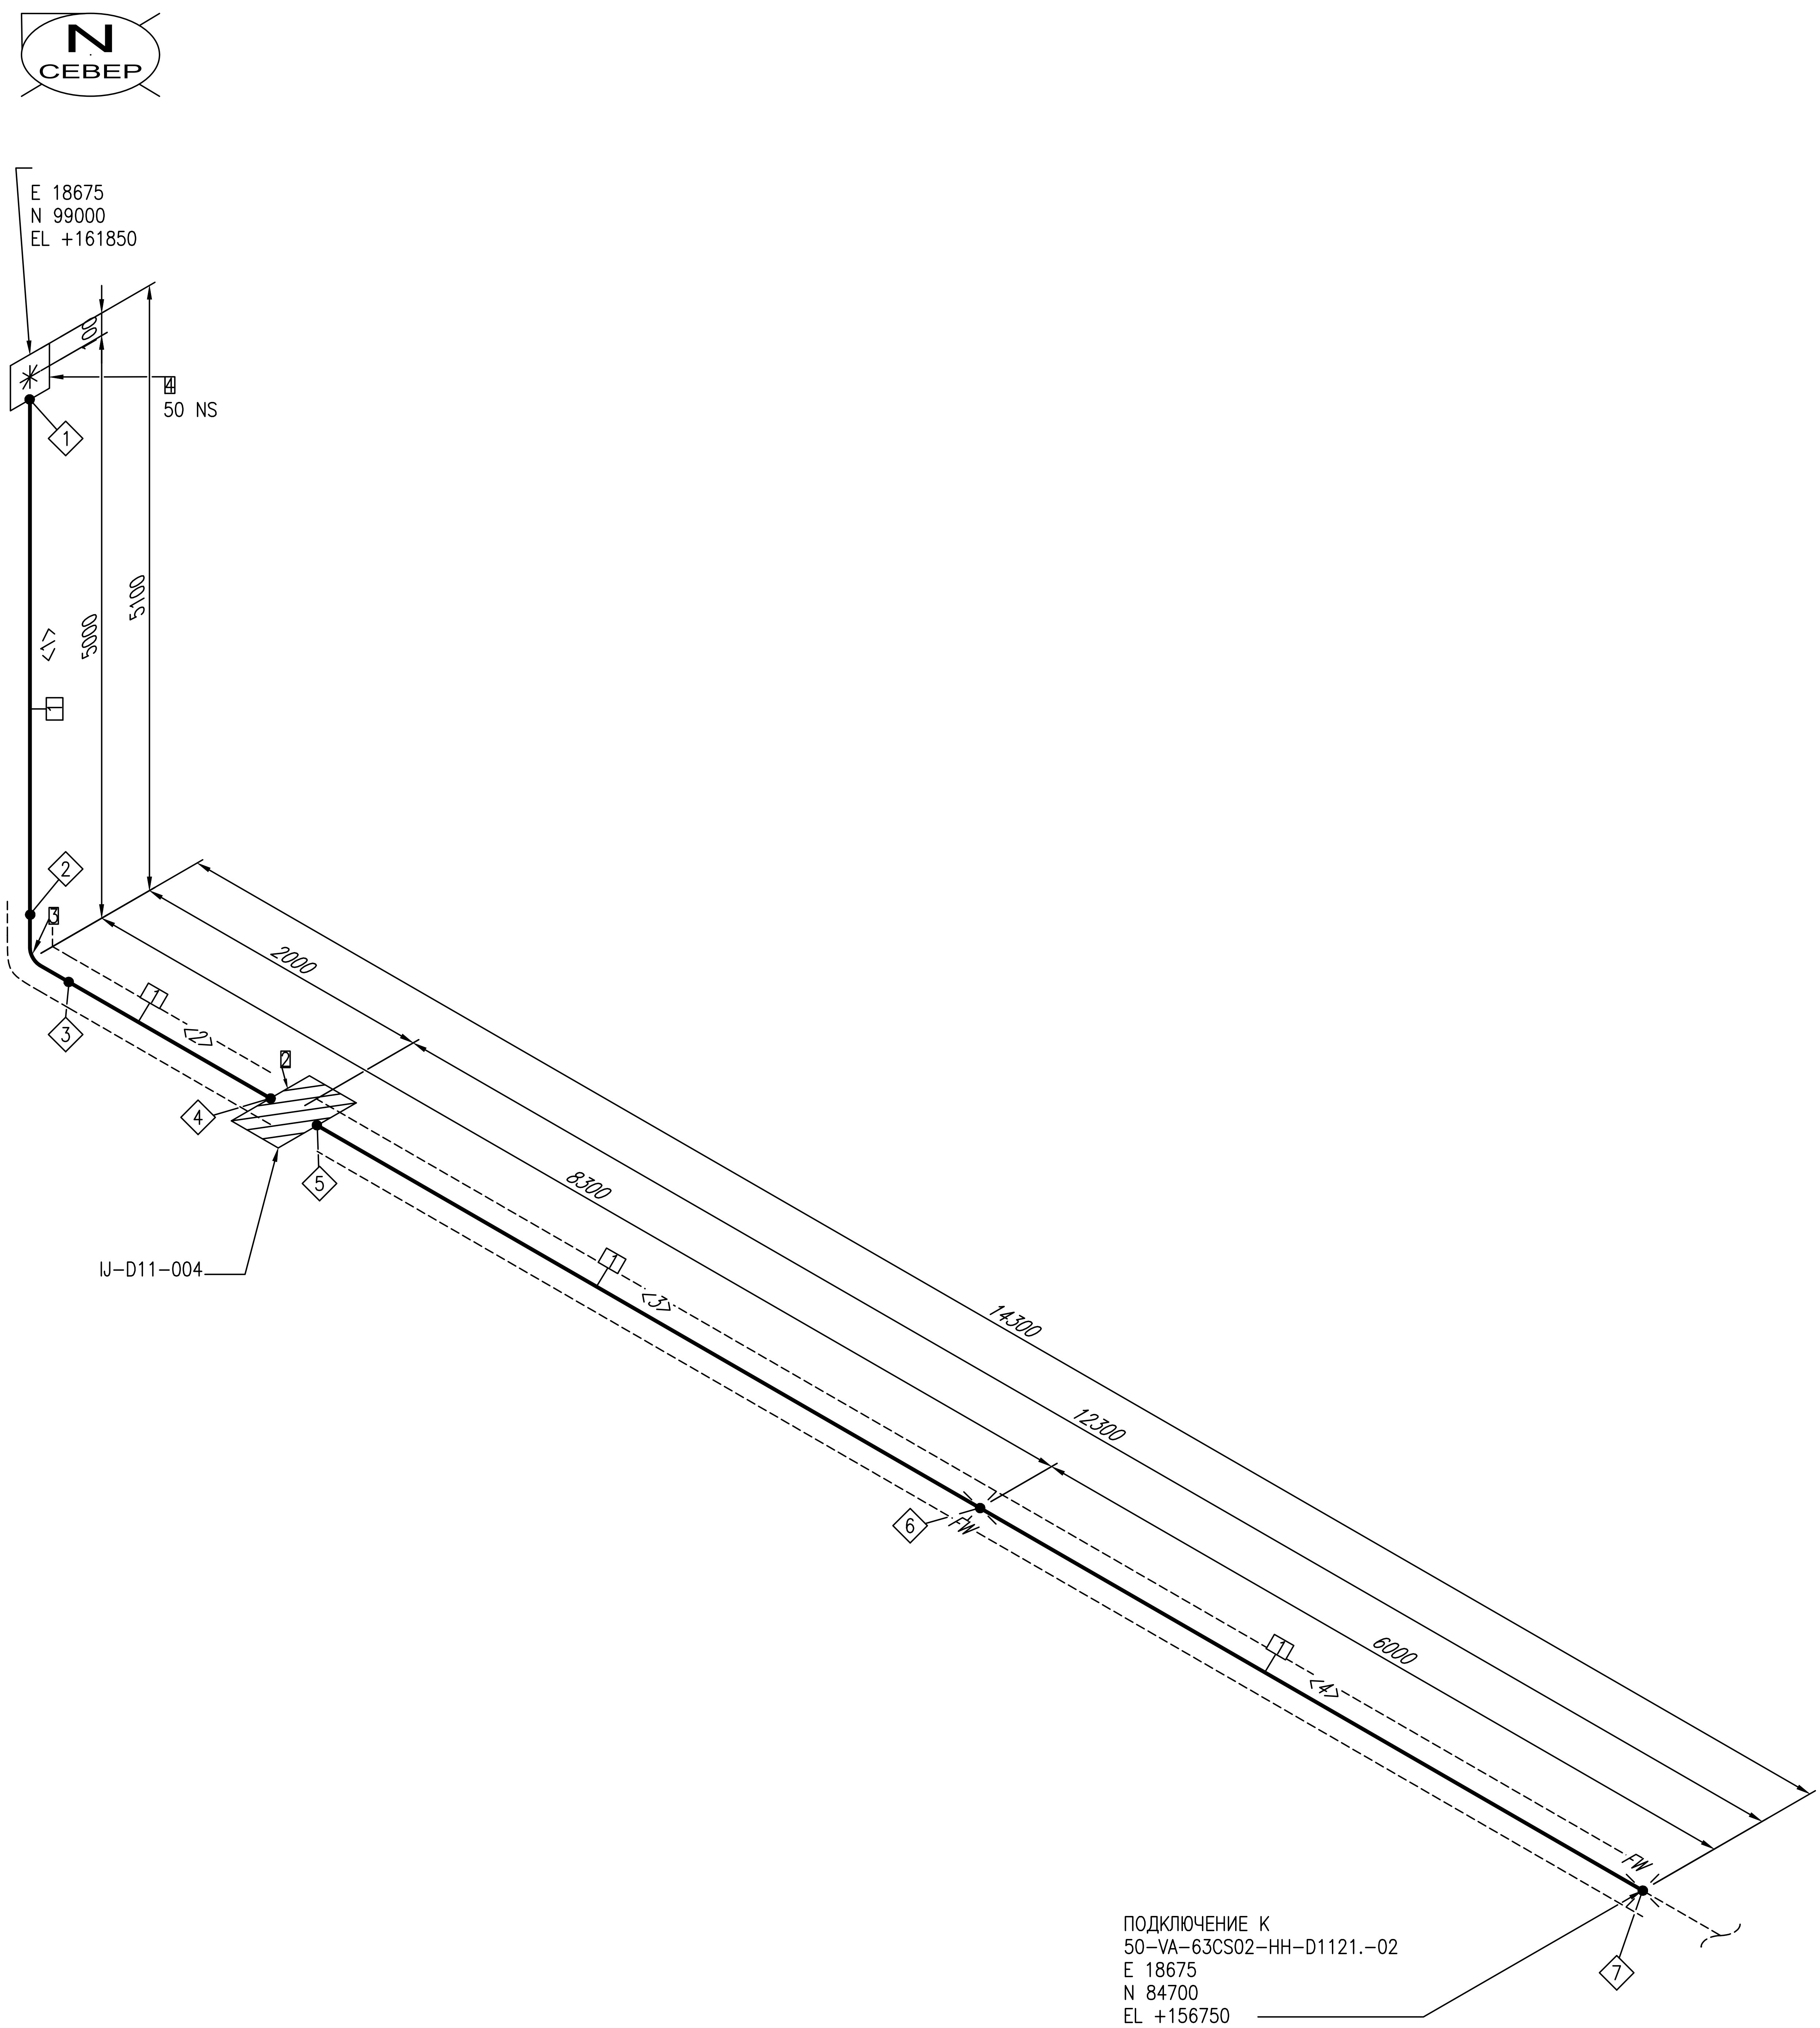

ПЕРЕЧЕНЬ СВАРНЫХ ШВОВ

№	DN	ТИП
1	50	BUTTWELD
2	50	BUTTWELD
3	50	BUTTWELD
4	50	BUTTWELD
5	50	BUTTWELD
6	50	FIELDWELD
7	50	FIELDWELD

ПЕРЕЧЕНЬ ТРУБНЫХ КАТУШЕК

№	DN	ДЛИНА
1	50	4825ММ
2	50	1625ММ
3	50	6000ММ
4	50	6000ММ

СПЕЦИФИКАЦИЯ ИЗДЕЛИЙ И МАТЕРИАЛОВ

ПОЗ.	НАИМЕНОВАНИЕ	СТАНДАРТ	КОЛ.	ПРИМЕЧАНИЕ
1	Трубы стальные бесшовные горячедеформированные Ст20, 57Х4	ГОСТ 8732-78/ ГОСТ 8731-74	18.5М	
2	Изолирующее соединение приварное, 6.3 МПа, 57Х4	EWE0426-MGL1-PRE-054-DSH-610135	1	
3	Отвод ОК I 90-57(4К42)-5,5(6,9)-0,75-1,5DN-30, Ст20	ТУ 1469-017-38948552-2015	1	
4	Оголовок продувочной свечи, приварной, 6.3 МПа, ОПС-57-С-У, 57Х4	ТУ 1469-020-96950580-2011	1	

Трубопровод	ДАННЫЕ ПО ТРУБОПРОВОДУ		
50-VA-63CS02-HH-D1121	Расчетные параметры	Температура	-26,9...+85 °C
		Давление	6,3 MPa
	Рабочие параметры	Температура	-20...+40 °C
		Давление	5,5 MPa
	Параметры испытания	Тип	Гидравлическое
Ссылочные чертежи No		Давление	6,9 MPa
EWE0426-MGL1-PRE-054-SCM-610102	Изоляция	Тип	HH
		Толщина	mm
	Катодная защита	Да или Нет	Да

Рев.	Дата	Назначение ревизии	Проверил	Утвердил
A1	25.09.2026	Утверждено для строительства		
R1	27.08.2026	Выпущено для рассмотрения		

ЗАКАЗЧИК: ГЕНЕРАЛЬНЫЙ ПОДРЯДЧИК: ПОДРЯДЧИК: ГЕНЕРАЛЬНЫЙ ПРОЕКТИРОВЩИК:

EWE0426-MGL1-PRE-054-ISO-690629-A1

«СТРОИТЕЛЬСТВО НОВЫХ НИТОК (УЧАСТКОВ) ГАЗОПРОВОДОВ «ГАЗЛИ - САРИМОЙ» И «АКЧАЛОК - ГАЗЛИ - НУКУС» ОБЩЕЙ ПРОТЯЖЕННОСТЬЮ НЕ МЕНЕЕ 275 КМ».

Изм.	Кол.уч.	Лист	№док.	Подпись	Дата
ГИП		Кирпичников С.			09.2026
Нач.отд.		Рябинин А.			09.2026
Исполн.		Таштимуров Р.			09.2026
Н.контр		Кирпичников С.			09.2026

ГАЗОПРОВОД «ГАЗЛИ-САРИМОЙ» (54 КМ)
Узел приема/запуска очистных устройств DN1200.УЗПОУ-D11.

Стадия	Лист	Листов
РД	1	3

Изометрический чертеж трубопровода
50-VA-63CS02-HH-D1121

ООО "EAST-WEST Engineering"
г. Ташкент 2026г.

Формат А2 594x420

Взам. инв. №
Подпись и дата
Инв.№ подл.

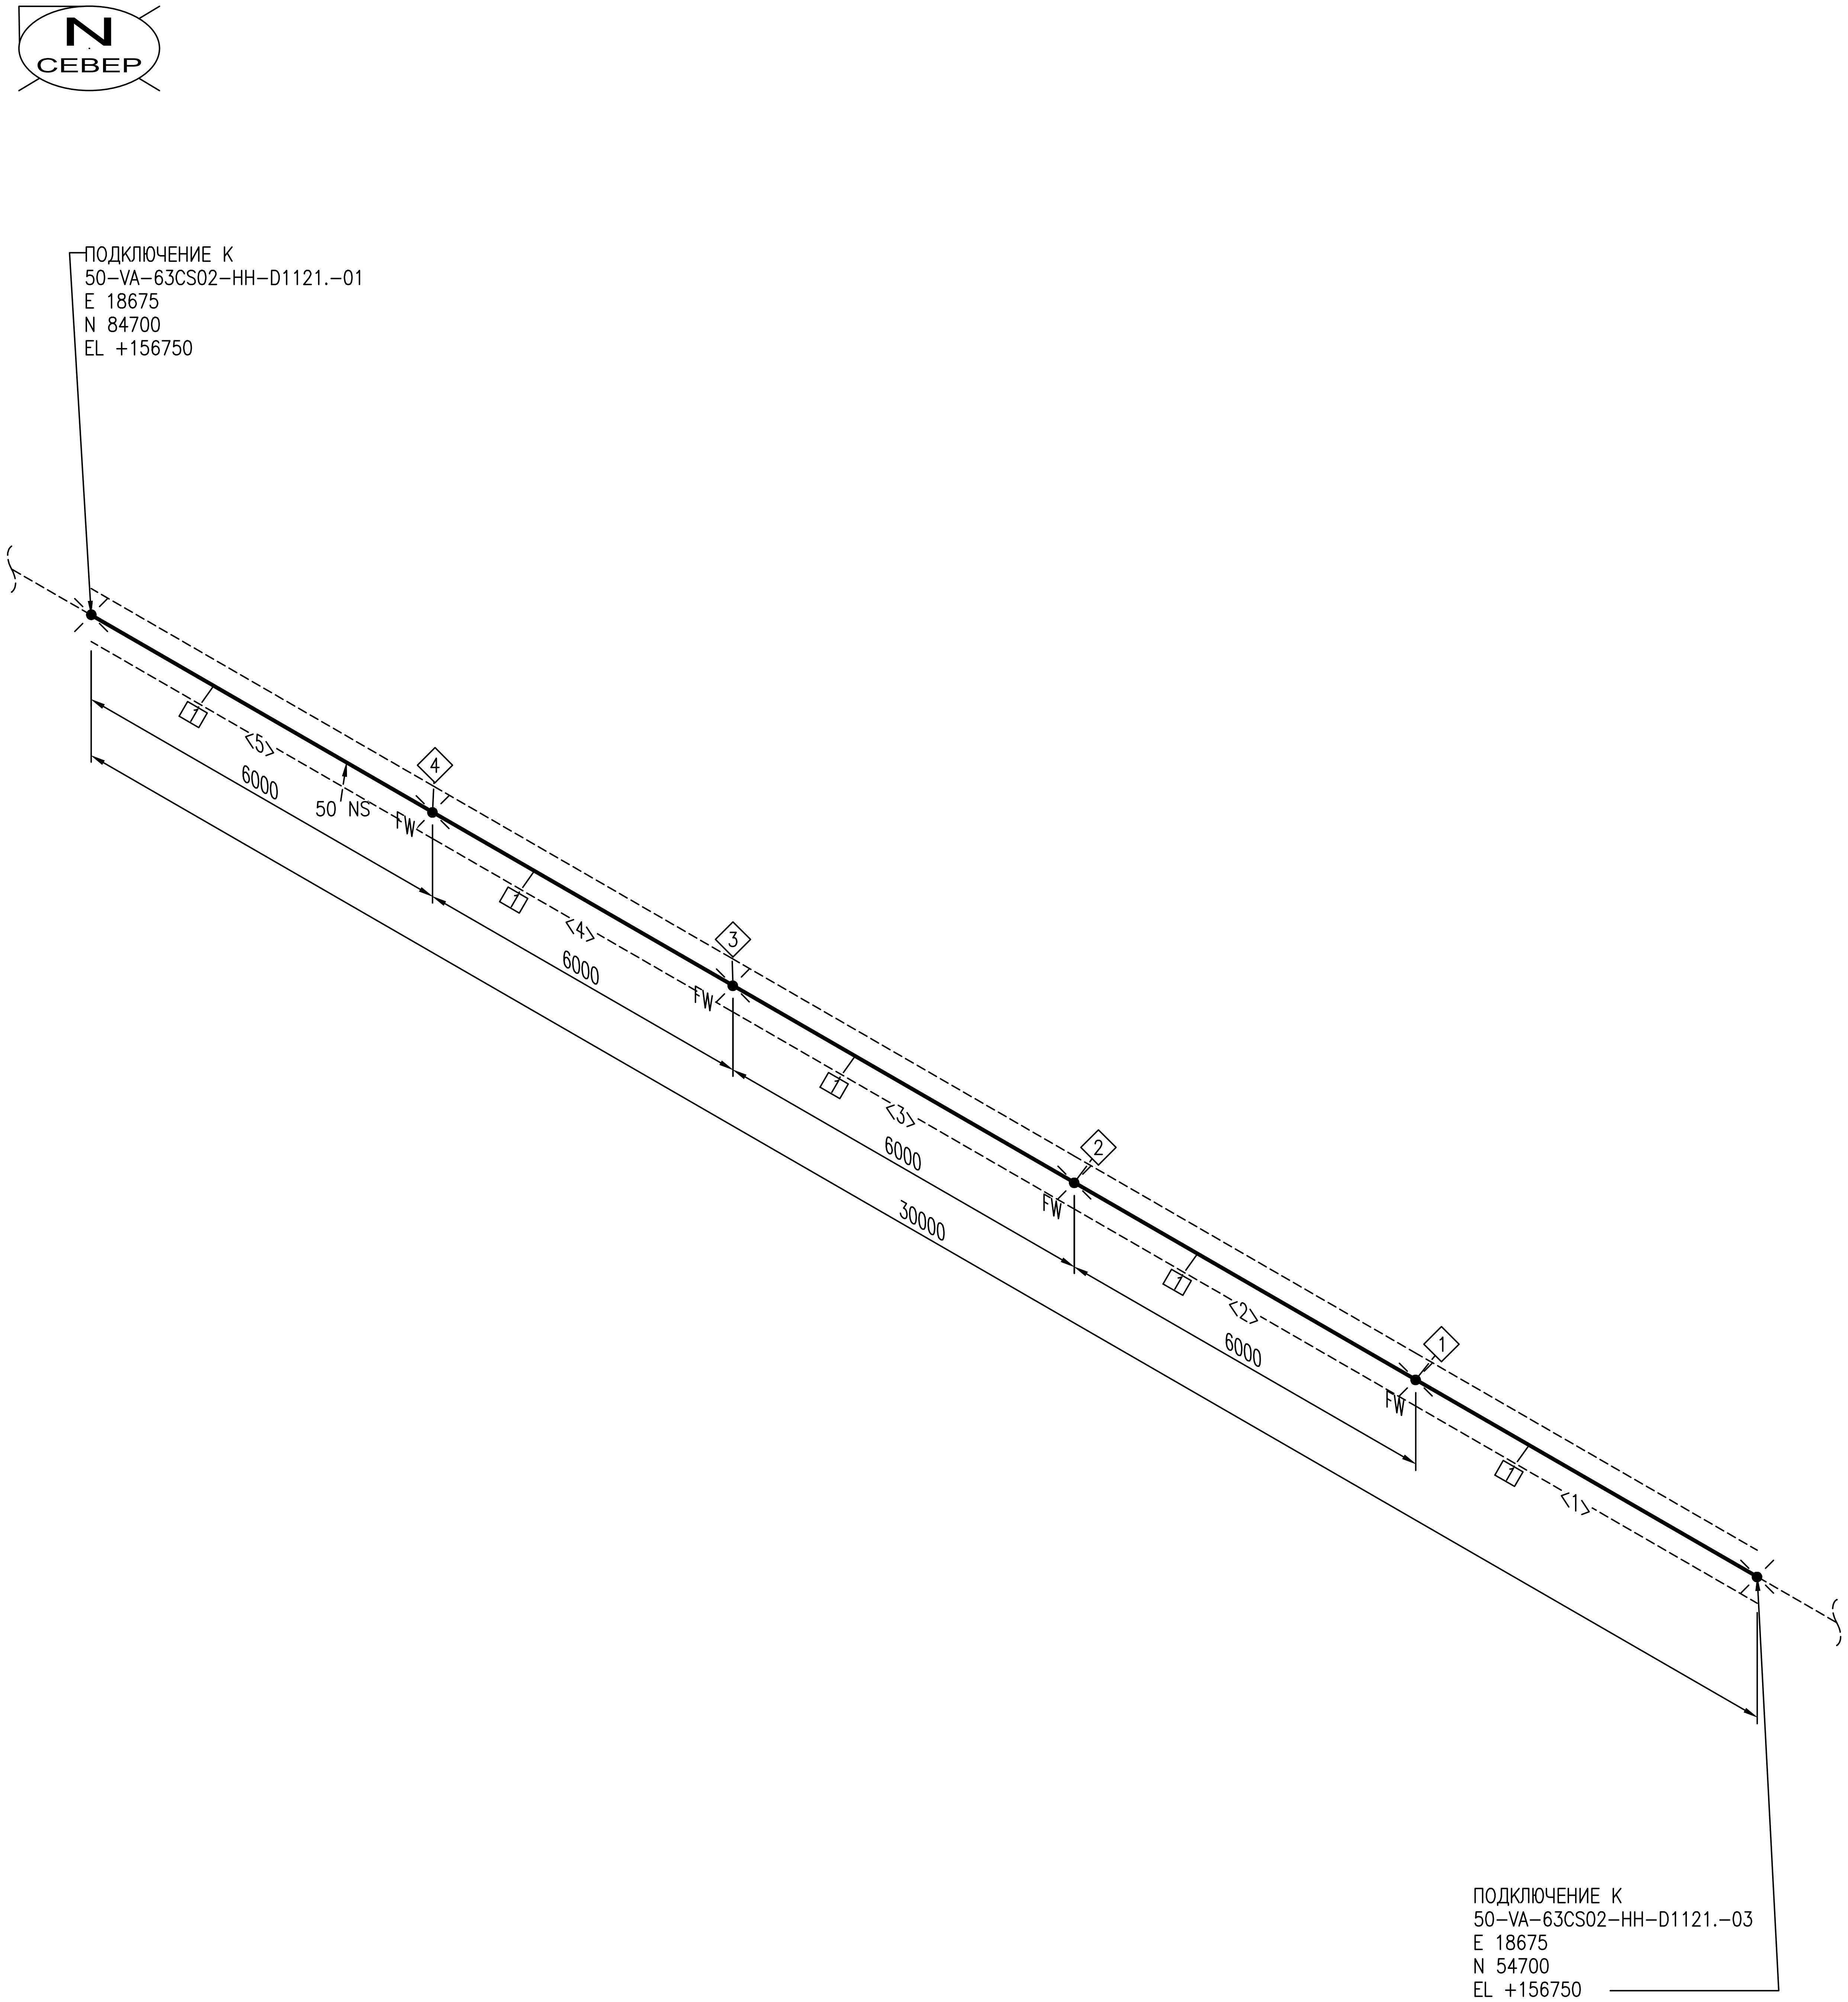

ПЕРЕЧЕНЬ СВАРНЫХ ШВОВ

№	DN	ТИП
1	50	FIELDWELD
2	50	FIELDWELD
3	50	FIELDWELD
4	50	FIELDWELD

ПЕРЕЧЕНЬ ТРУБНЫХ КАТУШЕК

№	DN	ДЛИНА
1	50	6000ММ
2	50	6000ММ
3	50	6000ММ
4	50	6000ММ
5	50	6000ММ

СПЕЦИФИКАЦИЯ ИЗДЕЛИЙ И МАТЕРИАЛОВ

ПОЗ.	НАИМЕНОВАНИЕ	СТАНДАРТ	КОЛ.	ПРИМЕЧАНИЕ
1	Трубы стальные бесшовные горячедеформированные Ст20, 57Х4	ГОСТ 8732-78/ ГОСТ 8731-74	30.0М	

Трубопровод	ДАННЫЕ ПО ТРУБОПРОВОДУ		
50-VA-63CS02-HH-D1121	Расчетные параметры	Температура	-26,9...+85 °С
		Давление	6,3 MPa
	Рабочие параметры	Температура	-20...+40 °С
		Давление	5,5 MPa
	Параметры испытания	Тип	Гидравлическое
Ссылочные чертежи No		Давление	6,9 MPa
EWE0426-MGL1-PRE-054-SCM-610102	Изоляция	Тип	НН
		Толщина	mm
	Катодная защита	Да или Нет	Да

Рев.	Дата	Назначение ревизии	Проверил	Утвердил
A1	25.09.2026	Утверждено для строительства		
R1	27.08.2026	Выпущено для рассмотрения		

ЗАКАЗЧИК: UTG UZTRANSGAZ

ГЕНЕРАЛЬНЫЙ ПОДРЯДЧИК: UET UZBEKENERGOTAMIR

ПОДРЯДЧИК: PBG Pro Build Generation

ГЕНЕРАЛЬНЫЙ ПРОЕКТИРОВЩИК: EAST WEST ENGINEERING

EWE0426-MGL1-PRE-054-ISO-690629-A1

«СТРОИТЕЛЬСТВО НОВЫХ НИТОК (УЧАСТКОВ) ГАЗОПРОВОДОВ «ГАЗЛИ - САРИМОЙ» И «АКЧАЛОК - ГАЗЛИ - НУКУС» ОБЩЕЙ ПРОТЯЖЕННОСТЬЮ НЕ МЕНЕЕ 275 КМ».

ГАЗОПРОВОД «ГАЗЛИ-САРИМОЙ» (54 КМ)
Узел приема/запуска очистных устройств DN1200.УЗПОУ-D11.

Изм.	Кол.уч.	Лист	№док.	Подпись	Дата
ГИП		Кирпичников С.			09.2026
Нач.отд.		Рябинин А.			09.2026
Исполн.		Таштимуров Р.			09.2026
Н.контр		Кирпичников С.			09.2026

Стадия	Лист	Листов
РД	2	3

Изометрический чертеж трубопровода
50-VA-63CS02-HH-D1121

EAST WEST ENGINEERING
ООО "EAST-WEST Engineering"
г. Ташкент 2026г.

Взам. инв. №
Подпись и дата
Инв.№ подл.

Формат А2 594х420

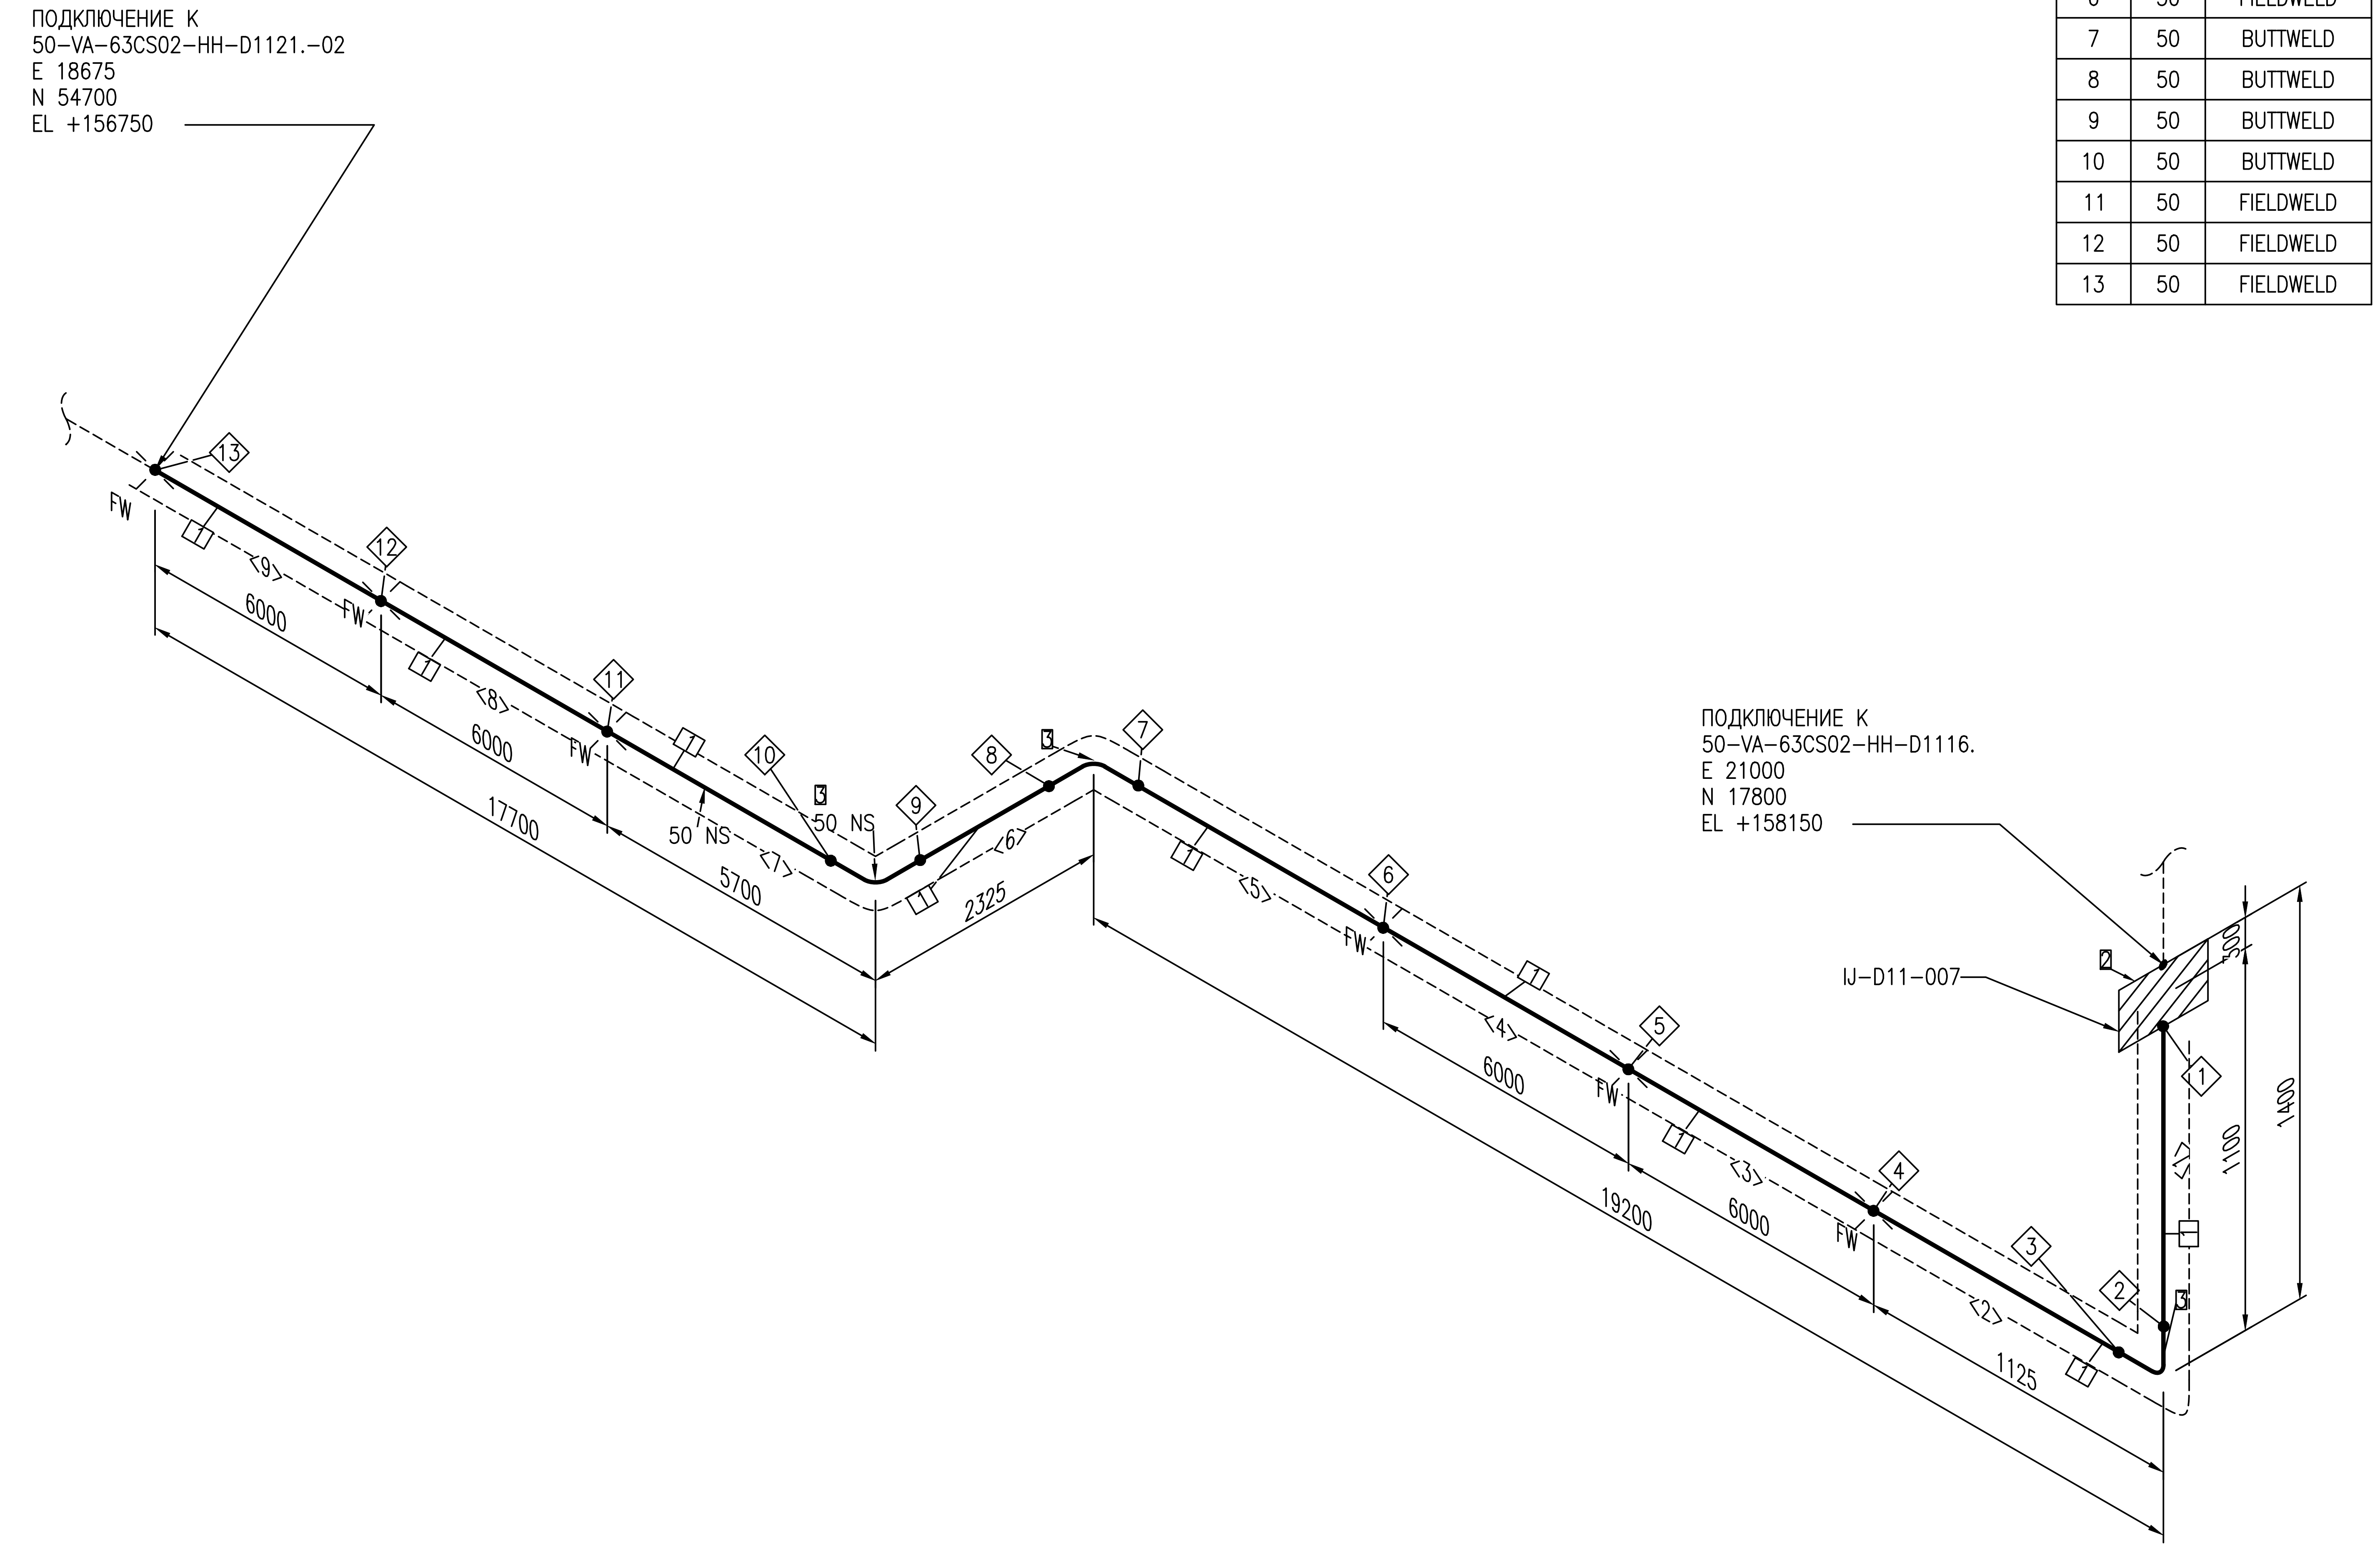

ПЕРЕЧЕНЬ СВАРНЫХ ШВОВ

№	DN	ТИП
1	50	BUTTWELD
2	50	BUTTWELD
3	50	BUTTWELD
4	50	FIELDWELD
5	50	FIELDWELD
6	50	FIELDWELD
7	50	BUTTWELD
8	50	BUTTWELD
9	50	BUTTWELD
10	50	BUTTWELD
11	50	FIELDWELD
12	50	FIELDWELD
13	50	FIELDWELD

ПЕРЕЧЕНЬ ТРУБНЫХ КАТУШЕК

№	DN	ДЛИНА
1	50	726MM
2	50	1050MM
3	50	6000MM
4	50	6000MM
5	50	6000MM
6	50	2176MM
7	50	5625MM
8	50	6000MM
9	50	6000MM

СПЕЦИФИКАЦИЯ ИЗДЕЛИЙ И МАТЕРИАЛОВ

ПОЗ.	НАИМЕНОВАНИЕ	СТАНДАРТ	КОЛ.	ПРИМЕЧАНИЕ
1	Трубы стальные бесшовные горячедеформированные Ст20, 57Х4	ГОСТ 8732-78/ ГОСТ 8731-74	39.6M	
2	Изолирующее соединение приварное, 6.3 МПа, 57Х4	EWE0426-MGL1-PRE-054-DSH-610135	1	
3	Отвод ОК I 90-57(4К42)-5,5(6,9)-0,75-1,5DN-30, Ст20	ТУ 1469-017-38948552-2015	3	

Трубопровод	ДАННЫЕ ПО ТРУБОПРОВОДУ		
50-VA-63CS02-HH-D1121	Расчетные параметры	Температура	-26,9...+85 °C
		Давление	6,3 MPa
	Рабочие параметры	Температура	-20...+40 °C
		Давление	5,5 MPa
	Параметры испытания	Тип	Гидравлическое
Ссылочные чертежи No		Давление	6,9 MPa
EWE0426-MGL1-PRE-054-SCM-610102	Изоляция	Тип	HH
		Толщина	mm
	Катодная защита	Да или Нет	Да

Рев.	Дата	Назначение ревизии	Проверил	Утвердил
A1	25.09.2026	Утверждено для строительства		
R1	27.08.2026	Выпущено для рассмотрения		

ЗАКАЗЧИК: UTG UZTRANSGAZ

ГЕНЕРАЛЬНЫЙ ПОДРЯДЧИК: UET UZBEKENERGOTAMIR

ПОДРЯДЧИК: PBG Pre Build Generation

ГЕНЕРАЛЬНЫЙ ПРОЕКТИРОВЩИК: EAST WEST ENGINEERING

EWE0426-MGL1-PRE-054-ISO-690629-A1

«СТРОИТЕЛЬСТВО НОВЫХ НИТОК (УЧАСТКОВ) ГАЗОПРОВОДОВ «ГАЗЛИ - САРИМОЙ» И «АКЧАЛОК - ГАЗЛИ - НУКУС» ОБЩЕЙ ПРОТЯЖЕННОСТЬЮ НЕ МЕНЕЕ 275 КМ».

Изм.	Кол.уч.	Лист	№док.	Подпись	Дата
ГИП		Кирпичников С.			09.2026
Нач.отд.		Рябинин А.			09.2026
Исполн.		Таштимуров Р.			09.2026
Н.контр		Кирпичников С.			09.2026

ГАЗОПРОВОД «ГАЗЛИ-САРИМОЙ» (54 КМ)
Узел приема/запуска очистных устройств DN1200.УЗПОУ-D11.

Стадия	Лист	Листов
РД	3	3

Изометрический чертеж трубопровода
50-VA-63CS02-HH-D1121

ООО "EAST-WEST Engineering"
г. Ташкент 2026г.

Взам. инв. №

Подпись и дата

Инв.№ подл.

Формат А2 594x420