## План (1:100)

## ПРИМЕЧАНИЯ

1. Общие данные см. EWE0426-MGL1-PRE-054-COM-690201;
2. * - Размеры для справок;
3. ** - Размеры уточнить по месту;
4. Размеры фитингов - по ГОСТ;
5. Все размеры указаны в миллиметрах;
6. Все отметки указаны в метрах, если не указано иное;
7. Высотные отметки уточнить по месту;
8. Система высот - Балтийская;
9. Данный чертеж разработан на основе EWE0426-MGL1-PIL-054-COM-660201;
10. Привязка к пикетажу указана в EWE0426-MGL1-PRE-054-DRW-690202;
11. Фундаменты под опоры, ЗРА, продувочные свечи см. EWE0426-MGL1-STR-054-COM-690501;
12. Детальную информацию по трубопроводам см. изометрические чертежи;
13. На схеме указано основное направление потока газа, согласно схеме PFD, см. EWE0426-MGL1-PRE-054-PFD-610101. В процессе эксплуатации поток может быть направлен в обратном направлении.

Условные обозначения:

▨ - Площадка (зона) облуживания показано условно

◺ 0.005 - Уклон трубопровода

+158.60 - Проектная отметка

Код изоляции трубопровода:
N - без изоляции
HH - гидроизоляция от почвенной корозии

| Рев | Дата | Назначение ревизии | Проверил | Утвердил |
|---|---|---|---|---|
| A1 | 25.09.2026 | Утверждено для строительства | | |
| R1 | 27.08.2026 | Выпущено для рассмотрения | | |

ЗАКАЗЧИК: UTG UZTRANSGAZ

ГЕНЕРАЛЬНЫЙ ПОДРЯДЧИК: UET UZBEKENERGOTAMIR

ПОДРЯДЧИК: PBG Pro Build Generation

ГЕНЕРАЛЬНЫЙ ПРОЕКТИРОВЩИК: EAST WEST ENGINEERING

EWE0426-MGL1-PRE-054-DRW-690203-A1

«СТРОИТЕЛЬСТВО НОВЫХ НИТОК (УЧАСТКОВ) ГАЗОПРОВОДОВ «ГАЗЛИ - САРИМОЙ» И «АКЧАЛОК - ГАЗЛИ - НУКУС» ОБЩЕЙ ПРОТЯЖЕННОСТЬЮ НЕ МЕНЕЕ 275 КМ».

| Изм. | Кол.уч. | Лист | №док. | Подпись | Дата |
|---|---|---|---|---|---|
| ГИП | | Кирпичников С. | | | 09.2026 |
| Нач.отд. | | Рябинин А. | | | 09.2026 |
| Исполн. | | Таштимуров Р. | | | 09.2026 |
| | | | | | |
| | | | | | |
| Н.контр | | Кирпичников С. | | | 09.2026 |

Узел приема/запуска очистных устройст DN1200. УЗПОУ-D11.

| Стадия | Лист | Листов |
|---|---|---|
| РП | 1 | 3 |

План. Разрезы. Узлы. Виды. М1:100

ООО "EAST-WEST Engineering"
г. Ташкент 2026г.

Формат / Format A2X3

Взам. инв. №
Подпись и дата
Инв.№ подл.

## Разрез 1-1 (1:100)

| | |
|---|---|
| 1 | 300-GT-63CS02-HH-D1106 |
| 2 | 50-VA-63CS02-HH-D1121 |
| 3 | 50-VA-63CS02-N-D1117 |
| 4 | 100-VA-63CS02-HH-D1113 |
| 5 | 100-VA-63CS02-N-D1113 |
| 6 | 100-VA-63CS02-HH-D1113 |
| 7 | 100-GT-63CS02-N-D1114 |
| 8 | 150-DC-63CS02-N-D1111 |
| 9 | 150-DC-63CS02-HH-D1111 |
| 10 | 50-VA-63CS02-N-D1117 |

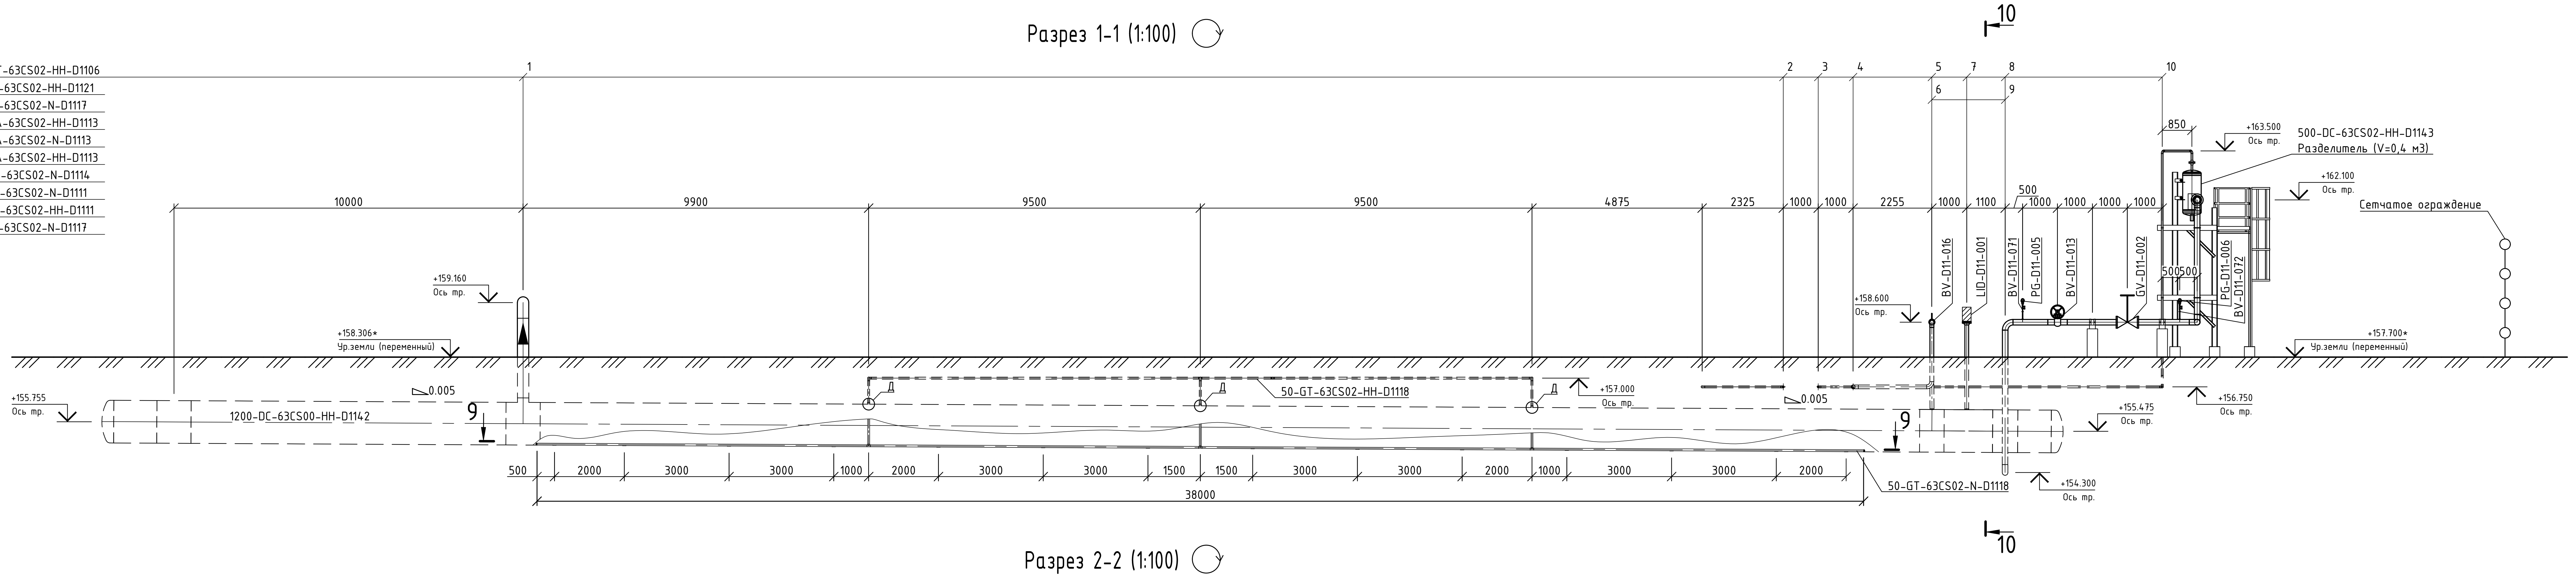

## Разрез 2-2 (1:100)

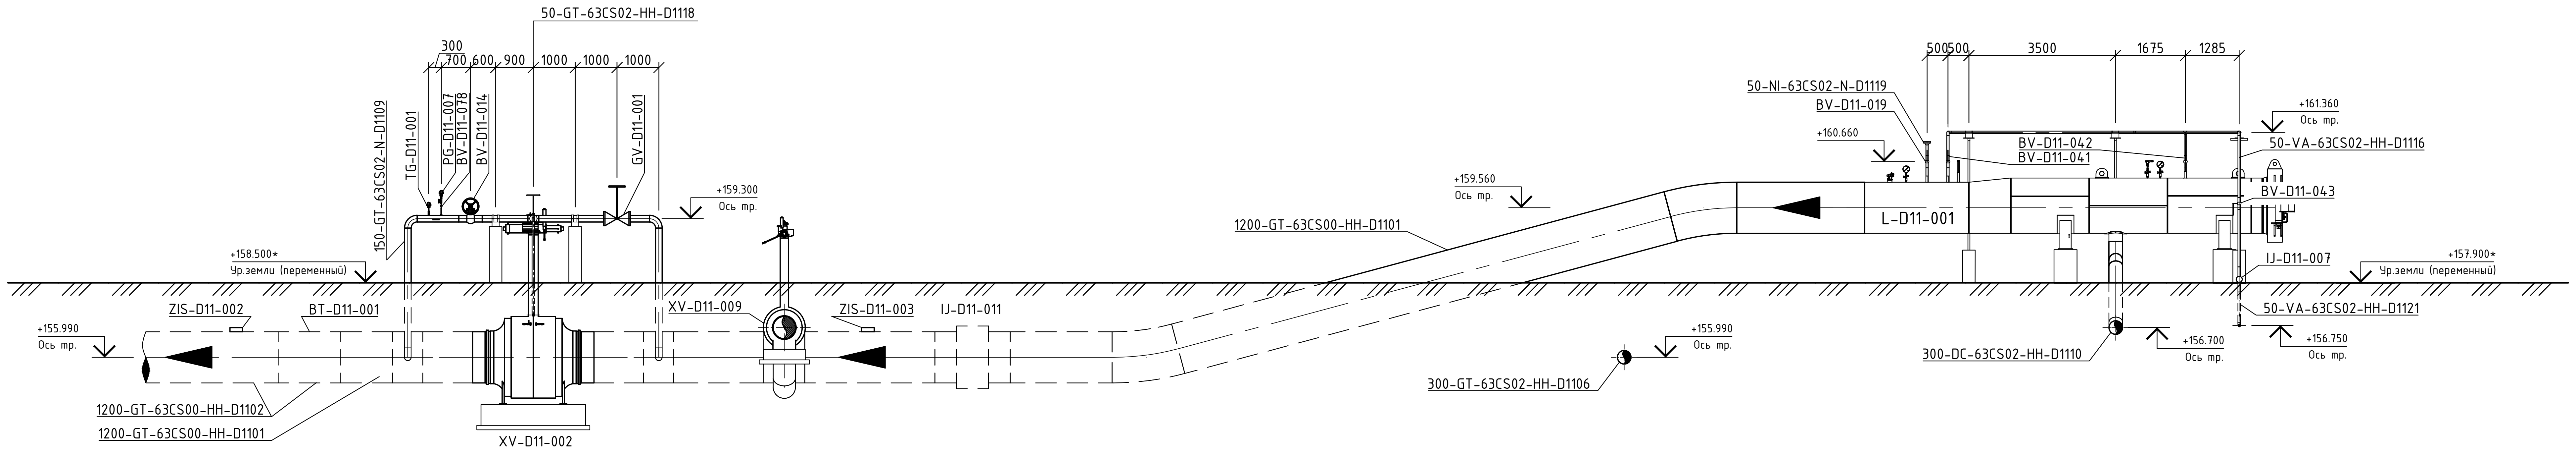

## Разрез 3-3 (1:100)

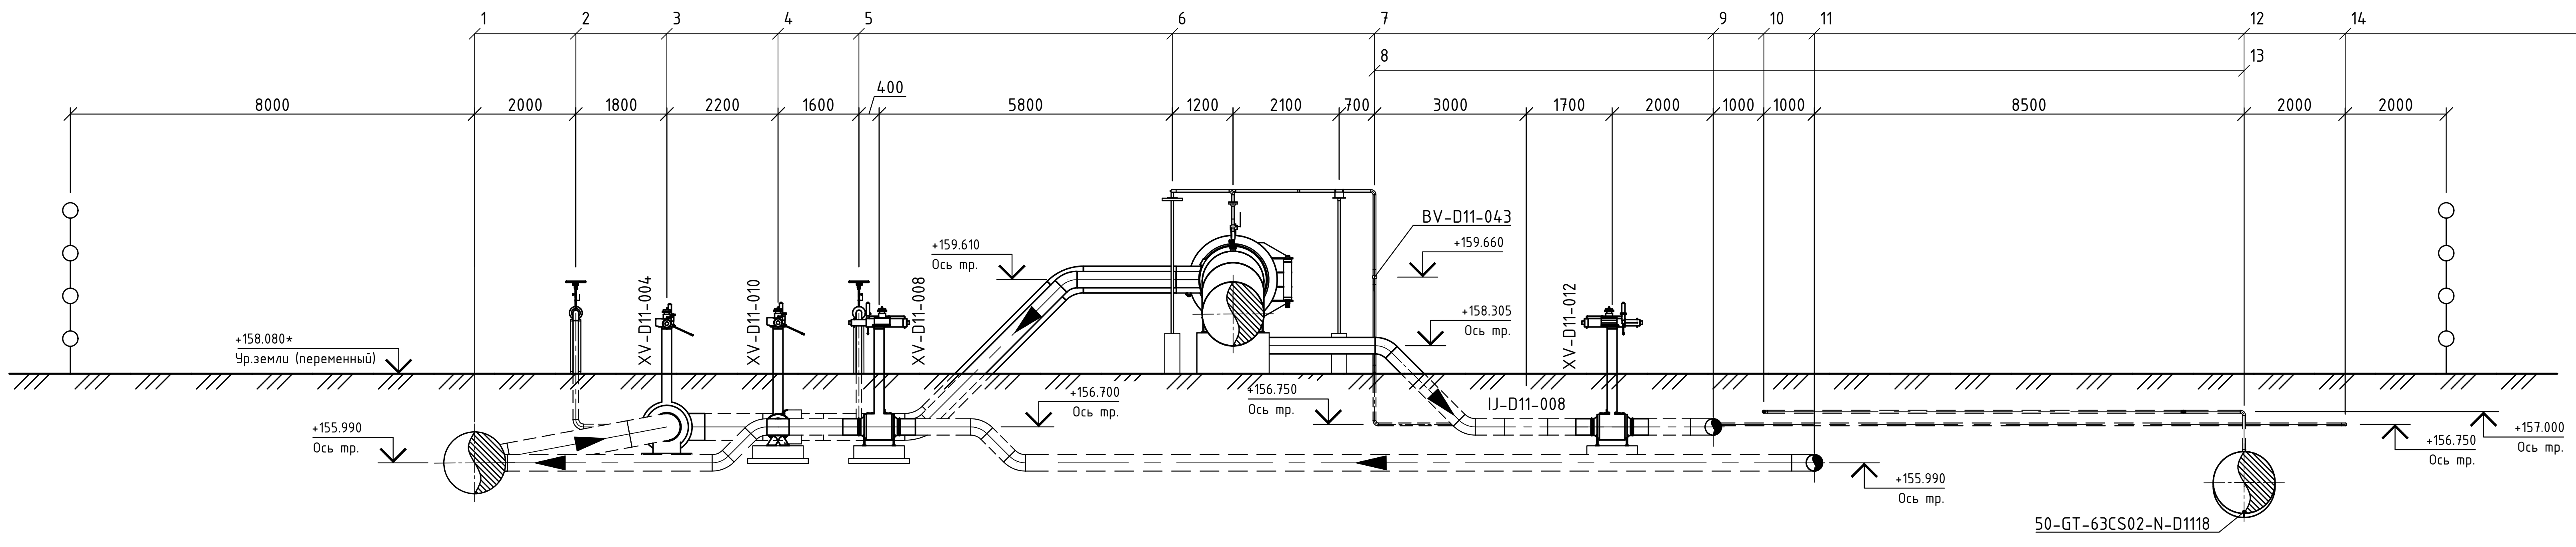

| | |
|---|---|
| 1 | 1200-GT-63CS00-HH-D1102 |
| 2 | 100-GT-63CS02-N-D1112 |
| 3 | 500-GT-63CS02-HH-D1103 |
| 4 | 300-GT-63CS02-HH-D1108 |
| 5 | 100-GT-63CS02-N-D1115 |
| 6 | 50-VA-63CS02-HH-D1116 |
| 7 | 50-VA-63CS02-HH-D1116 |
| 8 | 50-VA-63CS02-HH-D1121 |
| 9 | 300-DC-63CS02-HH-D1110 |
| 10 | 50-GT-63CS02-HH-D1118 |
| 11 | 300-GT-63CS02-HH-D1106 |
| 12 | 50-GT-63CS02-HH-D1118 |
| 13 | 1200-DC-63CS00-HH-D1142 |
| 14 | 50-VA-63CS02-HH-D1121 |

## Разрез 5-5 (1:100)

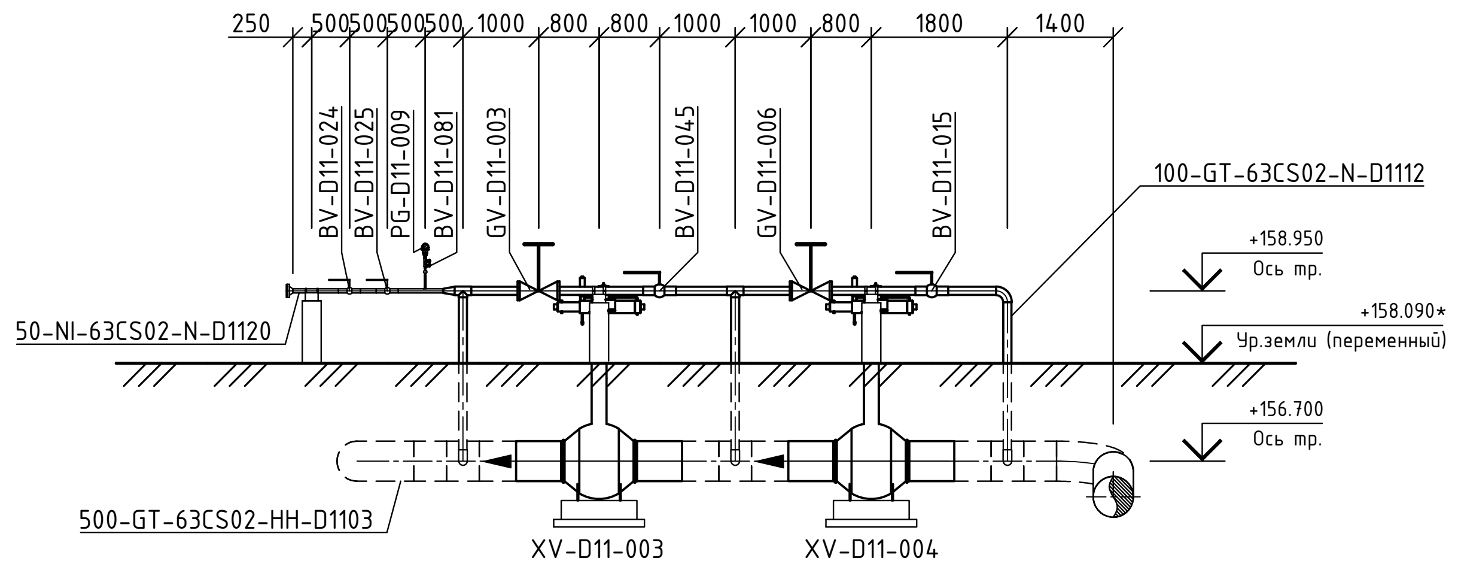

## Разрез 6-6 (1:100)

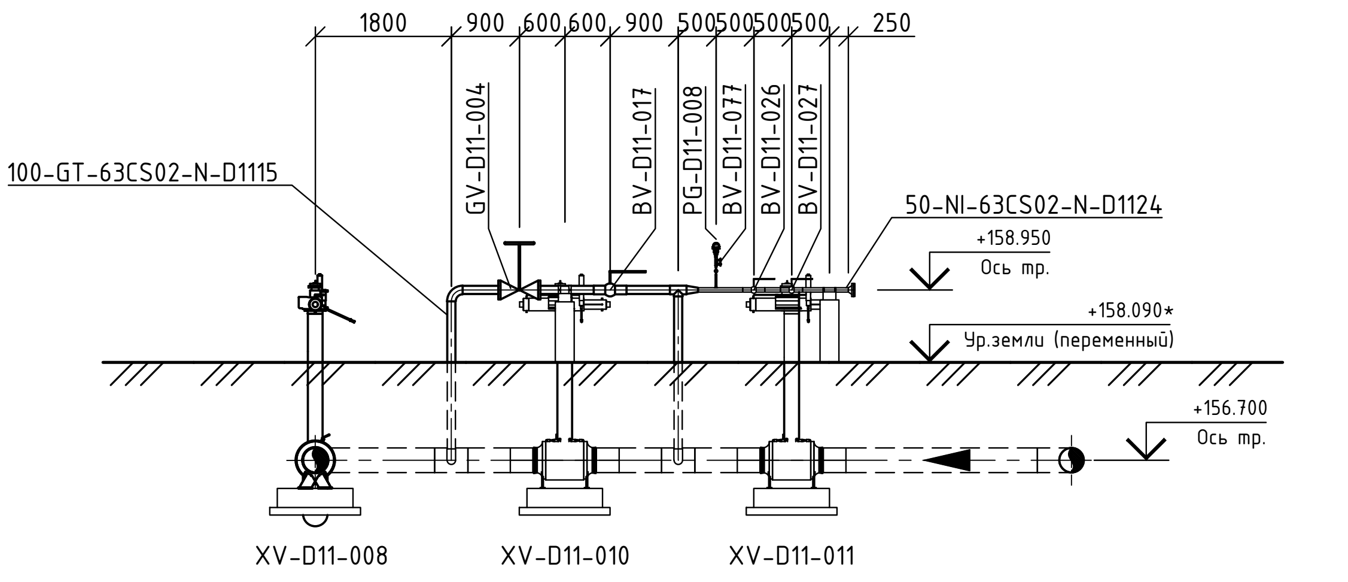

## Разрез 4-4 (1:100)

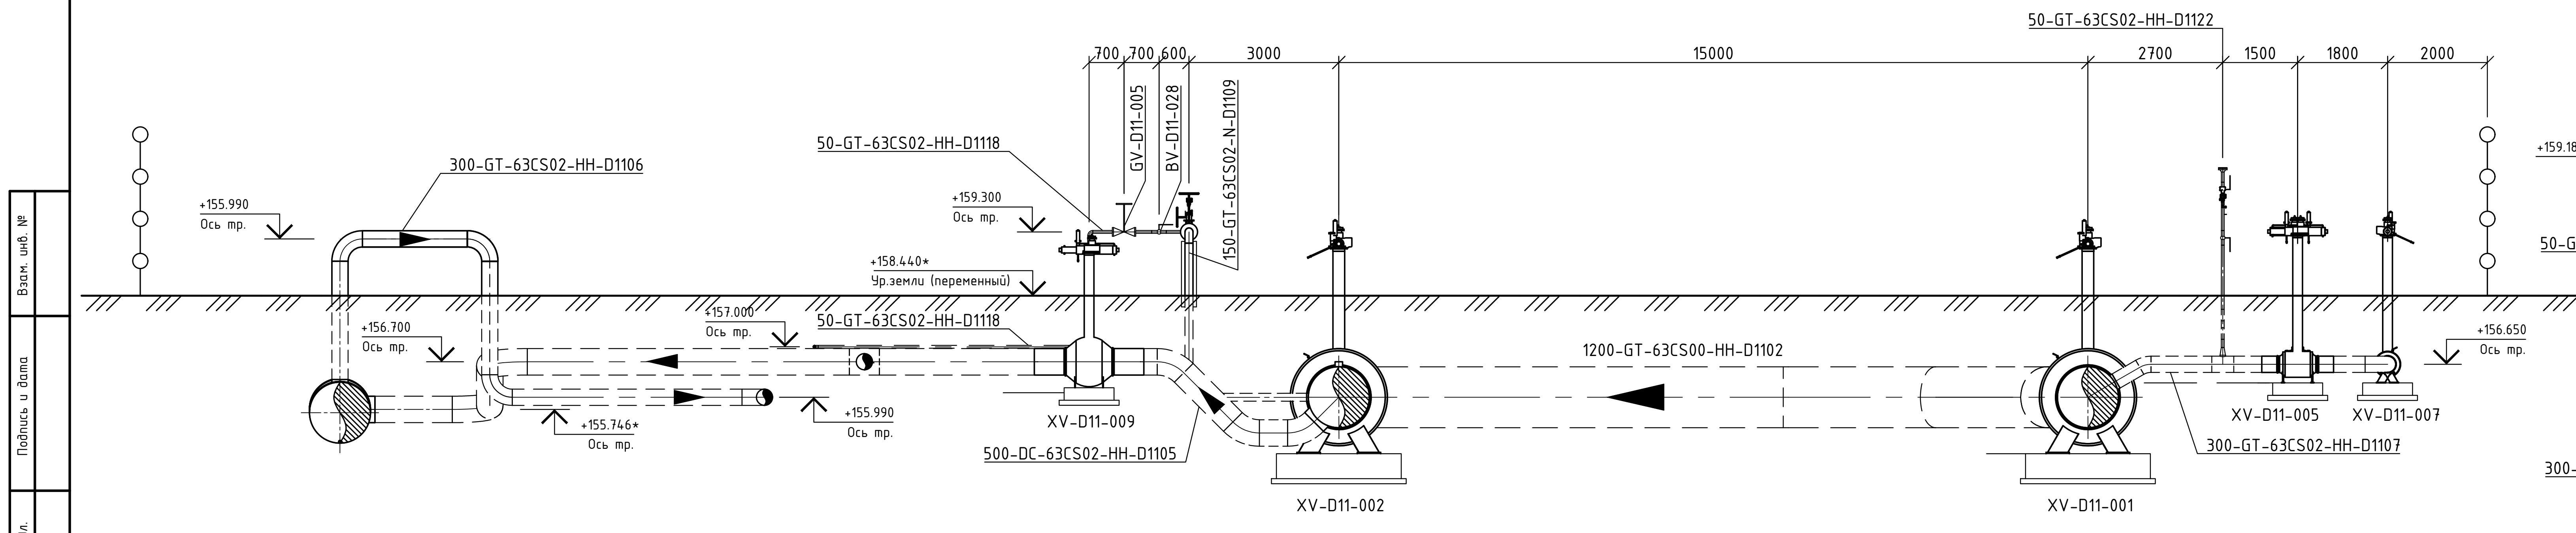

## Разрез 7-7 (1:50)

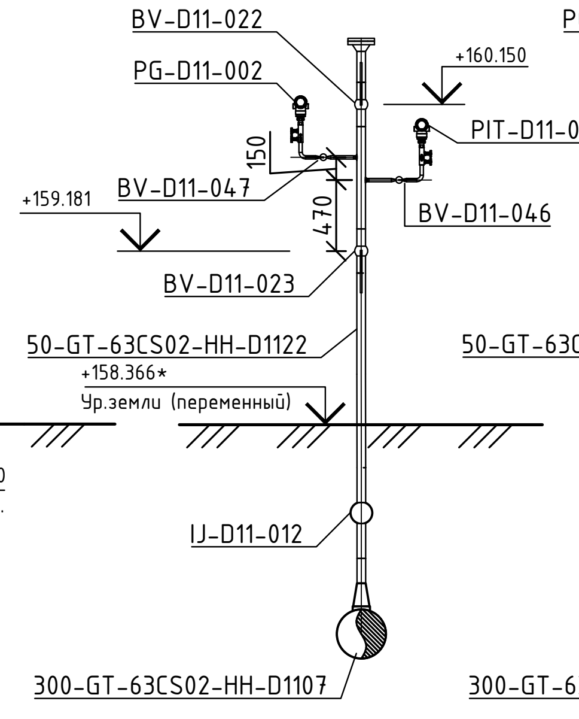

## Разрез 8-8 (1:50)

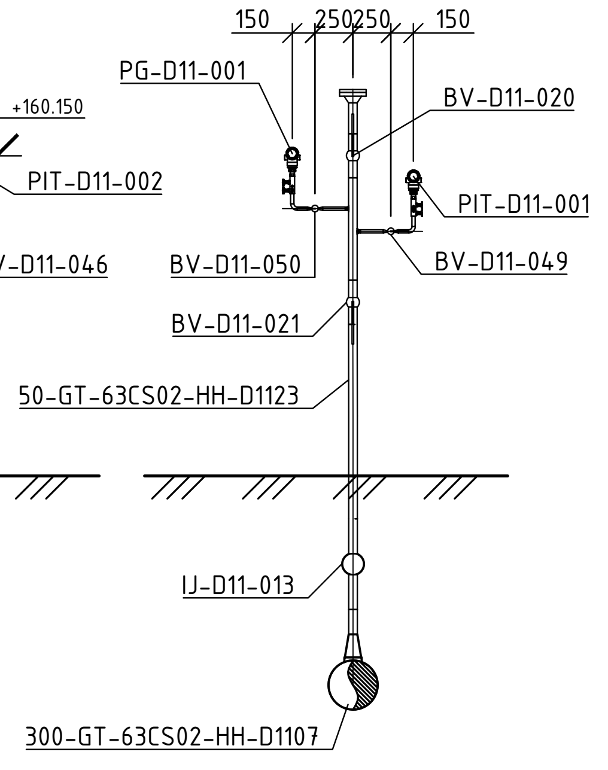

| Рев | Дата | Назначение ревизии | Проверил | Утвердил |
|---|---|---|---|---|
| | | | | |
| | | | | |
| | | | | |
| | | | | |
| A1 | 25.09.2026 | Утверждено для строительства | | |
| R1 | 27.08.2026 | Выпущено для рассмотрения | | |

ЗАКАЗЧИК: UTG UZTRANSGAZ
ГЕНЕРАЛЬНЫЙ ПОДРЯДЧИК: UET UZBEKENERGOTAMIR
ПОДРЯДЧИК: PBG Pro Build Generation
ГЕНЕРАЛЬНЫЙ ПРОЕКТИРОВЩИК: EAST WEST ENGINEERING

EWE0426-MGL1-PRE-054-DRW-690203-A1

«СТРОИТЕЛЬСТВО НОВЫХ НИТОК (УЧАСТКОВ) ГАЗОПРОВОДОВ «ГАЗЛИ – САРИМОЙ» И «АКЧАЛОК – ГАЗЛИ – НУКУС» ОБЩЕЙ ПРОТЯЖЕННОСТЬЮ НЕ МЕНЕЕ 275 КМ».

| Изм. | Кол.уч. | Лист | №док. | Подпись | Дата |
|---|---|---|---|---|---|
| ГИП | | Кирпичников С. | | | 09.2026 |
| Нач.отд. | | Рябинин А. | | | 09.2026 |
| Исполн. | | Таштимуров Р. | | | 09.2026 |
| | | | | | |
| | | | | | |
| Н.контр | | Кирпичников С. | | | 09.2026 |

Узел приема/запуска очистных устройств DN1200. УЗПОУ-D11.

| Стадия | Лист | Листов |
|---|---|---|
| РП | 2 | 3 |

План. Разрезы. Узлы. Виды. М1:100

EAST WEST ENGINEERING
ООО "EAST-WEST Engineering"
г. Ташкент 2026г.

Взам. инв. №
Подпись и дата
Инв.№ подл.

Формат / Format A1

## Разрез 9-9 (1:20)

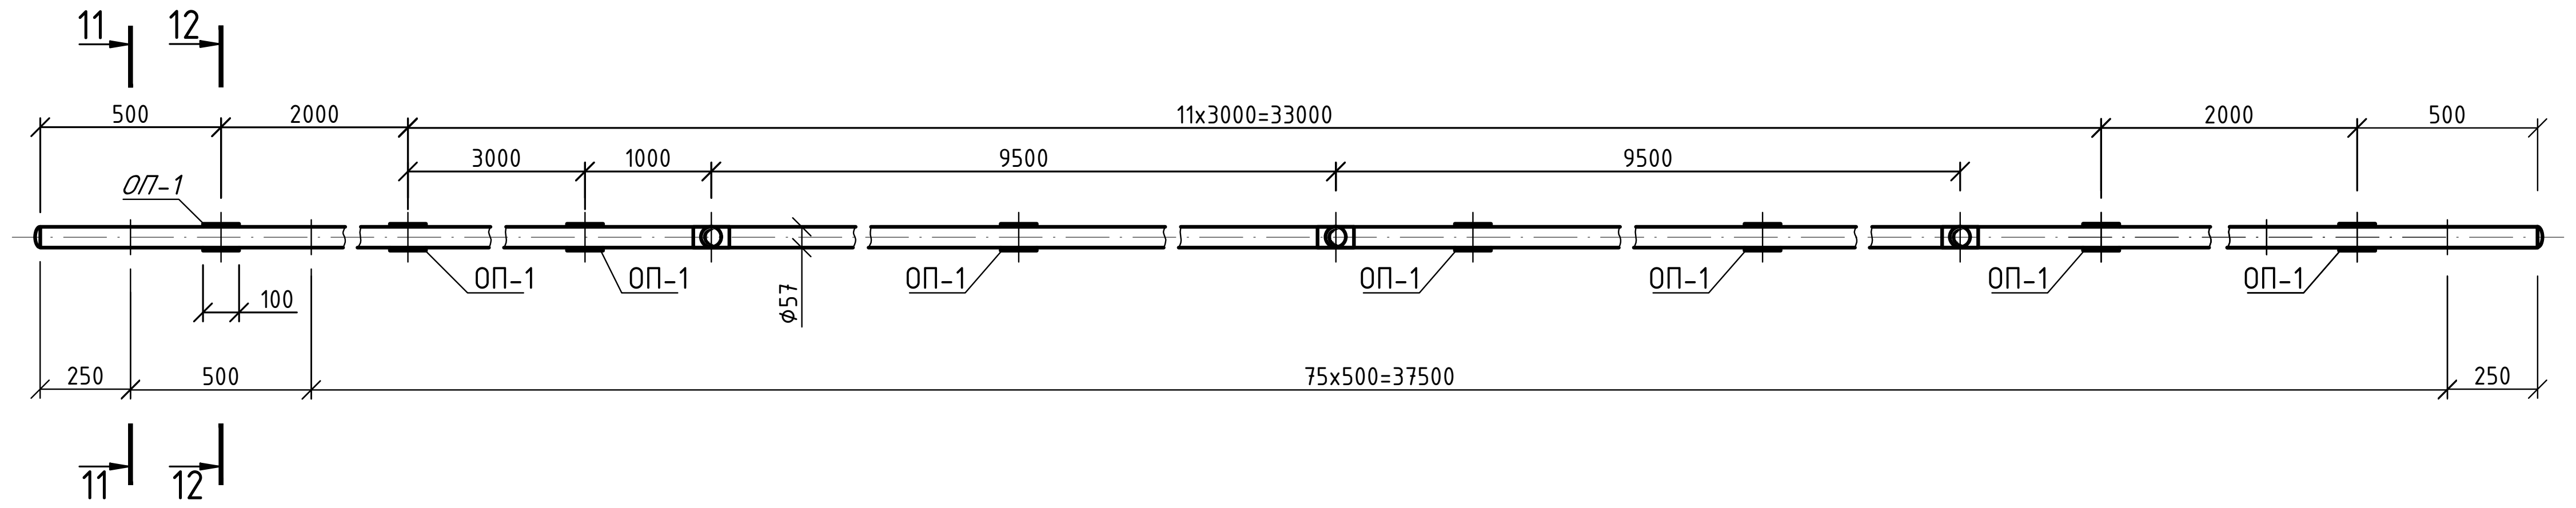

## Разрез 11-11 (1:2)

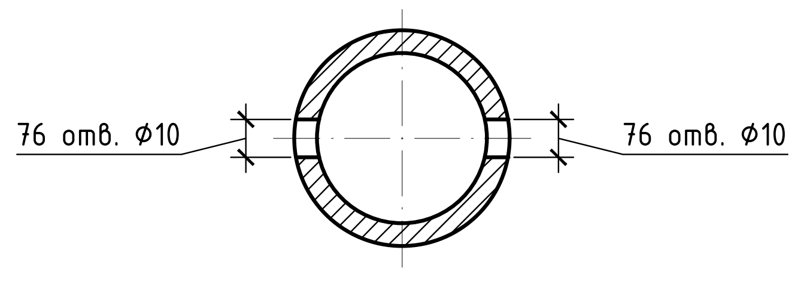

## Разрез 12-12 (1:2)

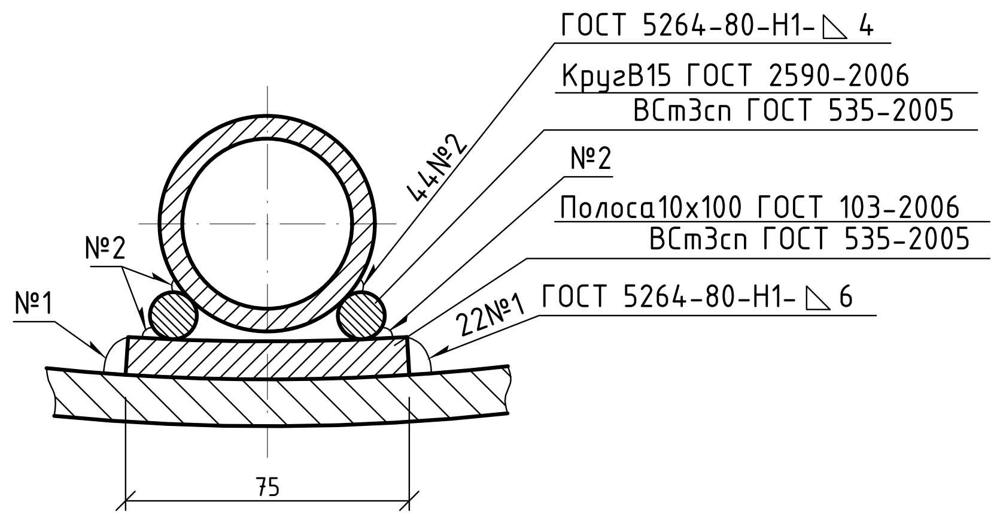

## Разрез 10-10 (1:20)

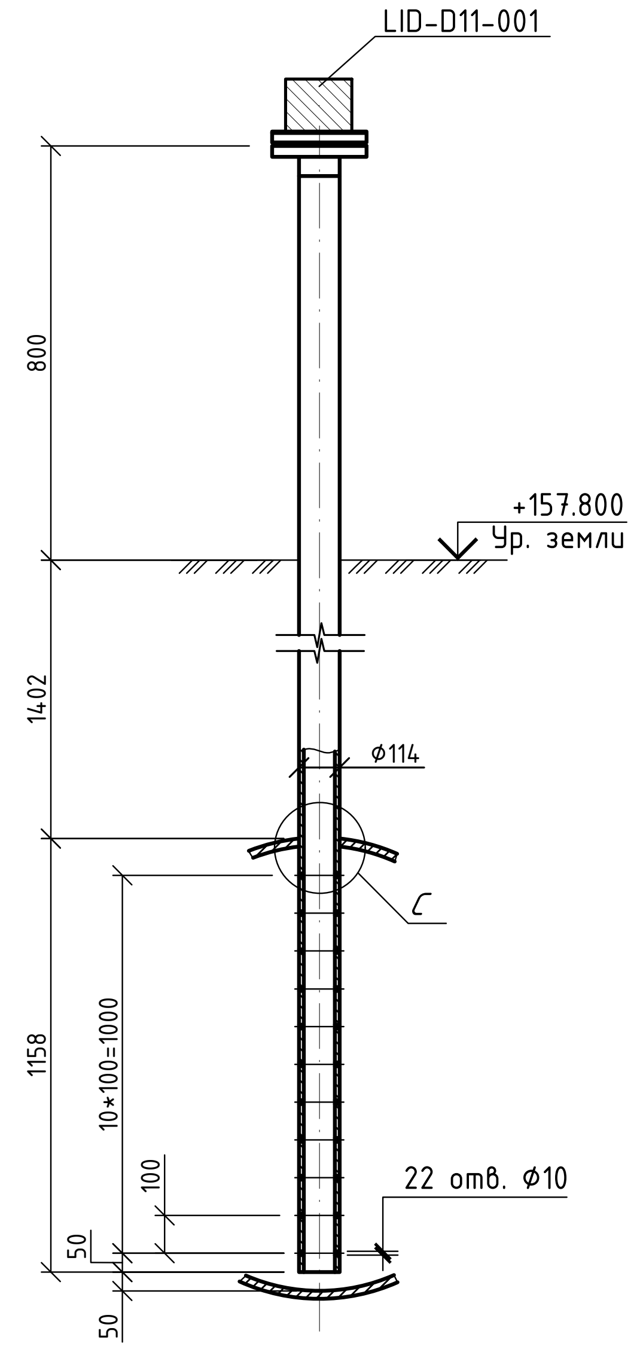

## Разделитель (V=0,4 м3)
М 1:25

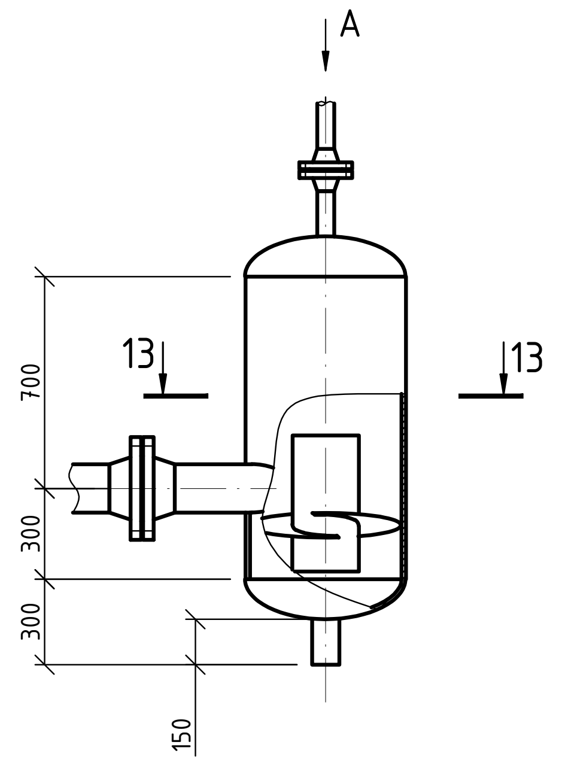

## Вид "А"
(1:25)

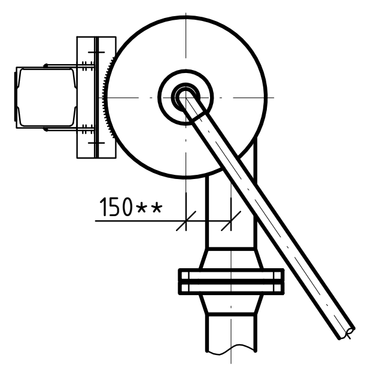

## Изометрический вид
М 1:200

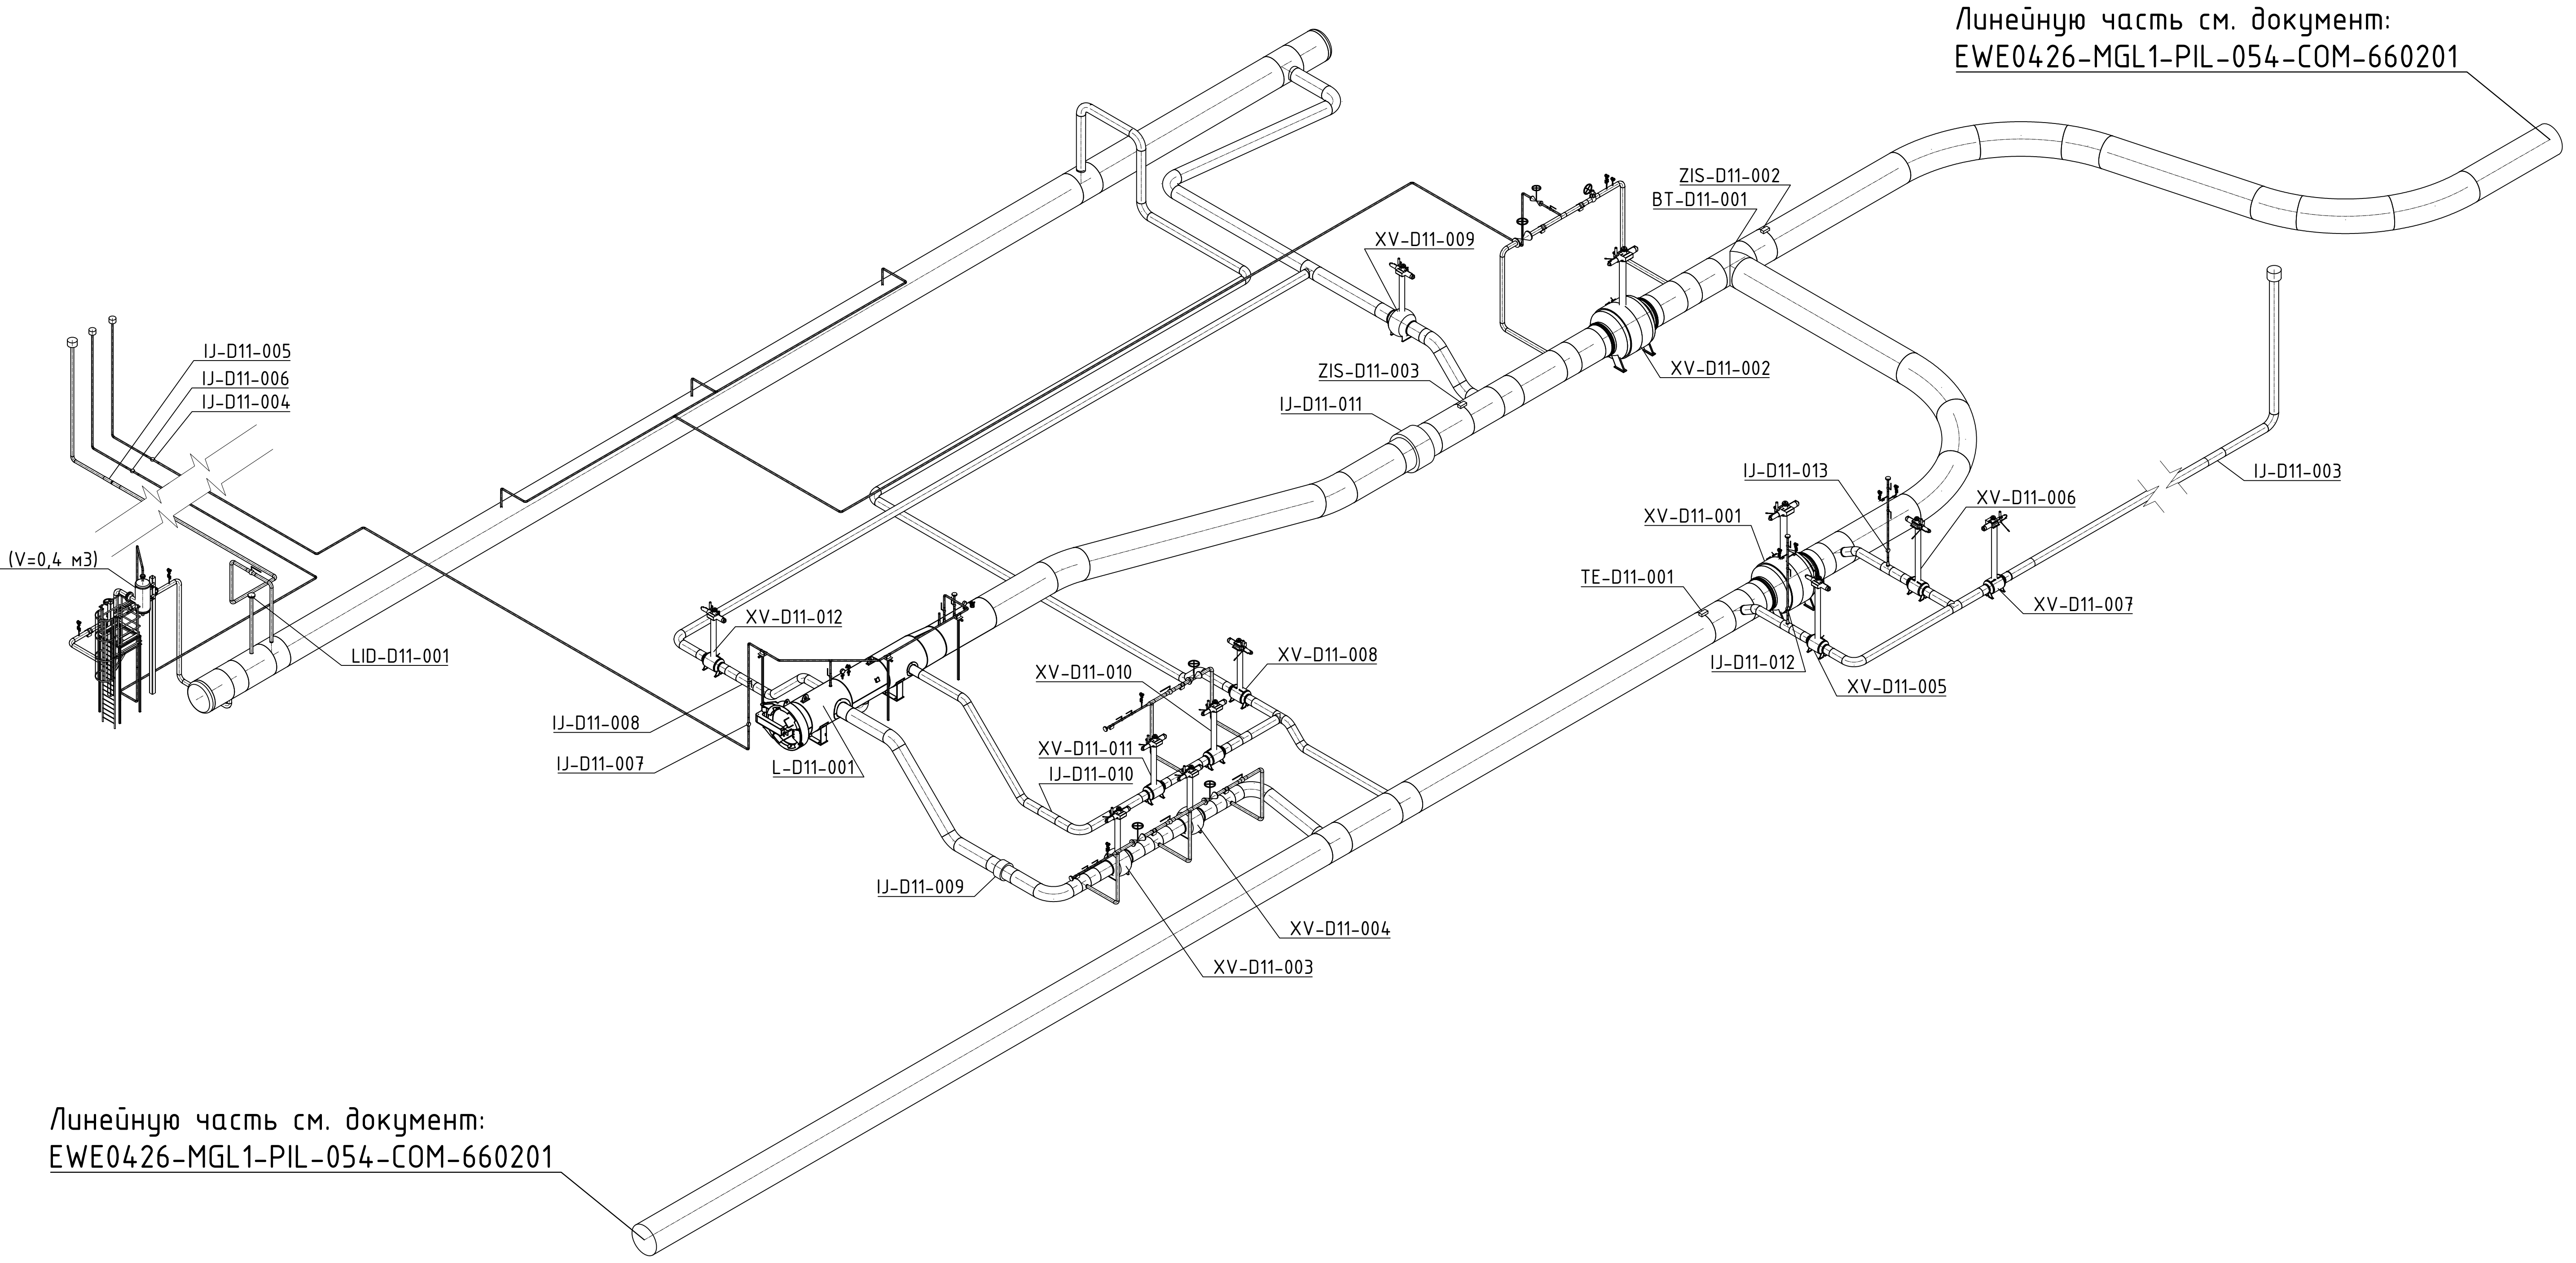

Линейную часть см. документ:
EWE0426-MGL1-PIL-054-COM-660201

Линейную часть см. документ:
EWE0426-MGL1-PIL-054-COM-660201

## Разрез 13-13 (1:25)

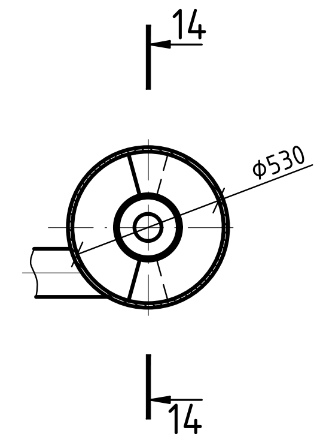

## Разрез 14-14 (1:10)

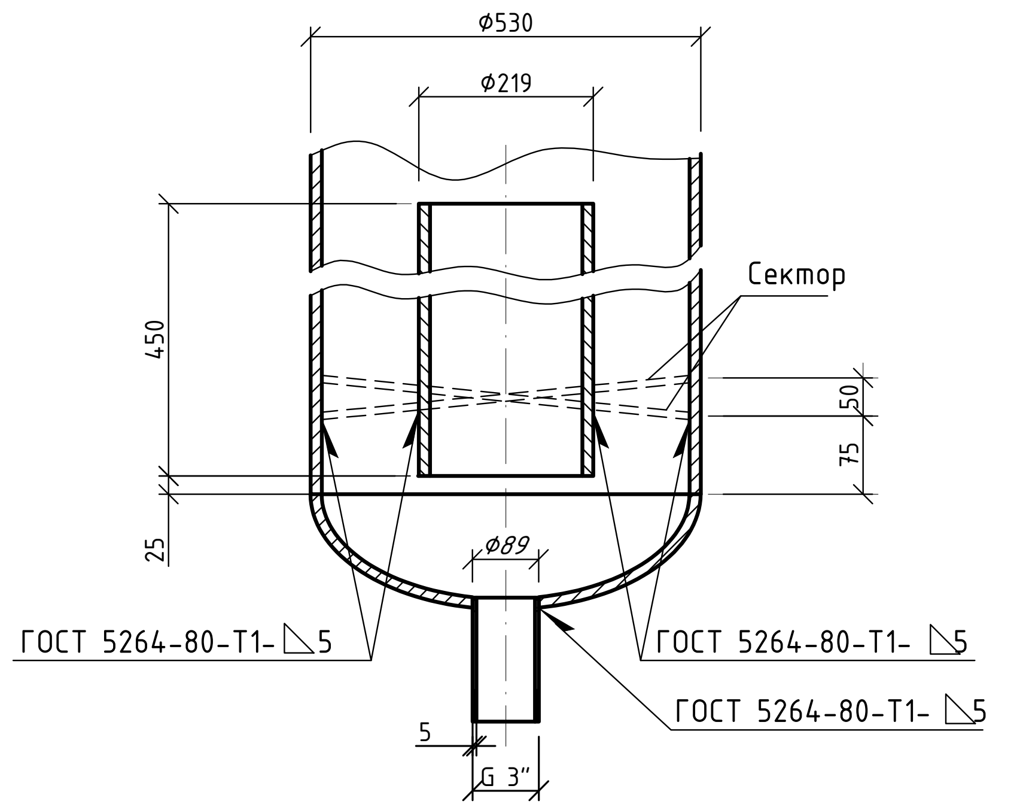

## Сектор
(1:10)

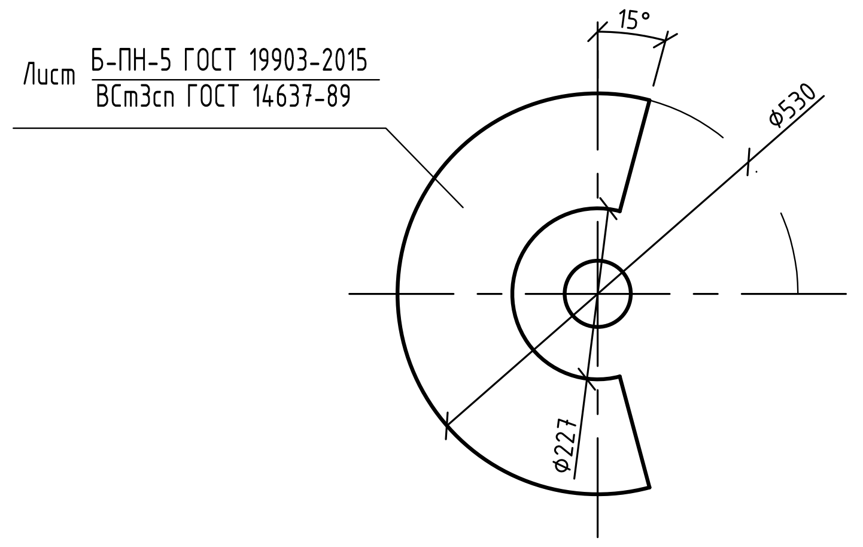

## Вид "С"
(1:5)

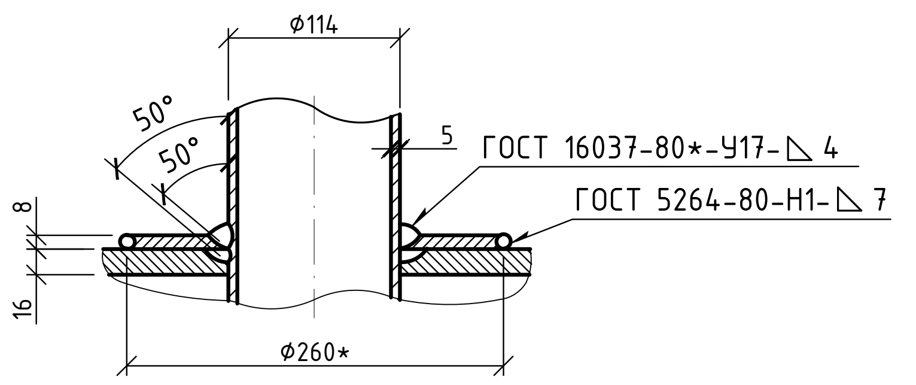

## Вид "Д"
(1:5)

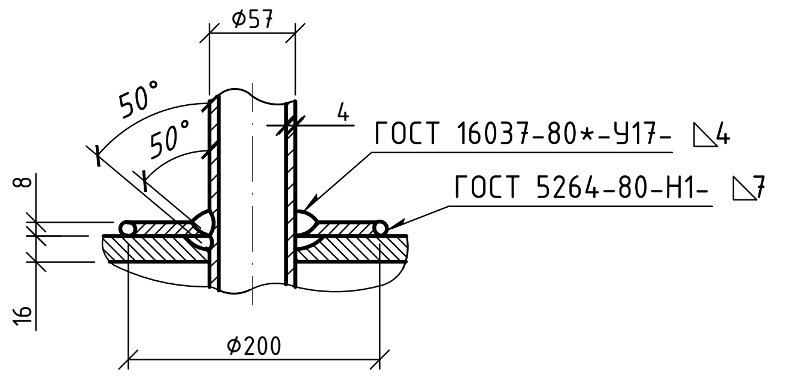

Взам. инв. №

Подпись и дата

Инв.№ подл.

| | | | | |
|---|---|---|---|---|
| | | | | |
| | | | | |
| | | | | |
| | | | | |
| A1 | 25.09.2026 | Утверждено для строительства | | |
| R1 | 27.08.2026 | Выпущено для рассмотрения | | |
| Рев | Дата | Назначение ревизии | Проверил | Утвердил |

ЗАКАЗЧИК: UTG UZTRANSGAZ
ГЕНЕРАЛЬНЫЙ ПОДРЯДЧИК: UET UZBEKENERGOTAMIR
ПОДРЯДЧИК: PBG Pro Build Generation
ГЕНЕРАЛЬНЫЙ ПРОЕКТИРОВЩИК: EAST WEST ENGINEERING

EWE0426-MGL1-PRE-054-DRW-690203-A1

«СТРОИТЕЛЬСТВО НОВЫХ НИТОК (УЧАСТКОВ) ГАЗОПРОВОДОВ «ГАЗЛИ - САРИМОЙ» И «АКЧАЛОК - ГАЗЛИ - НУКУС» ОБЩЕЙ ПРОТЯЖЕННОСТЬЮ НЕ МЕНЕЕ 275 КМ».

| Изм. | Кол.уч. | Лист | №док. | Подпись | Дата |
|---|---|---|---|---|---|
| ГИП | | Кирпичников С. | | | 09.2026 |
| Нач.отд. | | Рябинин А. | | | 09.2026 |
| Исполн. | | Таштимуров Р. | | | 09.2026 |
| | | | | | |
| | | | | | |
| Н.контр | | Кирпичников С. | | | 09.2026 |

Узел приема/запуска очистных устройст DN1200. УЗПОУ-D11.

| Стадия | Лист | Листов |
|---|---|---|
| РП | 3 | 3 |

План. Разрезы. Узлы. Виды. М1:100

ООО "EAST-WEST Engineering"
г. Ташкент 2026г.

Формат / Format A1