Схема расположения фундаментов. Схема расположения стоек.
Схема расположения сеточных панелей М 1:100

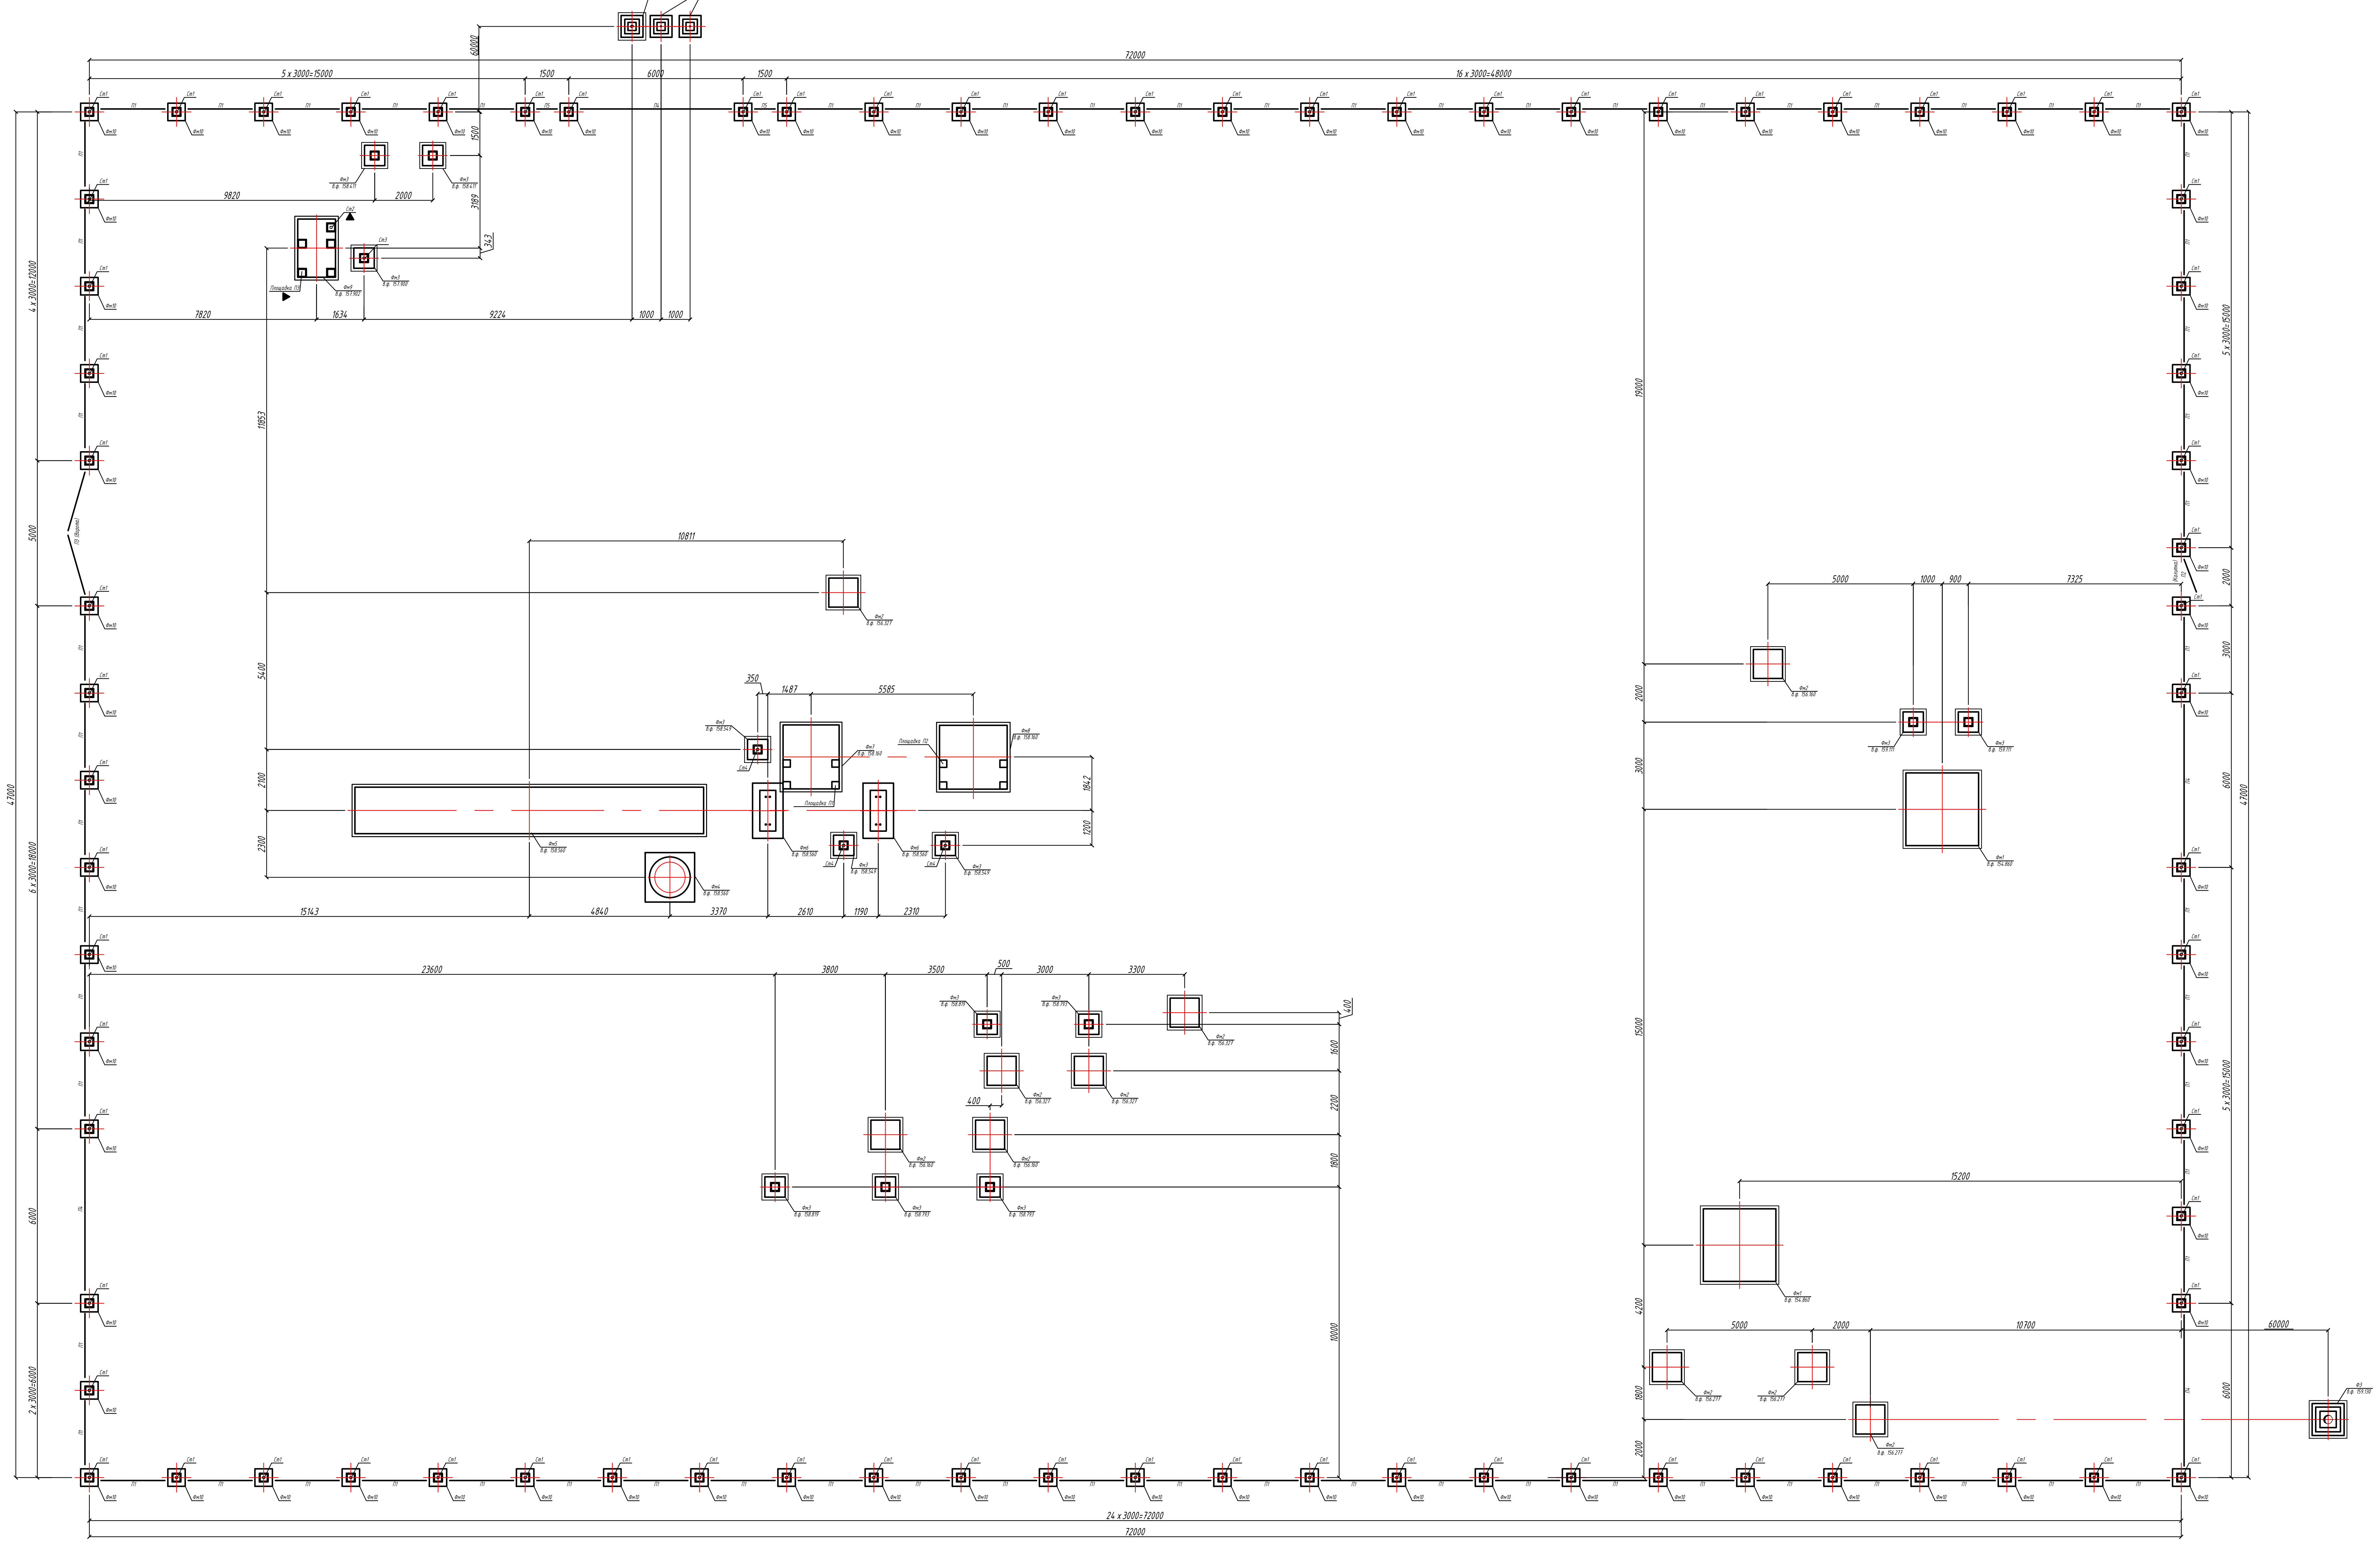

Ведомость элементов

Марка Поз.	Наименование	Кол. шт
	Фундамент Фм 1	2
	Фундамент Фм 2	10
	Фундамент Фм 3	13
	Фундамент Фм 4	1
	Фундамент Фм 5	1
	Фундамент Фм 6	2
	Фундамент Фм 7	1
	Фундамент Фм 8	1
	Фундамент Фм 9	1
	Фундамент Фм 10	75
	Стойка Ст 1	75
	Стойка Ст 2	1
	Стойка Ст 3	1
	Панель П 1	71
	Панель П 2	1
	Панель П 3	1
	Панель П 4	4
	Панель П 5	2
	Фундамент Ф 1	1
	Фундамент Ф 2	2
	Фундамент Ф 3	1

▲ - Ориентация сечения колонны

Примечание
1. Общие данные смотреть на листе EWE0426-MGL1-STR-054-COM-690501-A1

Рев.	Дата	Назначение ревизии	Проверил	Утвердил
A1	10.10.26	Утверждено для строительства		
R1	20.09.26	Выпущено для рассмотрения		

ЗАКАЗЧИК: UTG UZTRANSGAZ
ГЕНЕРАЛЬНЫЙ ПОДРЯДЧИК: UET UZBEKENERGOTAMIR
ПОДРЯДЧИК: PBG Pro Build Generation
ГЕНЕРАЛЬНЫЙ ПРОЕКТИРОВЩИК: EAST WEST ENGINEERING

EWE0426-MGL1-STR-054-DRW-690502-A1

«СТРОИТЕЛЬСТВО НОВЫХ НИТОК (УЧАСТКОВ) ГАЗОПРОВОДОВ «ГАЗЛИ - САРИМОЙ» И «АКЧАЛОК - ГАЗЛИ - НУКУС» ОБЩЕЙ ПРОТЯЖЕННОСТЬЮ НЕ МЕНЕЕ 275 КМ».

Изм.	Кол.уч.	Лист	№ док.	Подп.	Дата
ГИП		Кирпичников			10.26
Нач.отдела		Каршиев			10.26
Разраб.		Мамешов			10.26
Проверил		Каршиев			10.26
Н. контр.		Кирпичников			10.26

ГАЗОПРОВОД "ГАЗЛИ-САРИМОЙ" (54 КМ)

Стадия	Лист	Листов
РД	1	1

Схема расположения фундаментов. Схема расположения стоек. Схема расположения сеточных панелей

ООО "EAST-WEST Engineering"
г. Ташкент 2026г.

Формат А0

Взам.инв. N
Подп. и дата
Инв.N подл.