


Фундамент Фм 1

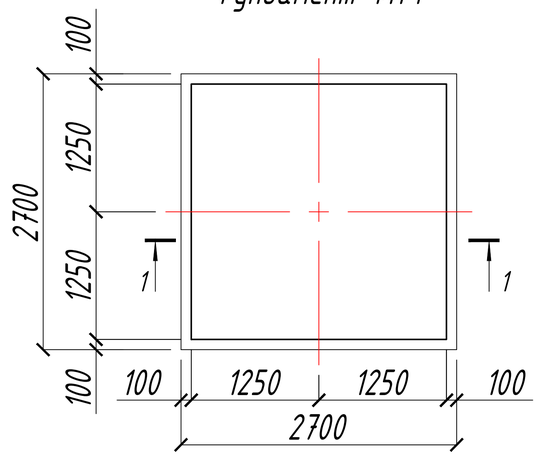


Разрез 1-1

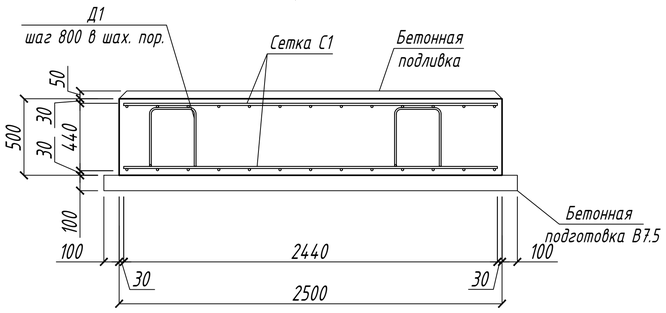

Сетка С 1

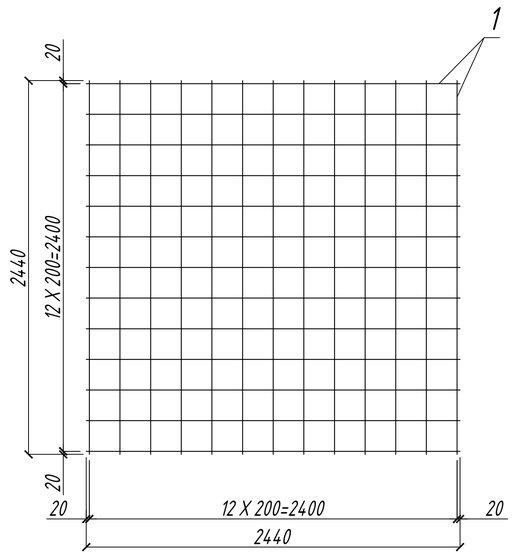


Фундамент Фм 2

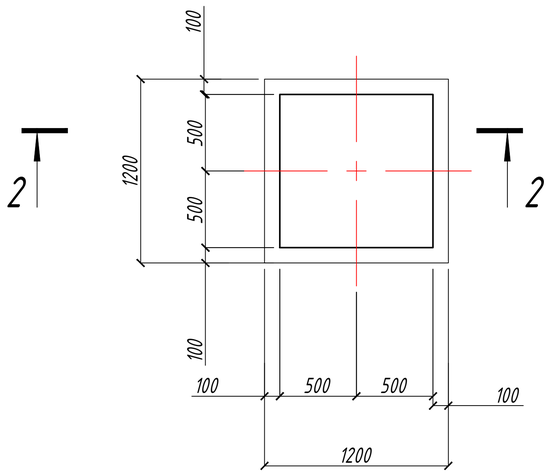


Разрез 2-2


Сетка С 2

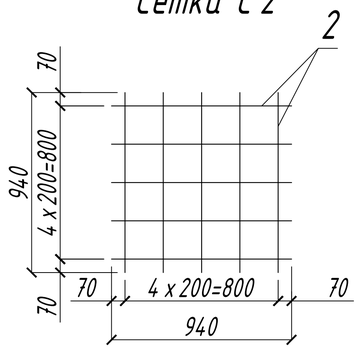


Фундамент Фм 3

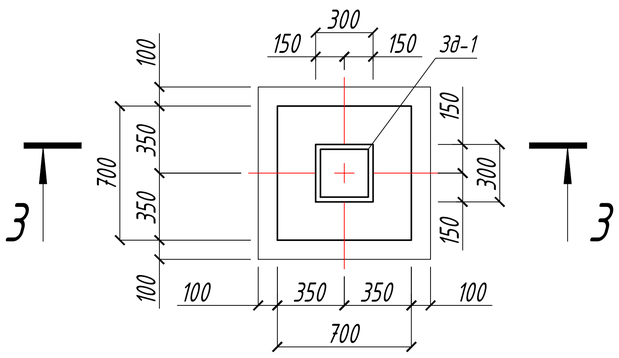


Разрез 3-3

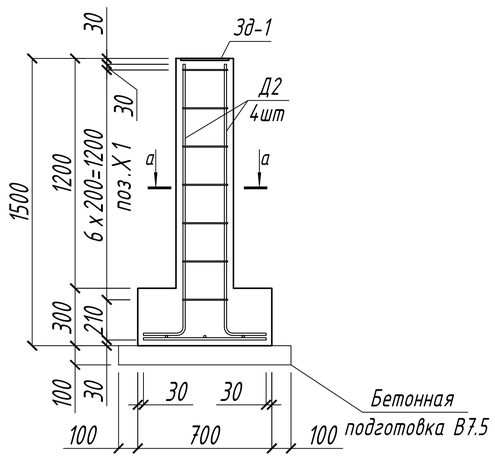


Сетка С 3

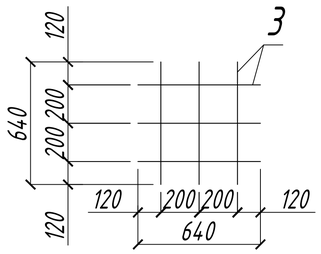



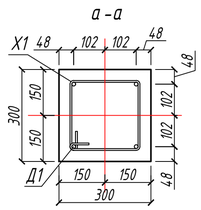


Закладная деталь 3д -1

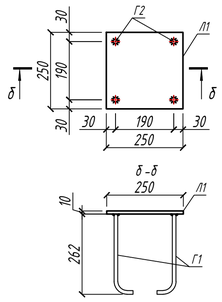

		Фундамент Фм 1 (на 1 шт.)			
		Сборочные единицы			
С 1	см. данный лист	Горизонтальная сетка С 1	2	56.29	112.59
		Детали			
Д 1	см. данный лист	ГОСТ 34028-2016 Ф12 А400 L=1560 мм	8	1.38	11.07
		Сетка С 1			
1	см. данный лист	ГОСТ 34028-2016 Ф12 А400 L=2440 мм	26	2.17	56.29
		Материал			
	см. данный лист	ГОСТ 26633-2010 Бетон В 25	3.7		м³
	см. данный лист	ГОСТ 26633-2010 Бетон В 7.5	0.9		м³
		Фундамент Фм 2 (на 1 шт.)			
		Сборочные единицы			
С 2	см. данный лист	Горизонтальная сетка С 2	2	8.34	16.68
		Детали			
Д 1	см. данный лист	ГОСТ 34028-2016 Ф12 А400 L=1560 мм	3	1.38	4.15
		Сетка С 2			
2	см. данный лист	ГОСТ 34028-2016 Ф12 А400 L=940 мм	10	0.83	8.34
		Материал			
	см. данный лист	ГОСТ 26633-2010 Бетон В 25	0.7		м³
	см. данный лист	ГОСТ 26633-2010 Бетон В 7.5	0.1		м³
		Фундамент Фм 3 (на 1 шт.)			
		Сборочные единицы			
С 3	см. данный лист	Горизонтальная сетка С 3	1	3.41	3.41
Зд -1	см. данный лист	Закладная деталь Зд -1	1	6.05	6.05
		Детали			
Д 2	см. данный лист	ГОСТ 34028-2016 Ф12 А400 L=1640 мм	4	1.46	5.82
Х1	см. данный лист	ГОСТ 34028-2016 Ф6 А240 L=1020 мм	7	0.23	1.58
		Сетка С 3			
3	см. данный лист	ГОСТ 34028-2016 Ф12 А400 L=640 мм	6	0.57	3.41
		Закладная деталь Зд -1			
Л 1	см. данный лист	ГОСТ 19903-2015 -Н10 250х250	1	4.91	4.91
Г 1	см. данный лист	ГОСТ 34028-2016 Ф12 А400 L=320 мм	4	0.28	1.14
		Материал			
	см. данный лист	ГОСТ 26633-2010 Бетон В 25	0.3		м³
	см. данный лист	ГОСТ 26633-2010 Бетон В 7.5	0.1		м³

Ведомость деталей

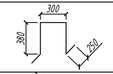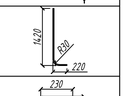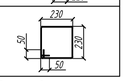Поз.	Эскиз
Д 1	
Д 2	
Х 1	

Все размеры даны по внешнем граням детали

Примечание

1. Общие данные смотреть на листе EWE0426-MGL1-STR-054-COM-690501-A1
2. Отметки верха фундамента смотреть на листе EWE0426-MGL1-STR-054-DRW-690502-A1
3. Под монолитным фундаментом выполнить подготовку из бетона кл. В 7.5 толщиной 100 мм с уширением на 100 мм в каждую сторону от размеров подошвы фундамента. Под ним выполнить подготовку из щебня, вдавленного в грунт, толщиной 100 мм, с проливкой горячим битумом с выступом за боковые грани бетонной подготовки по 100 мм в каждую сторону.

Рев.	Дата	Назначение ревизии	Проверил	Утвердил
A1	10.10.26	Утверждено для строительства		
R1	20.09.26	Выпущено для рассмотрения		

ЗАКАЗЧИК: UTG UKRAINE | ГЕНЕРАЛЬНЫЙ ПОДРЯДЧИК: UET | ПОДРЯДЧИК: PBG | ГЕНЕРАЛЬНЫЙ ПРОЕКТИРОВЩИК: EAST WEST ENGINEERING

EWE0426-MGL1-STR-054-DRW-690503-A1

«СТРОИТЕЛЬСТВО НОВЫХ НИТОК (УЧАСТКОВ) ГАЗОПРОВОДОВ «ГАЗЛИ - САРИМОЙ» И «АКЧАЛОК - ГАЗЛИ - НУКУС» ОБЩЕЙ ПРОТЯЖЕННОСТЬЮ НЕ МЕНЕЕ 275 КМ».

Изм.	Кол.уч.	Лист	№ док.	Подп.	Дата				
ГИП		Кирпичников			10.26	ГАЗОПРОВОД "ГАЗЛИ-САРИМОЙ" (54 КМ)	Стадия	Лист	Листов
Нач.отдела		Каршиев			10.26		РД	1	1
Разраб.		Мангиов			10.26				
Проверил		Каршиев			10.26	Фундаменты Фм 1; Фм 2; Фм 3	ООО "EAST-WEST Engineering" г. Ташкент 2026г.		
Н. контр.		Кирпичников			10.26				

Инв. N подл. | Подп. и дата | Взам. инв. N

Формат А1