Фундамент Фм 4

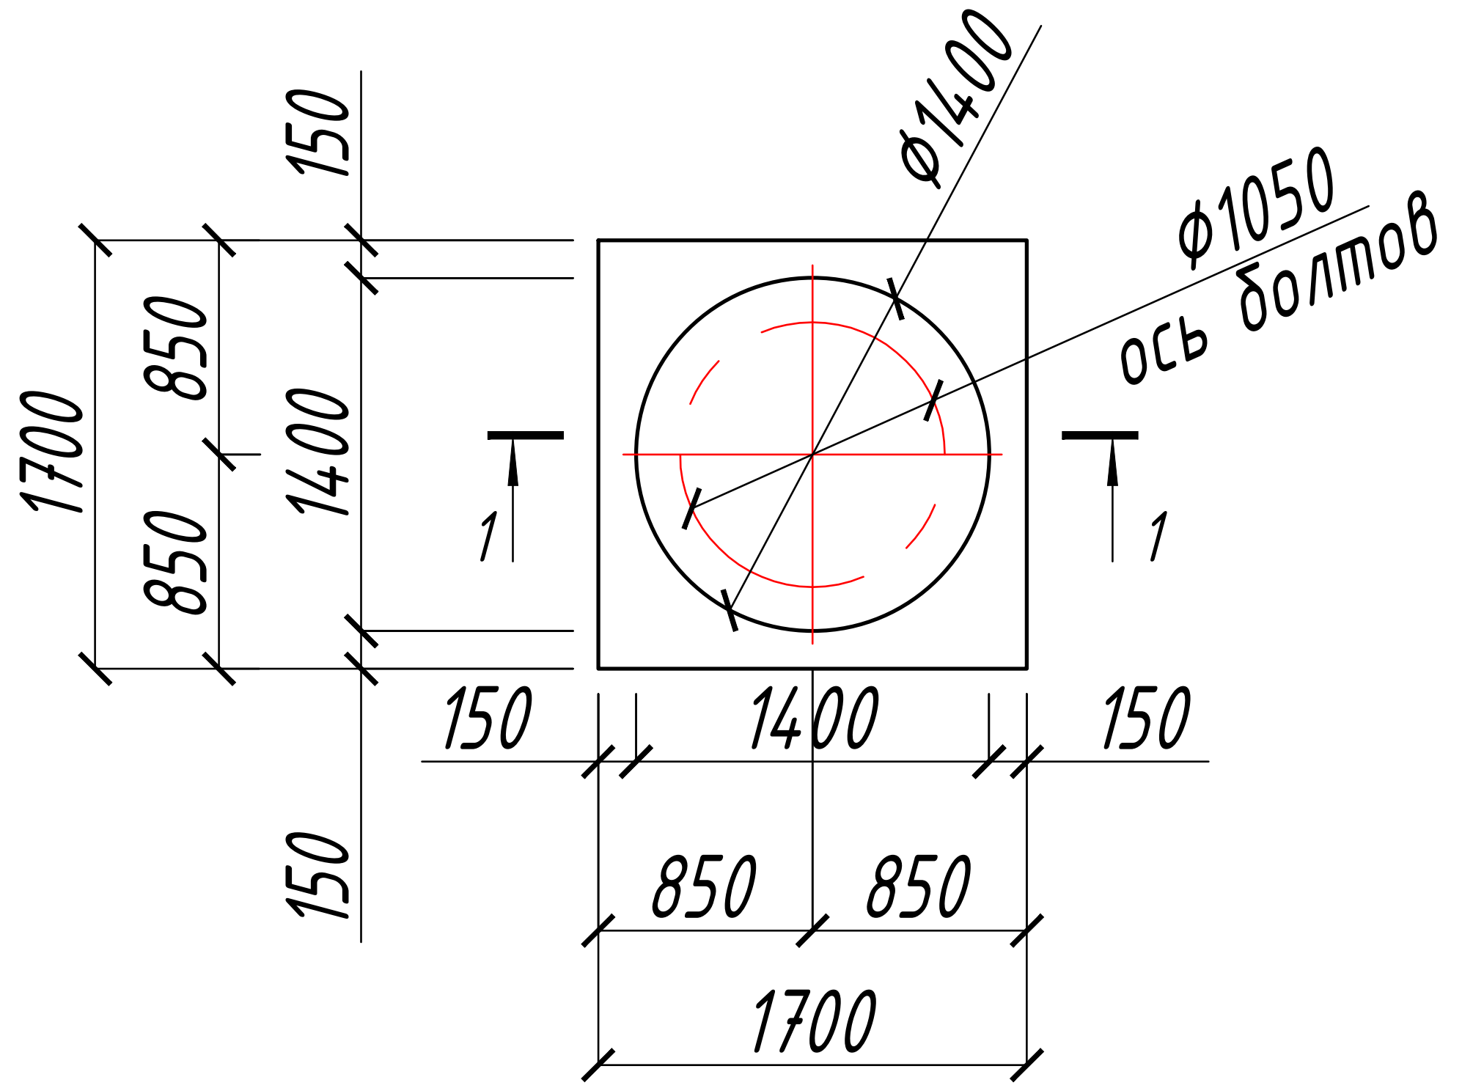

Разрез 1-1

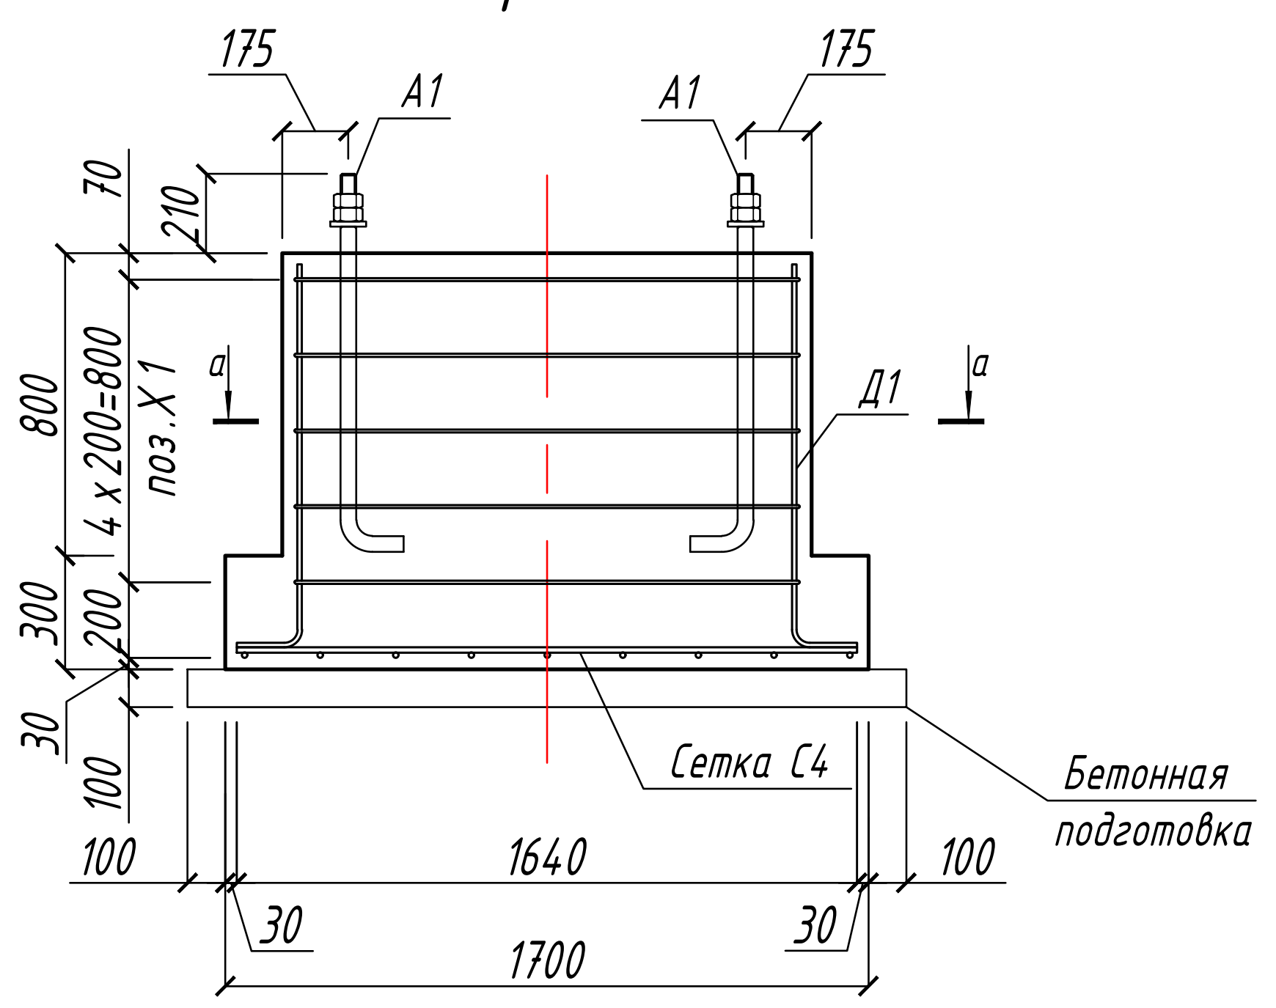

а-а

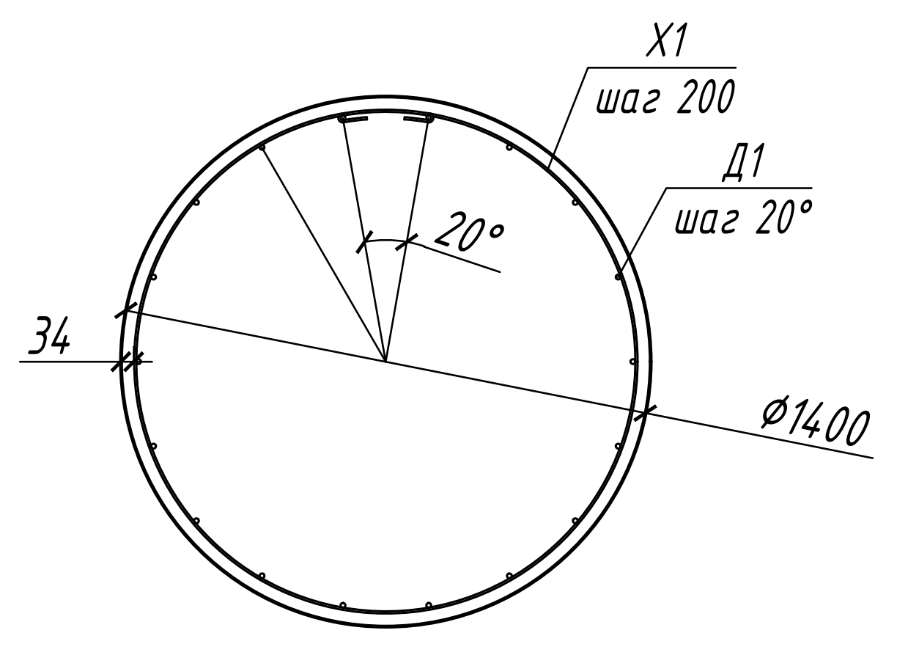

Сетка С 4

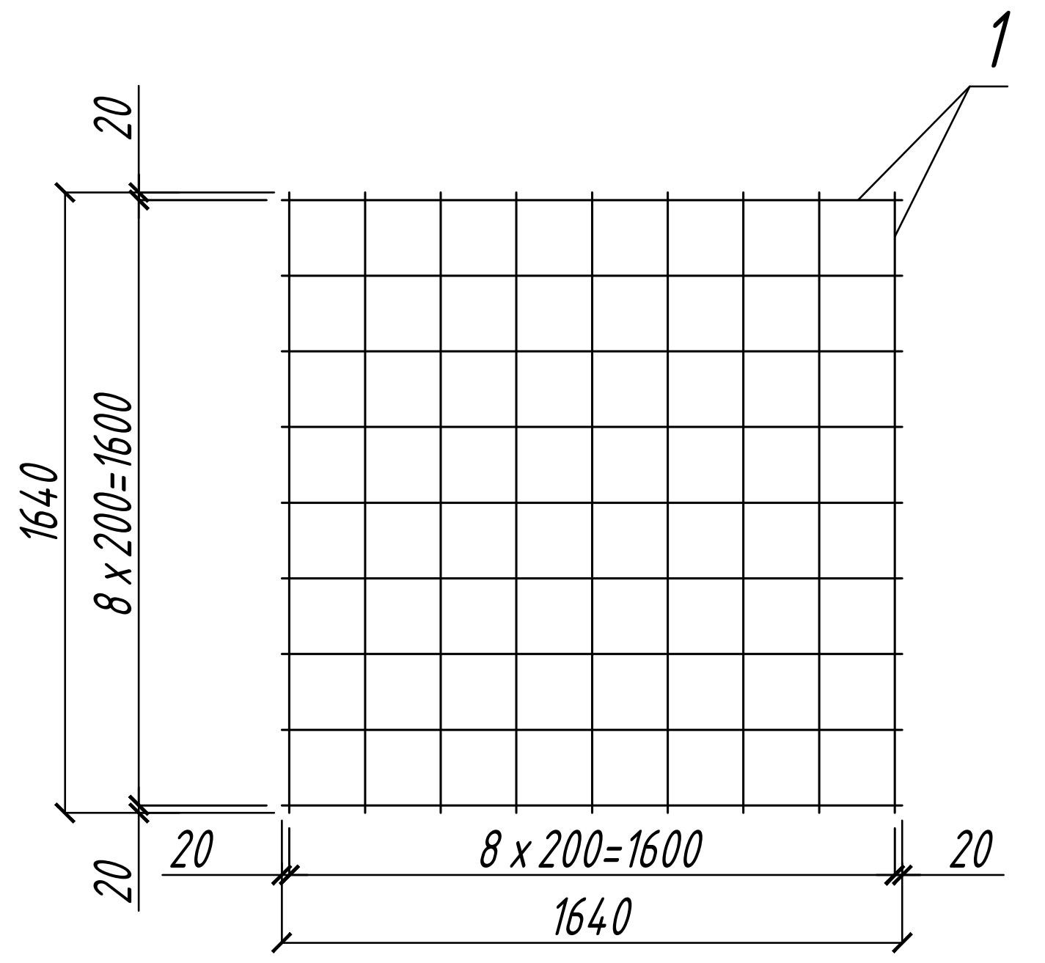

Фундамент Фм 5

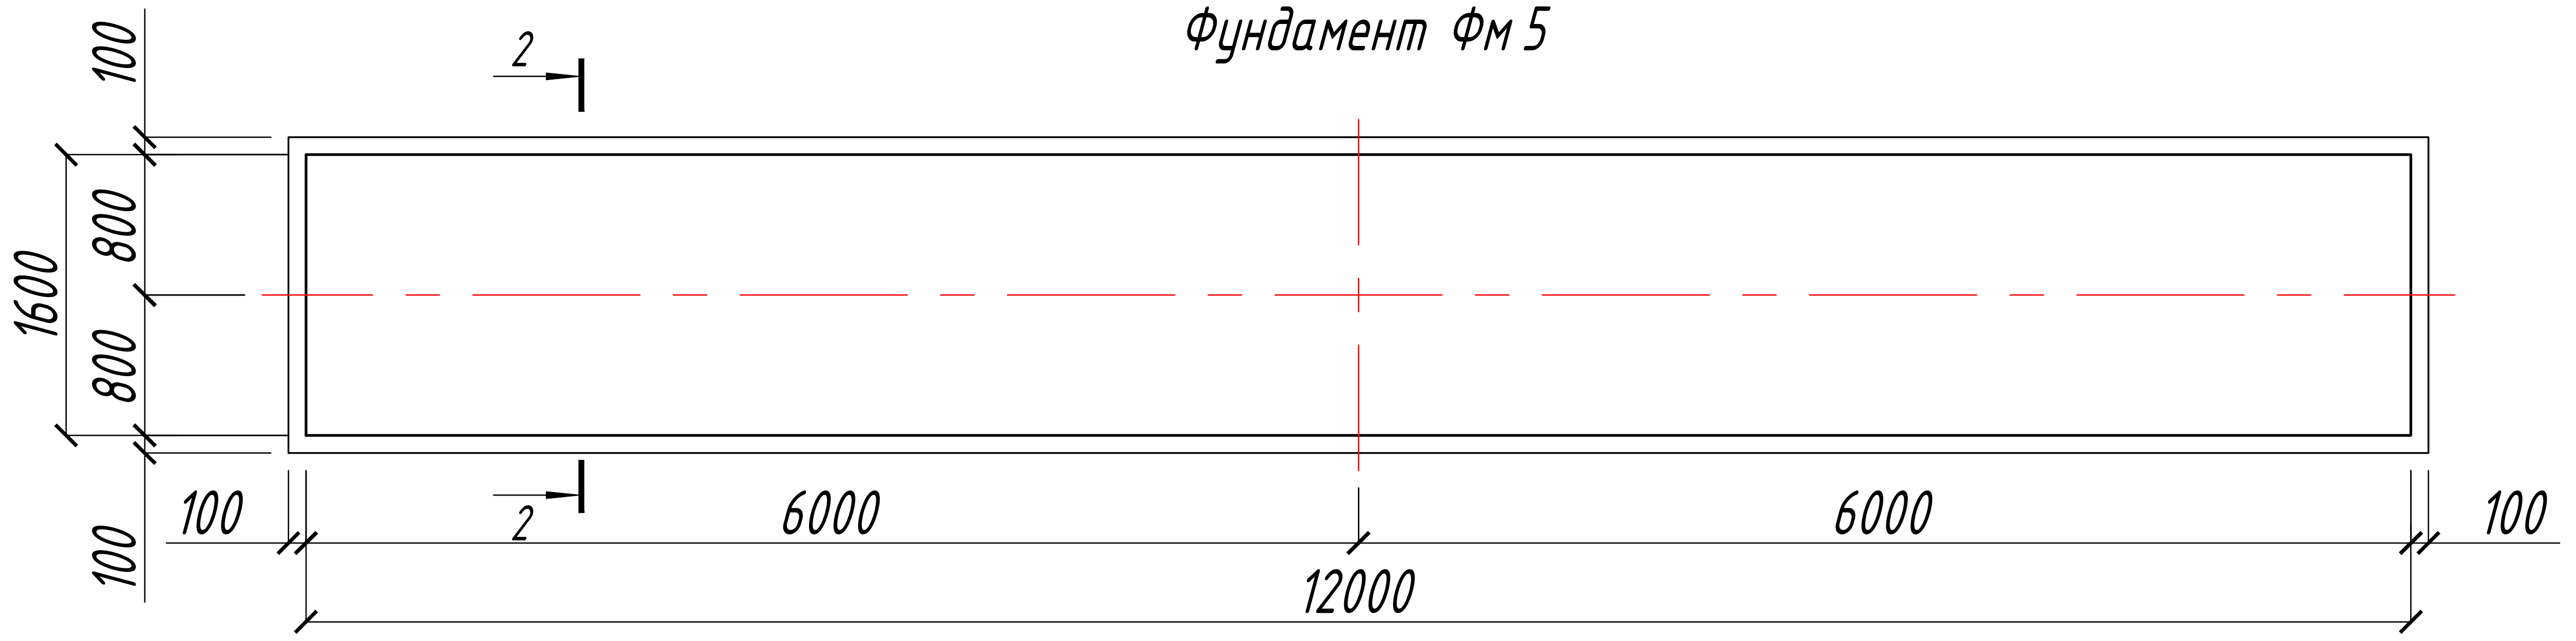

Разрез 2-2

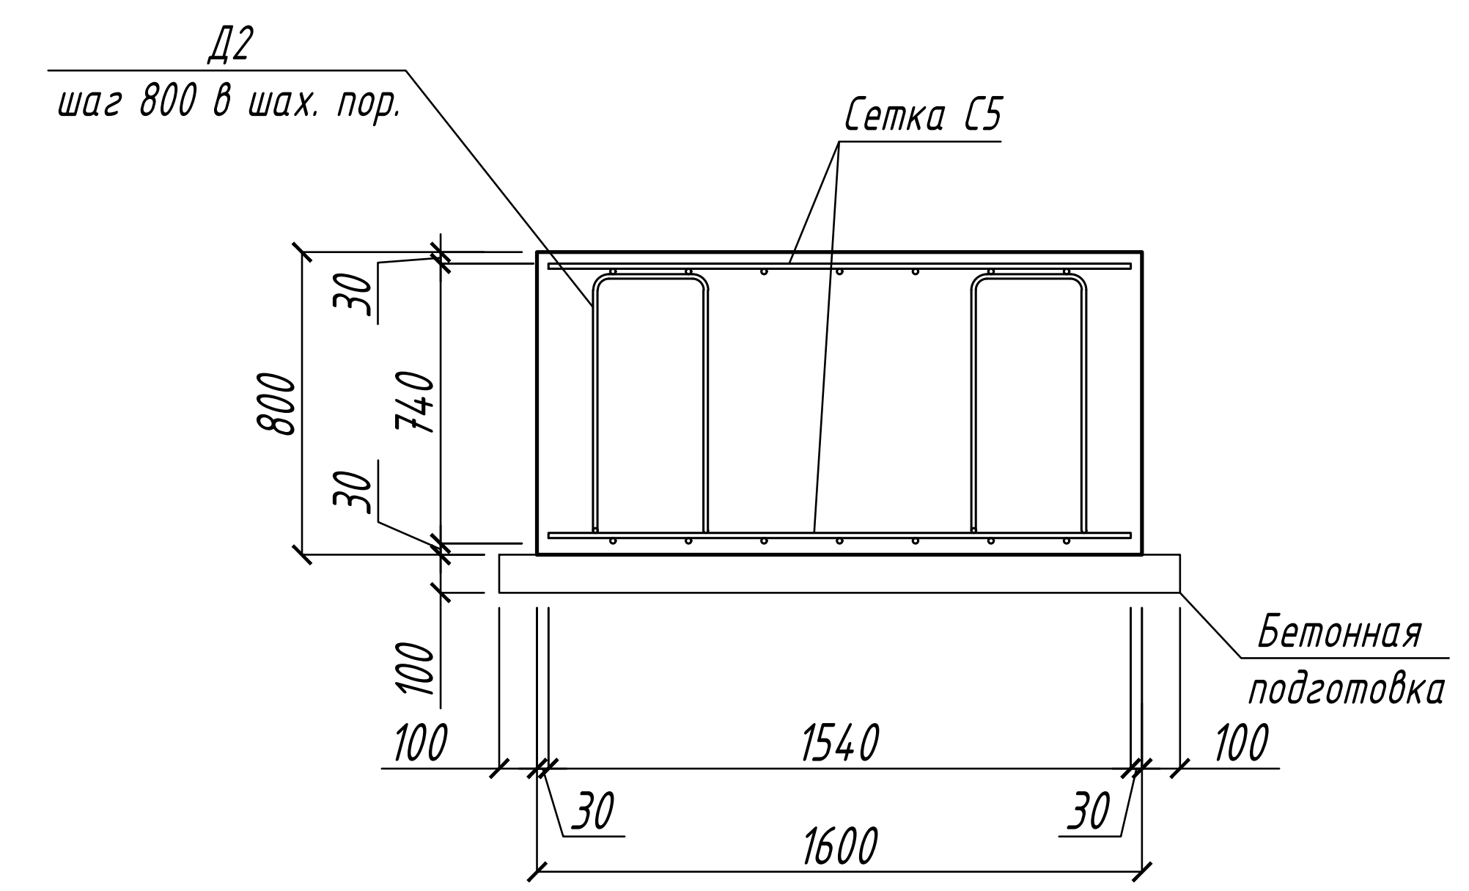

Сетка С 5 (п.м.)

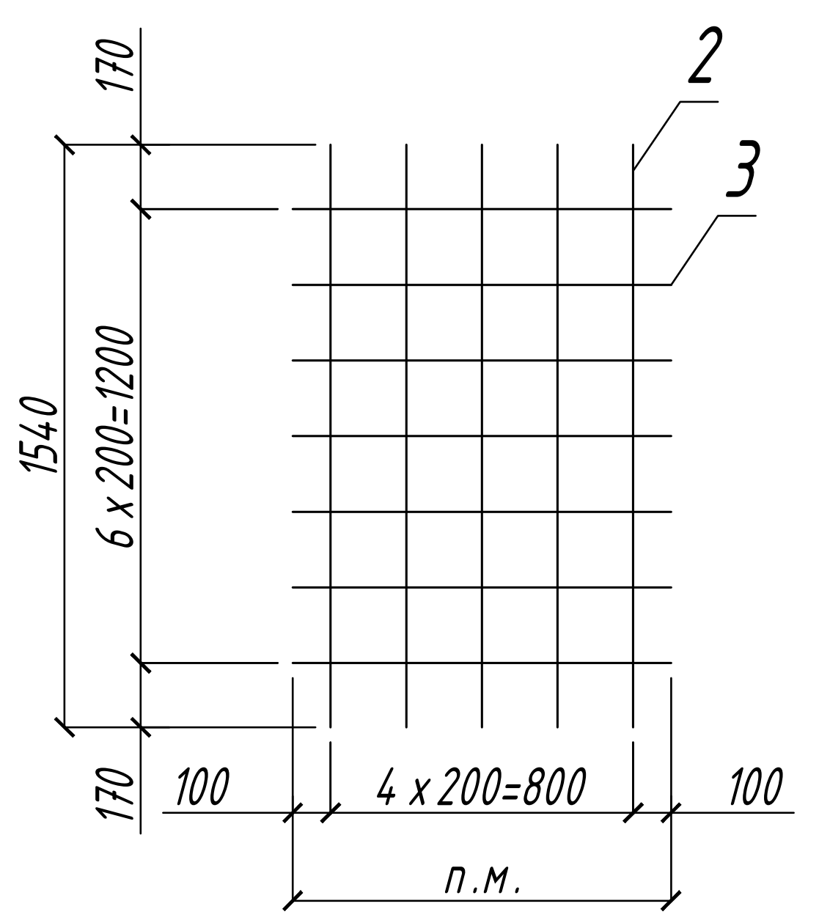

Фундамент Фм 6

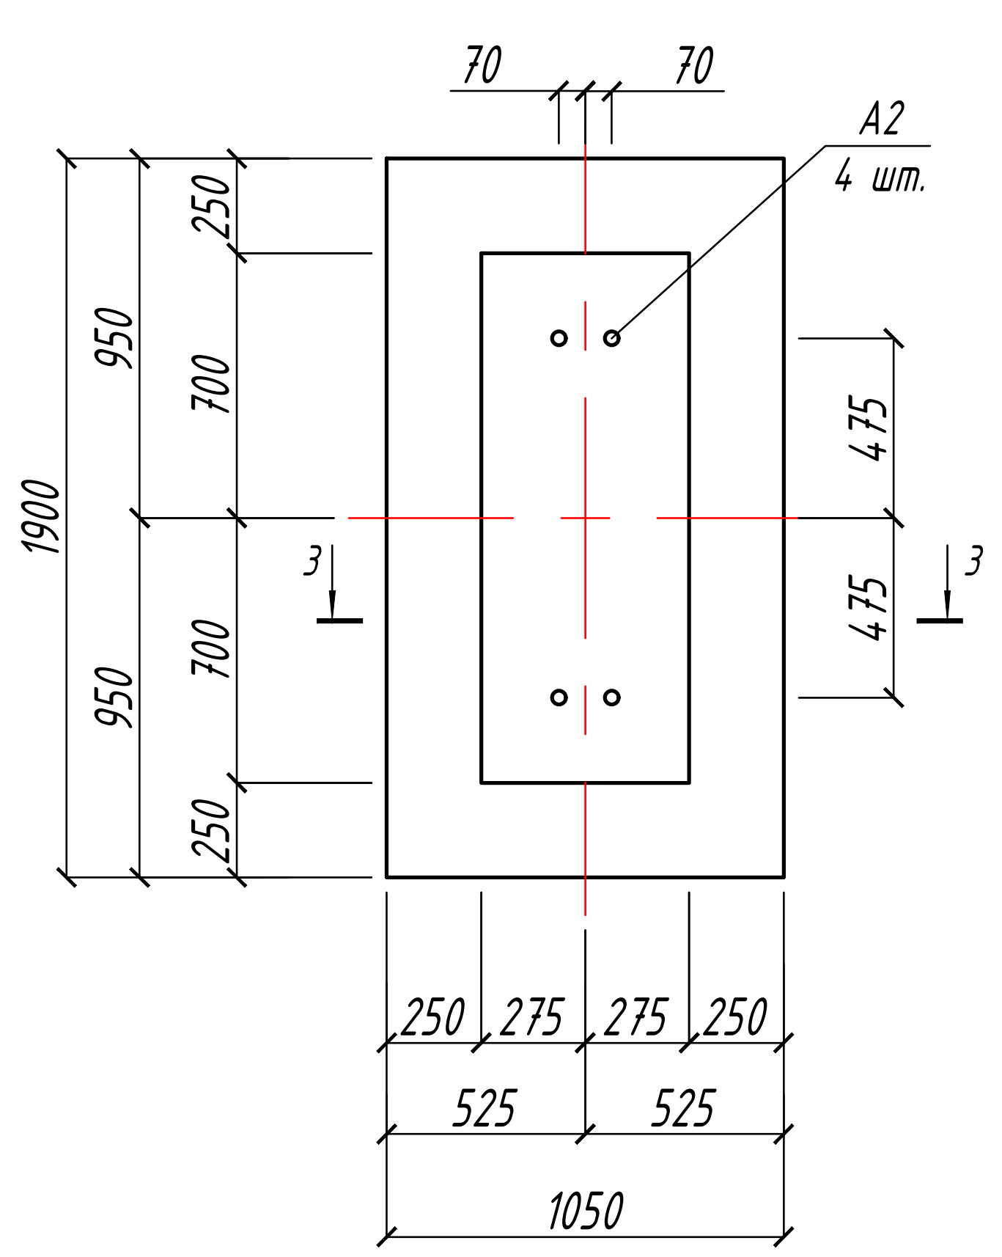

Разрез 3-3

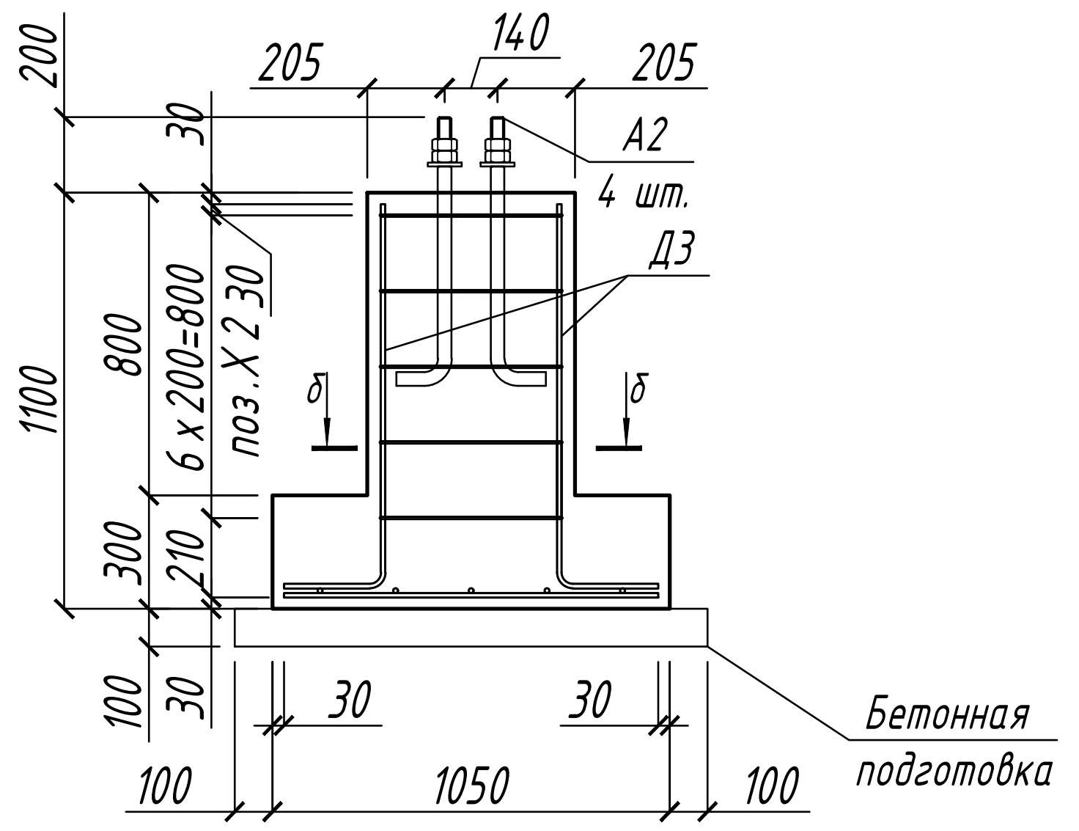

б-б

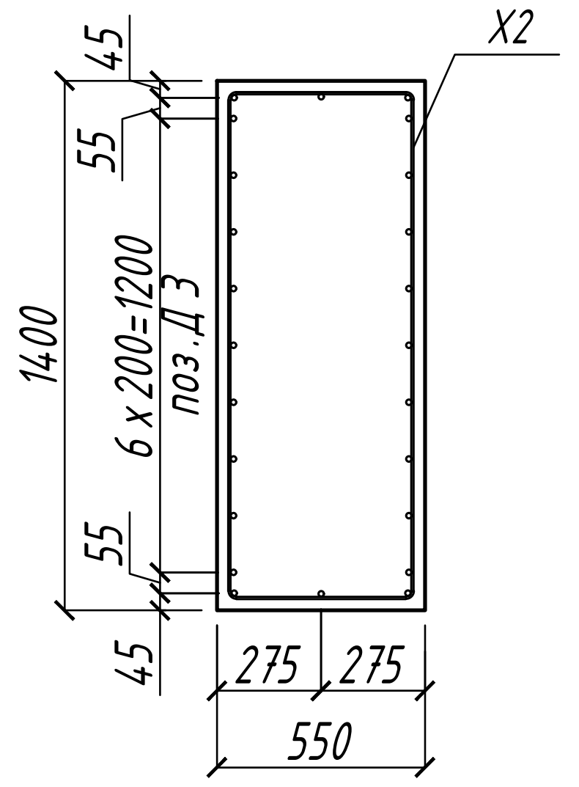

Сетка С 6

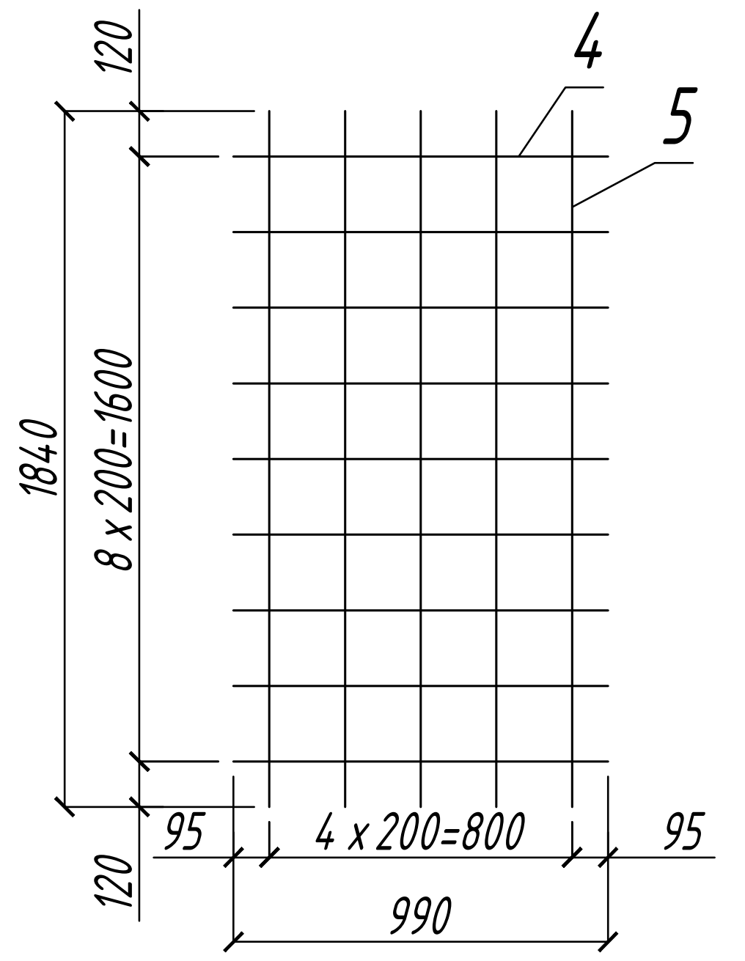

Ведомость деталей

Поз.	Эскиз
Д 1	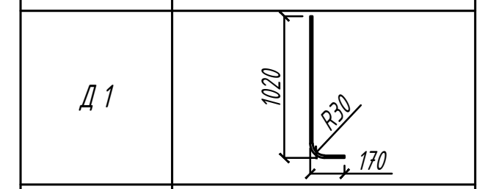
X1	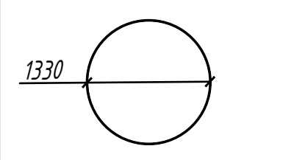
Д 2	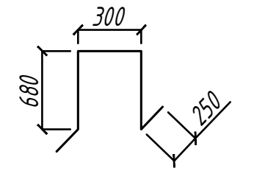
Д 3	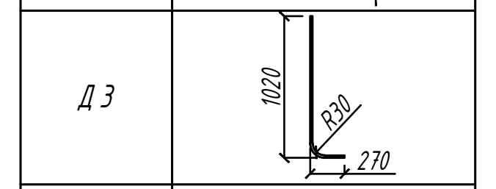
X2	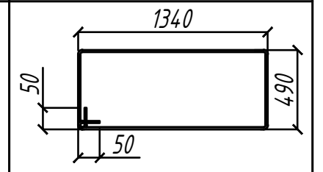

Все размеры даны по внешнем граням детали

Спецификация элементов

Марка Поз.	Обозначение	Наименование		Кол. шт	Масса ед., кг	Прим.
		Фундамент Фм 4 (на 1 шт.)				
		Сборочные единицы				
С 4	см. данный лист	Горизонтальная сетка С 4		1	26.19	26.19
		Детали				
Д 1	см. данный лист	ГОСТ 34028-2016 ø12 A400	L=1190 мм	18	1.06	19.01
X 1	см. данный лист	ГОСТ 34028-2016 ø6 A240	L=4080 мм	5	0.91	4.53
A 1	ГОСТ 24379.1-2012	Болт 1.1. М 42 x 1000 ВСт 3 пс 2		12	13.98	167.76
		Сетка С 4				
1	см. данный лист	ГОСТ 34028-2016 ø12 A400	L=1640 мм	18	1.46	26.19
		Материал				
	см. данный лист	ГОСТ 26633-2010 Бетон В 25		2.1		$м^3$
	см. данный лист	ГОСТ 26633-2010 Бетон В 7.5		0.4		$м^3$
		Фундамент Фм 5 (на 1 шт.)				
		Сборочные единицы				
С 5	см. данный лист	Горизонтальная сетка С 5 (п.м.)		12	6.83	81.99
		Детали				
Д 2	см. данный лист	ГОСТ 34028-2016 ø12 A400	L=2160 мм	36	1.92	69.00
		Сетка С 5(п.м.)				
2	см. данный лист	ГОСТ 34028-2016 ø12 A400	L=1540 мм	5	1.37	6.83
3	см. данный лист	ГОСТ 34028-2016 ø12 A400	L=1000 мм	7	0.89	6.21
		Материал				
	см. данный лист	ГОСТ 26633-2010 Бетон В 25		15.4		$м^3$
	см. данный лист	ГОСТ 26633-2010 Бетон В 7.5		2.2		$м^3$
		Фундамент Фм 6 (на 1 шт.)				
		Сборочные единицы				
С 6	см. данный лист	Горизонтальная сетка С 6		1	7.91	7.91
		Детали				
Д 3	см. данный лист	ГОСТ 34028-2016 ø12 A400	L=1290 мм	20	1.14	22.89
X 2	см. данный лист	ГОСТ 34028-2016 ø6 A240	L=3760 мм	5	0.83	4.17
A 2	ГОСТ 24379.1-2012	Болт 1.1. М 36 x 710 ВСт 3 пс 2		4	7.59	30.36
		Сетка С 6				
4	см. данный лист	ГОСТ 34028-2016 ø12 A400	L=990 мм	9	0.88	7.91
5	см. данный лист	ГОСТ 34028-2016 ø12 A400	L=1840 мм	5	1.63	8.16
		Материал				
	см. данный лист	ГОСТ 26633-2010 Бетон В 25		1.3		$м^3$
	см. данный лист	ГОСТ 26633-2010 Бетон В 7.5		0.3		$м^3$

Примечание

1. Общие данные смотреть на листе EWE0426-MGL1-STR-054-COM-690501-A1
2. Отметки верха фундамента смотреть на листе EWE0426-MGL1-STR-054-DRW-690502-A1
3. Под монолитным фундаментом выполнить подготовку из бетона кл. В 7.5 толщиной 100 мм с уширением на 100 мм в каждую сторону от размеров подошвы фундамента. Под ним выполнить подготовку из щебня, вдавленного в грунт, толщиной 100 мм, с проливкой горячим битумом с выступом за боковые грани бетонной подготовки по 100 мм в каждую сторону.

Рев.	Дата	Назначение ревизии	Проверил	Утвердил
A1	10.10.26	Утверждено для строительства		
R1	20.09.26	Выпущено для рассмотрения		

ЗАКАЗЧИК: UTG UZTRANSGAZ
ГЕНЕРАЛЬНЫЙ ПОДРЯДЧИК: UET UZBEKENERGOTAMIR
ПОДРЯДЧИК: PBG Pro Build Generation
ГЕНЕРАЛЬНЫЙ ПРОЕКТИРОВЩИК: EAST WEST ENGINEERING

EWE0426-MGL1-STR-054-DRW-690504-A1

«СТРОИТЕЛЬСТВО НОВЫХ НИТОК (УЧАСТКОВ) ГАЗОПРОВОДОВ «ГАЗЛИ - САРИМОЙ» И «АКЧАЛОК - ГАЗЛИ - НУКУС» ОБЩЕЙ ПРОТЯЖЕННОСТЬЮ НЕ МЕНЕЕ 275 КМ».

Изм.	Кол.уч.	Лист	№ док.	Подп.	Дата
ГИП		Кирпичников			10.26
Нач.отдела		Каршиев			10.26
Разраб.		Мамешов			10.26
Проверил		Каршиев			10.26
Н. контр.		Кирпичников			10.26

ГАЗОПРОВОД "ГАЗЛИ-САРИМОЙ" (54 КМ)

Стадия	Лист	Листов
РД	1	1

Фундаменты Фм 4; Фм 5; Фм 6

ООО "EAST-WEST Engineering"
г. Ташкент 2026г.

Формат A 2 x 3

Взам. инв. N
Подп. и дата
Инв. N подл.