Фундамент Фм 7

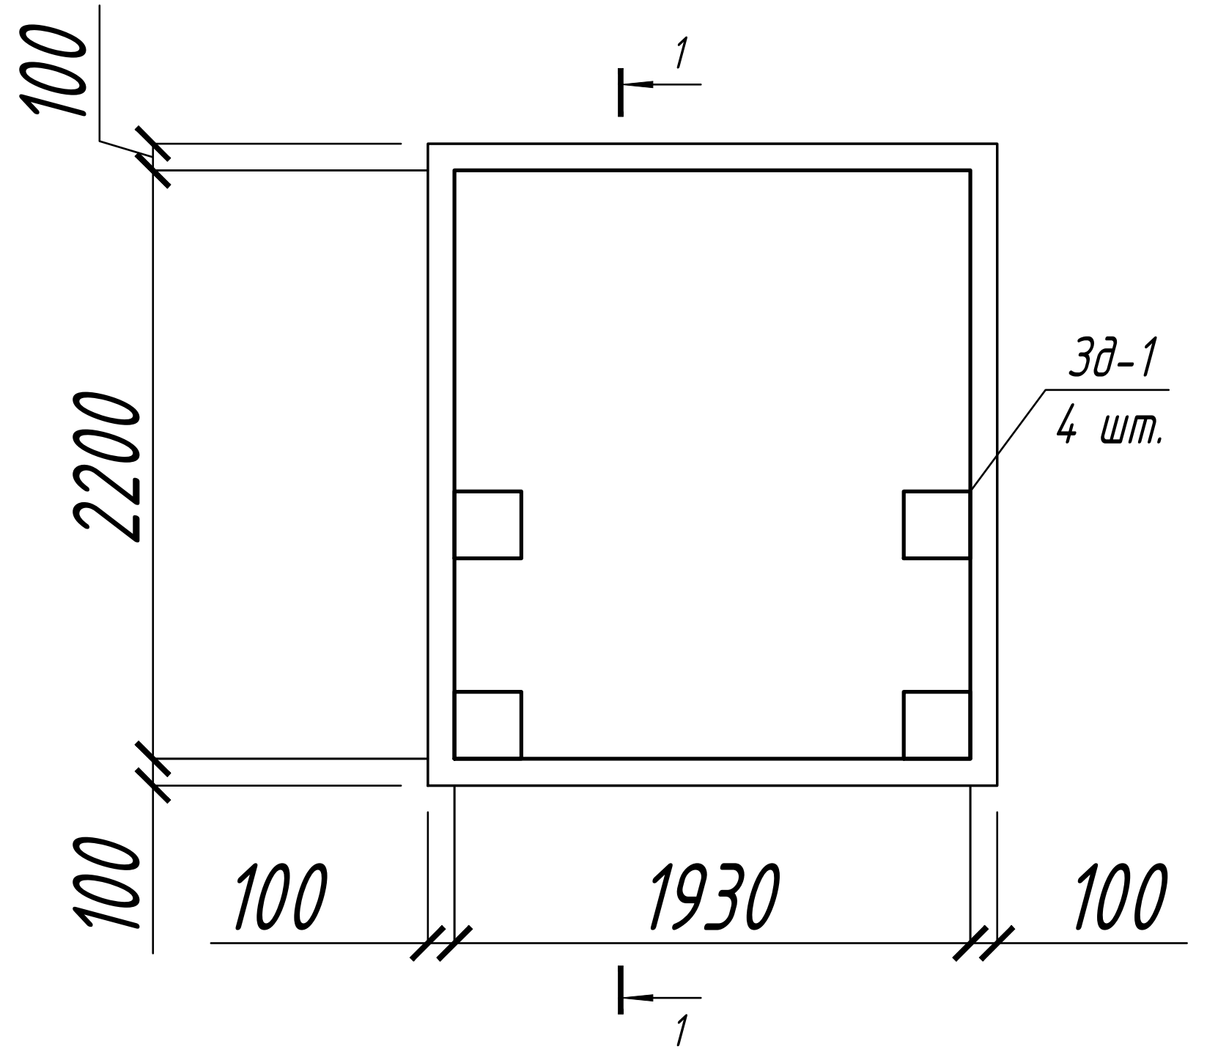
100
2200
100
1
1
Зд-1
4 шт.
100
1930
100

Фундамент Фм 8

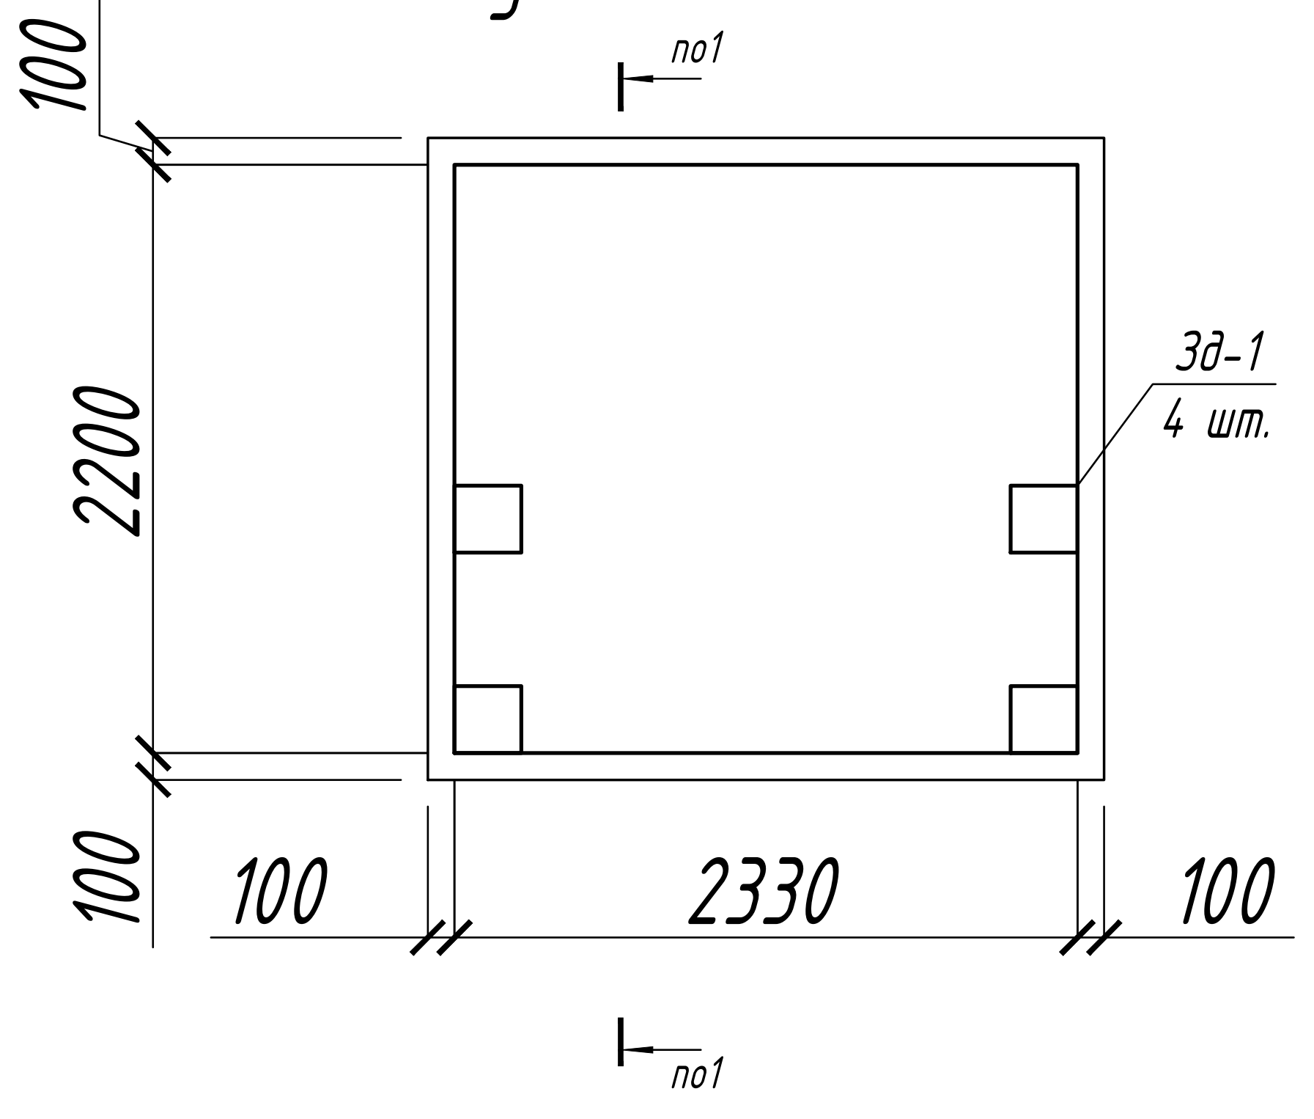
100
2200
100
по1
по1
Зд-1
4 шт.
100
2330
100

Фундамент Фм 9

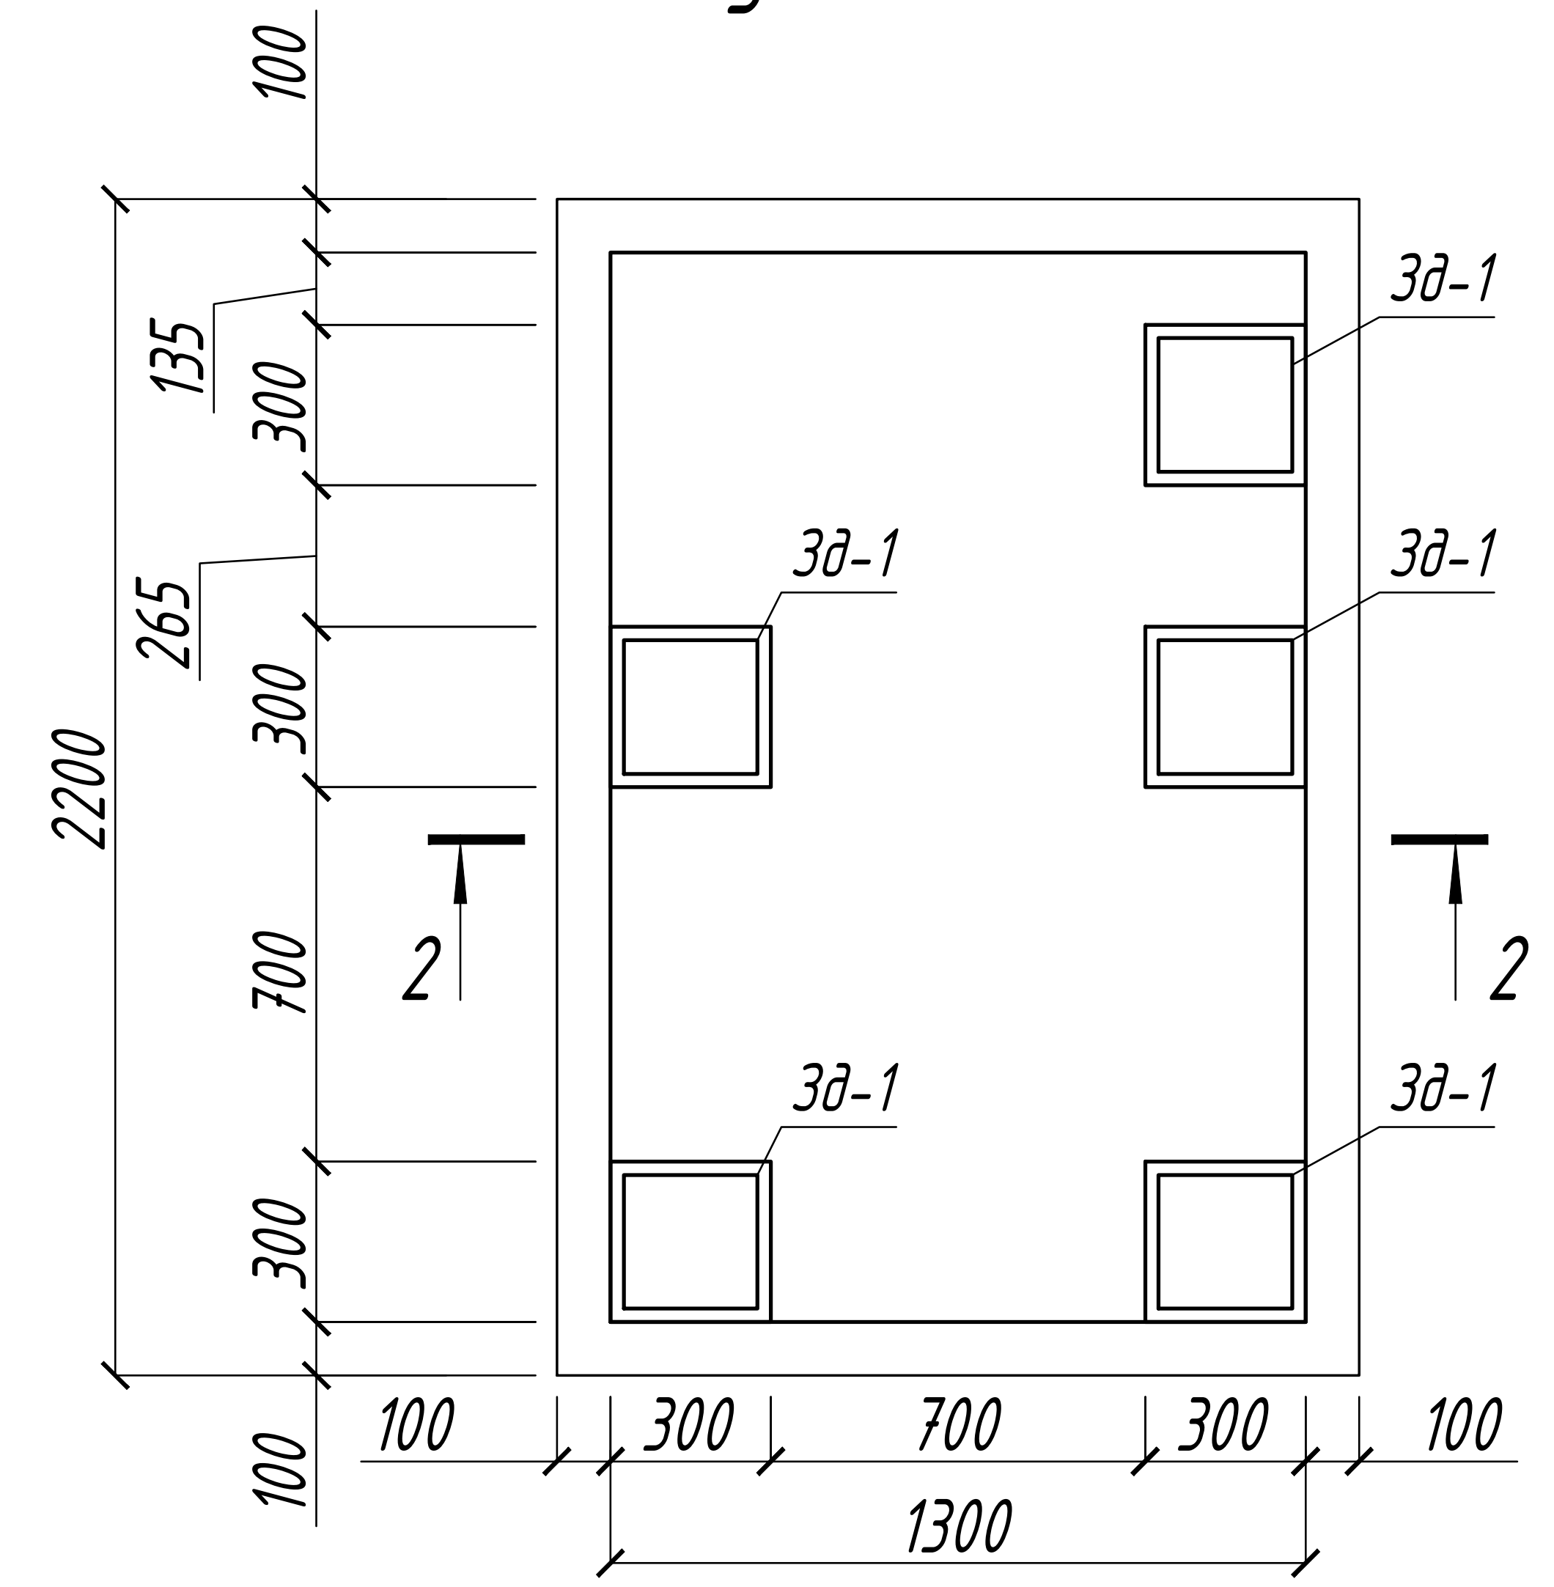
100
135
300
265
300
2200
700
300
100
Зд-1
Зд-1
Зд-1
Зд-1
Зд-1
2
2
100
300
700
300
100
1300

Сетка С 1

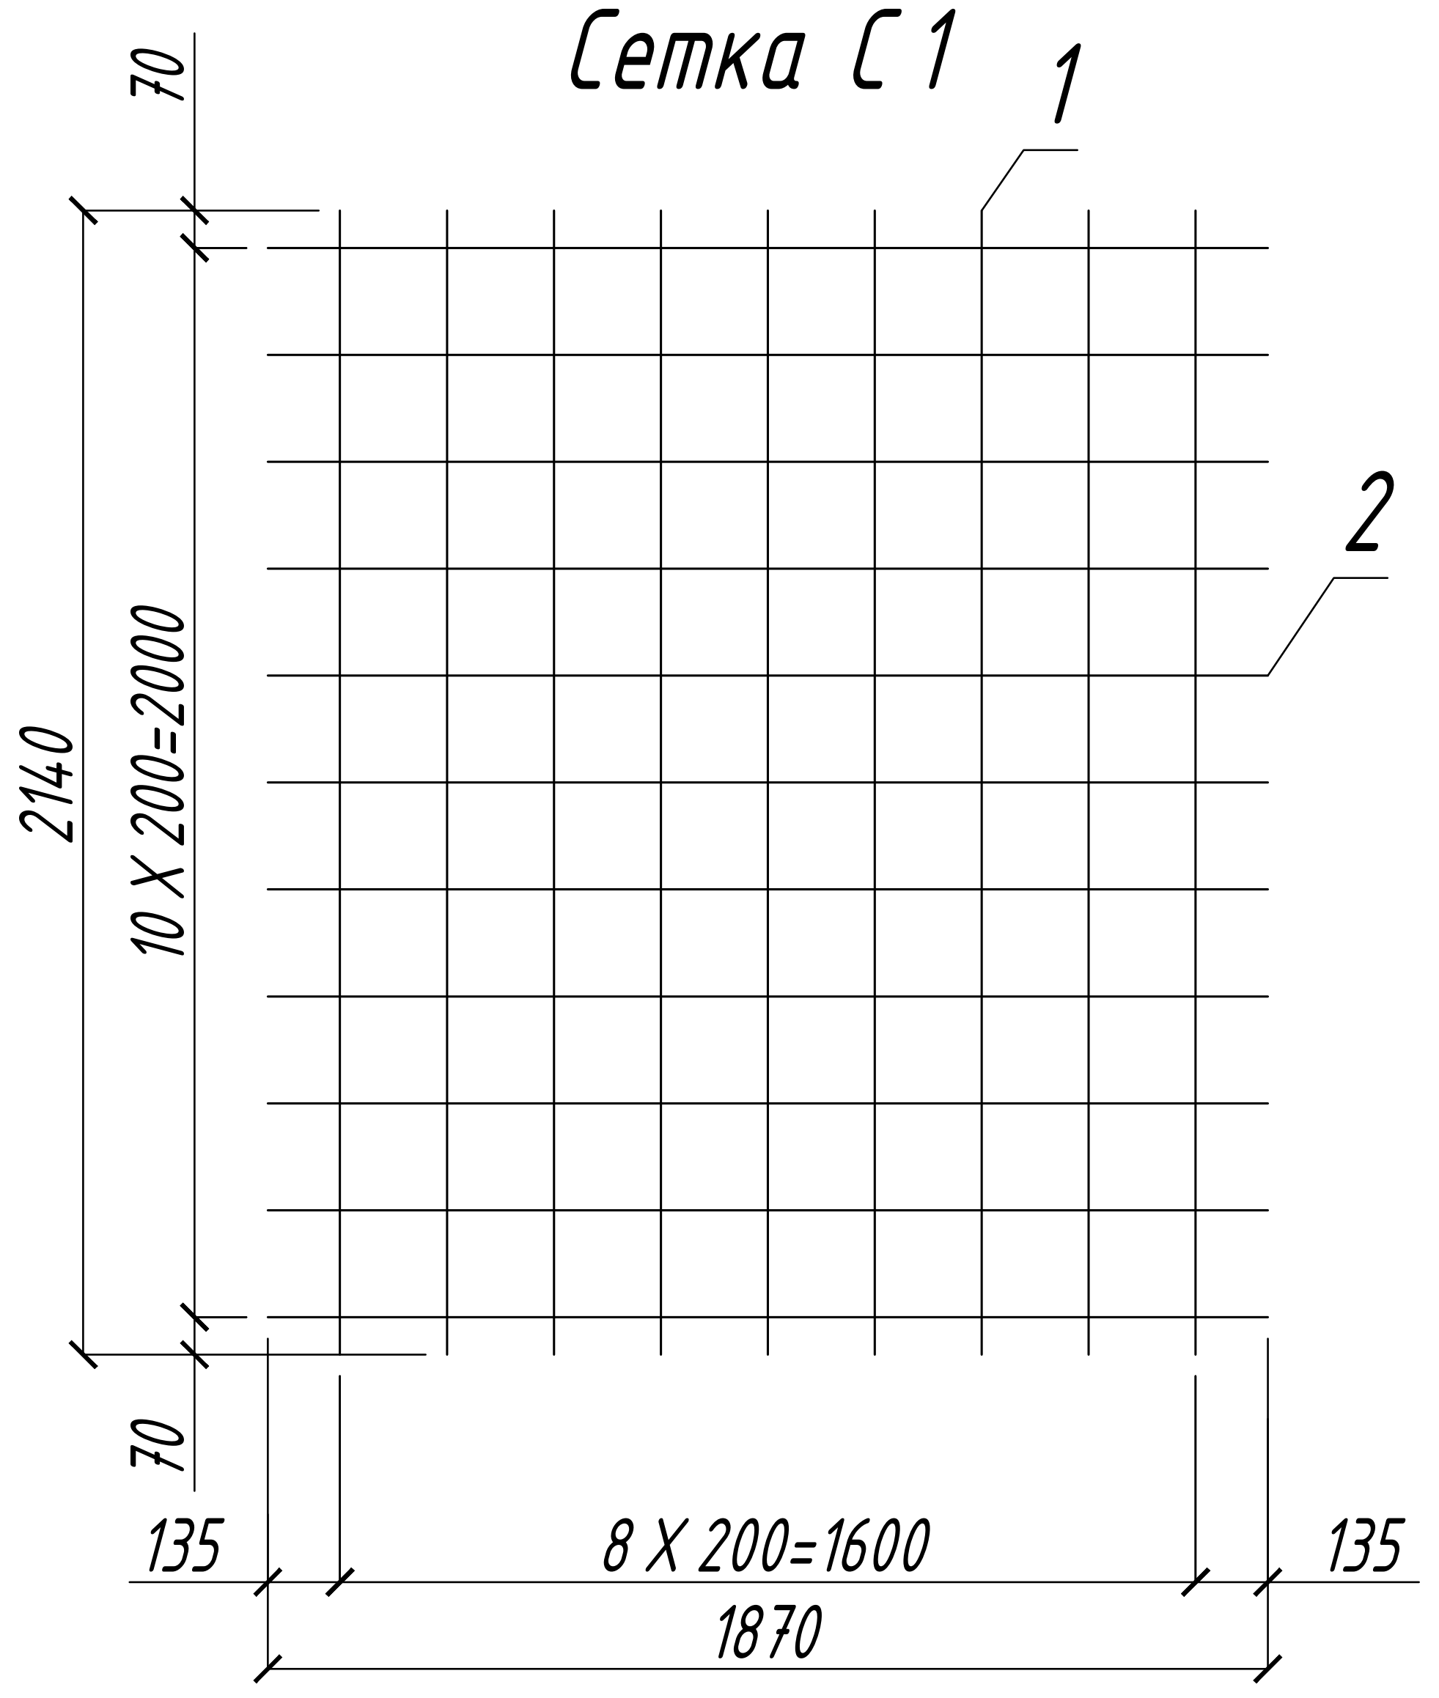
1
2
70
2140
10 X 200=2000
70
135
8 X 200=1600
135
1870

Сетка С 2

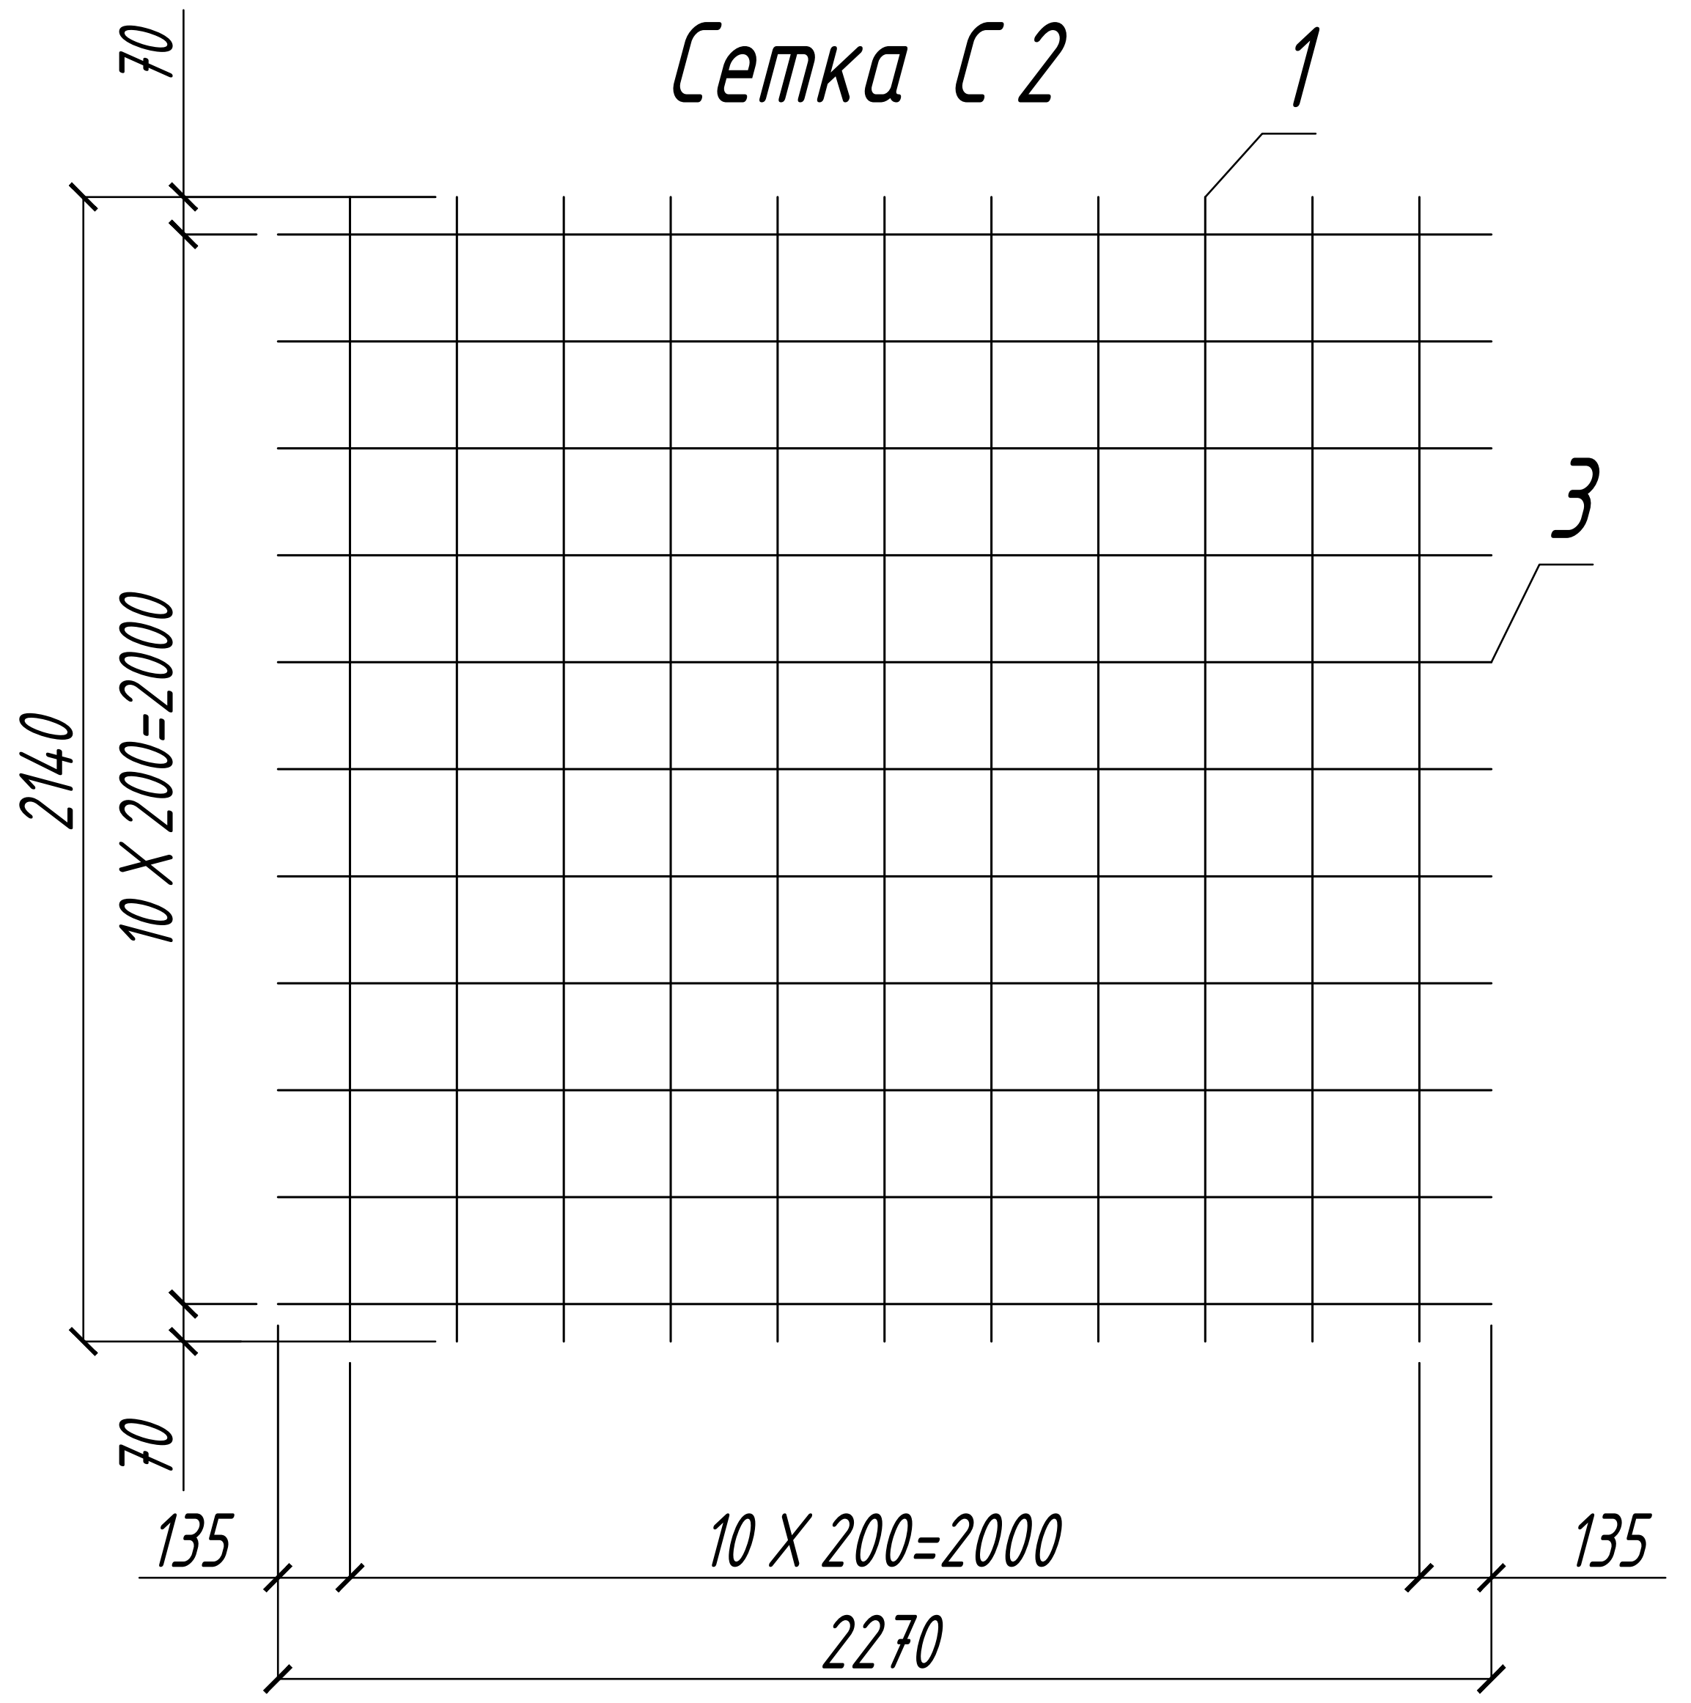
1
3
70
2140
10 X 200=2000
70
135
10 X 200=2000
135
2270

Разрез 1-1

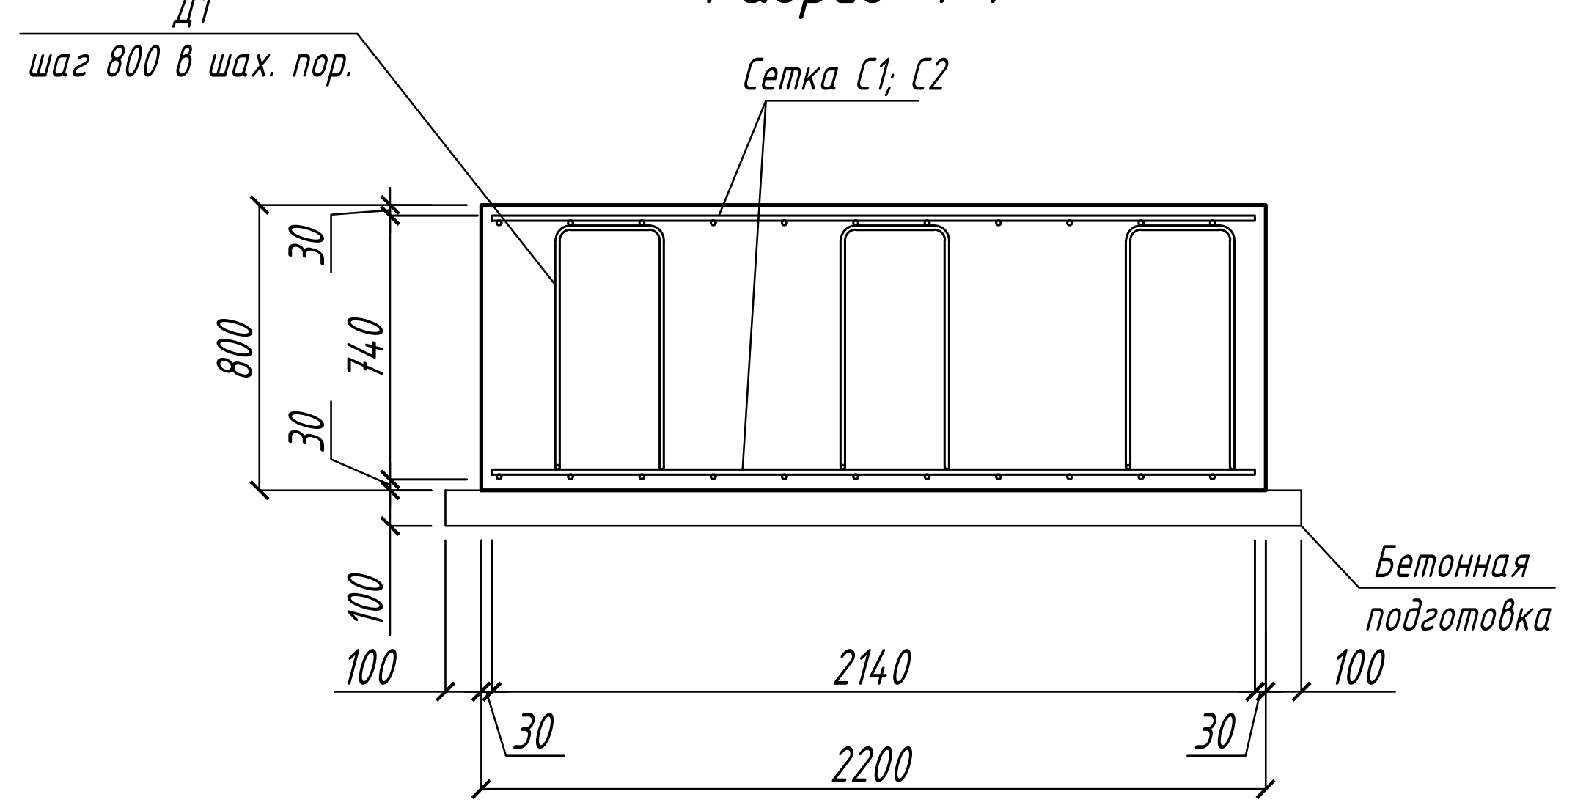
Д1
шаг 800 в шах. пор.
Сетка С1; С2
30
800
740
30
100
Бетонная
подготовка
100
2140
100
30
30
2200

Сетка С 3

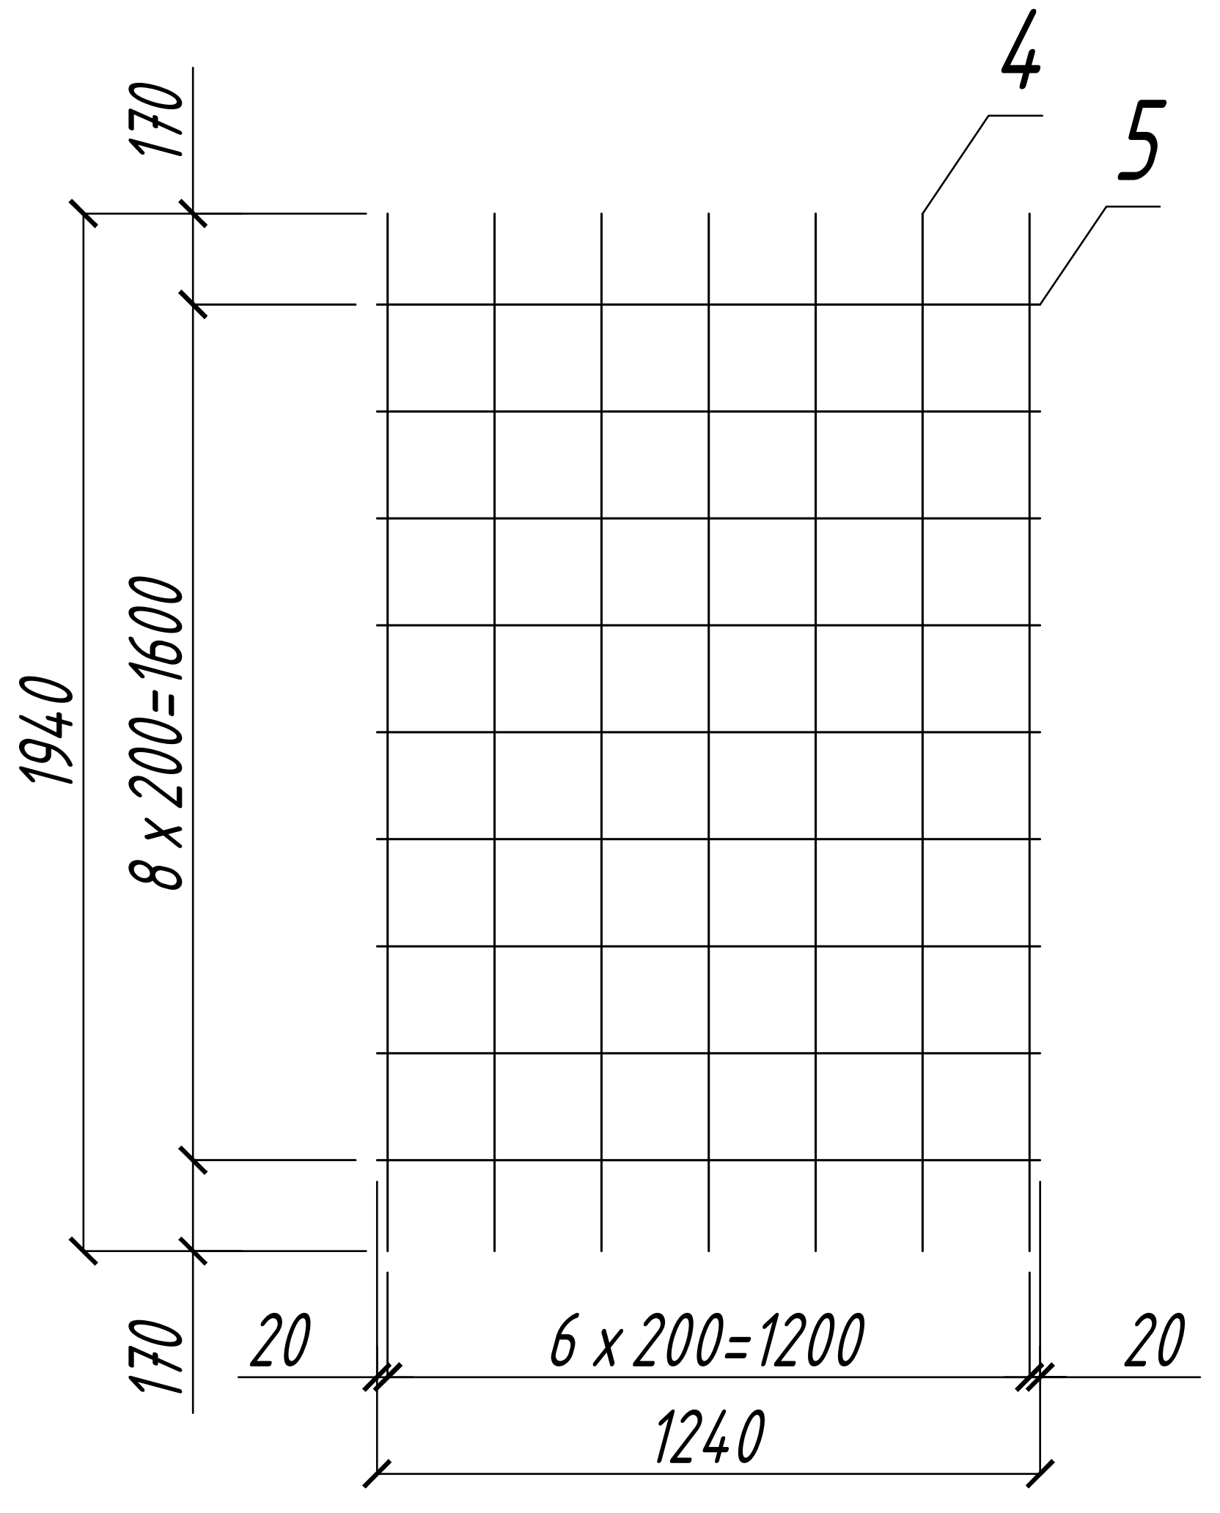
4
5
170
1940
8 x 200=1600
170
20
6 x 200=1200
20
1240

Разрез 2-2

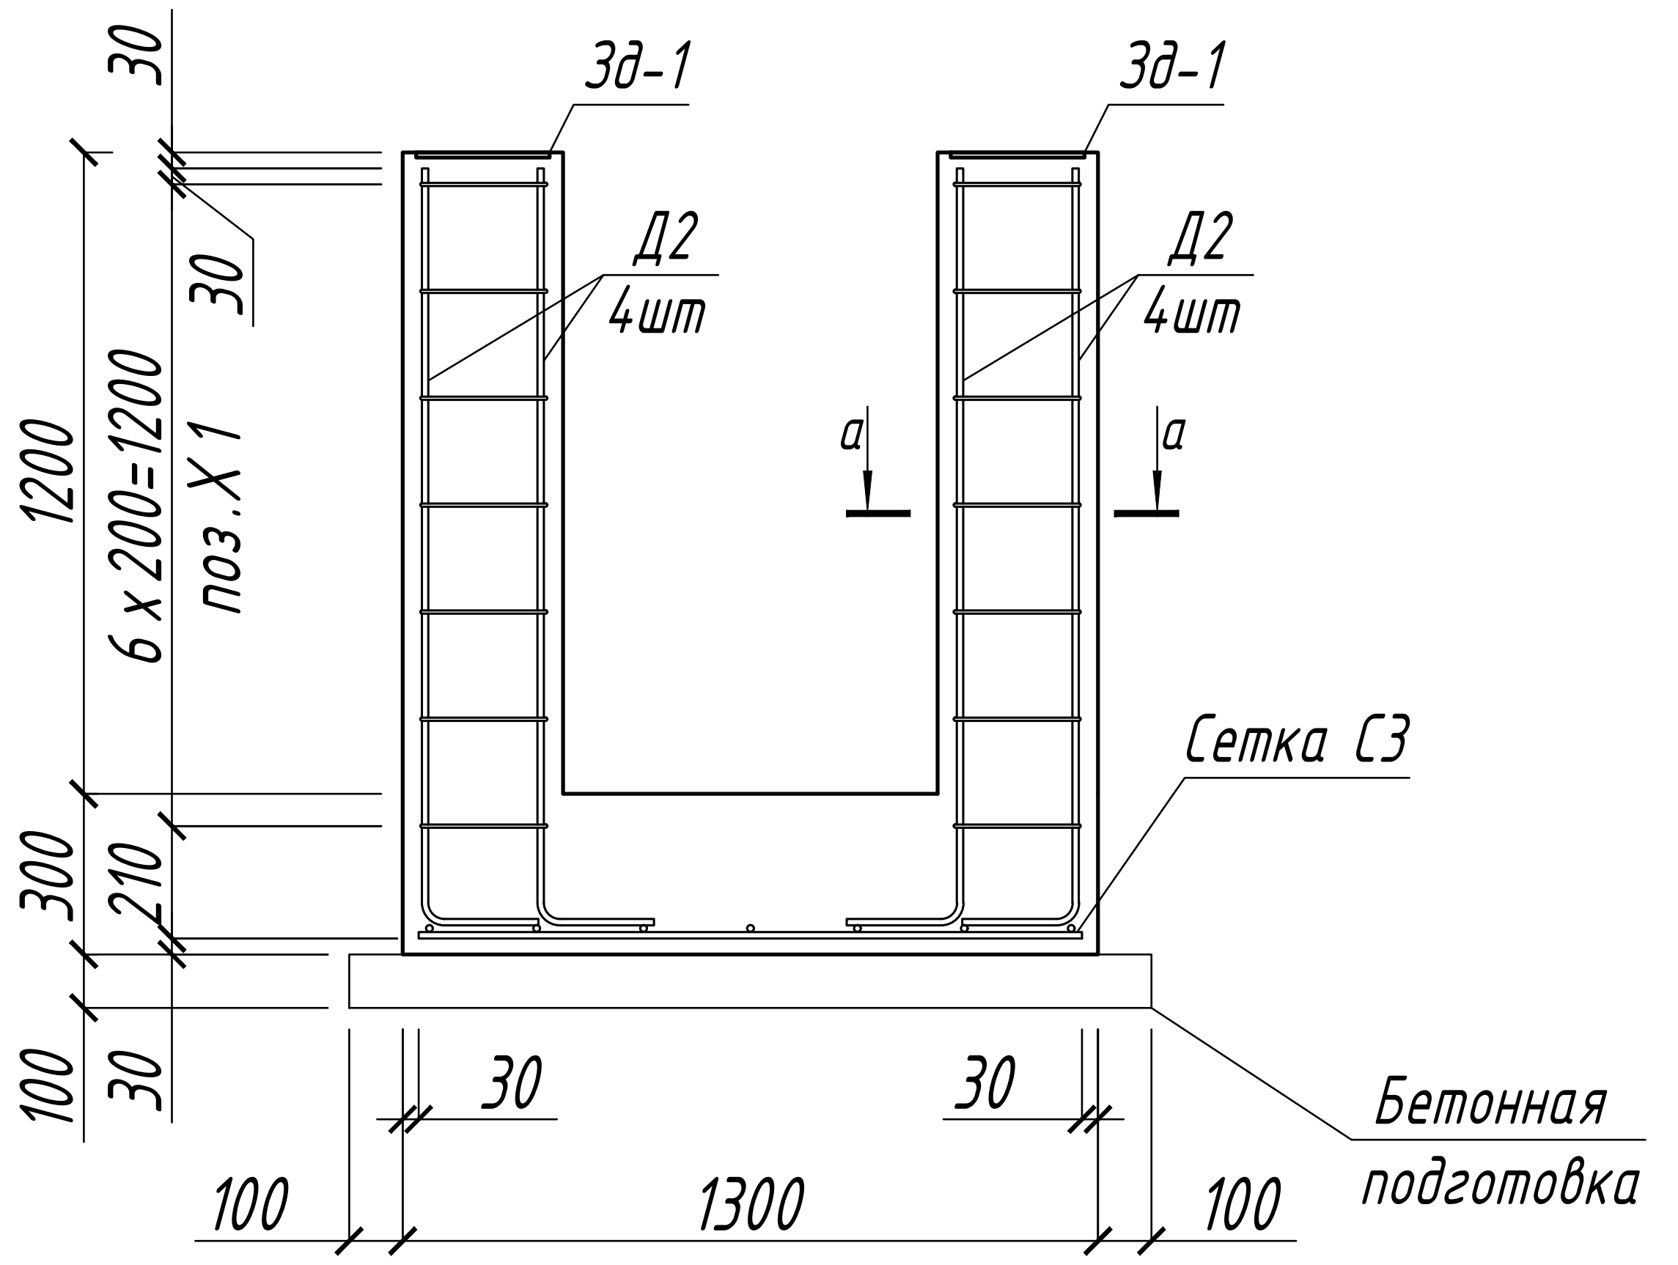
30
Зд-1
Зд-1
30
Д2
4шт
Д2
4шт
1200
6 x 200=1200
поз. X 1
а
а
Сетка С3
300
210
100
30
30
30
Бетонная
подготовка
100
1300
100

а -а

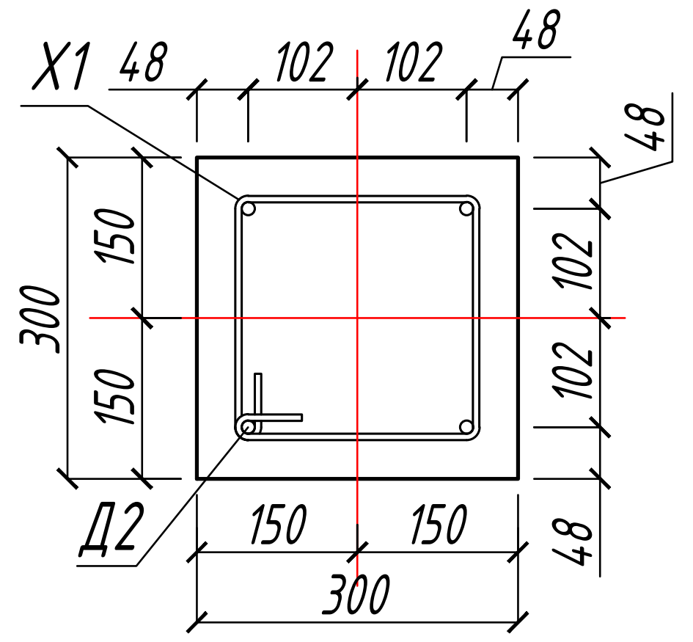
X1
48
102
102
48
48
300
150
150
102
102
48
Д2
150
150
300

Спецификация элементов

Марка Поз.	Обозначение	Наименование		Кол. шт	Масса ед., кг	Прим.
		Фундамент Фм 7 (на 1 шт.)				
		Сборочные единицы				
С 1	см. данный лист	Горизонтальная сетка С 1		2	17.09	34.18
Зд -1	см. данный лист	Закладная деталь Зд -1		4	6.05	24.18
		Детали				
Д 1	см. данный лист	ГОСТ 34028-2016 Ø12 А500	L=2160 мм	8	1.92	15.33
		Сетка С 1				
1	см. данный лист	ГОСТ 34028-2016 Ø12 А400	L=2140 мм	9	1.90	17.09
2	см. данный лист	ГОСТ 34028-2016 Ø12 А400	L=1870 мм	11	1.66	18.25
		Закладная деталь Зд -1				
Л 1	см. данный лист	ГОСТ 19903-2015 -t10 250x250		1	4.91	4.91
Г 2	см. данный лист	ГОСТ 34028-2016 Ø12 А400	L=320 мм	4	0.28	1.14
		Материал				
	см. данный лист	ГОСТ 26633-2010 Бетон В 25		1.3		м^3
	см. данный лист	ГОСТ 26633-2010 Бетон В 7.5		0.2		м^3
		Фундамент Фм 8 (на 1 шт.)				
		Сборочные единицы				
С 2	см. данный лист	Горизонтальная сетка С 2		2	20.89	41.78
Зд -1	см. данный лист	Закладная деталь Зд -1		4	6.05	24.18
		Детали				
Д 1	см. данный лист	ГОСТ 34028-2016 Ø12 А400	L=2160 мм	8	1.92	15.33
		Сетка С 2				
1	см. данный лист	ГОСТ 34028-2016 Ø12 А400	L=2140 мм	11	1.90	20.89
3	см. данный лист	ГОСТ 34028-2016 Ø12 А400	L=2270 мм	11	2.01	22.16
		Закладная деталь Зд -1				
Л 1	см. данный лист	ГОСТ 19903-2015 -t10 250x250		1	4.91	4.91
Г 2	см. данный лист	ГОСТ 34028-2016 Ø12 А400	L=320 мм	4	0.28	1.14
		Материал				
	см. данный лист	ГОСТ 26633-2010 Бетон В 25		1.6		м^3
	см. данный лист	ГОСТ 26633-2010 Бетон В 7.5		0.2		м^3

Спецификация элементов

Марка Поз.	Обозначение	Наименование		Кол. шт	Масса ед., кг	Прим.
		Фундамент Фм 9 (на 1 шт.)				
		Сборочные единицы				
С 3	см. данный лист	Горизонтальная сетка С 3		1	12.05	12.05
Зд -1	см. данный лист	Закладная деталь Зд -1		5	6.05	30.23
		Детали				
Д 2	см. данный лист	ГОСТ 34028-2016 Ø12 А400	L=1640 мм	20	1.46	29.11
X1	см. данный лист	ГОСТ 34028-2016 Ø6 А240	L=1020 мм	35	0.23	7.92
		Сетка С 3				
4	см. данный лист	ГОСТ 34028-2016 Ø12 А400	L=1940 мм	7	1.72	12.05
5	см. данный лист	ГОСТ 34028-2016 Ø12 А400	L=1240 мм	9	1.10	9.90
		Закладная деталь Зд -1				
Л 1	см. данный лист	ГОСТ 19903-2015 -t10 250x250		1	4.91	4.91
Г 2	см. данный лист	ГОСТ 34028-2016 Ø12 А400	L=320 мм	4	0.28	1.14
		Материал				
	см. данный лист	ГОСТ 26633-2010 Бетон В 25		1.4		м^3
	см. данный лист	ГОСТ 26633-2010 Бетон В 7.5		0.2		м^3

Ведомость деталей

Поз.	Эскиз
Д 1	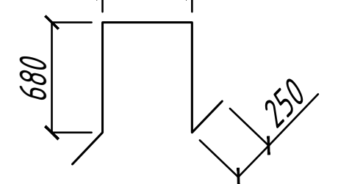
Д 2	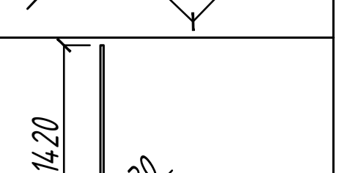 1420 R30 220
X 1	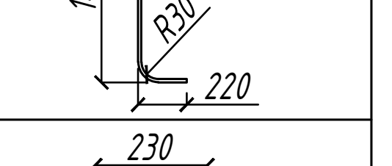 230 230 50 50

Все размеры даны по внешнем граням детали

Примечание

1. Общие данные смотреть на листе EWE0426-MGL1-STR-054-COM-690501-A1
2. Отметки верха фундамента смотреть на листе EWE0426-MGL1-STR-054-DRW-690502-A1
3. Под монолитным фундаментом выполнить подготовку из бетона кл. В 7.5 толщиной 100 мм с уширением на 100 мм в каждую сторону от размеров подошвы фундамента. Под ним выполнить подготовку из щебня, вдавленного в грунт, толщиной 100 мм, с проливкой горячим битумом с выступом за боковые грани бетонной подготовки по 100 мм в каждую сторону.

Рев.	Дата	Назначение ревизии	Проверил	Утвердил
A1	10.10.26	Утверждено для строительства		
R1	20.09.26	Выпущено для рассмотрения		

ЗАКАЗЧИК: UTG UZTRANSGAZ «TRANSGAZINJINIRING»
ГЕНЕРАЛЬНЫЙ ПОДРЯДЧИК: UET UZBEKENERGOTAMIR
ПОДРЯДЧИК: PBG Pro Build Generation
ГЕНЕРАЛЬНЫЙ ПРОЕКТИРОВЩИК: EAST WEST ENGINEERING

EWE0426-MGL1-STR-054-DRW-690505-A1

«СТРОИТЕЛЬСТВО НОВЫХ НИТОК (УЧАСТКОВ) ГАЗОПРОВОДОВ «ГАЗЛИ - САРИМОЙ» И «АКЧАЛОК - ГАЗЛИ - НУКУС» ОБЩЕЙ ПРОТЯЖЕННОСТЬЮ НЕ МЕНЕЕ 275 КМ».

Изм.	Кол.уч.	Лист	№ док.	Подп.	Дата
ГИП		Кирпичников			10.26
Нач.отдела		Каршиев			10.26
Разраб.		Мамешов			10.26
Проверил		Каршиев			10.26
Н. контр.		Кирпичников			10.26

ГАЗОПРОВОД "ГАЗЛИ-САРИМОЙ" (54 КМ)

Стадия	Лист	Листов
РД	1	1

Фундаменты Фм 7; Фм 8; Фм 9

EAST WEST ENGINEERING
ООО "EAST-WEST Engineering"
г. Ташкент 2026г.

Формат А3х3

Взам. инв.N
Подп. и дата
Инв.N подл.