Фундамент Фм 10

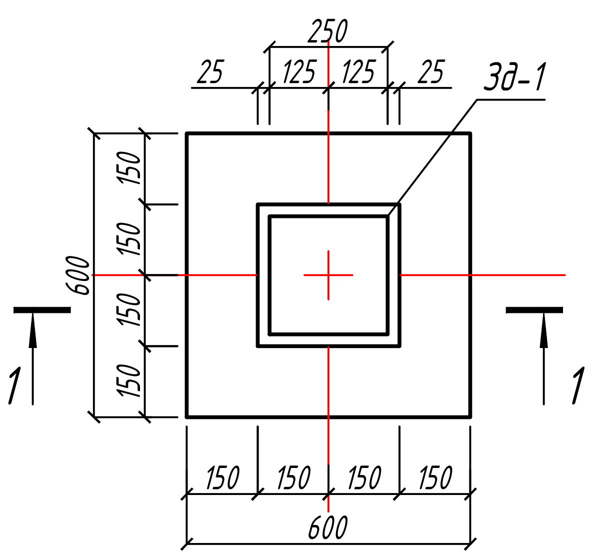

а - а

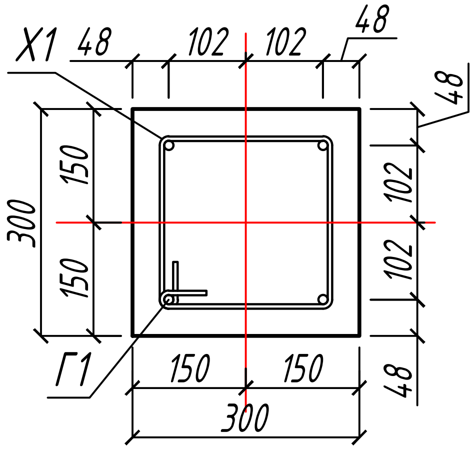

Закладная деталь Зд-1

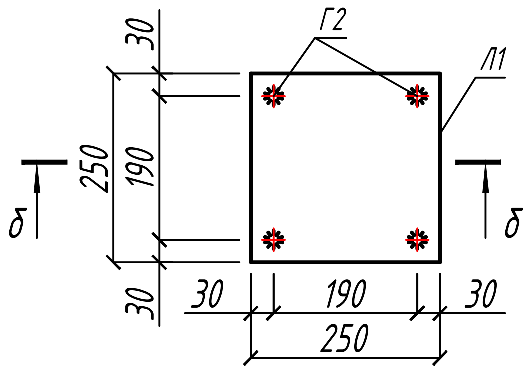

б - б

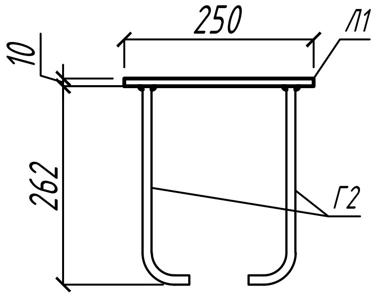

Разрез 1-1

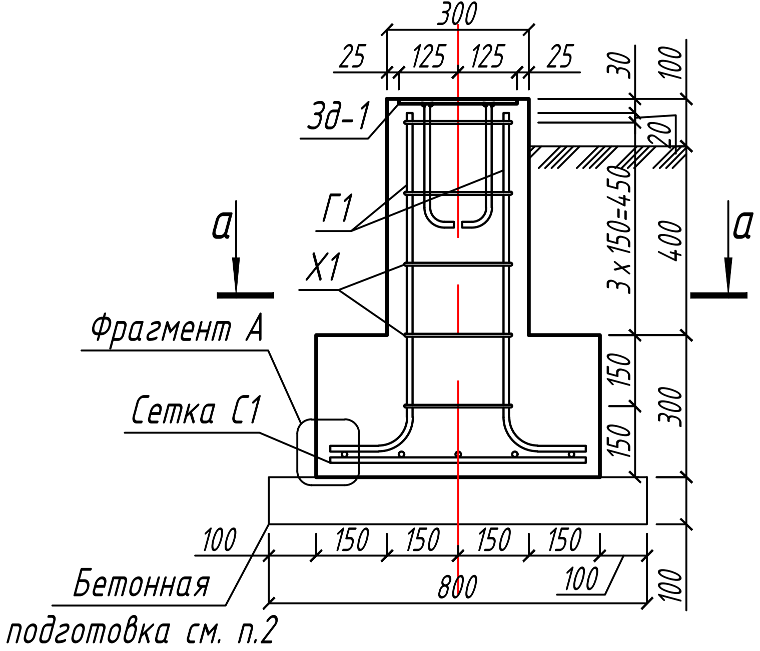

Сетка горизонтальная С1

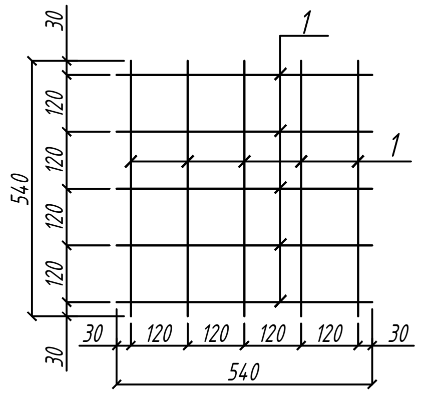

Ведомость деталей

Поз.	Эскиз
Г1	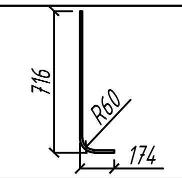
Г2	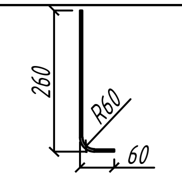
Х1	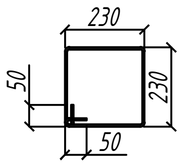

Все размеры даны по внешнем граням детали

Спецификация элементов

Марка Поз.	Обозначение	Наименование		Кол. шт	Масса ед., кг	Прим.
		Фундамент Фм 10 (на 1 шт.)				
		Сборочные единицы				
С 1	см. данный лист	Горизонтальная сетка С 1		1	4.79	4.79
Зд -1	см. данный лист	Закладная деталь Зд -1		1	6.05	6.05
		Детали				
Г 1	см. данный лист	ГОСТ 34028-2016 Ø12 А400	L=890 мм	4	0.79	3.16
Х 1	см. данный лист	ГОСТ 34028-2016 Ø6 А240	L=1020 мм	5	0.23	1.13
		Сетка С 1				
1	см. данный лист	ГОСТ 34028-2016 Ø12 А400	L=540 мм	10	0.48	4.79
		Закладная деталь Зд -1				
Л 1	см. данный лист	ГОСТ 19903-2015 -t10 250x250		1	4.91	4.91
Г 2	см. данный лист	ГОСТ 34028-2016 Ø12 А400	L=320 мм	4	0.28	1.14
		Материал				
	см. данный лист	ГОСТ 26633-2010 Бетон В 25		0.2		$м^3$
	см. данный лист	ГОСТ 26633-2010 Бетон В 7.5		0.1		$м^3$

Примечание

1. Общие данные смотреть на листе EWE0426-MGL1-STR-054-COM-690501-A1
2. Под монолитным фундаментом выполнить подготовки из бетона кл. В 7.5 толщиной 100 мм с уширением на 100 мм в каждую сторону от размеров подошвы фундамента. Под ним выполнить подготовку из щебня, вдавленного в грунт, толщиной 100 мм, с проливкой горячим битумом с выступом за боковые грани бетонной подготовки по 100 мм в каждую сторону.

Рев.	Дата	Назначение ревизии	Проверил	Утвердил
A1	10.10.26	Утверждено для строительства		
R1	20.09.26	Выпущено для рассмотрения		

ЗАКАЗЧИК: UTG UZTRANSGAZ

ГЕНЕРАЛЬНЫЙ ПОДРЯДЧИК: UET UZBEKENERGOTAMIR

ПОДРЯДЧИК: PBG Pro Build Generation

ГЕНЕРАЛЬНЫЙ ПРОЕКТИРОВЩИК: EAST WEST ENGINEERING

EWE0426-MGL1-STR-054-DRW-690506-A1

«СТРОИТЕЛЬСТВО НОВЫХ НИТОК (УЧАСТКОВ) ГАЗОПРОВОДОВ «ГАЗЛИ - САРИМОЙ» И «АКЧАЛОК - ГАЗЛИ - НУКУС» ОБЩЕЙ ПРОТЯЖЕННОСТЬЮ НЕ МЕНЕЕ 275 КМ».

Изм.	Кол.уч.	Лист	№ док.	Подп.	Дата
ГИП		Кирпичников			10.26
Нач.отдела		Каршиев			10.26
Разраб.		Мамешов			10.26
Проверил		Каршиев			10.26
Н. контр.		Кирпичников			10.26

ГАЗОПРОВОД "ГАЗЛИ-САРИМОЙ" (54 КМ)

Стадия	Лист	Листов
РД	1	1

Фундаменты Фм 10

EAST WEST ENGINEERING
ООО "EAST-WEST Engineering"
г. Ташкент 2026г.

Формат А3

Взам.инв.N

Подп. и дата

Инв.N подл.