


Стойка Ст 1

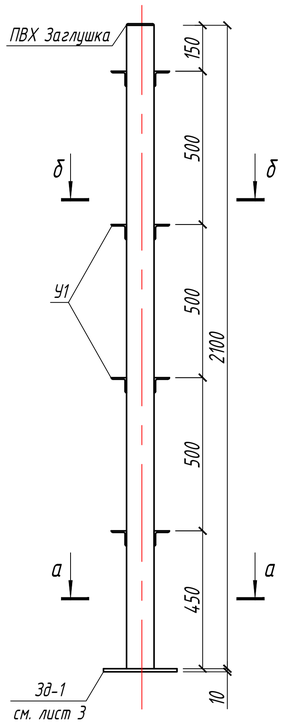

а-а

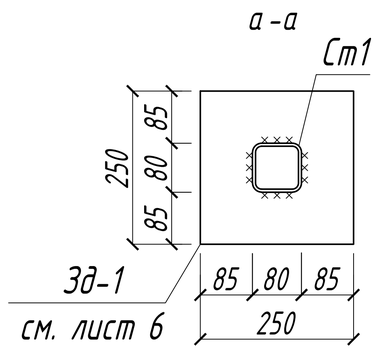


Узел А

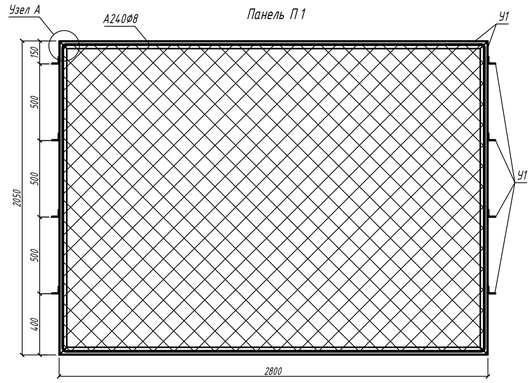

Панель П1

Панель П2
(калитка)

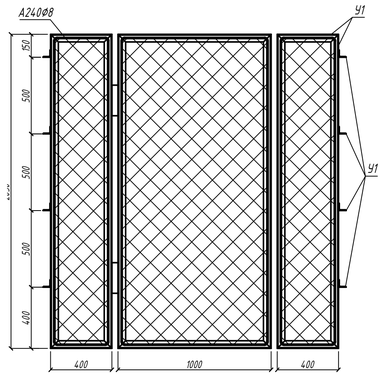


Наименование элемента	Эскиз	Поз.	Состав	Q, тс	N, тс	M, тс*м	Марка металла	
Ст 1	□		80х80х5				С255	
Ст 2	□		80х80х5				С255	
Ст 3	□		100х100х5				С255	
Ст 4	□		80х80х5				С255	
	[		14 П				С255	
У 1	∟		50х50х4				С255	
У 2	∟		100х100х6				С255	
2			-14				С255	
3			-110				С255	


Спецификация элементов

Марка Поз.	Обозначение	Наименование		Кол. шт	Масса ед., кг	Прим.
		Детали				
	см. данный лист	ГОСТ 34028-2016 Ø8 А240	L=1000 мм	74.3	0.39	293.03


Панель П3
(ворота)

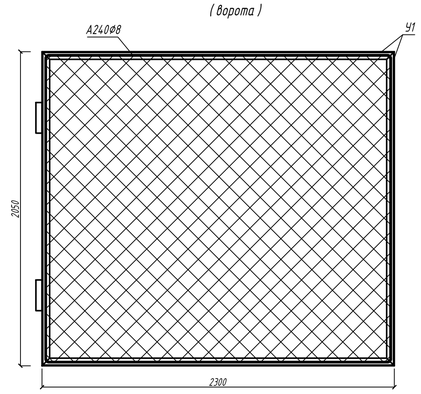

Узел А

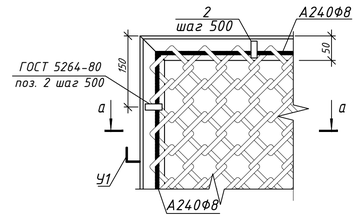

а-а

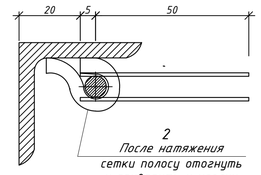


Спецификация металлопроката


Наименование профиля ГОСТ, ТУ	Наименование или марка металла ГОСТ, ТУ	Обозначение и размер профиля, мм	N п.п.	Масса металла по элементам конструкций, т				Общая масса, т
				Стойки	Ограждение	Площадки	Прочее	
1	2	3	4	5	6	7	8	9
Гнутые замкнутые сварные профили квадратного сечения	С 255 ГОСТ 27772-2015	100 х 5	1	0.08				
		80 х 5	2	2.00		0.51		
		40 х 4	3			0.13		
Всего профиля			4	2.080		0.640		2.72
Уголки стальные горячекатаные равнополочные ГОСТ 8509-93	С 255 ГОСТ 27772-2015	∟ 50 х 5	5	0.19	3.26	0.08		
		∟ 100 х 6	6	0.05	0.58			
Всего профиля			7	0.24	3.84	0.08		4.16
Швеллеры стальные горячекатаные ГОСТ 8240-97	С 255 ГОСТ 27772-2015	П 14	8	0.06		0.06		
Всего профиля			9	0.06		0.06		0.12
Трубы стальные электросварные прямошовные ГОСТ 10704-91	С 255 ГОСТ 27772-2015	Ø16	10			0.01		
Всего профиля			11			0.01		0.01
Прокат листовой горячекатаный ГОСТ 19903-2015	С 255 ГОСТ 27772-2015	t5	12			0.16		
		t4	13		0.05			
Всего профиля			14		0.05	0.16		0.21
Всего масса			15	2.33	0.63	0.87		3.83

Техническая спецификация подсчитана без учета добавления к общей массе : 1% наплавленного


Стойка Ст 3

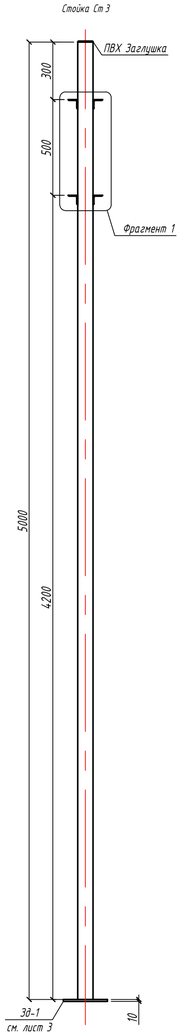


Стойка Ст 4

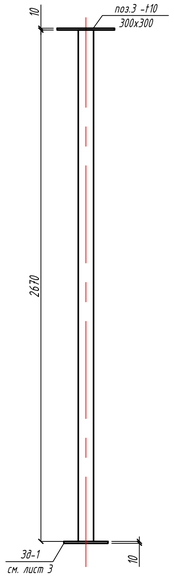


Стойка Ст 2

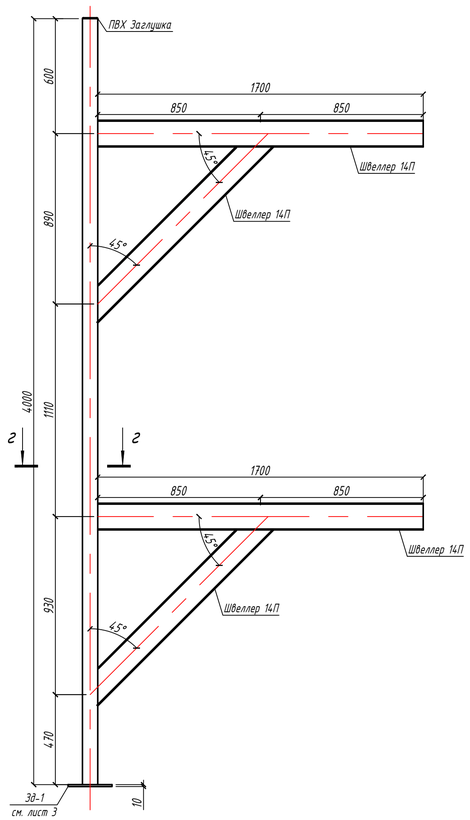


Панель П4

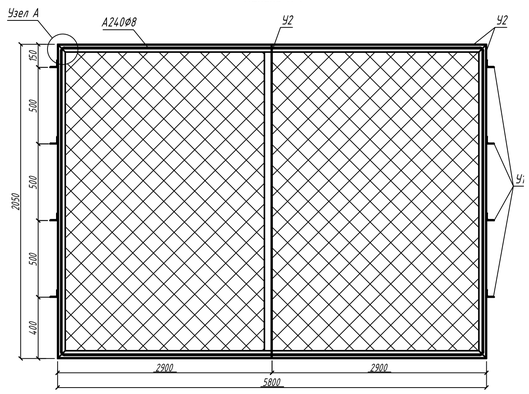


Фрагмент 1

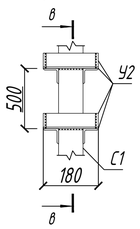


в-в

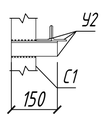


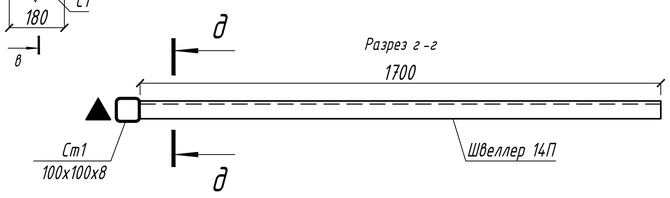

Панель П5

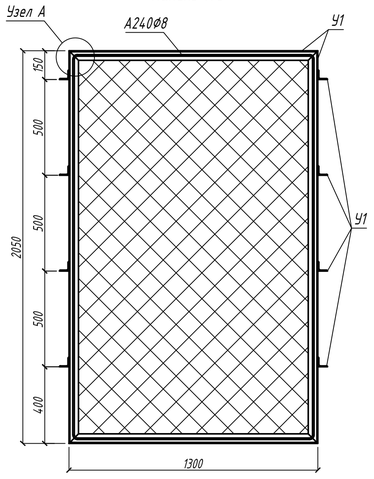

Разрез д-д

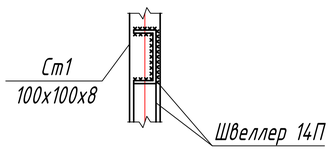

▲ - Ориентация сечения колонны

Примечание

1. Общие данные смотреть на листе EWE0426-MGL1-STR-054-COM-690501-A1
2. Сварку производить электродами типа Э42А по ГОСТ 9467-75. Высоту швов принять равной наименьшей толщине свариваемых элементов, длину - по длине примыкания. Длину шва выполнять по всей длине свариваемых элементов.

Изм.	Дата	Назначение ревизии	Проверил	Утвердил
А1	10.10.26	Утверждено для строительства		
R1	20.09.26	Выпущено для рассмотрения		

ЗАКАЗЧИК: UTG | ГЕНЕРАЛЬНЫЙ ПОДРЯДЧИК: UET | ПОДРЯДЧИК: PBG | ГЕНЕРАЛЬНЫЙ ПРОЕКТИРОВЩИК: EAST WEST ENGINEERING

Изм.	Кол.уч.	Лист	№ док.	Подп.	Дата
ГИП		Кирпичников			10.26
Нач.отдела		Каршиев			10.26
Разраб.		Мамешов			10.26
Проверил		Каршиев			10.26
Н. контр.		Кирпичников			10.26

EWE0426-MGL1-STR-054-DRW-690507-A1

«СТРОИТЕЛЬСТВО НОВЫХ НИТОК (УЧАСТКОВ) ГАЗОПРОВОДОВ «ГАЗЛИ - САРИМОЙ» И «АКЧАЛОК - ГАЗЛИ - НУКУС» ОБЩЕЙ ПРОТЯЖЕННОСТЬЮ НЕ МЕНЕЕ 275 КМ».

ГАЗОПРОВОД "ГАЗЛИ-САРИМОЙ" (54 КМ)

Стадия	Лист	Листов
РД	1	1

Стойка Ст 1, Ст 2, Ст 3, Ст 4

ООО "EAST-WEST Engineering" г. Ташкент 2026г.

Формат А1

Взам. инв. N | Подп. и дата | Инв. N подл.