

Площадка П1

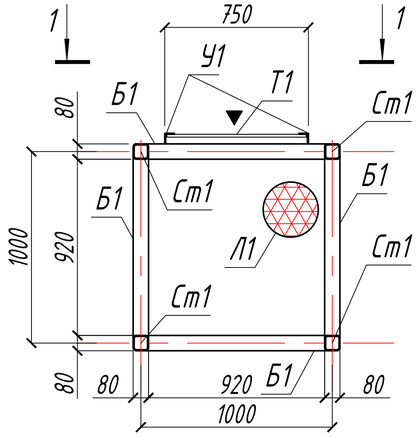

Разрез 1-1

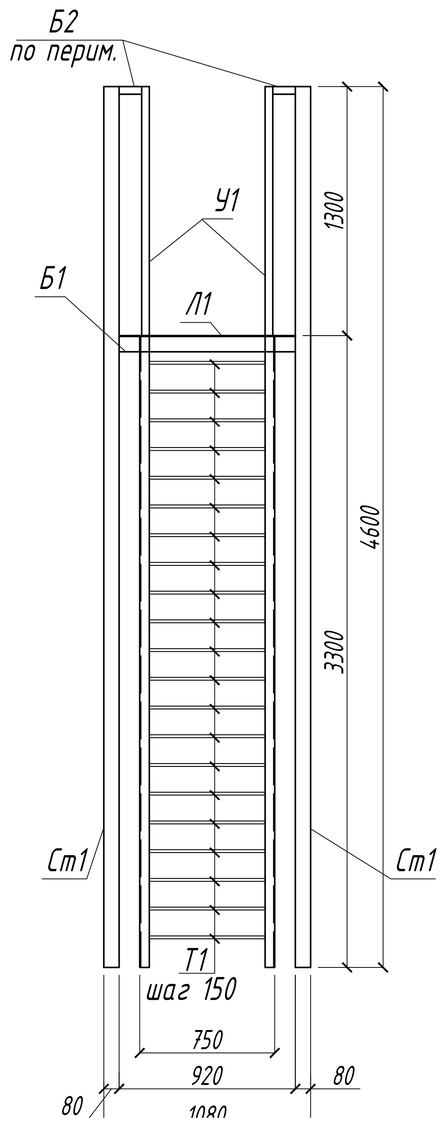

Ведомость элементов

Марка элемента	Сечение			Усилие для прикрепления			Наименование или марка металла	Примечание
	Эскиз	Поз.	Состав	Q, тс	N, тс	M, тс*м		
Ст 1	□		80х80х5				С255	
Б 1	□		80х80х5				С255	
Б 2	□		40 х 40х4				С255	
У 1	∟		50х50х4				С255	
Т 1	○		⌀16				С255	
Л 1			-15				С255	Рифленный

▲ - Ориентация сечения колонны

Примечание

1. Общие данные смотреть на листе EWE0426-MGL1-STR-054-COM-690501-A1
2. Сварку производить электродами типа Э 42 А по ГОСТ 9467-75. Высоту швов принять равной наименьшей толщине свариваемых элементов, длину - по длине примыкания. Длину шва выполнять по всей длине свариваемых элементов.
2. Техническую спецификацию металла смотреть на листе EWE0426-MGL1-STR-054-DRW-690507-A1

Рев.	Дата	Назначение ревизии	Проверил	Утвердил
A1	10.10.26	Утверждено для строительства		
R1	20.09.26	Выпущено для рассмотрения		

ЗАКАЗЧИК: ГТС | ГЕНЕРАЛЬНЫЙ ПОДРЯДЧИК: UET | ПОДРЯДЧИК: PBG | ГЕНЕРАЛЬНЫЙ ПРОЕКТИРОВЩИК: EAST WEST ENGINEERING

Изм.	Кол.уч.	Лист	№ док.	Подп.	Дата
ГИП		Кирпичников			10.26
Нач.отдела		Каршиев			10.26
Разраб.		Мамешов			10.26
Проверил		Каршиев			10.26
Н. контр.		Кирпичников			10.26

EWE0426-MGL1-STR-054-DRW-690508-A1

«СТРОИТЕЛЬСТВО НОВЫХ НИТОК (УЧАСТКОВ) ГАЗОПРОВОДОВ «ГАЗЛИ - САРИМОЙ» И «АКЧАЛОК - ГАЗЛИ - НУКУС» ОБЩЕЙ ПРОТЯЖЕННОСТЬЮ НЕ МЕНЕЕ 275 КМ».

ГАЗОПРОВОД "ГАЗЛИ-САРИМОЙ" (54 КМ)

Стадия	Лист	Листов
РД	1	1

Площадка П1

ООО "EAST-WEST Engineering" г. Ташкент 2026г.

Взам. инв. N | Подп. и дата | Инв. N подл.

Формат А1