


Фундамент Ф 1

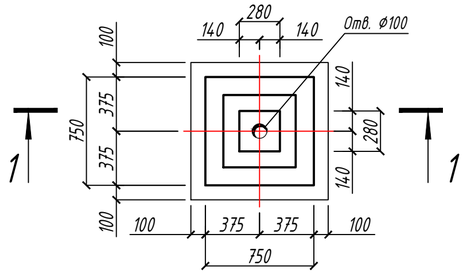


Фундамент Ф 2

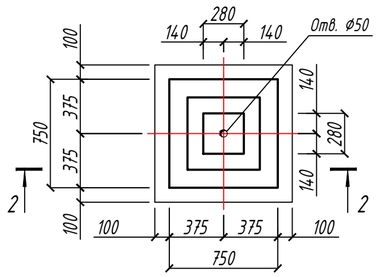


Разрез 1-1

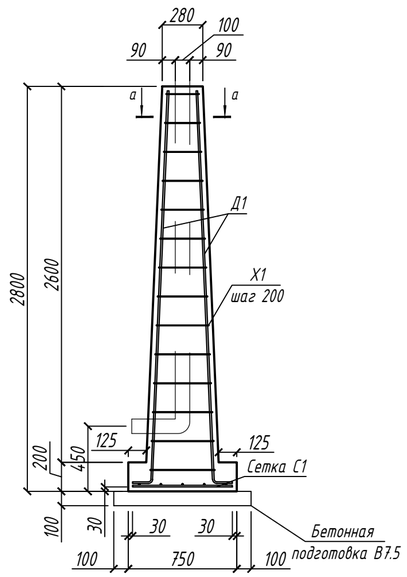


Разрез 2-2

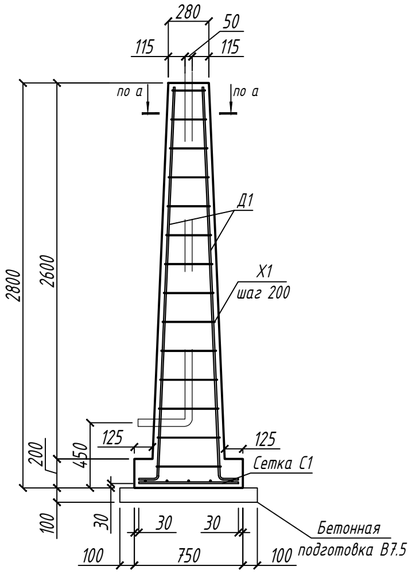


а-а

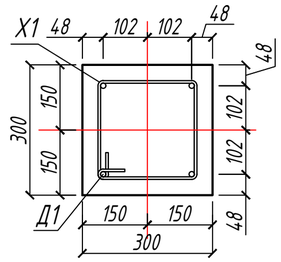





Сетка С 1

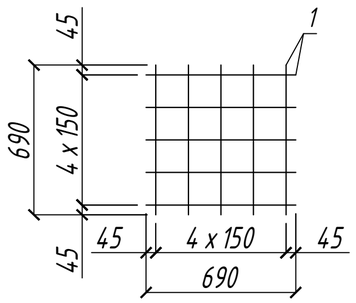

Сетка С 2

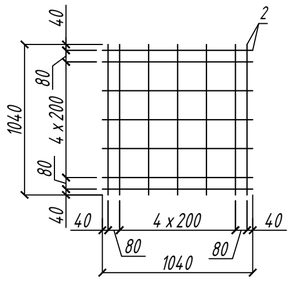


Ведомость деталей

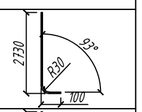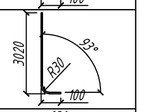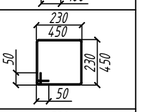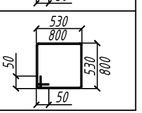
Поз.	Эскиз
Д 1	
Д 2	
X 1	
X 2	

Все размеры даны по внешнем граням детали

Фундамент Ф 3

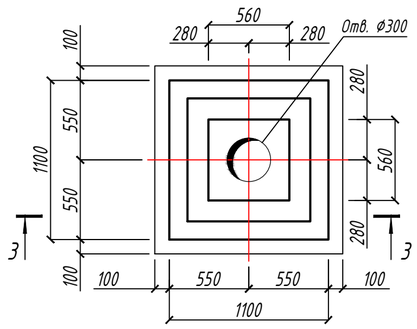

Разрез 3-3

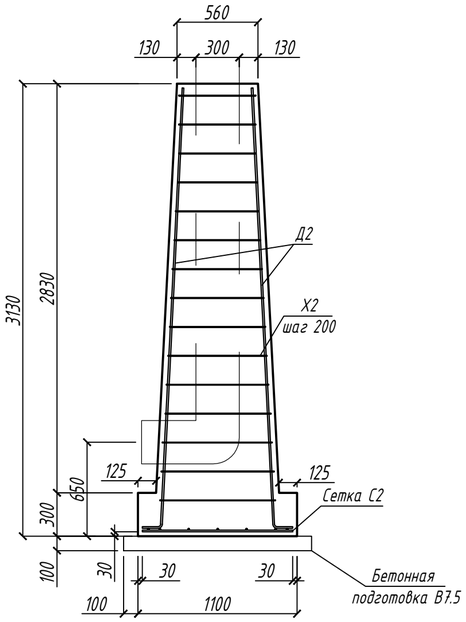

Спецификация элементов

Марка Поз.	Обозначение	Наименование		Кол. шт	Масса ед., кг	Прим.
		Фундамент Фм 1, Фм 2 (на 1 шт.)				
		Сборочные единицы				
С 1	см. данный лист	Горизонтальная сетка С 1		1	6.12	6.12
		Детали				
Д 1	см. данный лист	ГОСТ 34028-2016 Ø12 А400	L=2830 мм	4	2.51	10.04
X1	см. данный лист	ГОСТ 34028-2016 Ø6 А240	L=1460 мм	14	0.32	4.53
		Сетка С 1				
1	см. данный лист	ГОСТ 34028-2016 Ø12 А400	L=690 мм	10	0.61	6.12
		Материал				
	см. данный лист	ГОСТ 26633-2010 Бетон В 25		0.5		м³
	см. данный лист	ГОСТ 26633-2010 Бетон В 7.5		0.1		м³
		Фундамент Фм 3 (на 1 шт.)				
		Сборочные единицы				
С 1	см. данный лист	Горизонтальная сетка С 2		1	12.92	12.92
		Детали				
Д 2	см. данный лист	ГОСТ 34028-2016 Ø12 А400	L=3120 мм	4	2.77	11.07
X2	см. данный лист	ГОСТ 34028-2016 Ø6 А240	L=2760 мм	15	0.61	9.18
		Сетка С 2				
2	см. данный лист	ГОСТ 34028-2016 Ø12 А400	L=1040 мм	14	0.92	12.92
		Материал				
	см. данный лист	ГОСТ 26633-2010 Бетон В 25		0.8		м³
	см. данный лист	ГОСТ 26633-2010 Бетон В 7.5		0.2		м³

Примечание

1. Общие данные смотреть на листе EWE0426-MGL1-STR-054-COM-690501-A1
2. Под монолитным фундаментом выполнить подготовку из бетона кл. В 7.5 толщиной 100 мм с уширением на 100 мм в каждую сторону от размеров подошвы фундамента. Под ним выполнить подготовку из щебня, вдавленного в грунт, толщиной 100 мм, с проливкой горячим битумом с выступом за боковые грани бетонной подготовки по 100 мм в каждую сторону.

Рев.	Дата	Назначение ревизии	Проверил	Утвердил
R1	10.10.26	Выпущено для рассмотрения		

ЗАКАЗЧИК: UTG ГЕНЕРАЛЬНЫЙ ПОДРЯДЧИК: UET ПОДРЯДЧИК: PBG ГЕНЕРАЛЬНЫЙ ПРОЕКТИРОВЩИК: EAST WEST ENGINEERING

Изм.	Кол.уч.	Лист	№ док.	Подп.	Дата	EWE0426-MGL1-STR-054-DRW-690509-R1		
						«СТРОИТЕЛЬСТВО НОВЫХ НИТОК (УЧАСТКОВ) ГАЗОПРОВОДОВ «ГАЗЛИ - САРИМОЙ» И «АКЧАЛОК - ГАЗЛИ - НУКУС» ОБЩЕЙ ПРОТЯЖЕННОСТЬЮ НЕ МЕНЕЕ 275 КМ».		
ГИП		Кирпичников			10.26			
Нач.отдела		Каршиев			10.26	ГАЗОПРОВОД "ГАЗЛИ-САРИМОЙ" (54 КМ)	Стадия	Лист	Листов
Разраб.		Мамешов			10.26		РД	1	1
Проверил		Каршиев			10.26	Фундамент Ф 1, Ф 2, Ф 3	ООО "EAST-WEST Engineering" г. Ташкент 2026г.		
Н. контр.		Кирпичников			10.26				

Формат А 2

Взам. инв. N | Подп. и дата | Инв. N подл.