Навес для электрического шкафа

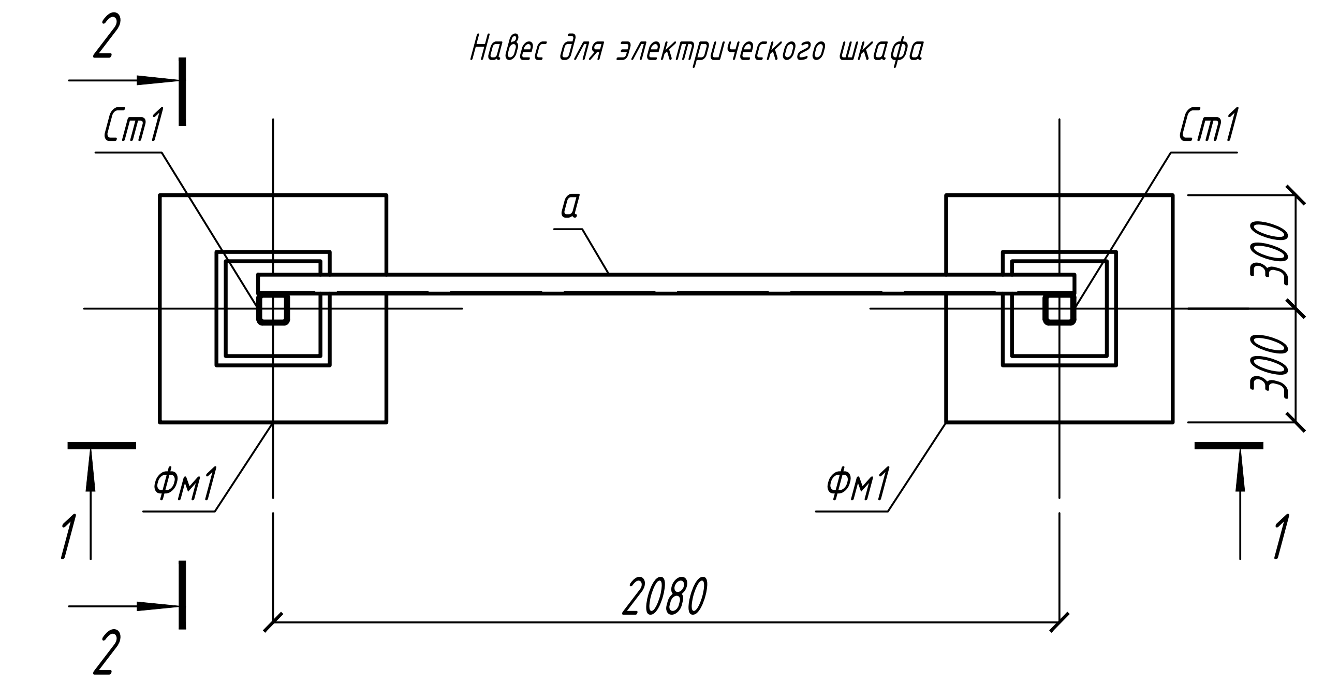

Фундамент Фм 1

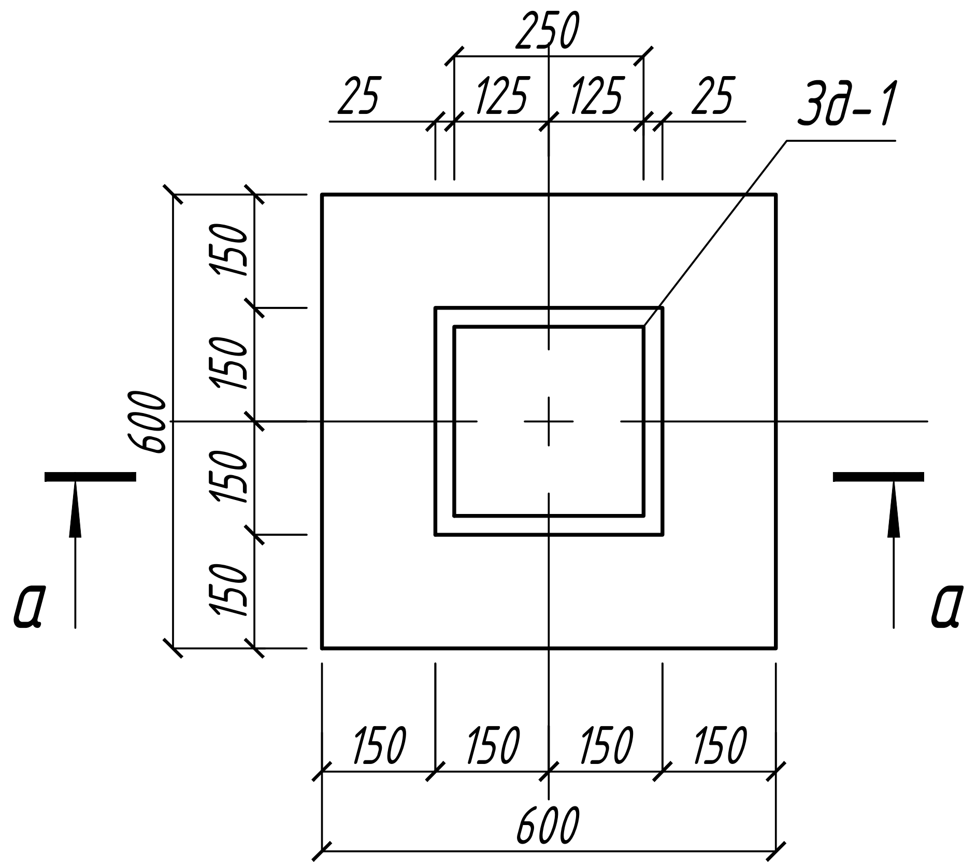

Разрез а -а

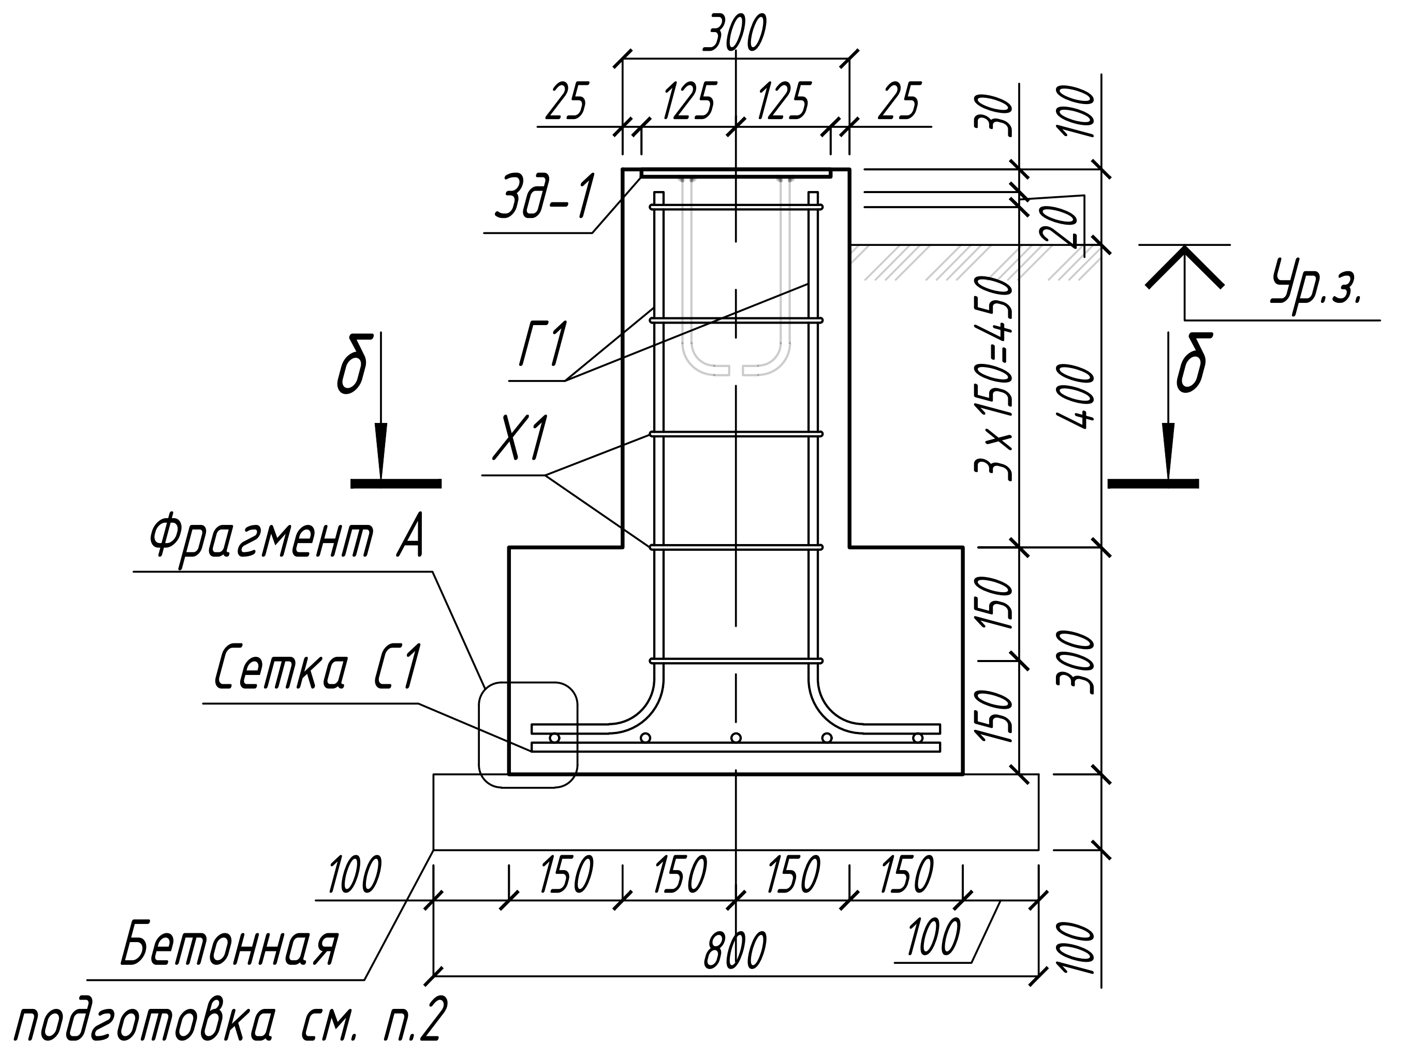

Разрез 1-1

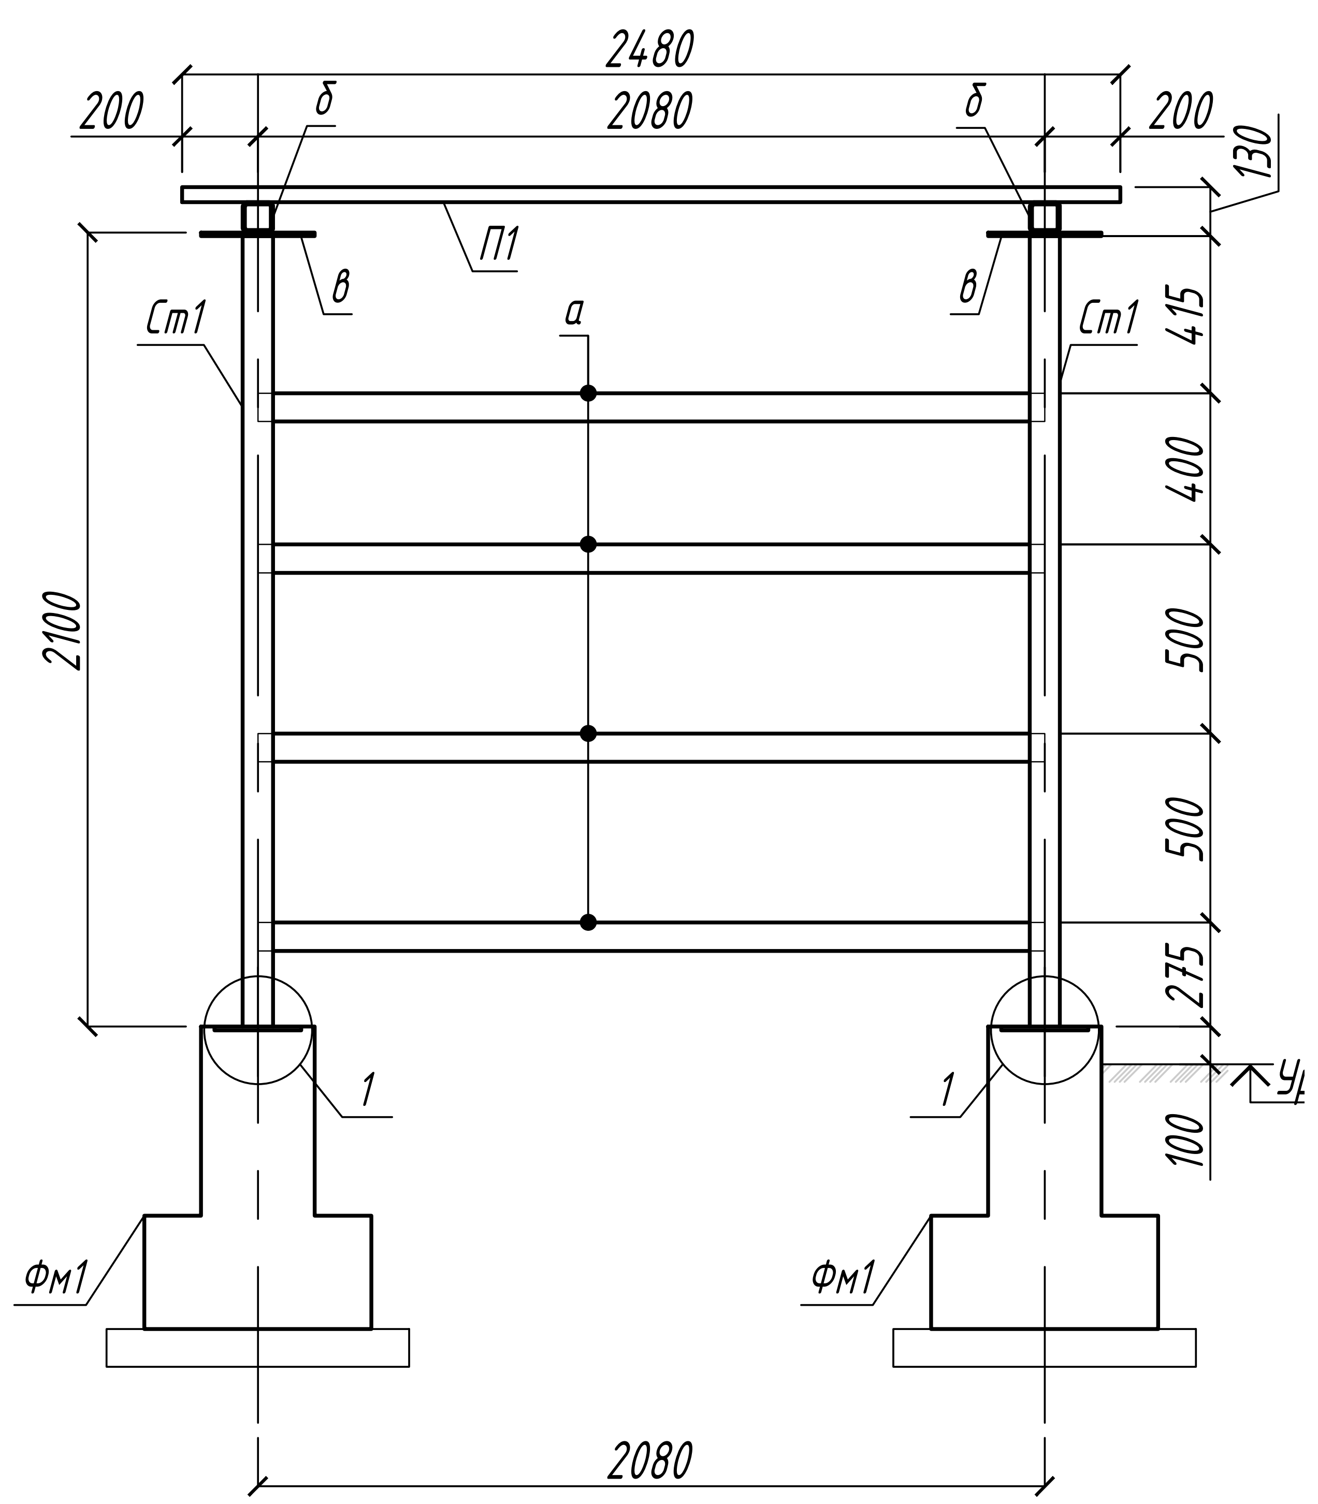

Разрез 2-2

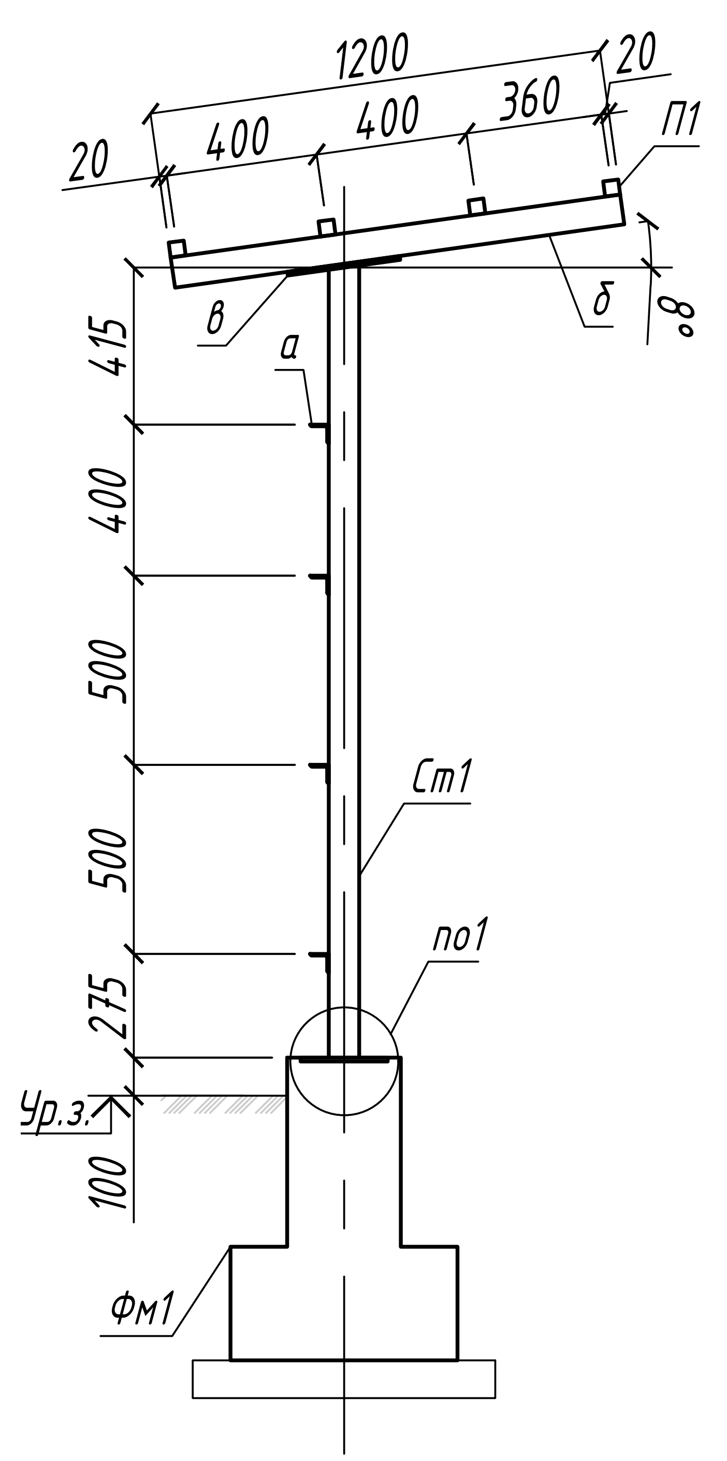

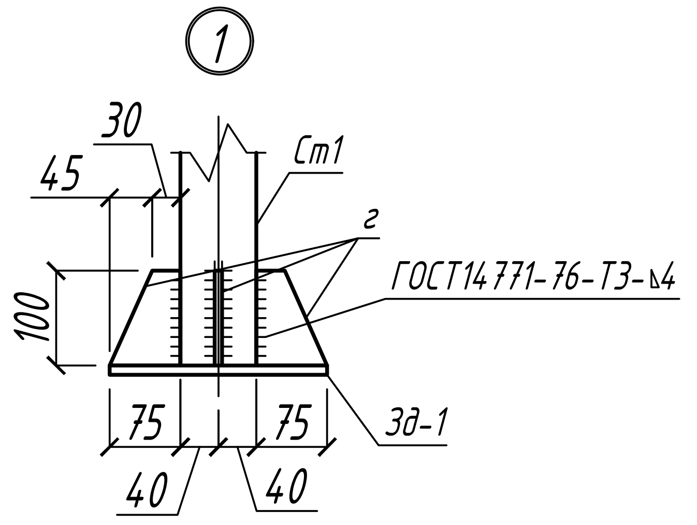

Ведомость деталей

Поз.	Эскиз
Г 1	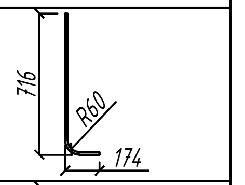
Г 2	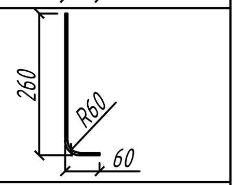
Х 1	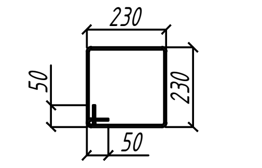

Все размеры даны по внешнем граням детали

Спецификация элементов

Марка Поз.	Обозначение	Наименование		Кол. шт	Масса ед., кг	Прим.
		Фундамент Фм 1 (на 1 шт.)				
		Сборочные единицы				
С 1	см. данный лист	Горизонтальная сетка С 1		1	4.79	4.79
Зд-1	см. данный лист	Закладная деталь Зд-1		1	6.05	6.05
		Детали				
Г 1	см. данный лист	ГОСТ 34028-2016 Ф12 А400	L=890 мм	4	0.79	3.16
Х 1	см. данный лист	ГОСТ 34028-2016 Ф6 А240	L=1020 мм	5	0.23	1.13
		Сетка С 1				
1	см. данный лист	ГОСТ 34028-2016 Ф12 А400	L=540 мм	10	0.48	4.79
		Закладная деталь Зд-1				
Л 1	см. данный лист	ГОСТ 19903-2015 -t10 250x250		1	4.91	4.91
Г 2	см. данный лист	ГОСТ 34028-2016 Ф12 А400	L=320 мм	4	0.28	1.14
		Материал				
	см. данный лист	ГОСТ 26633-2010 Бетон В 25		0.2		м^3
	см. данный лист	ГОСТ 26633-2010 Бетон В 7.5		0.1		м^3

Спецификация металлопроката

Наименование профиля ГОСТ, ТУ	Наименование или марка металла ГОСТ, ТУ	Обозначение и размер профиля, мм	N п.п.	Масса металла по элементам конструкций, т		Общая масса, т
				Навес		
1	2	3	4	5	6	7
Гнутые замкнутые сварные профили квадратного сечения	С 255 ГОСТ 27772-2015	80 x 5	1	0.08		
		40 x 4	2	0.03		
Всего профиля			3	0.110		0.11
Уголки стальные горячекатаные неравнополочные ГОСТ 8509-93	С 255 ГОСТ 27772-2015	∟ 50 x 75 x 5	4	0.03		
			5			
Всего профиля			6	0.03		0.03
Прокат листовой горячекатаный ГОСТ 19903-2015	С 255 ГОСТ 27772-2015	t8	7	0.02		
			8			
Всего профиля			9	0.02		0.02
Всего масса			10	0.16		0.16

Техническая спецификация подсчитана без учета добавления к общей массе: 1% наплавленного металла (на сварку) и 3% на изготовление КМД.

Ведомость элементов

Марка элемента	Сечение			Усилие для прикрепления			Наименование или марка металла	Примечание
	Эскиз	Поз.	Состав	Q, тс	N, тс	M, тс*м		
Ст 1	□		80x80x5				С255	
б	□		80x80x5				С255	
в			-t8 300x300				С255	
П 1	□		40x40x4				С255	
а	∟		75x50x5				С255	
г			-t8 200 x 75				С255	

б - б

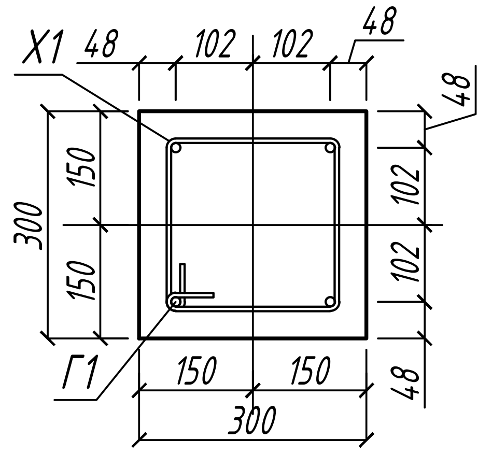

Фрагмент А

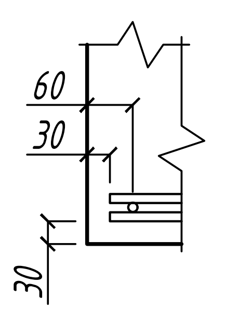

Закладная деталь Зд-1

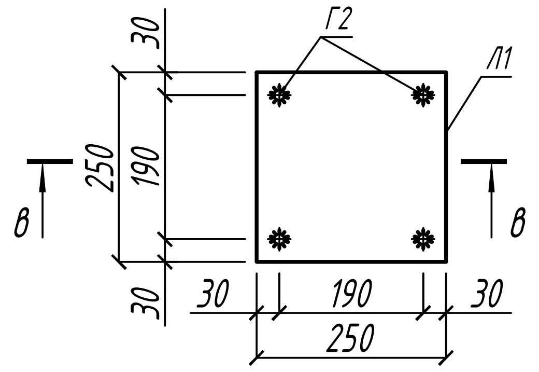

в - в

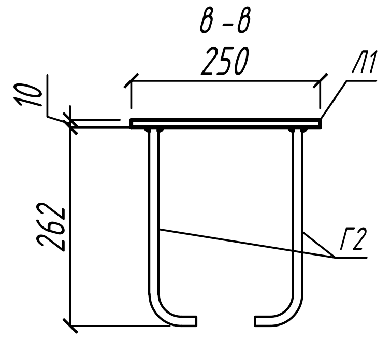

Сетка горизонтальная С 1

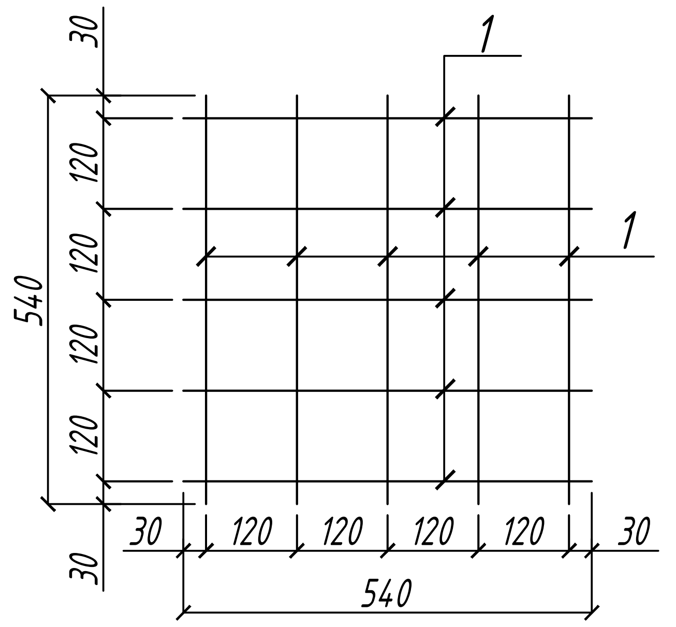

Примечание

1. Общие данные смотреть на листе EWE0426-MGL1-STR-054-COM-690501
2. Под монолитным фундаментом выполнить подготовку из бетона кл. В 7.5 толщиной 100 мм с уширением на 100 мм в каждую сторону от размеров подошвы фундамента. Под ним выполнить подготовку из щебня, вдавленного в грунт, толщиной 100 мм, с проливкой горячим битумом с выступом за боковые грани бетонной подготовки по 100 мм в каждую сторону.
3. Сварку производить электродами типа Э 42 А по ГОСТ 9467-75. Высоту швов принять равной наименьшей толщине свариваемых элементов, длину - по длине примыкания. Длину шва выполнять по всей длине свариваемых элементов.
4. Схему расположения навеса для шкафа смотреть в разделе ГП

Рев.	Дата	Назначение ревизии	Проверил	Утвердил
R1	10.26	Выпущено для рассмотрения		

ЗАКАЗЧИК: UTG UZTRANSGAZ

ГЕНЕРАЛЬНЫЙ ПОДРЯДЧИК: UET UZBEKENERGOTAMIR

ПОДРЯДЧИК: PBG Pro Build Generation

ГЕНЕРАЛЬНЫЙ ПРОЕКТИРОВЩИК: EAST WEST ENGINEERING

EWE0426-MGL1-STR-054-DRW-690512-R1

«СТРОИТЕЛЬСТВО НОВЫХ НИТОК (УЧАСТКОВ) ГАЗОПРОВОДОВ «ГАЗЛИ - САРИМОЙ» И «АКЧАЛОК - ГАЗЛИ - НУКУС» ОБЩЕЙ ПРОТЯЖЕННОСТЬЮ НЕ МЕНЕЕ 275 КМ».

Изм.	Кол.уч.	Лист	№ док.	Подп.	Дата
ГИП		Кирпичников			10.26
Нач.отдела		Каршиев			10.26
Разраб.		Мамешов			10.26
Проверил		Каршиев			10.26
Н. контр.		Кирпичников			10.26

ГАЗОПРОВОД "ГАЗЛИ-САРИМОЙ" (54 КМ)

Стадия	Лист	Листов
РД	1	

Навес для электрического шкафа

ООО "EAST-WEST Engineering"
г. Ташкент 2026г.

Формат А3x3

Взам. инв. N

Подп. и дата

Инв. N подл.