Таблица 1.1


Позиция прибора	Место установки
Узел приема/запуска очистных устройств DN1200.УЗПОУ-D11. EWE0426-MGL1-PRE-054-SCM-610102	
PG-D11-001	Трубопровод 50-GT-63CS02-HH-D1123
PG-D11-002	Трубопровод 50-GT-63CS02-HH-D1122

Таблица 1.2


Позиция прибора	Место установки
Узел приема/запуска очистных устройств DN1200.УЗПОУ-D11. EWE0426-MGL1-PRE-054-SCM-610102	
PG-D11-005	Трубопровод 150-DC-63CS02-N-D1111
PG-D11-006	Трубопровод 150-DC-63CS02-N-D1111
PG-D11-007	Трубопровод 150-GT-63CS02-N-D1109
PG-D11-008	Трубопровод 50-NI-63CS02-N-D1124
PG-D11-009	Трубопровод 50-NI-63CS02-N-D1120

Поз.	Обозначение	Наименование	Кол.	Масса ед, кг	Примечание
Материалы предназначены для монтажа одного прибора. Общее количество будет учтено в документе "Спецификация оборудования, изделий и материалов" EWE0426-MGL1-SYS-054-SPC-690303					
1	См. таблицу 1.1 См. таблицу 1.2	Манометр для установки на трубопроводе	1		
2		Двухвентильный манифольд	1		в компл. с датчиком
3	ОС-16-02-Ш(В)-Ш(Н)-1/2NPT-1/2NPT-Ац-Б	Трубка угловая. Присоединение со стороны процесса - наружная резьба 1/2'' NPT-M, присоединение со стороны датчика - внутренняя резьба 1/2'' NPT-F	1		
4	ОС-16-01-Ш(В)-Ш(Н)-1/2NPT-1/2NPT-Б- длина трубки 200мм	Трубка прямая 1/2'' NPT-M - 1/2'' NPT-F (длина трубки 200мм)	1		

Установочный чертеж манометра на трубопроводе (Таблица 1.1)

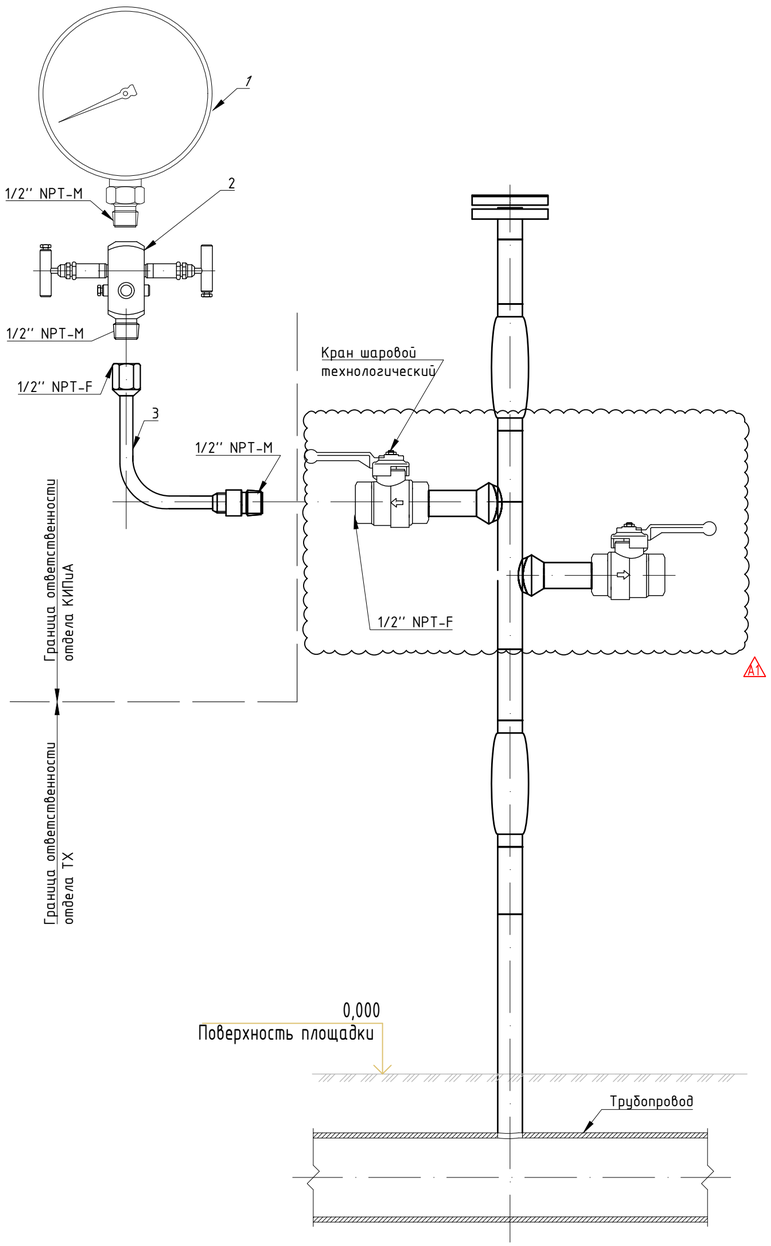

Установочный чертеж манометра на горизонтальном трубопроводе (Таблица 1.2)

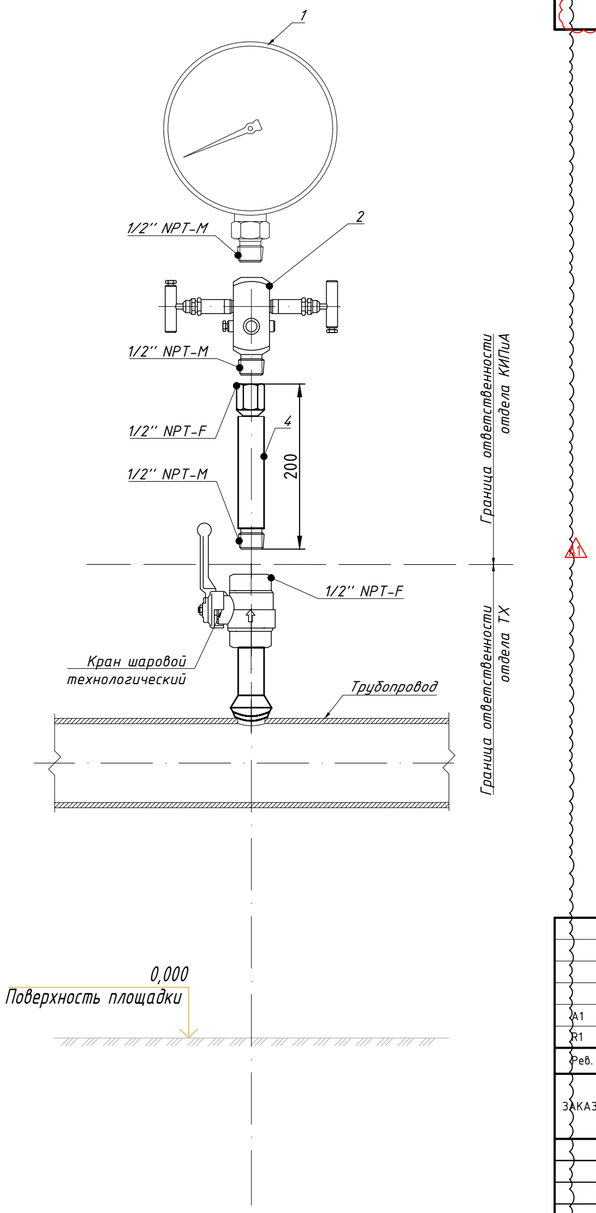

Рев.	Дата	Назначение ревизии	Проверил	Утвердил
A1	11.09.2026	Утверждено для строительства		
R1	24.07.2026	Выпущено для рассмотрения		

ЗАКАЗЧИК: UTG ГЕНЕРАЛЬНЫЙ ПОДРЯДЧИК: UET ПОДРЯДЧИК: PBG ГЕНЕРАЛЬНЫЙ ПРОЕКТИРОВЩИК: EAST WEST ENGINEERING

EWE0426-MGL1-SYS-054-DRW-690302-A1

«СТРОИТЕЛЬСТВО НОВЫХ НИТОК (УЧАСТКОВ) ГАЗОПРОВОДОВ «ГАЗЛИ - САРИМОЙ» И «АКЧАЛОК - ГАЗЛИ - НУКУС» ОБЩЕЙ ПРОТЯЖЕННОСТЬЮ НЕ МЕНЕЕ 275 КМ».

Изм.	Кол.уч.	Лист	№док.	Подпись	Дата			
ГИП		Кирпичников С.			09.2026	Газопрвод «Газли-Сарымой» (54 КМ). Узел приема/запуска очистных устройств DN1200.УЗПОУ-D11.	Стадия	Лист	Листов
Нач.отд.		Кабулова Е.			09.2026		РД	1	6
Исполн.		Усманов Д.			09.2026				
Н.контр		Кирпичников С.			09.2026	Монтажный чертеж КИП	EAST WEST ENGINEERING	ООО "EAST-WEST Engineering" г. Ташкент 2026г.	

Взам. инв. №


Подпись и дата

Инв.№ подл.

Таблица 2

Позиция прибора	Место установки	Номер импульсной линии
Узел приема/запуска очистных устройств DN1200.УЗПОУ-D11. EWE0426-MGL1-PRE-054-SCM-610102		
PIT-D11-001	Трубопровод 50-GT-63CS02-HH-D1123	
PIT-D11-002	Трубопровод 50-GT-63CS02-HH-D1122	

Установочный чертеж преобразователя давления

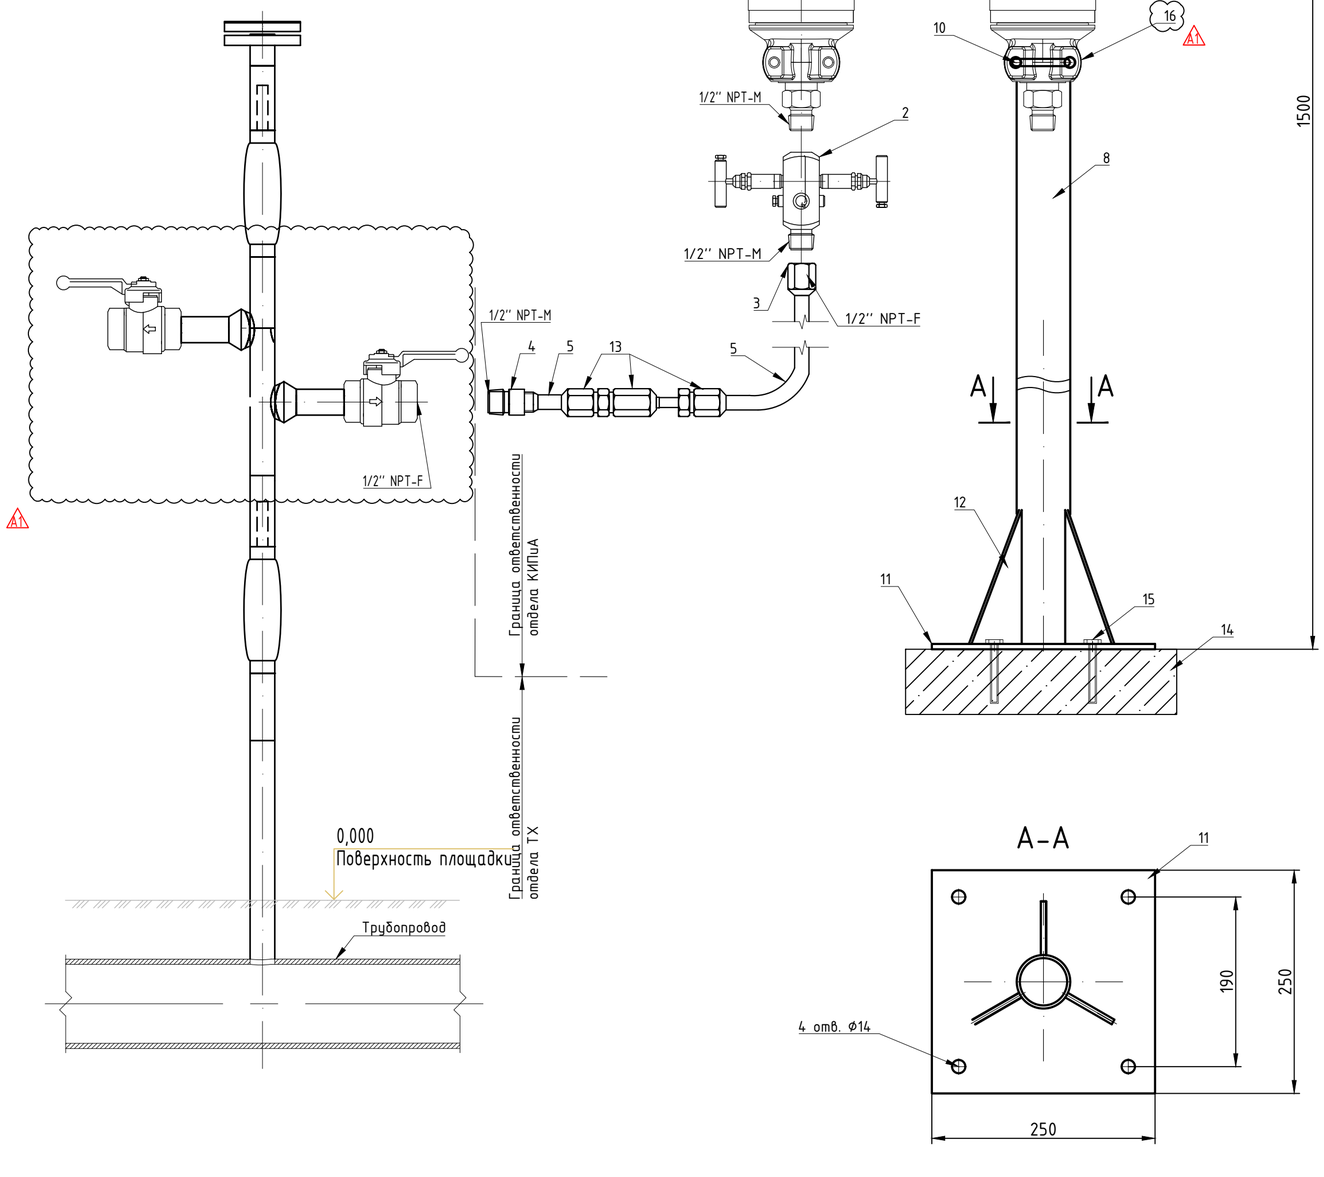

Поз.	Обозначение	Наименование	Кол.	Масса ед, кг	Примеча- ние
Материалы предназначены для монтажа одного прибора. Общее количество будет учтено в документе "Спецификация оборудования, изделий и материалов" EWE0426-MGL1-SYS-054-SPC-690303					
1	См. таблицу 2	Преобразователь давления	1		
2		Двухвентильный манифольд	1		в компл. с датчиком
3	A1 SS-810-7-8	Трубный обжимной фитинг Swagelok из нерж. стали, соединитель с внутренней резьбой, диам. трубки 1/2 дюйма – внутр. резьба NPT 1/2 дюйма.	1		
4	SS-810-1-8	Трубный обжимной фитинг Swagelok из нерж. стали, соединитель с наруж. резьбой, наруж. диам. трубки 1/2 дюйма – наруж. резьба NPT 1/2 дюйма.	1		
5	SS-T8-S-049-20	Импульсная трубка 1/2x0,049; 12Х18Н10Т, Swagelok	2		м
6	A1	Кабельный ввод для бронированного кабеля (Dн=11...17мм)	1		комплектно с датчиком
7		Кабельная заглушка	1		
8		Труба оцинкованная Ц-50х3,5 ГОСТ 3262-75	1,5		м
9		Сталь листовая 2×500×500 ГОСТ 19903-2015 ОК360В-1 ГОСТ 16523-97	1		
10		Хомут Х50 ТУ 34-1107-80, С439	1		
11		Опорная плита 10×300×300 ГОСТ 19903-2015 Ст3сп ГОСТ 14637-2024	1		
12		Сталь листовая 4×400×500 ГОСТ 19903-2015 Ст3сп ГОСТ 14637-2024	2		
13	SS-8-DE-6	Муфта проходная диэлектрическая на трубку 1/2" (Swagelock)	1		
14		Бетон марки М200 (300x300x400)мм		0,036	$м^3$
15		Болт анкерный с гайкой и шайбой М12х150L	4	шт	
16		Кронштейн для монтажа на 2" трубу			комплектно с датчиком

A1

Взам. инв. №

Подпись и дата

Инв.№ подл.


Изм.	Кол.уч.	Лист	№док	Подпись	Дата	EWE0426-MGL1-SYS-054-DRW-690302-A1	Лист 2

Формат / Format A2

Таблица 3

Позиция прибора	Место установки
Узел приема/запуска очистных устройств DN1200.УЗПОУ-D11. EWE0426-MGL1-PRE-054-SCM-610102	
TIT-D11-001	Трубопровод 1200-GT-63CS00-HH-D1102

Установочный чертеж термопреобразователя

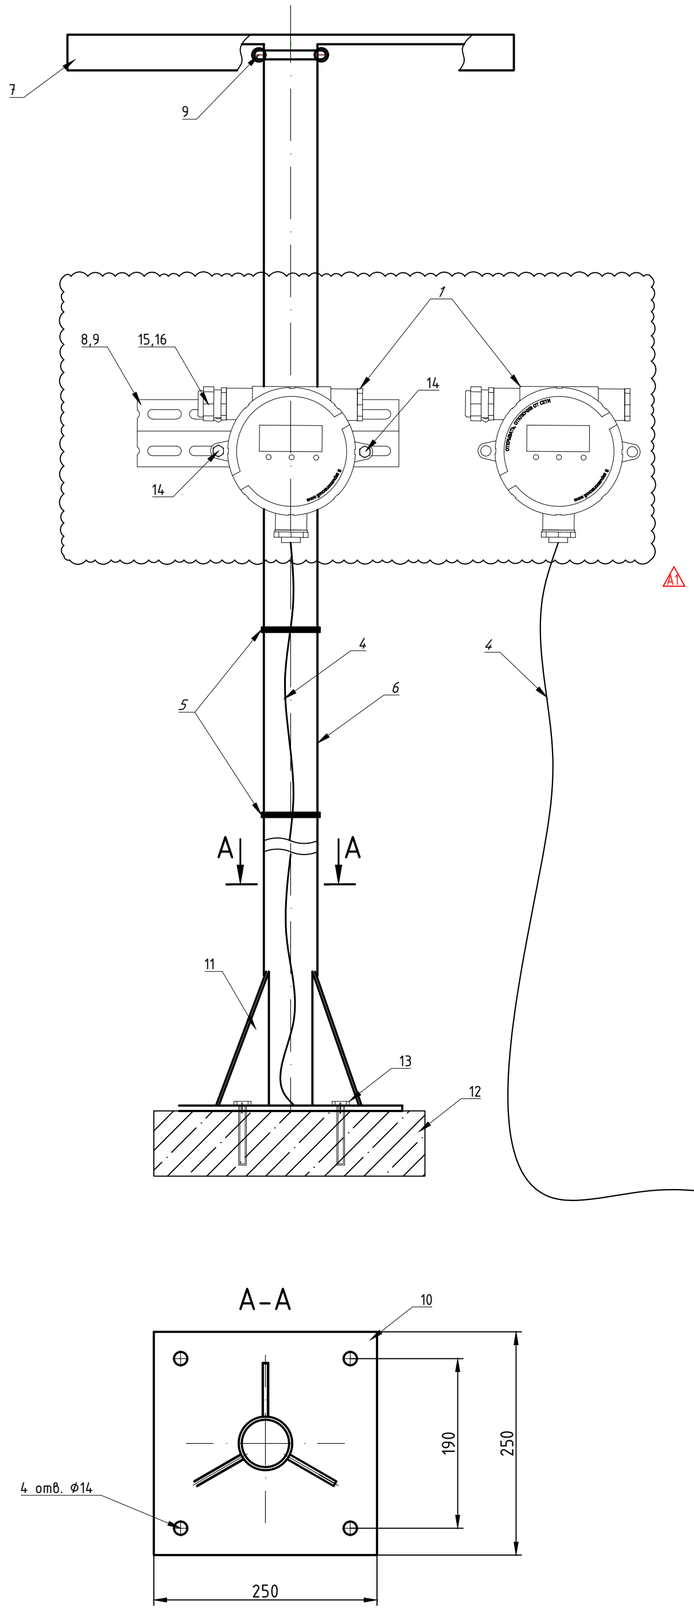

Поз.	Обозначение	Наименование	Кол.	Масса ед, кг	Примечание
Материалы предназначены для монтажа одного прибора. Общее количество будет учтено в документе "Спецификация оборудования, изделий и материалов" EWE0426-MGL1-SYS-054-SPC-690303					
1	См. таблицу 5	Термопреобразователь	1		
2		Сенсор термопреобразователя	1		
3		Хомут для сенсора термопреобразователя	1		в компл. с датчиком
4		Кабель для сенсора термопреобразователя	1		
5		Хомут червячный (металлический) Ф100 мм для крепления к трубе кабеля от сенсора к датчику	2		
6		Труба оцинкованная Ц-50х3,5 ГОСТ 3262-75	1,5		м
7		Сталь листовая 2×500×500 ГОСТ 19903-2015 ОК360В-1 ГОСТ 16523-97	1		
8		Профиль перфорированный Z-образный К241 (L=300мм)	1		
9		Хомут Х50 ТУ 34-1107-80, С439	1		
10		Опорная плита 10×300×300 ГОСТ 19903-2015 Ст3сп ГОСТ 14637-2024	1		
11		Сталь листовая 4×400×500 ГОСТ 19903-2015 Ст3сп ГОСТ 14637-2024	2		
12		Бетон марки М200 (300х300х400)мм		0,036	$м^3$
13		Болт анкерный с гайкой и шайбой М12х150L	4	шт	
14		Комплект монтажных изделий (болт, гайка, шайба)	1		
15		Кабельный ввод для бронированного кабеля (Dн=11...17мм)	1		в компл. с датчиком
16		Кабельная заглушка	1		

Взам. инв. №

Подпись и дата

Инв.№ подл.

Изм.	Кол.уч	Лист	№док	Подпись	Дата	EWE0426-MGL1-SYS-054-DRW-690302-A1	Лист 3


Формат / Format A2

Таблица 4

Позиция прибора	Место установки
Узел приема/запуска очистных устройств DN1200.УЗПОУ-D11. EWE0426-MGL1-PRE-054-SCM-610102	
TG-D11-001	Трубопровод 150-GT-63CS02-N-D1109

Поз.	Обозначение	Наименование	Кол.	Масса ед, кг	Примечание
Материалы предназначены для монтажа одного прибора. Общее количество будет учтено в документе "Спецификация оборудования, изделий и материалов" EWE0426-MGL1-SYS-054-SPC-690303					
1	См. таблицу 4	Термометр показывающий	1		
2		Защитная гильза	1		в компл. с прибором

Установочный чертеж термометра показывающего на горизонтальном трубопроводе

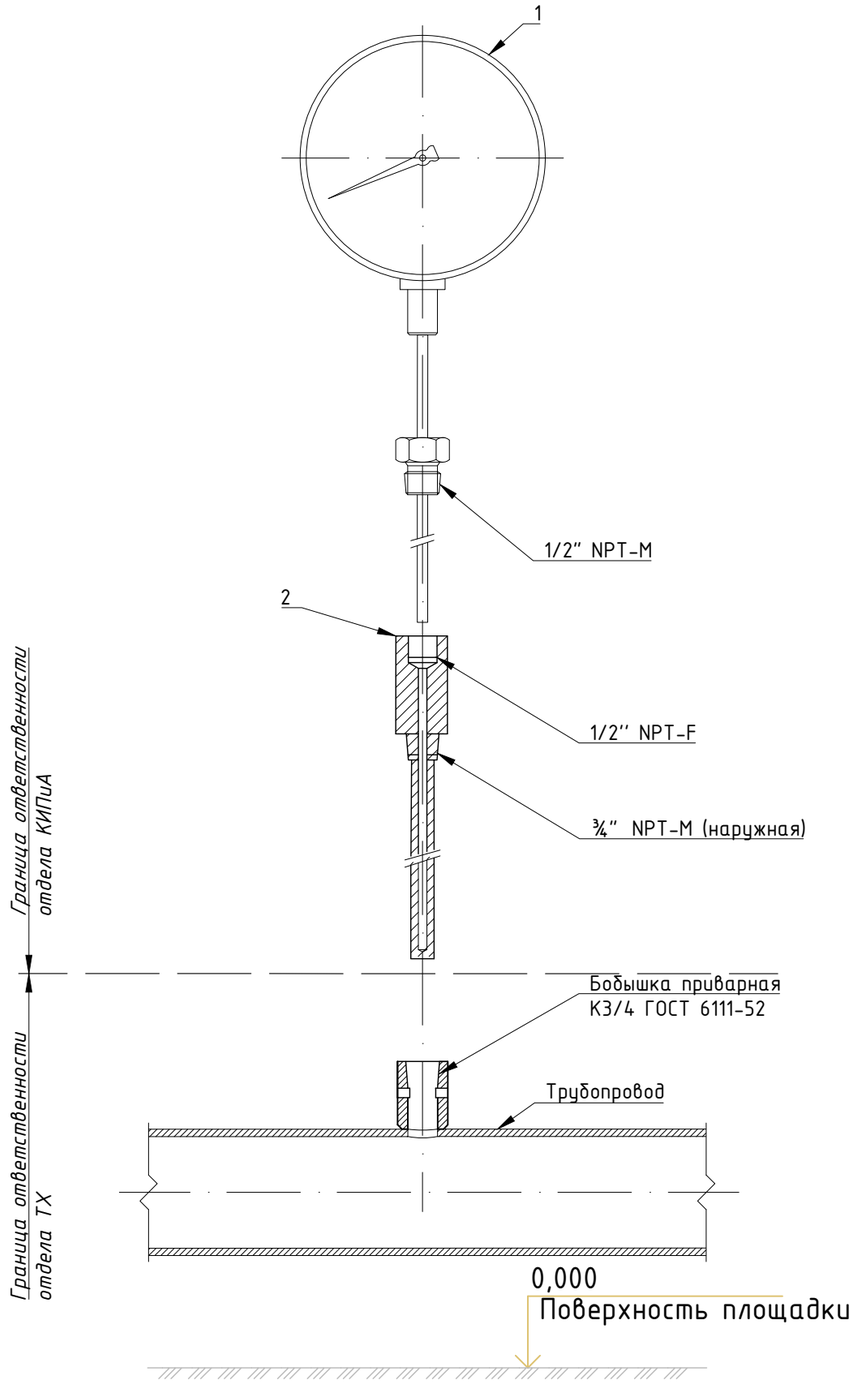

1. По данному чертежу смонтировать позиции указанные в таблице.
2. Позиции приборов соответствуют схемам P&ID (указанным в таблицах) и заказной спецификации.


Взам. инв. №								
Подпись и дата								
Инв.№ подл.								
		Изм.	Кол.уч	Лист	№док	Подпись	Дата	EWE0426-MGL1-SYS-054-DRW-690302-A1

Лист 4

Таблица 5

Позиция прибора	Место установки
Узел приема/запуска очистных устройств DN1200.УЗПОУ-D11. EWE0426-MGL1-PRE-054-SCM-610102	
ZIS-D11-001	Трубопровод 1200-GT-63CS00-HH-D1102
ZIS-D11-002	Трубопровод 1200-GT-63CS00-HH-D1102
ZIS-D11-003	Трубопровод 1200-GT-63CS00-HH-D1101

Установочный чертеж сигнализатора прохождения очистного устройства с клеммной коробкой

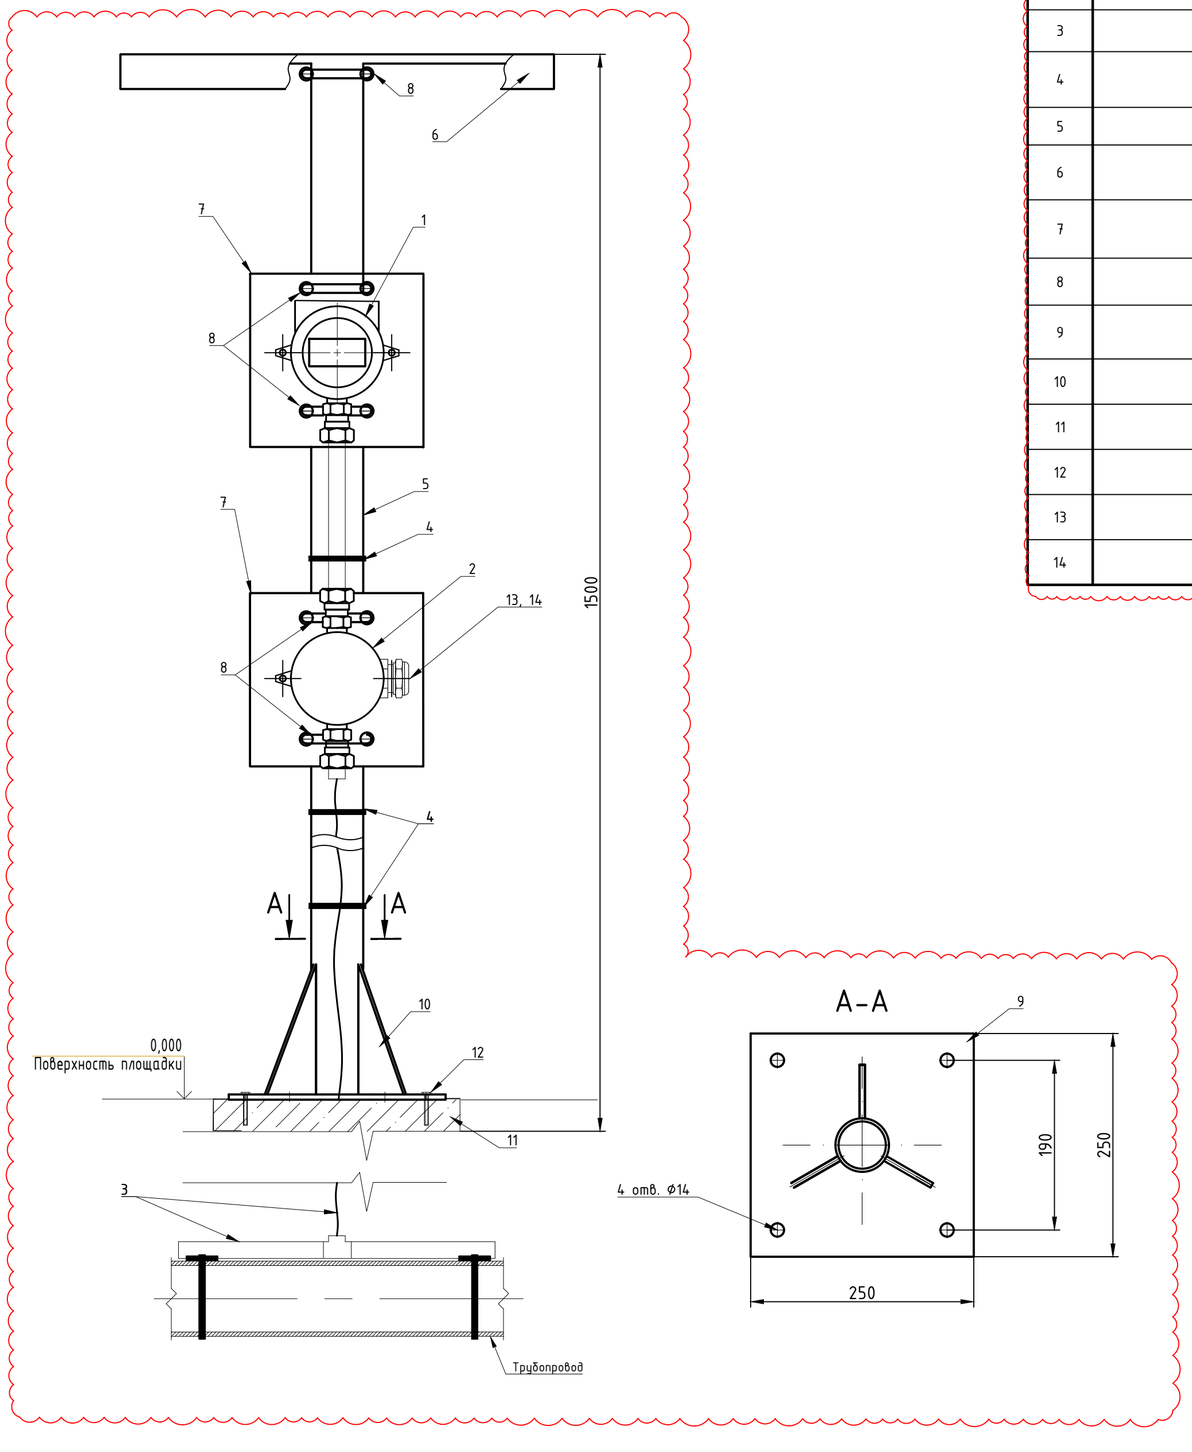

Поз.	Обозначение	Наименование	Кол.	Масса ед, кг	Примечание
Материалы предназначены для монтажа одного прибора. Общее количество будет учтено в документе "Спецификация оборудования, изделий и материалов" EWE0426-MGL1-SYS-054-SPC-690303					
1		Сигнализатор прохождения очистного устройства	1		
2		Клеммная коробка сигнализатора	1		в компл. с сигнализатором
3		Гибкий кабель (L=5м) с антенной сигнализатора	1		
4		Хомут червячный (металлический) ⌀100 мм для крепления к трубе кабеля от сенсора к датчику	3		
5		Труба оцинкованная Ц-50х3,5 ГОСТ 3262-75	1,5		м
6		Сталь листовая 2×500×500 ГОСТ 19903-2015 ОК360В-1 ГОСТ 16523-97	1		
7		Сталь листовая, 4×200х200 800х500 ГОСТ 19903-2015 ОК 360В-1 ГОСТ 16523-97	2		
8		Хомут Х50 ТУ 34-1107-80	5		
9		Опорная плита 10×300×300 ГОСТ 19903-2015 Ст3сп ГОСТ 14637-89	1		
10		Лист 2х400х500 ГОСТ19903-2015/ ОК 360В-1 ГОСТ 16523-97	2		
11		Бетон марки М200 (300х300х400)мм		0,036	$м^3$
12		Болт анкерный с гайкой и шайбой М12х150L	4		
13		Кабельный ввод для бронированного кабеля (Dн=11...17мм)	1		в компл. с сигнализатором
14		Кабельная заглушка	1		

А1

Взам. инв. №

Подпись и дата

Инв.№ подл.

Изм.	Кол.уч	Лист	№док	Подпись	Дата	EWE0426-MGL1-SYS-054-DRW-690302-A1	Лист 5


Формат / Format A2

Таблица 6

Позиция прибора	Место установки
Узел приема/запуска очистных устройств DN1200.УЗПОУ-D11. EWE0426-MGL1-PRE-054-SCM-610102	
LIS-D11-001	Трубопровод 100-GT-63CS02-N-D1114

Поз.	Обозначение	Наименование	Кол.	Масса ед, кг	Примечание
1	См. таблицу 6	Сигнализатор уровня фланцевый	1		А1
2		Кабельный ввод для бронированного кабеля (Dн=11…17мм)	1		в компл. с прибором
3		Кабельная заглушка	1		
4		Комплект монтажных изделий (прокладка, шпильки, гайки, шайбы)	1		

Установочный чертеж фланцевого сигнализатора уровня на подземной горизонтальной емкости

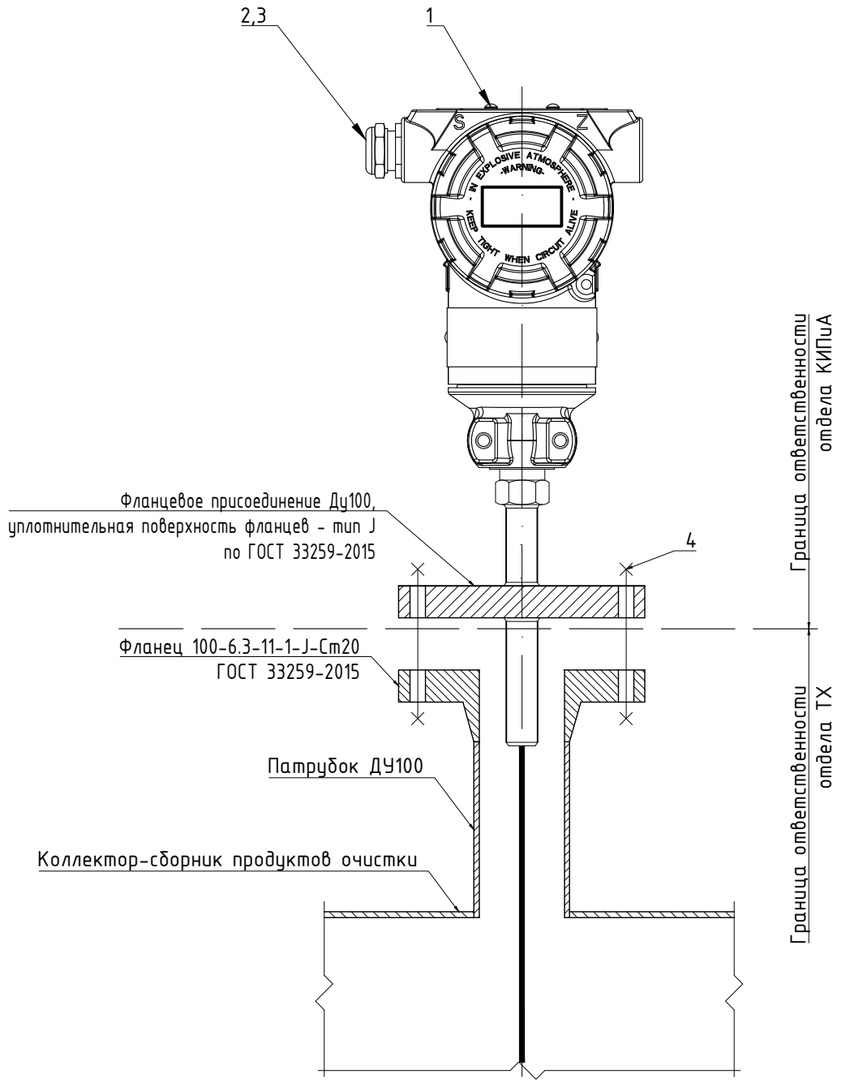

1. По данному чертежу смонтировать позиции указанные в таблице.
2. Позиции приборов соответствуют схемам P&ID (указанным в таблицах) и заказной спецификации.
3. * - HOLD в ожидании документации от поставщика.

Изм.	Кол.уч	Лист	№док	Подпись	Дата	EWE0426-MGL1-SYS-054-DRW-690302-A1	Лист 6

Взам. инв. № | Подпись и дата | Инв.№ подл.