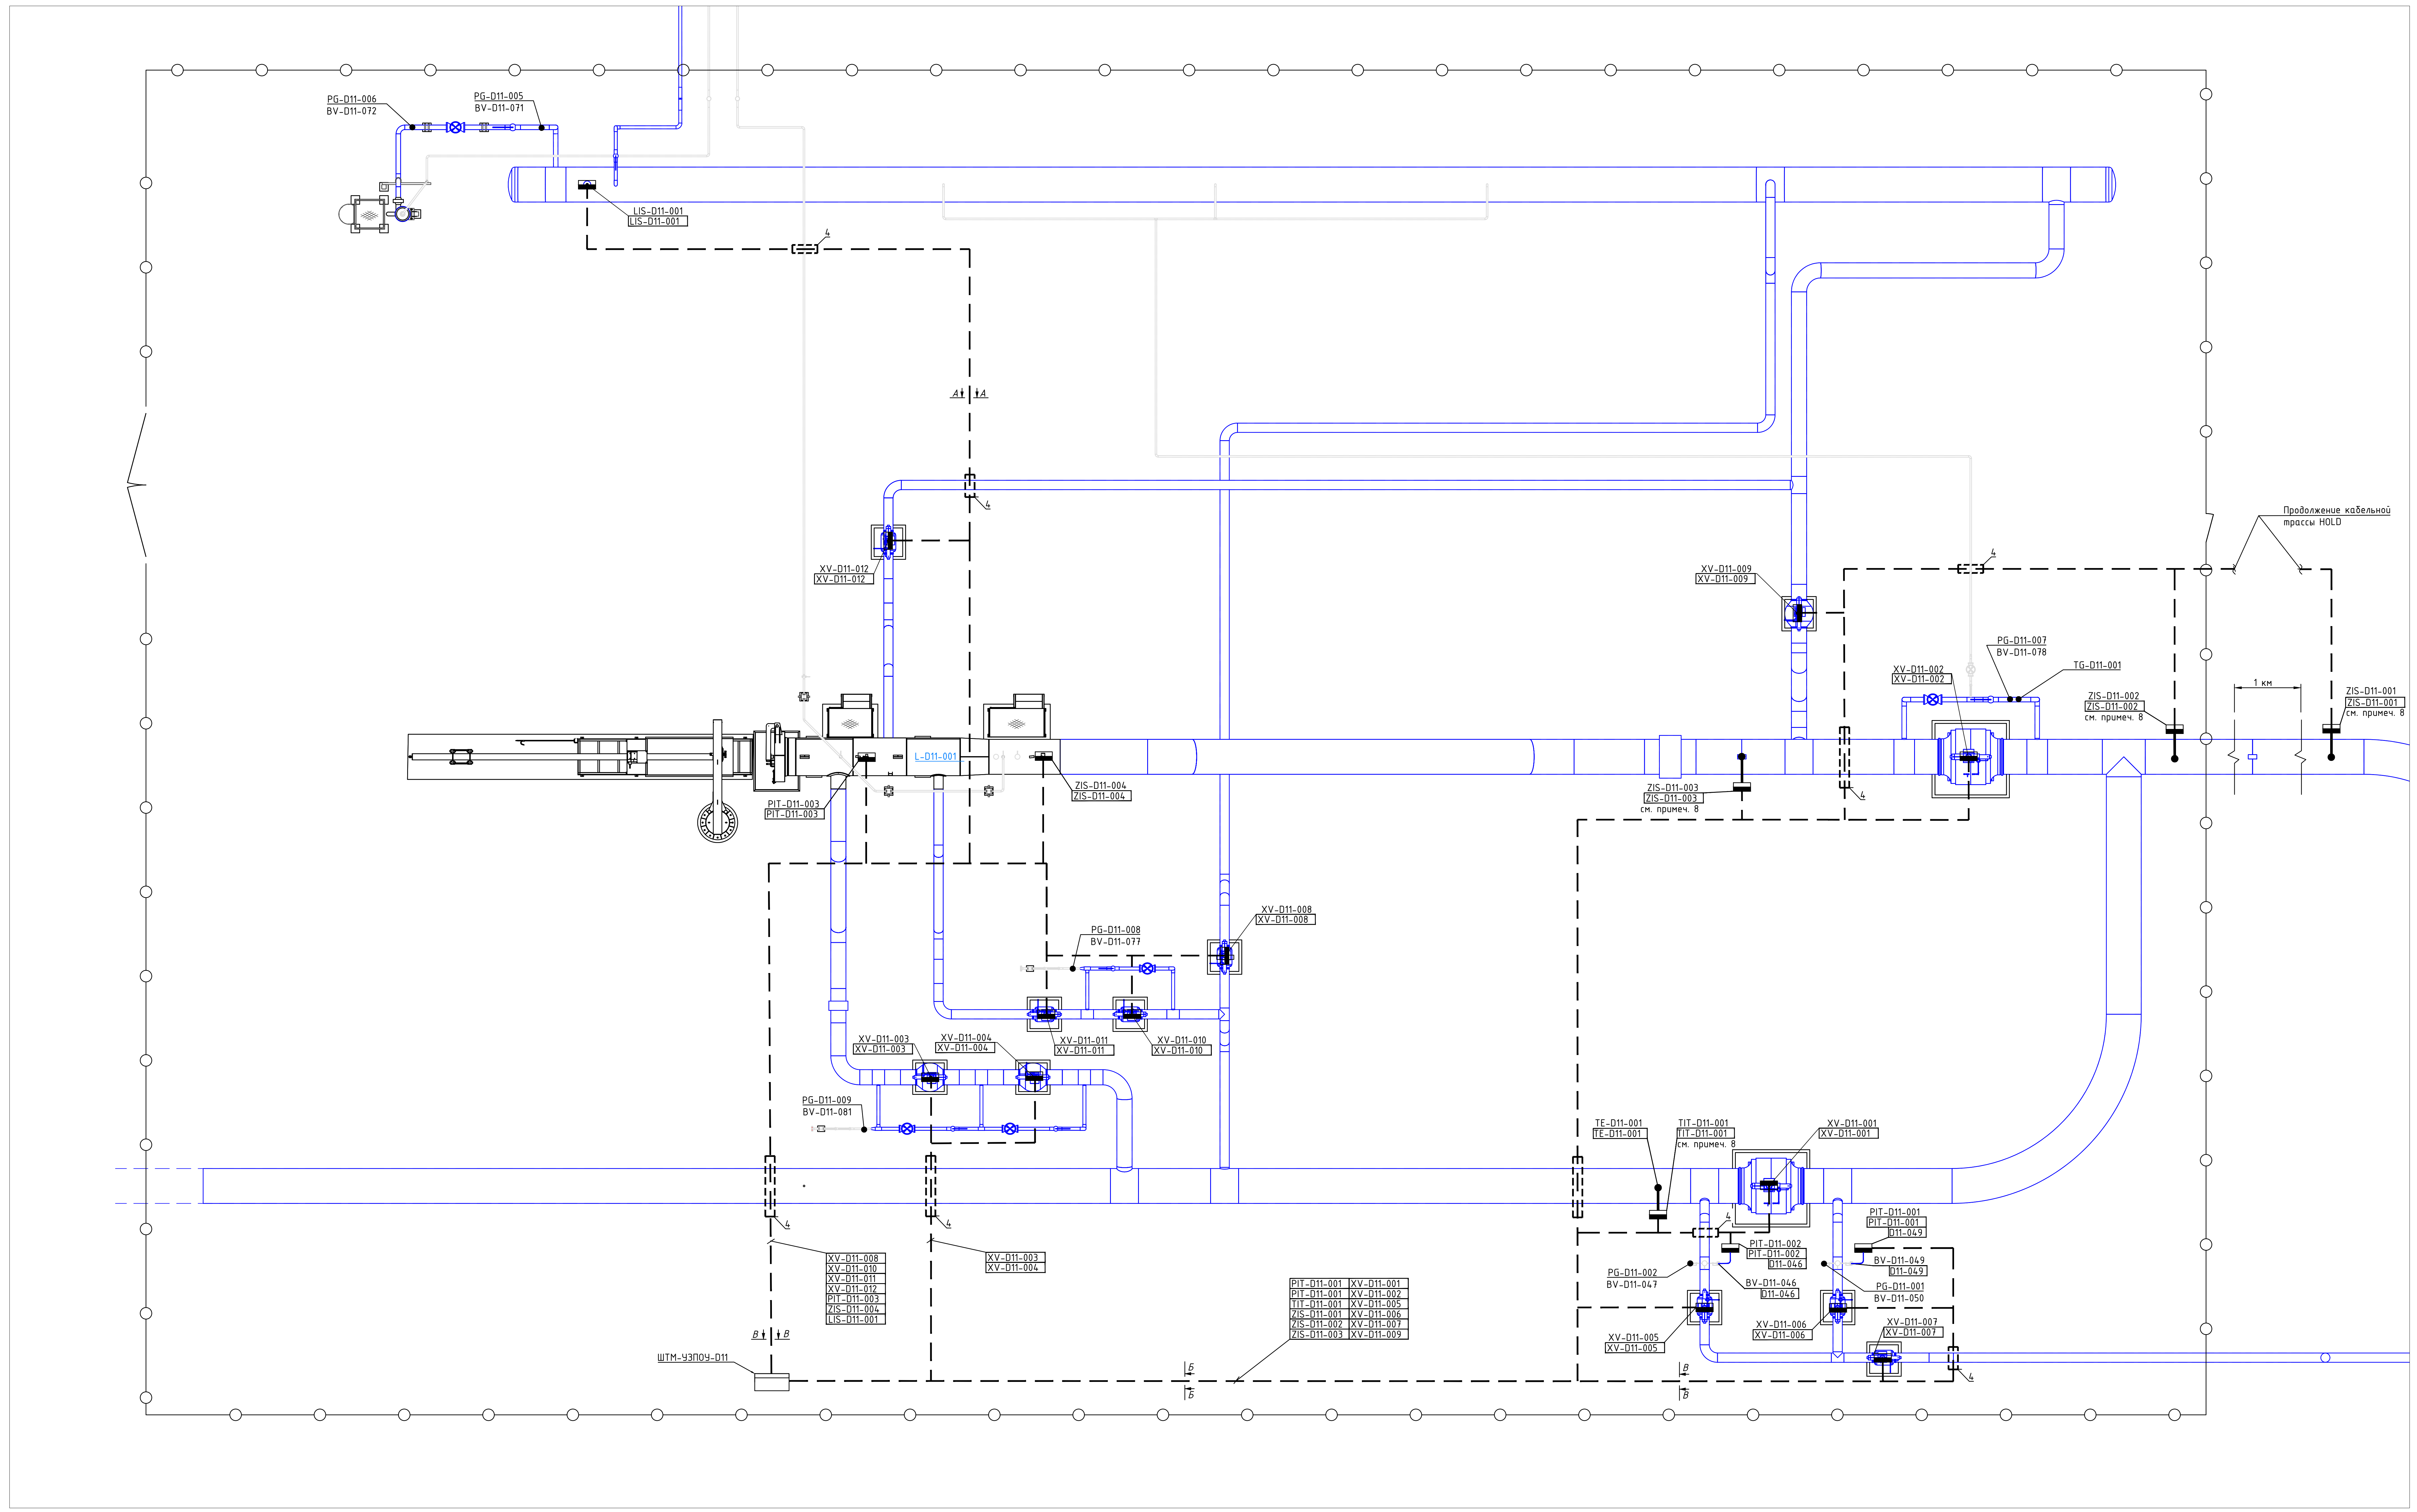

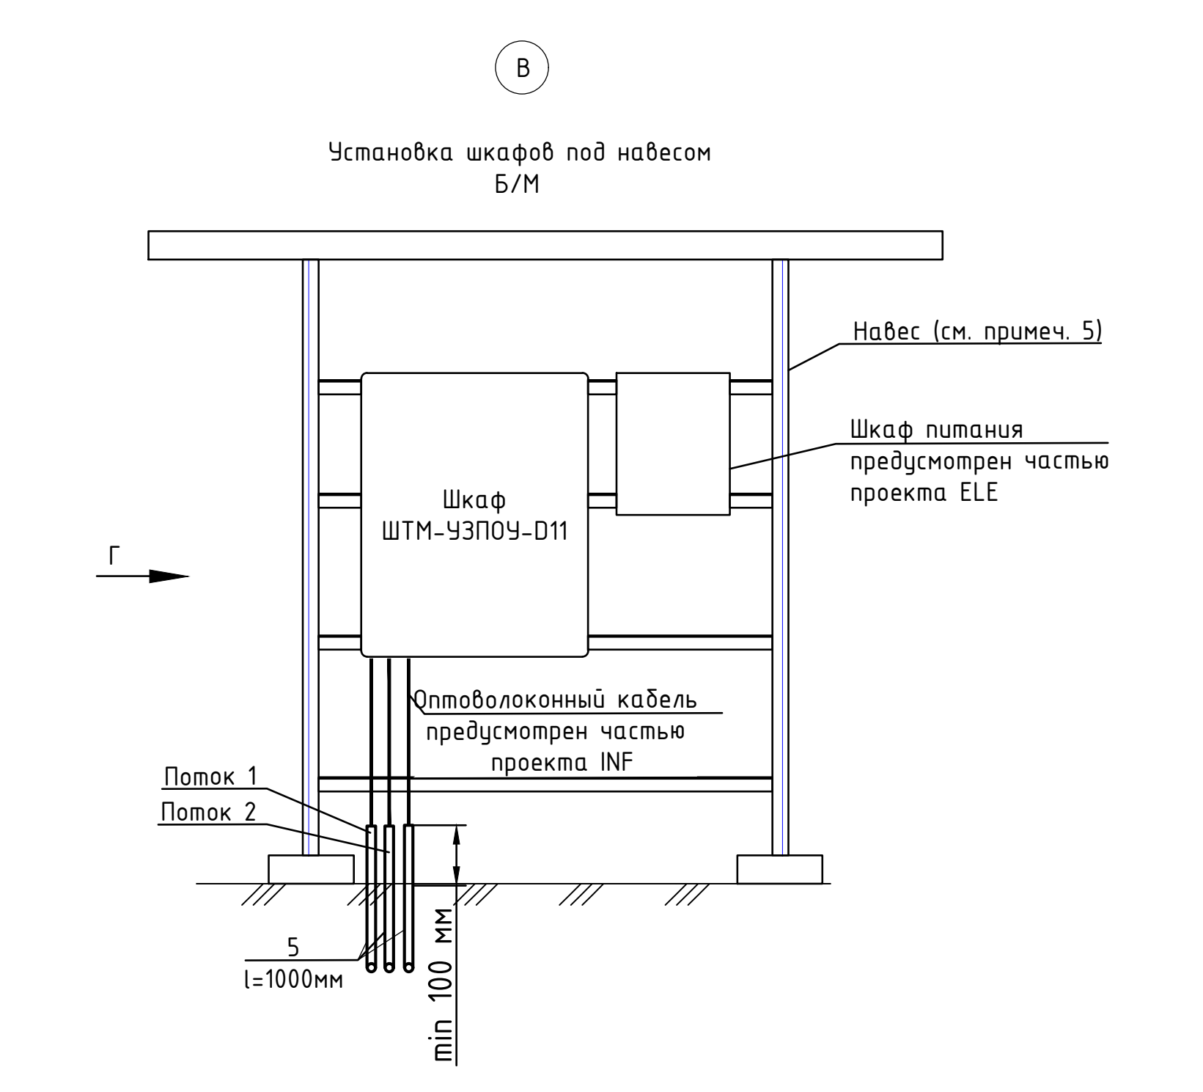
В

Установка шкафов под навесом
Б/М
Навес (см. примеч. 5)
Шкаф питания предусмотрен частью проекта ELE
Шкаф ШТМ-УЗПОУ-D11
Г
Оптоволоконный кабель предусмотрен частью проекта INF
Поток 1
Поток 2
5
l=1000мм
min 100 мм

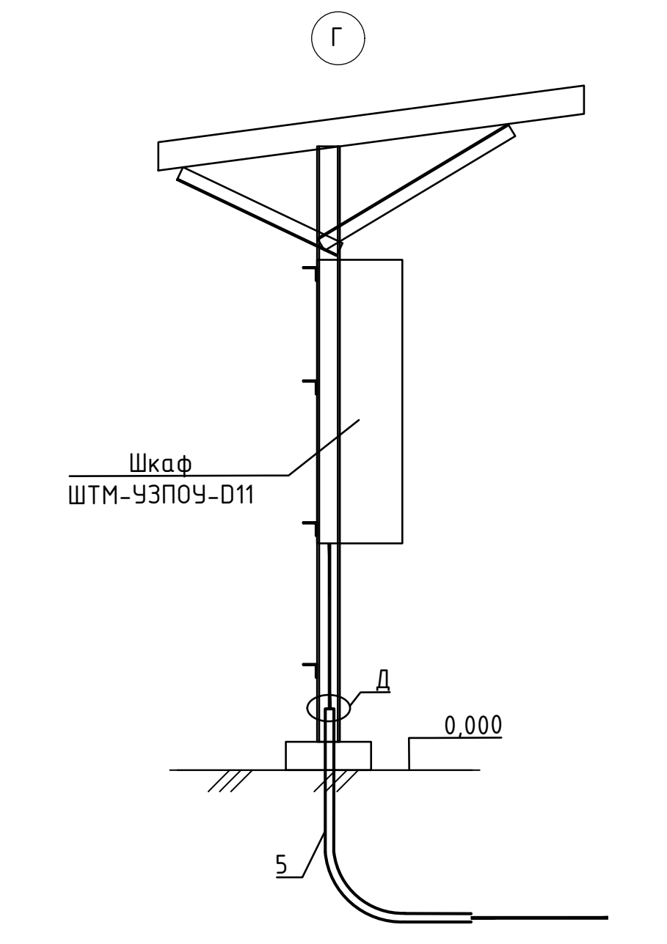
Г

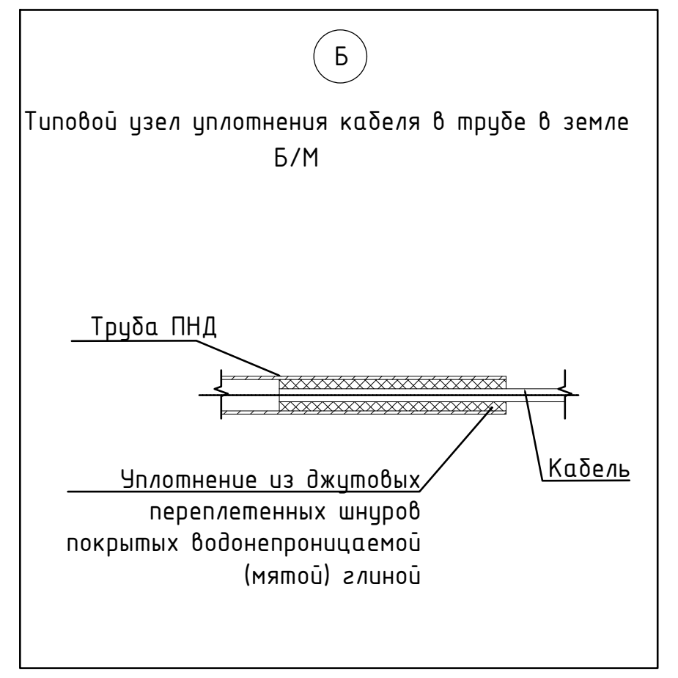
Б

Типовой узел уплотнения кабеля в трубе в земле
Б/М
Труба ПНД
Уплотнение из джутовых переплетенных шнуров покрытых водонепроницаемой (мятой) глиной
Кабель

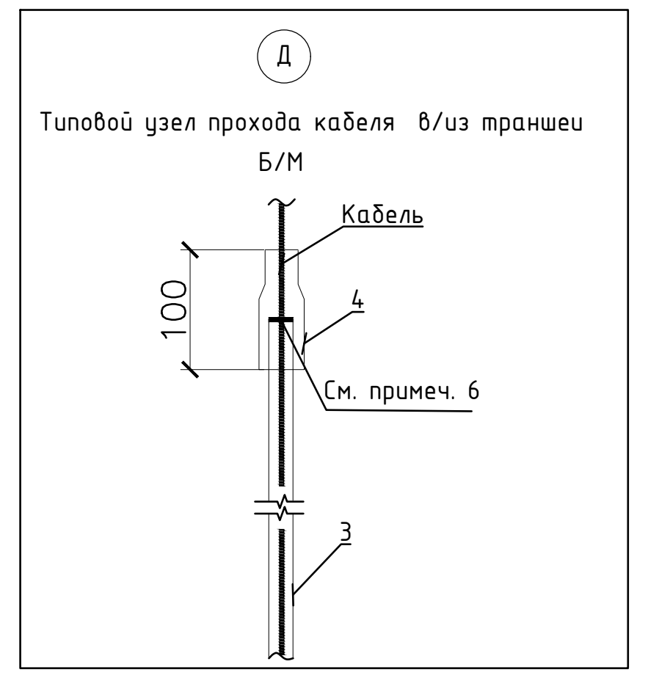
Д

Типовой узел прохода кабеля в/из траншеи
Б/М

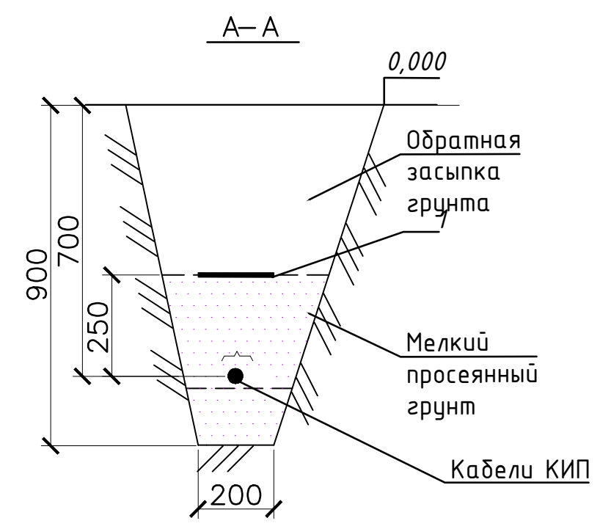
А–А

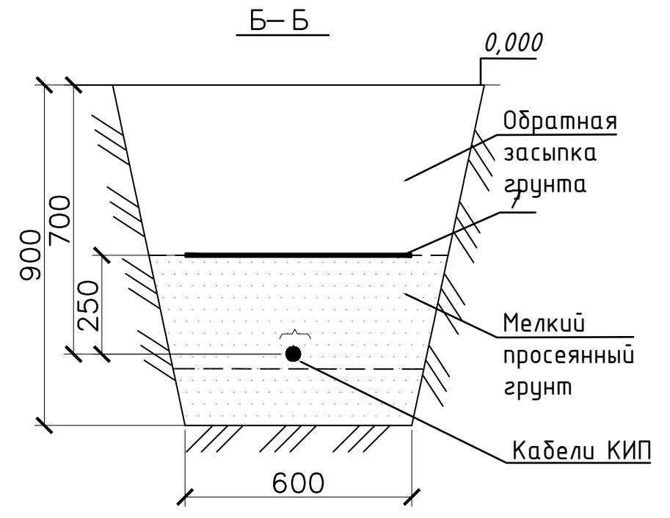
Б–Б

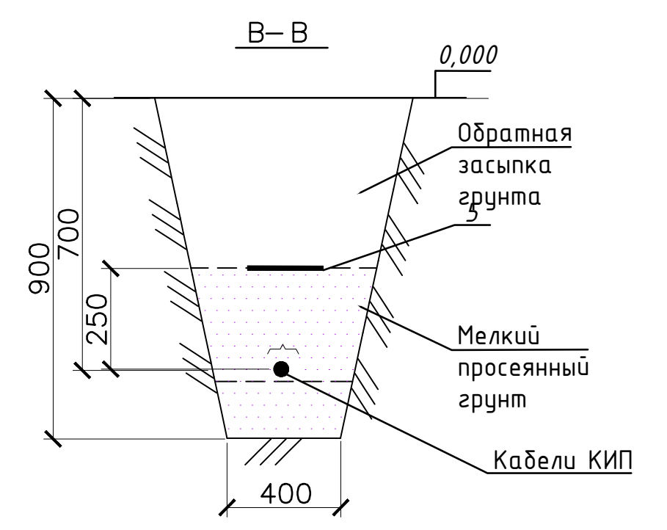
В–В

Поз.	Обозначение	Наименование	Кол.	Масса ед., кг	Примечание
1	ЛСЭ-150	Лента сигнальная	1100		м
2	ЛСЭ-400	Лента сигнальная	110		м
3	ЛСЭ-600	Лента сигнальная	30		м
4	ТУ 2248-019-47022248-2008	Жесткая двустенная гофрированная труба для прокладки в грунте и под автомобильными дорогами, ПНД, Ø75мм	8		м
5	ТУ 2248-015-47022248-2006	Труба жесткая гладкая ПНД Ø50 мм для защиты кабельных линий, для прокладки в грунте и на открытом воздухе, УФ-стойкая, без протяжки.	42		м
6	ТУ 2247-011-79523310-2006	Термоусадочная трубка с коэффициентом усадки 2:1 ТНТнг-LS-60/30	6		м

1. Данный чертёж разработан для УЗПОУ на основании чертежа EWE0426-MGL1-PRE-054-DRW-690205.
2. Позиции приборов и нумерация кабелей соответствует схеме соединений внешних проводок EWE0426-MGL1-SYS-054-SCM-690305.
3. Все приборы, находящиеся под напряжением, заземлить согласно ПУЭ и руководствам по эксплуатации на приборы.
4. Монтаж защитного заземления выполнить в соответствии с требованиями ПУЭ.
5. Шкаф телемеханики установить под навесом, предусмотрен частью проекта STR. Отверстия для крепления шкафа сверлить по месту.
6. При прокладке кабелей в земле в ПНД трубах выполнить уплотнение кабеля с обоих концов труб джутовыми плетеными шнурами, обмазанными водонепроницаемой (мятой) глиной на глубину не менее 300 мм., согласно узлу Б.
7. При пересечении в земле кабелем КИП технологических трубопроводов кабель проложить на расстоянии не менее 0,25 м в свету по вертикали от трубопровода. На участке пересечения, а также на расстоянии по 2 м в каждую сторону от него, кабель проложить в трубе ПНД двустенной жесткой.
8. Установка приборов на стойке КИПиА см. документ EWE0426-MGL1-SYS-054-DRW-690302.
9. За относительную отметку 0,000 принята проектная отметка уровня земли.
10. Земляные работы на территории площадки производить ручным методом.

Рев.	Дата	Назначение ревизии	Проверил	Утвердил
A1	11.09.2026	Утверждено для строительства		
R1	24.07.2026	Выпущено для рассмотрения		

ЗАКАЗЧИК: UTG UZTRANSGAZ
ГЕНЕРАЛЬНЫЙ ПОДРЯДЧИК: UET UZBEKENERGOTAMIR
ПОДРЯДЧИК: PBG Pro Build Generation
ГЕНЕРАЛЬНЫЙ ПРОЕКТИРОВЩИК: EAST WEST ENGINEERING

EWE0426-MGL1-SYS-054-PLA-690306-A1

«СТРОИТЕЛЬСТВО НОВЫХ НИТОК (УЧАСТКОВ) ГАЗОПРОВОДОВ «ГАЗЛИ – САРИМОЙ» И «АКЧАЛОК – ГАЗЛИ – НУКУС» ОБЩЕЙ ПРОТЯЖЕННОСТЬЮ НЕ МЕНЕЕ 275 КМ».

Изм.	Кол.уч.	Лист	№док.	Подпись	Дата
ГИП		Кирпичников С.			09.2026
Нач.отд.		Кабулова Е.		Екаш	09.2026
Исполн.		Усманов Д.			09.2026
Н.контр		Кирпичников С.			09.2026

Газопрвод «Газли-Сарымой» (54 КМ).
Узел приема/запуска очистных устройств DN1200.УЗПОУ-D11.

Стадия	Лист	Листов
РД	1	1

План расположения оборудования и проводок

ООО "EAST-WEST Engineering"
г. Ташкент 2026г.

Формат / Format A2X3

Взам. инв. №
Подпись и дата
Инв.№ подл.