Поз. обозна-чение	Наименование	Кол.	Примечание
	Кабель универсальный инструментальный КУИН нг(А) ВЭК-УФ		
	1х2х1,0	334	м
	5х2,5	1290	м
	8х2,5	615	м
	Труба ПНД 50	42	м
	Провод ПуГВ-Т 1х6 ж-з.	63	м

Условные обозначения:

- Заземление
- Экран кабеля
- OS — Общий экран кабеля отогнуть и изолировать
- Поставщик EAST-WEST Engineering
- S — Индивидуальный экран кабеля отогнуть и изолировать
- Броня кабеля
- Заземление брони кабеля через кабельный ввод

1. Схема разработана на основании P&ID EWE0426-MGL1-PRE-054-SCM-610102 ... EWE0426-MGL1-PRE-054-SCM-610120.
2. Двухвентильный манофольд поставляется комплектно с манометром или датчиком давления.
3. Свободные жилы кабеля и экран со стороны приборов изолировать от проводящих конструкций и грунта.
4. Броню кабелей присоединить к системе уравнивания потенциалов в устройствах кабельного ввода.
5. Длины кабелей даны с 10% запасом на изгибы, повороты и отходы.
6. Заземление приборов КИП выполнить присоединением провода ПуГВ-Т 1х6 ж-з к металлоконструкции стойки приборной КИПиА.
7. Корпус шкафа телемеханики и соединительных коробок присоединить к контуру заземления проводом ПуГВ-Т 1х6 ж-з.
8. Экран кабелей со стороны шкафа телемеханики присоединить к контору функционального заземления.
9. Подключение кабеля к пневмоприводу крана XV-* выполнить к клеммам, согласно принципиальной схемы крана.

Рев.	Дата	Назначение ревизии	Проверил	Утвердил
A1	11.09.2026	Утверждено для строительства		
R1	24.07.2026	Выпущено для рассмотрения		

ЗАКАЗЧИК: UTG UZTRANSGAZ | ГЕНЕРАЛЬНЫЙ ПОДРЯДЧИК: UET UZBEKENERGOTAMIR | ПОДРЯДЧИК: PBG Pro Build Generation | ГЕНЕРАЛЬНЫЙ ПРОЕКТИРОВЩИК: EAST WEST ENGINEERING

Взам. инв. №

Подпись и дата

Инв.№ подл.

Изм.	Кол.уч.	Лист	№док.	Подпись	Дата
ГИП		Кирпичников С.			09.2026
Нач.отд.		Кабулова Е.			09.2026
Исполн.		Усманов Д.			09.2026
Н.контр		Кирпичников С.			09.2026

EWE0426-MGL1-SYS-054-SCM-690305-A1

«СТРОИТЕЛЬСТВО НОВЫХ НИТОК (УЧАСТКОВ) ГАЗОПРОВОДОВ «ГАЗЛИ – САРИМОЙ» И «АКЧАЛОК – ГАЗЛИ – НУКУС» ОБЩЕЙ ПРОТЯЖЕННОСТЬЮ НЕ МЕНЕЕ 275 КМ».

Газопрвод «Газли-Сарымой» (54 КМ). Узел приема/запуска очистных устройств DN1200.УЗПОУ-D11.


Стадия	Лист	Листов
РД	1	6

Схема соединений и подключения внешних проводок

ООО "EAST-WEST Engineering"
г. Ташкент 2026г.

Формат / Format A4

Наименование параметра и место отбора импульса	Датчик температуры	Датчик давления			Сигнализатор уровня	Сигнализаторы прохождения очистного устройства			
	Контроль температуры	Контроль давления			Контроль уровня	Контроль прохождения очистного устройства			
	Трубопровод 1200-GT-63CS00-HH-D1102	Трубопровод 50-GT-63CS02-HH-D1123	Трубопровод 50-GT-63CS02-HH-D1122	Камера L-D11-001	Коллектор-сборник продуктов очистки	Трубопровод 1200-GT-63CS00-HH-D1102	Трубопровод 1200-GT-63CS00-HH-D1102	Трубопровод 1200-GT-63CS00-HH-D1101	Камера L-D11-001
Обозначение чертежа установки									
Позиция	TIT-D11-001	PIT-D11-001	PIT-D11-002	PIT-D11-003	LIS-D11-001	ZIS-D11-001	ZIS-D11-002	ZIS-D11-003	ZIS-D11-004

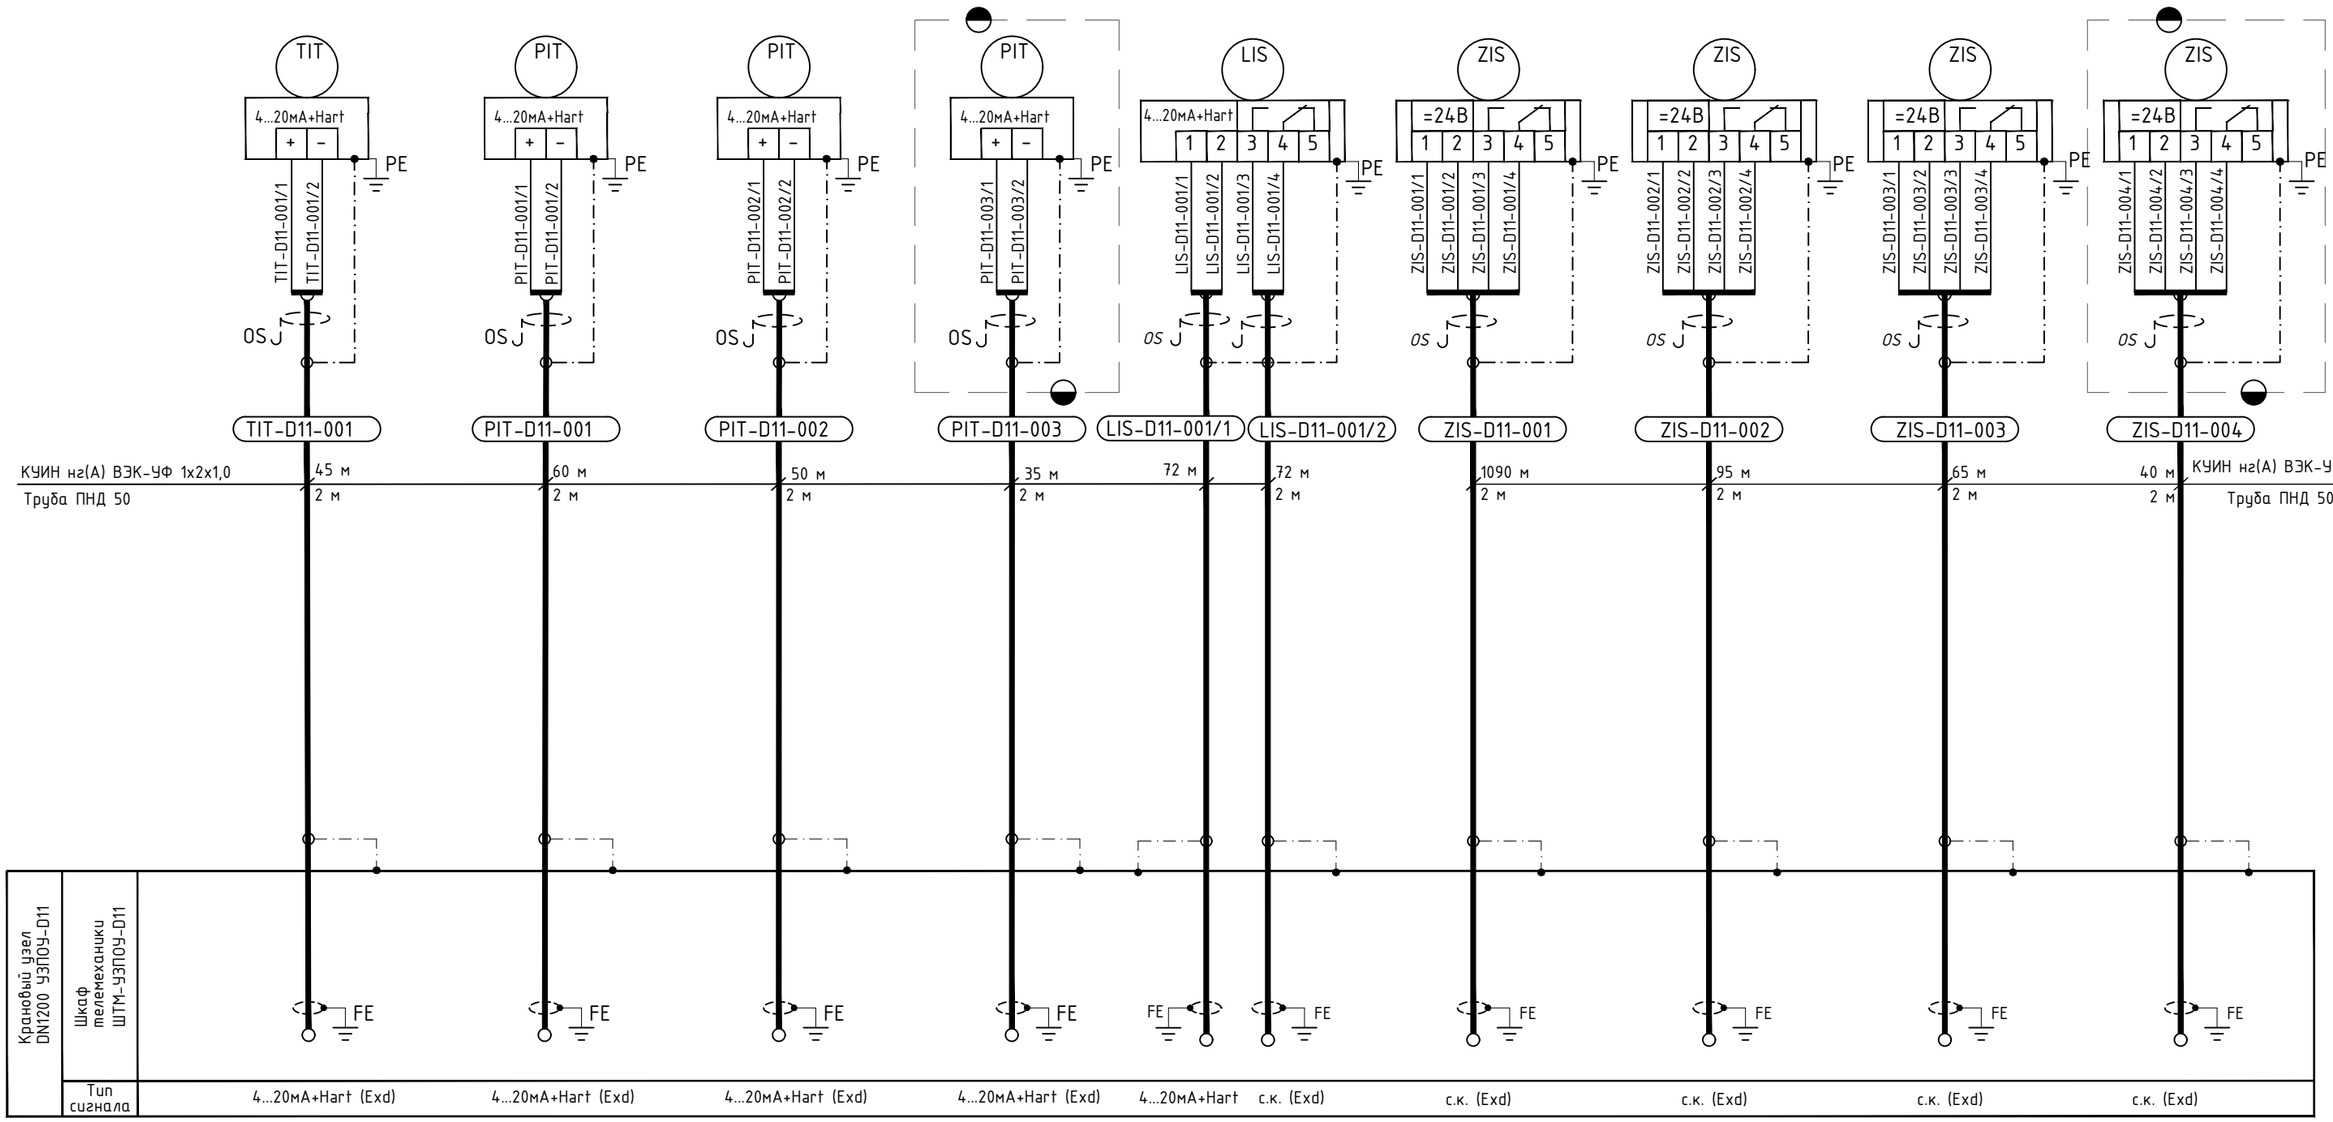

Взам. инв. №

Подпись и дата


Инв.№ подл.

Изм.	Кол.уч.	Лист	№док.	Подпись	Дата

EWE0426-MGL1-SYS-054-SCM-690305-A1

Лист 2

Наименование параметра и место отбора импульса	Пневмопривод крана	Пневмопривод крана	Пневмопривод крана
	Управление краном	Управление краном	Управление краном
	Трубопровод 1200-GT-63CS00-HH-D1102	Трубопровод 1200-GT-63CS00-HH-D1101	Трубопровод 500-GT-63CS02-HH-D1103
Обозначение чертежа установки			
Позиция	XV-D11-001	XV-D11-002	XV-D11-003

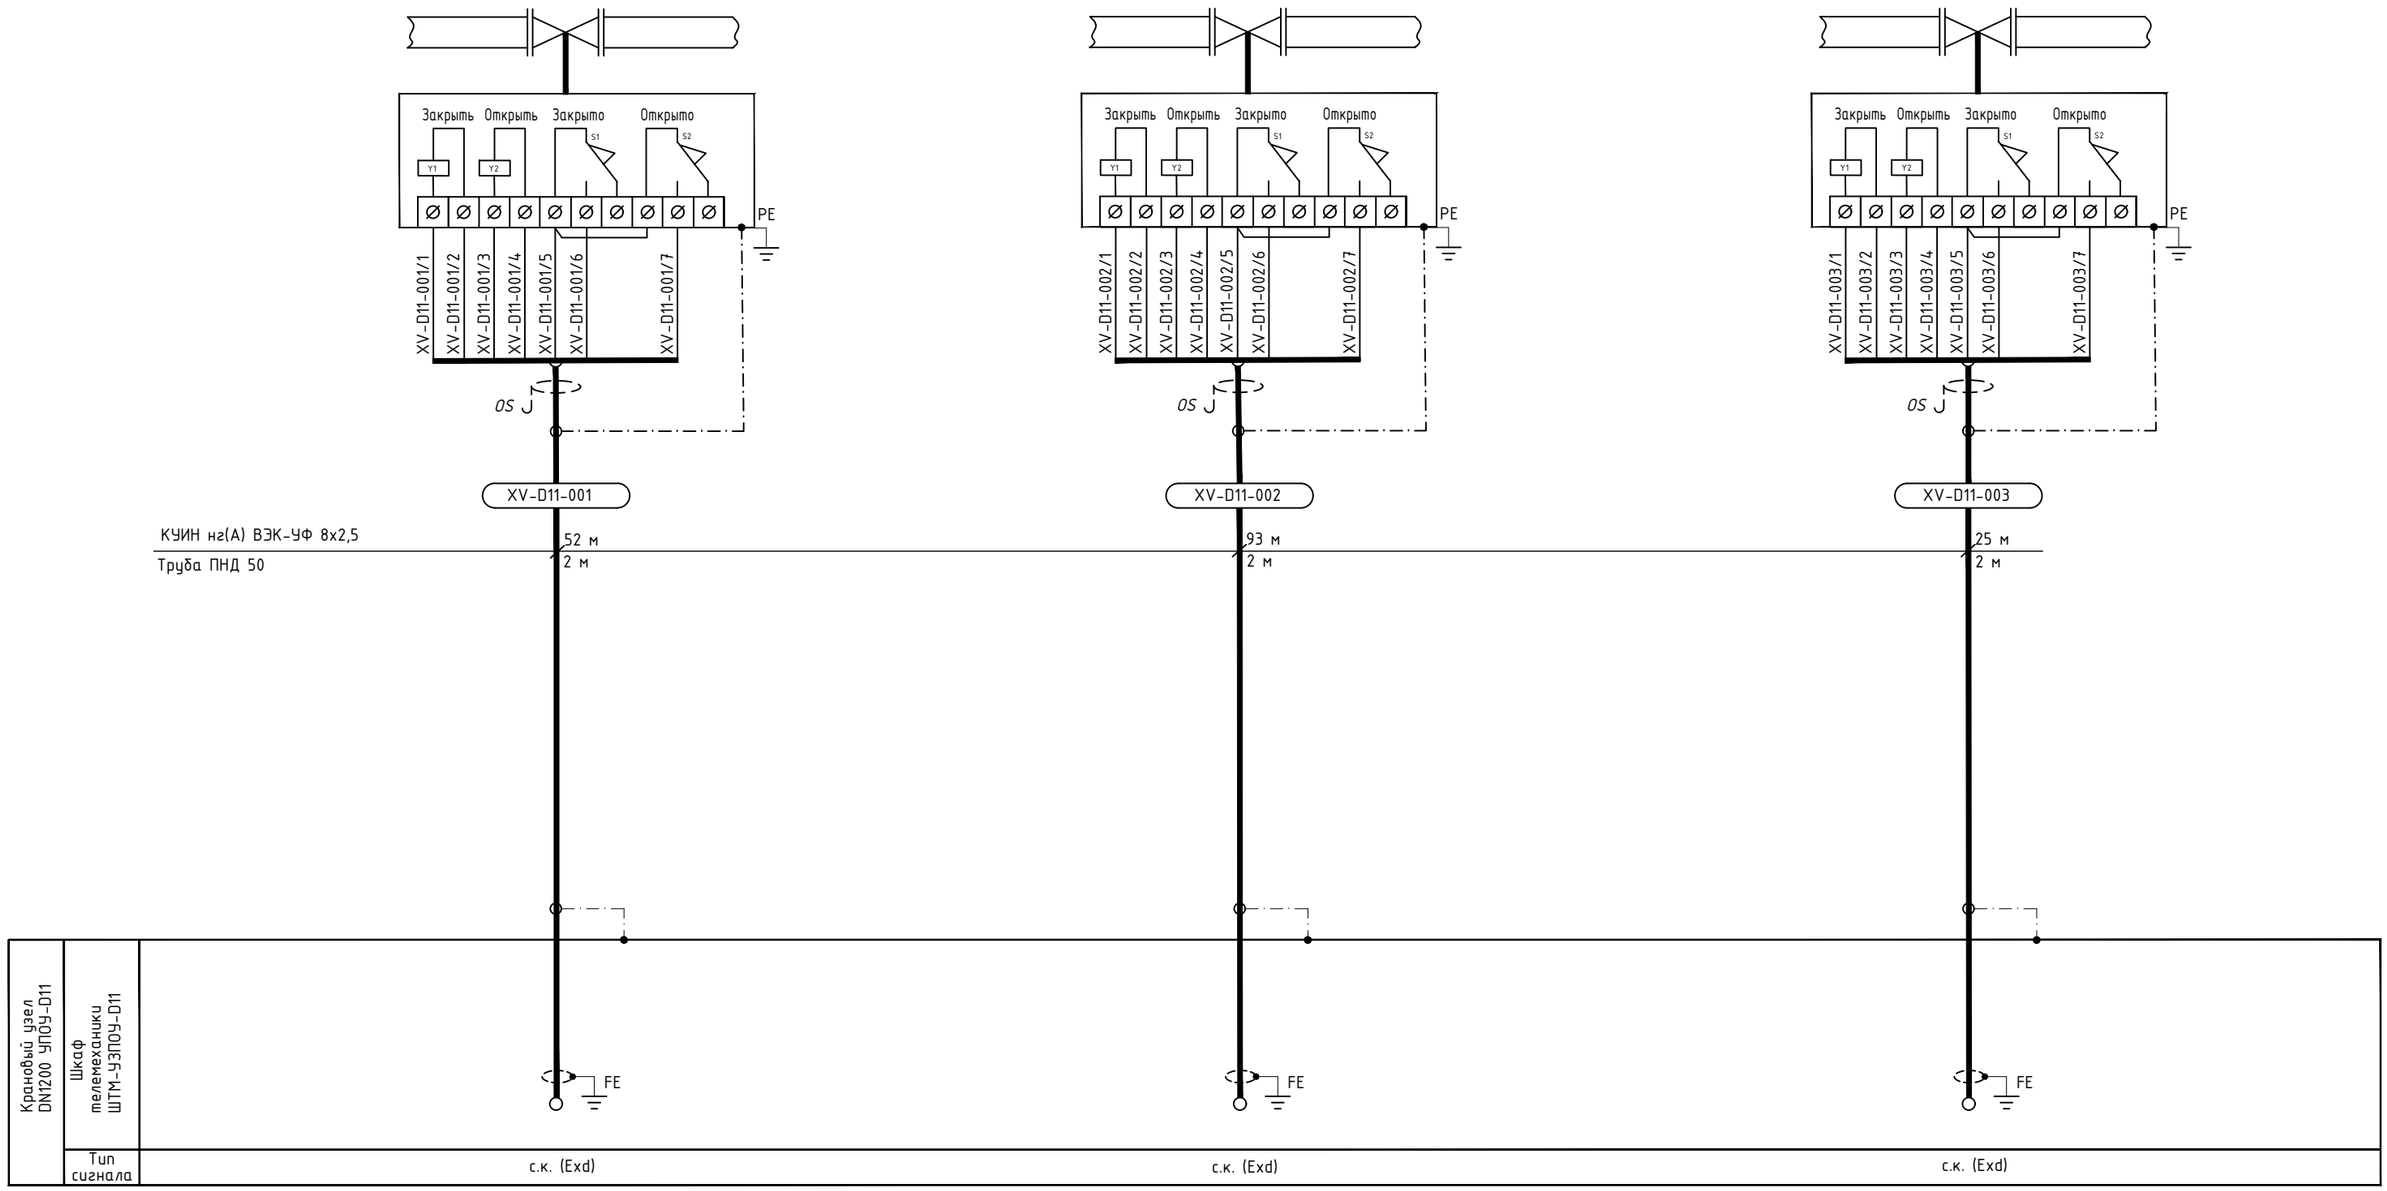

Взам. инв. №

Подпись и дата


Инв.№ подл.

Изм.	Кол.уч.	Лист	№док.	Подпись	Дата

EWE0426-MGL1-SYS-054-SCM-690305-A1

Лист 3

Наименование параметра и место отбора импульса	Пневмопривод крана	Пневмопривод крана	Пневмопривод крана
	Управление краном	Управление краном	Управление краном
	Трубопровод 500-GT-63CS02-HH-D1103	Трубопровод 300-GT-63CS02-HH-D1107	Трубопровод 300-GT-63CS02-HH-D1107
Обозначение чертежа установки			
Позиция	XV-D11-004	XV-D11-005	XV-D11-006

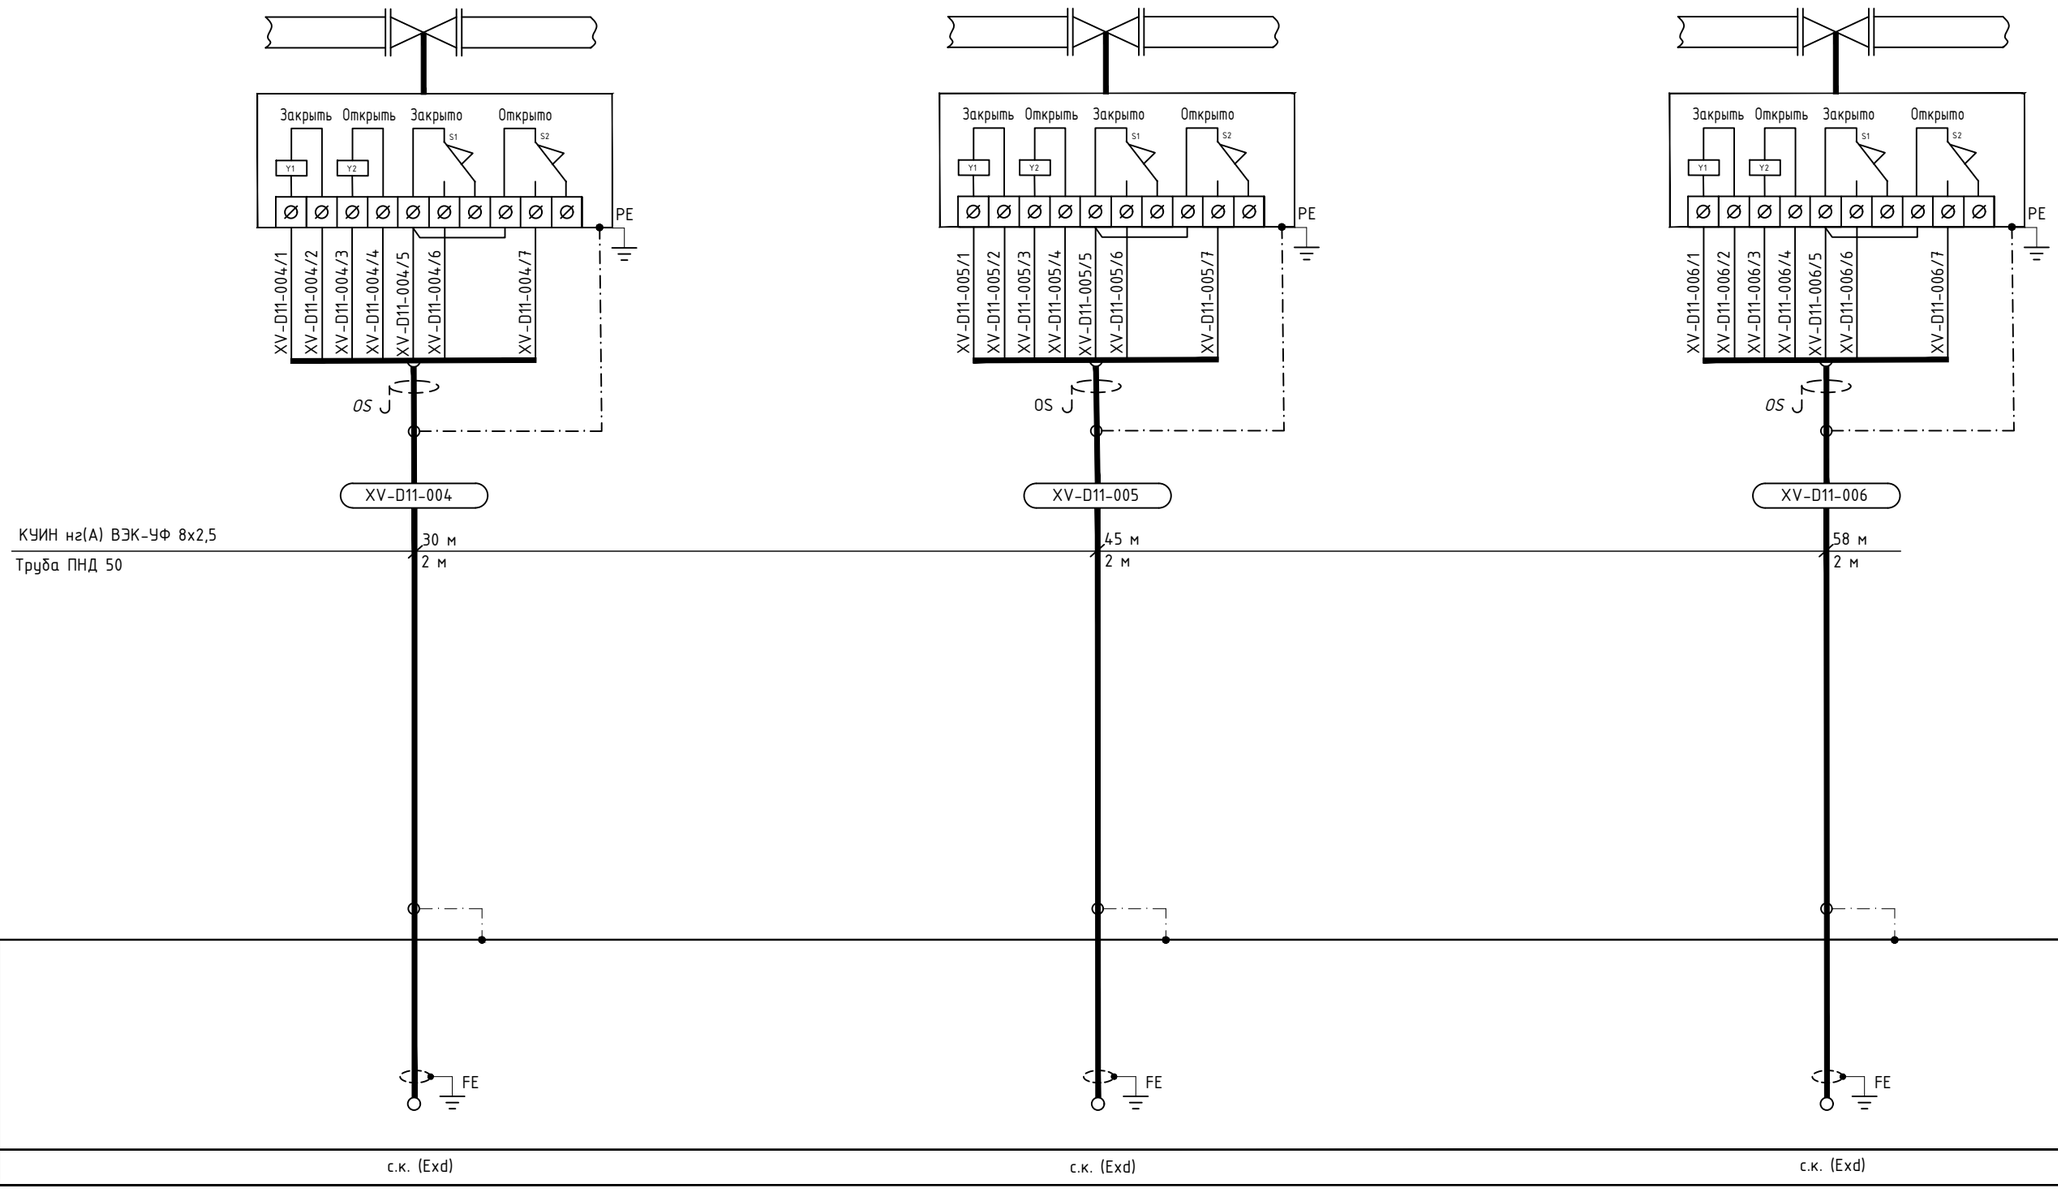

Взам. инв. №

Подпись и дата


Инв.№ подл.

Изм.	Кол.уч.	Лист	№док.	Подпись	Дата

EWE0426-MGL1-SYS-054-SCM-690305-A1

Лист 4

Наименование параметра и место отбора импульса	Пневмопривод крана	Пневмопривод крана	Пневмопривод крана
	Управление краном	Управление краном	Управление краном
	Трубопровод 300-VA-63CS02-HH-D1104	Трубопровод 300-GT-63CS02-HH-D1106	Трубопровод 300-GT-63CS02-HH-D1105
Обозначение чертежа установки			
Позиция	XV-D11-007	XV-D11-008	XV-D11-009

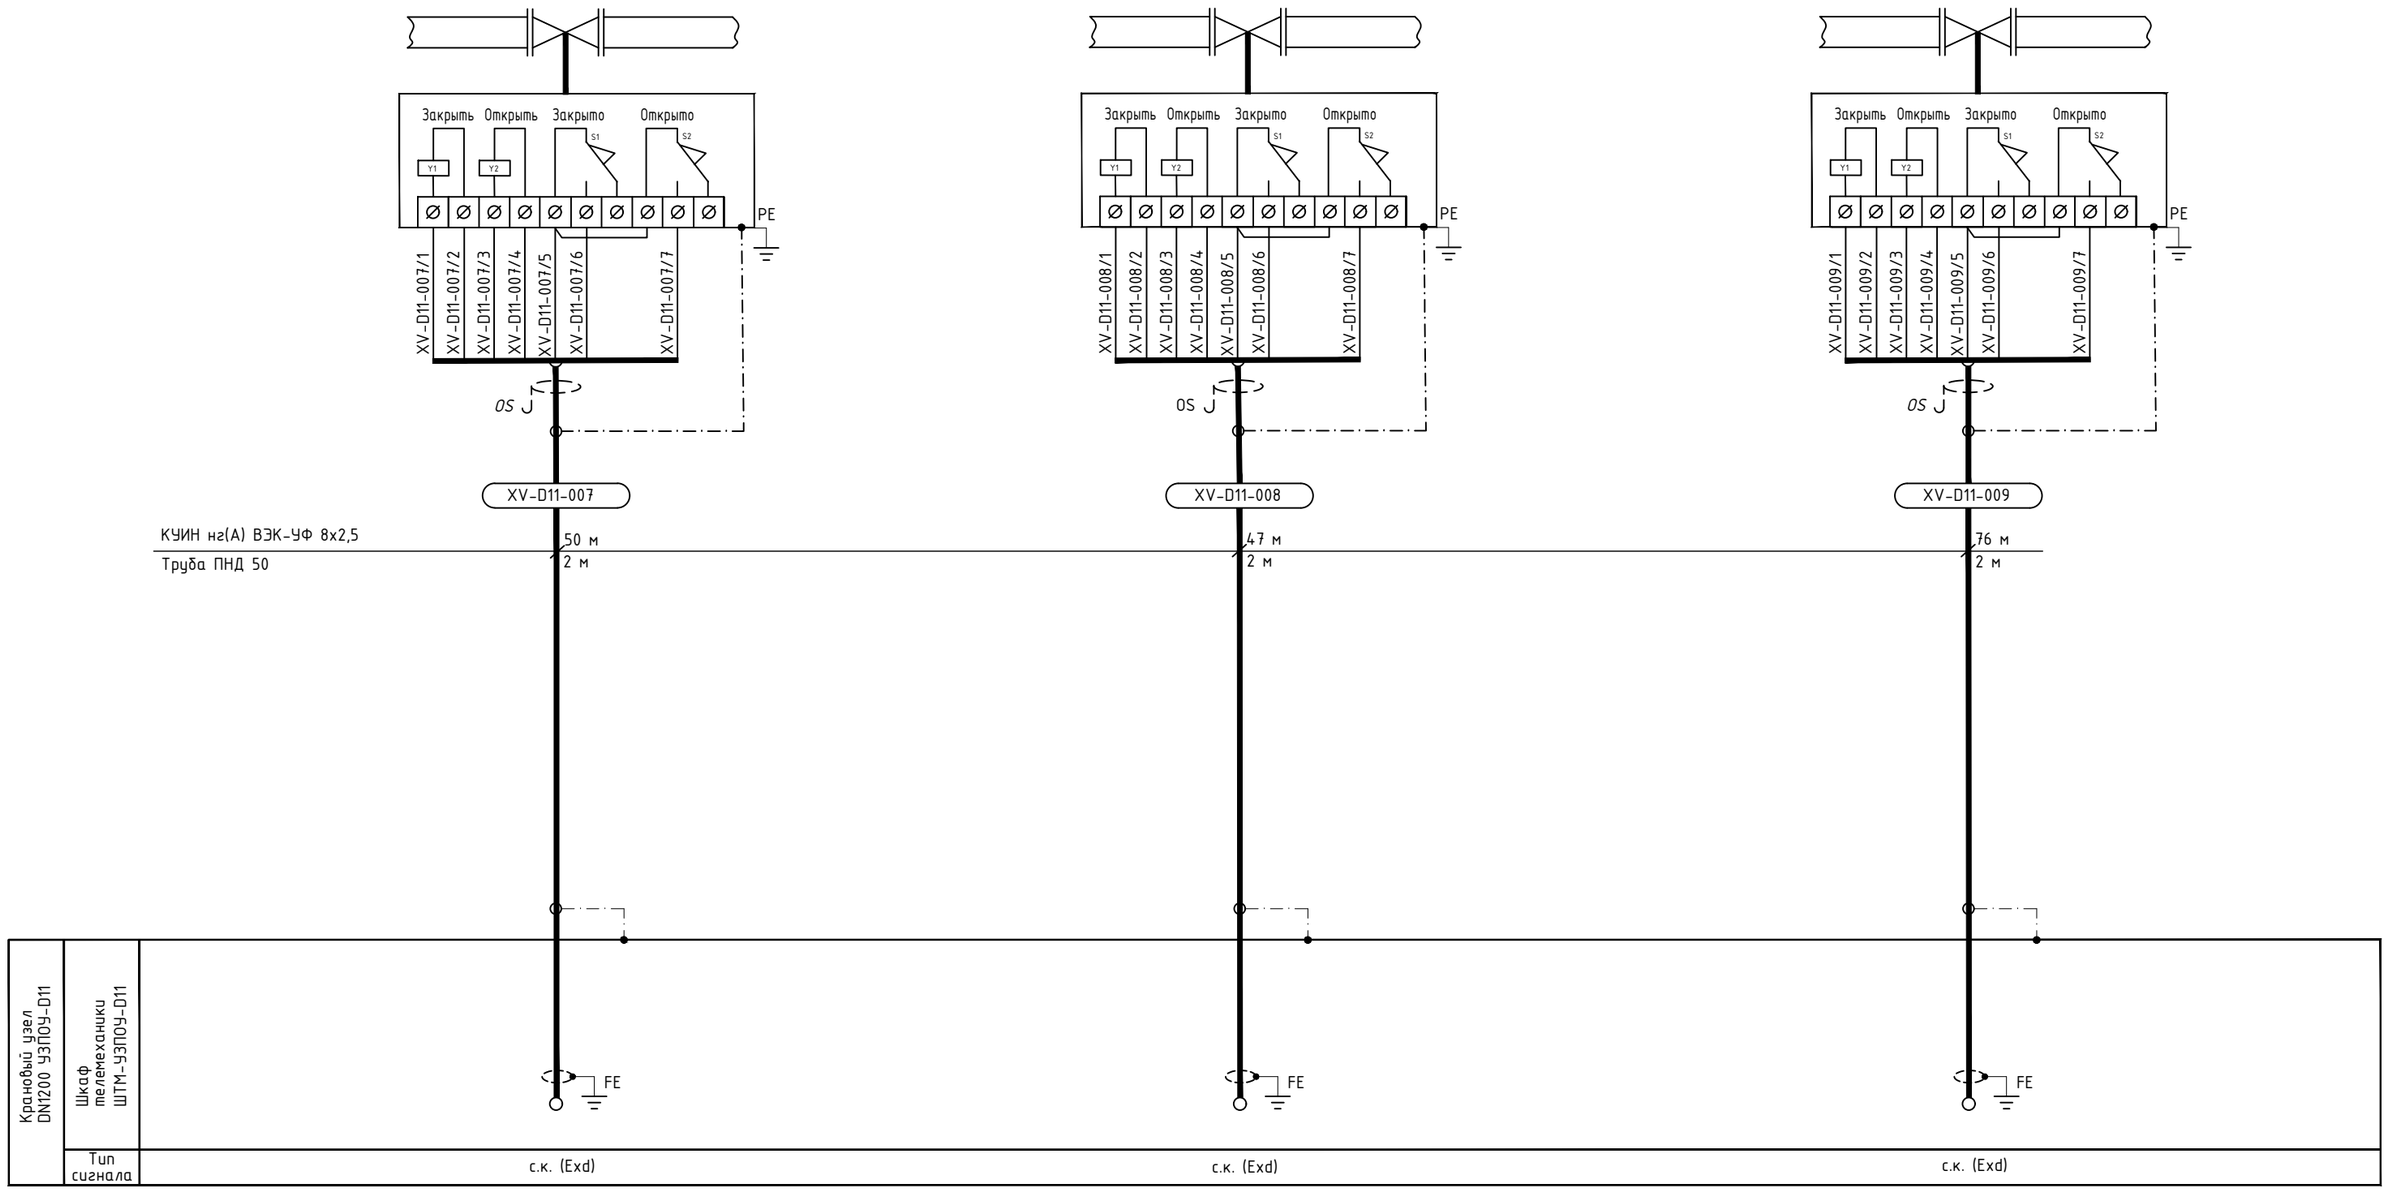

Взам. инв. №

Подпись и дата


Инв.№ подл.

Изм.	Кол.уч.	Лист	№док.	Подпись	Дата

EWE0426-MGL1-SYS-054-SCM-690305-A1

Лист 5

Наименование параметра и место отбора импульса	Пневмопривод крана	Пневмопривод крана	Пневмопривод крана
	Управление краном	Управление краном	Управление краном
	Трубопровод 300-GT-63CS02-HH-D1108	Трубопровод 300-GT-63CS02-HH-D1108	Трубопровод 300-DC-63CS02-HH-D1110
Обозначение чертежа установки			
Позиция	XV-D11-010	XV-D11-011	XV-D11-012

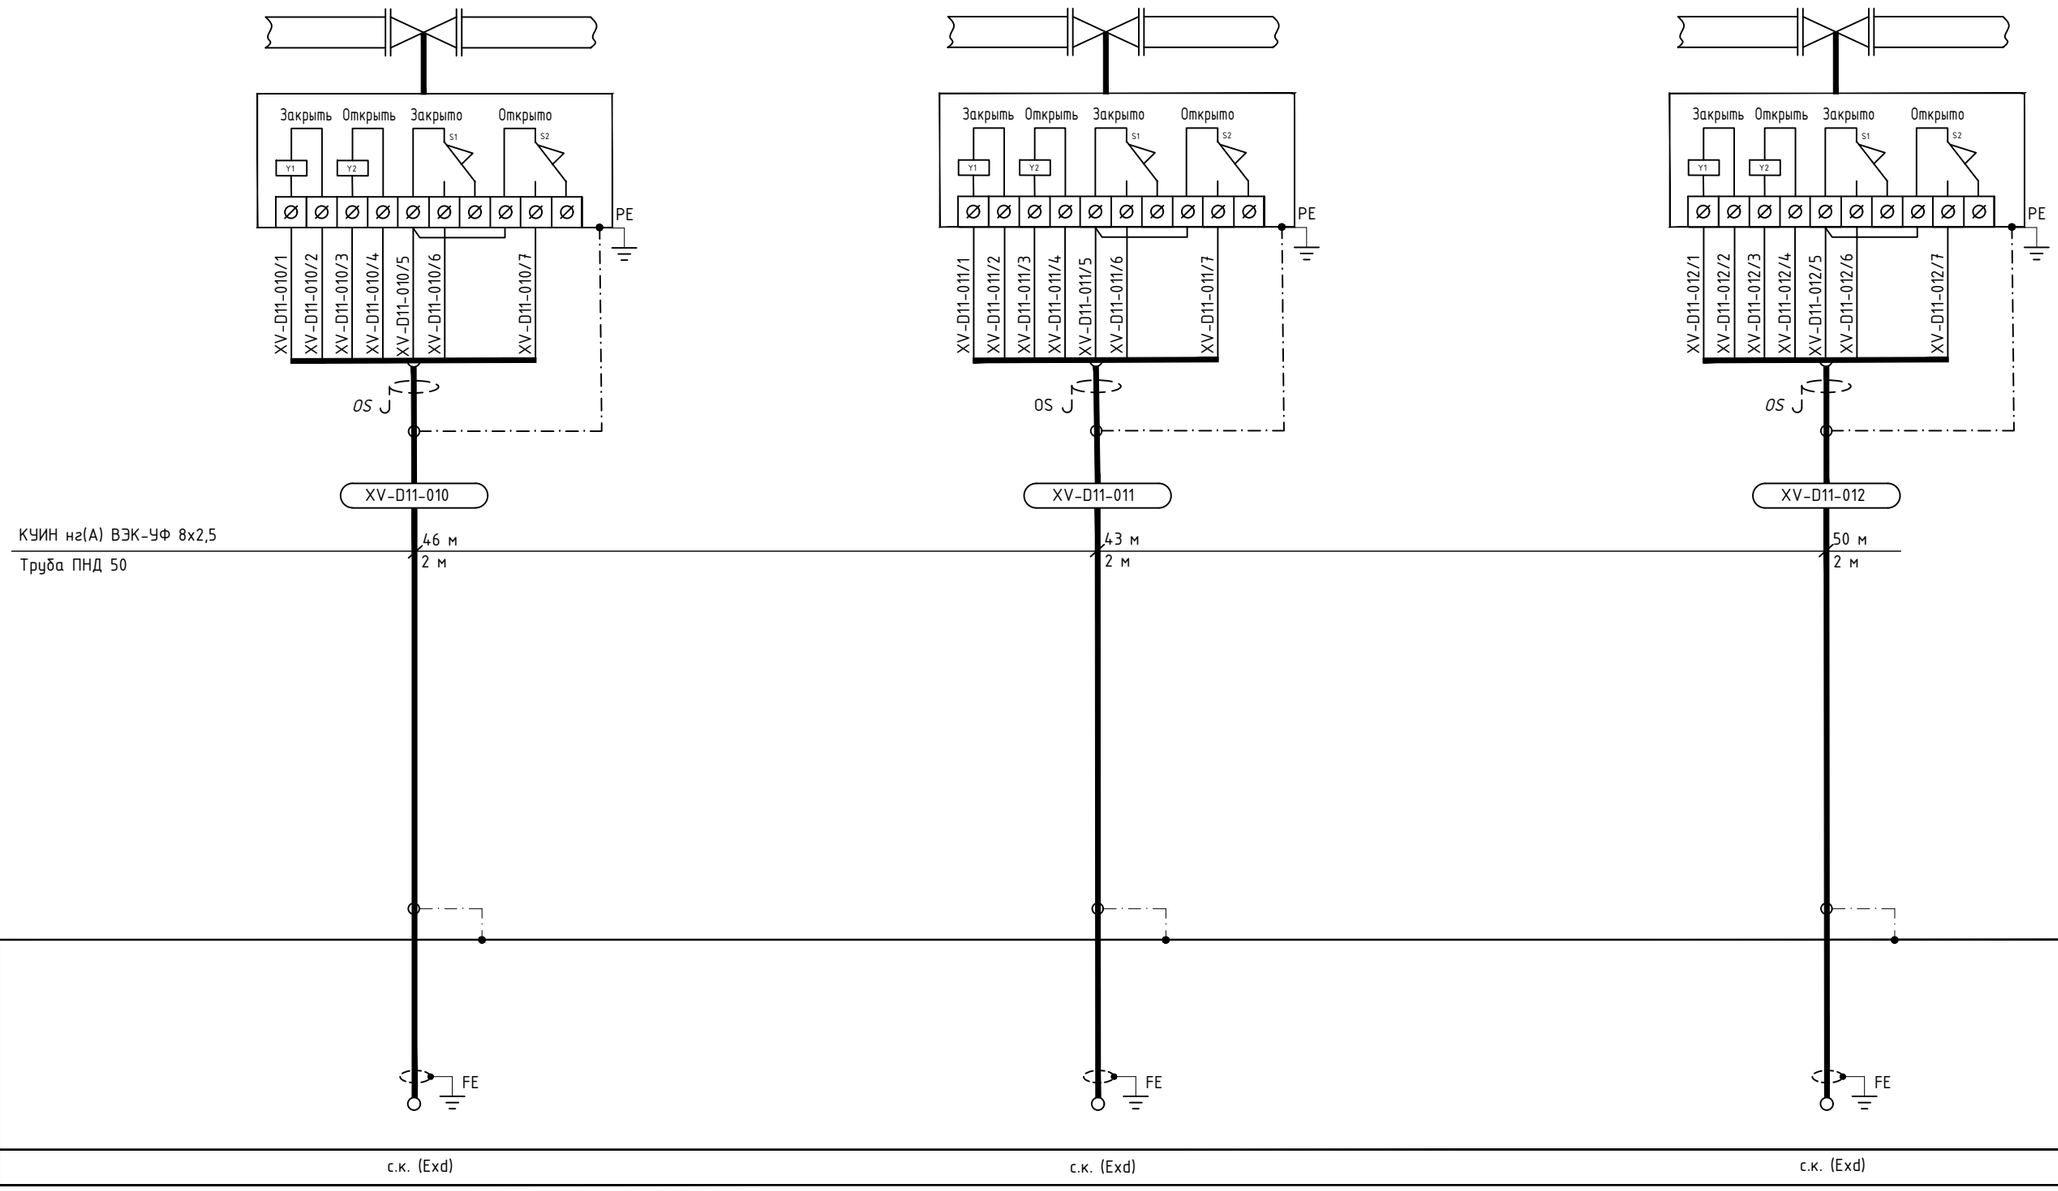

Взам. инв. №

Подпись и дата

Инв.№ подл.

Изм.	Кол.уч.	Лист	№док.	Подпись	Дата

EWE0426-MGL1-SYS-054-SCM-690305-A1

Лист 6