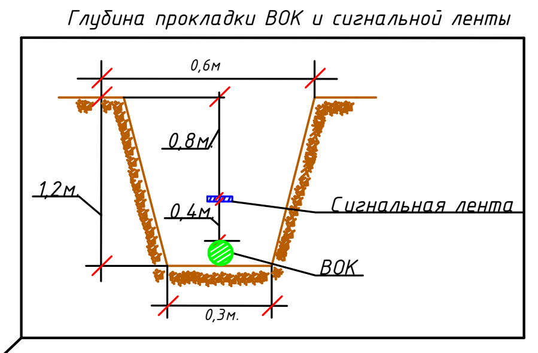

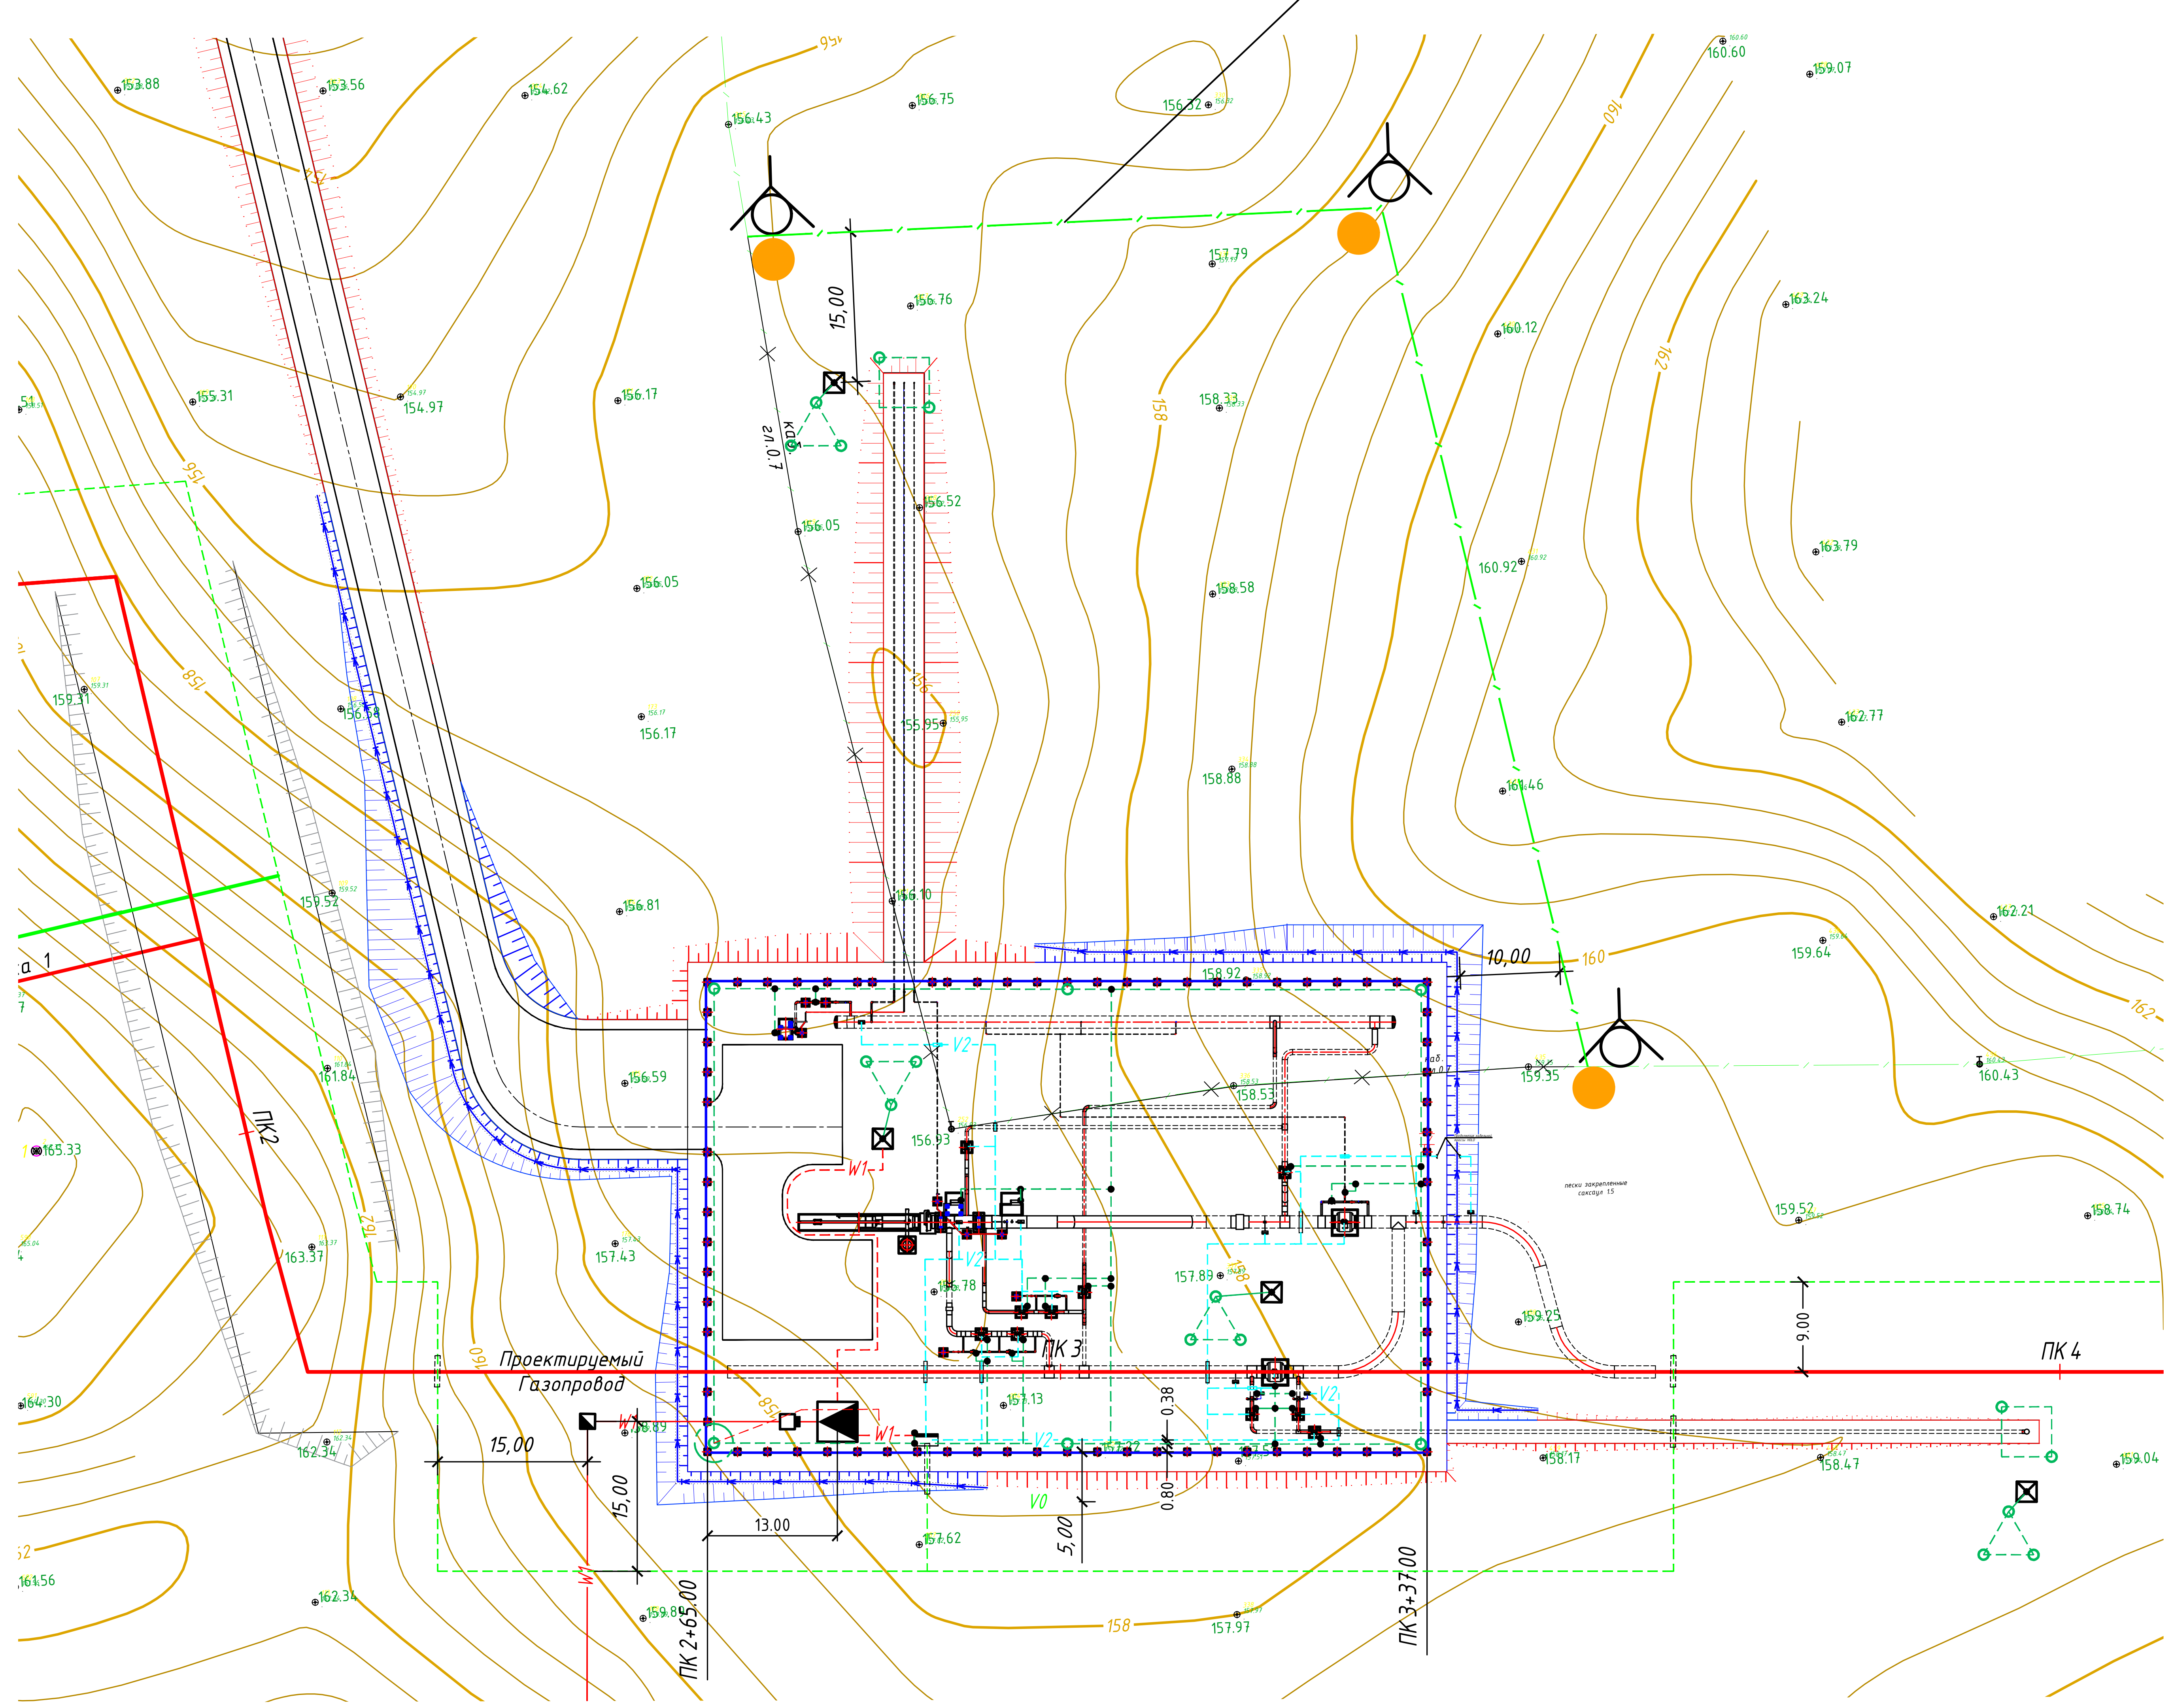

Условные обозначения

— · —	Существующая линия связи
—×—×—	Перекладка существующей линии связи
⛉	Столбик
●	Маркер

Рев.	Дата	Назначение ревизии	Проверил	Утвердил
A1	16.10.2026	Выпущено для строительства		
R1	08.10.2026	Выпущено для рассмотрения		

ЗАКАЗЧИК: UTG UZTRANSGAZ
ГЕНЕРАЛЬНЫЙ ПОДРЯДЧИК: UET UZBEKENERGOTAMIR
ПОДРЯДЧИК: PBG Pro Build Generation
ГЕНЕРАЛЬНЫЙ ПРОЕКТИРОВЩИК: EAST WEST ENGINEERING

EWE0426-MGL1-COS-054-PLA-690702-A1

Строительство новых ниток (участков) газопроводов «Газли - Саримой» и «Акчалок - Газли - Нукус» общей протяженностью не менее 275 км

Изм.	Кол. уч	Лист.	№док.	Подп.	Дата
ГИП		Кирпичников С.			16.10.26
Нач. отд.		Кабулова Е.		Ecaauf	16.10.26
Исполн.		Кабулова Е.		Ecaauf	16.10.26
Н.контр.		Кирпичников С.			16.10.26

Газопровод Газли-Сарымай (54км)
Перенос ВОЛС

Стадия	Лист	Листов
РД	1	1

Ситуационный план

ООО "EAST-WEST Engineering"
г. Ташкент 2026г.

Взам. инв. №
Подпись и дата
Инв.№ подл.

Формат А1 / Format A1